



ITEM	QTY/MODULE	PART NUMBER	DIM	APPEARANCE
1	7	n/a	3425x1250x0,75	RAL9006_C4-M
2	1	n/a	3020x1250x0,75	RAL9006_C4-M
3	2	n/a	2180x1250x0,75	RAL9006_C4-M
4	1	n/a	120x800x0,75	RAL9006_C4-M
5	2	n/a	790x1250x0,75	RAL9006_C4-M

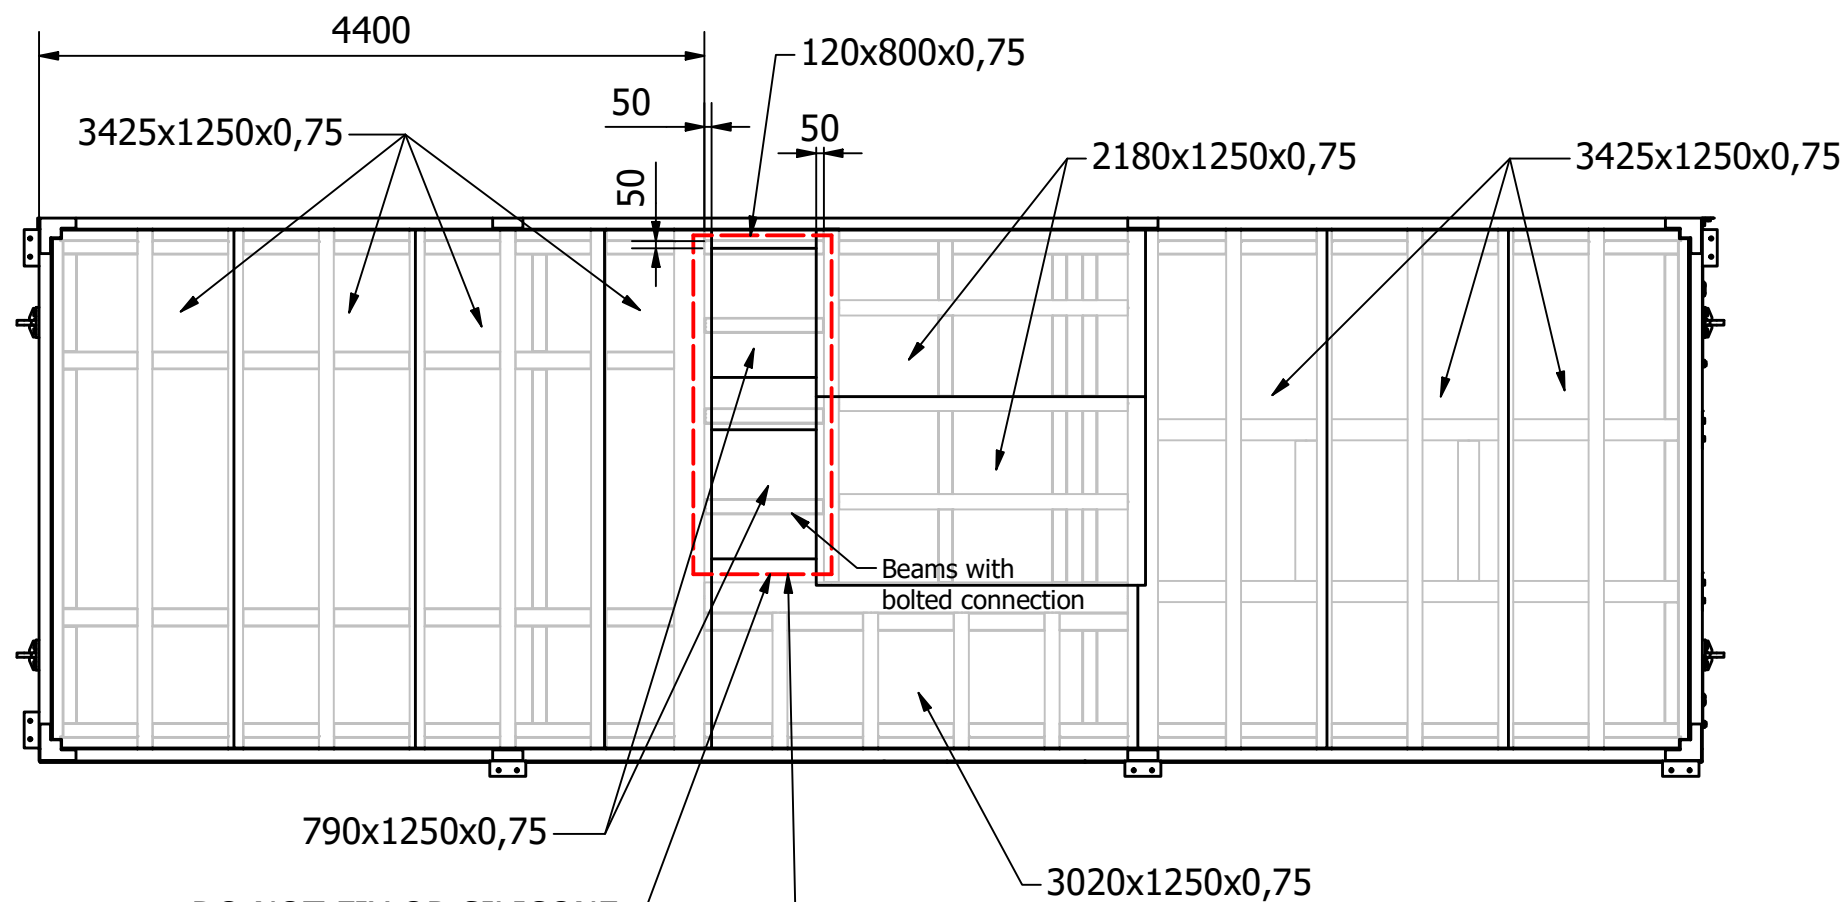


DO NOT FIX OR SILICONE
790x1250x0,75 SHEETS
ADD RIVET NUT WITH BOLT THAT
MUST BE REMOVABLE FROM INSIDE MODULE

– PLACE THESE SHEETS LAST,
THEY MUST BE REMOVABLE FROM THE INSIDE



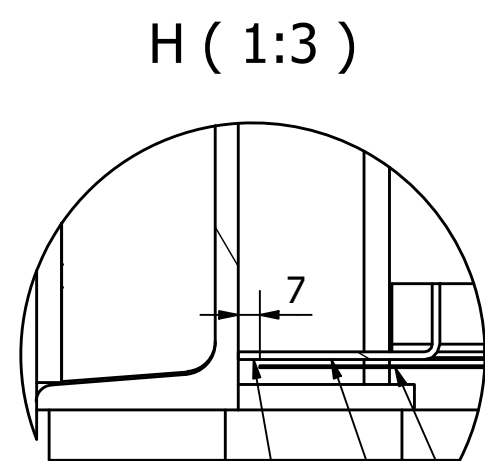


Sealant UV resistant
Sikaflex 521 UV 300ML-WHITE
Painted side
Fix with SCREW JT3-12-5.5x40 E16

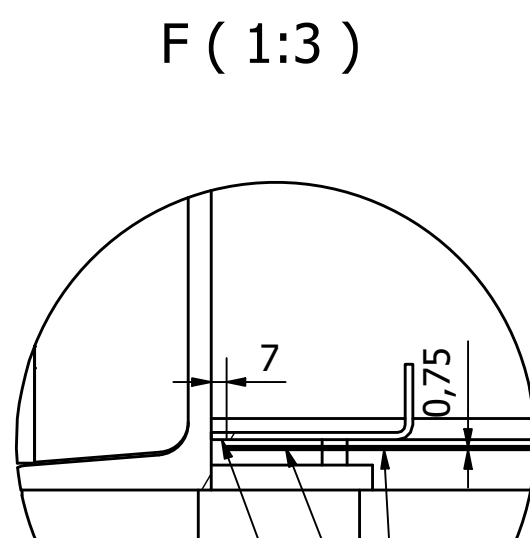

Sealant UV resistant
Sikaflex 521 UV 300ML-WHITE


Fix with SCREW JT3-12-5.5x40 E16

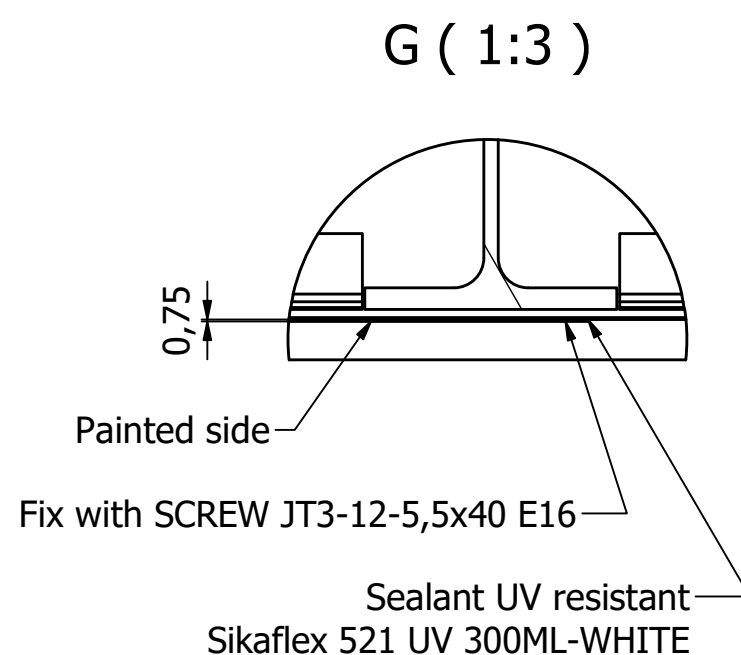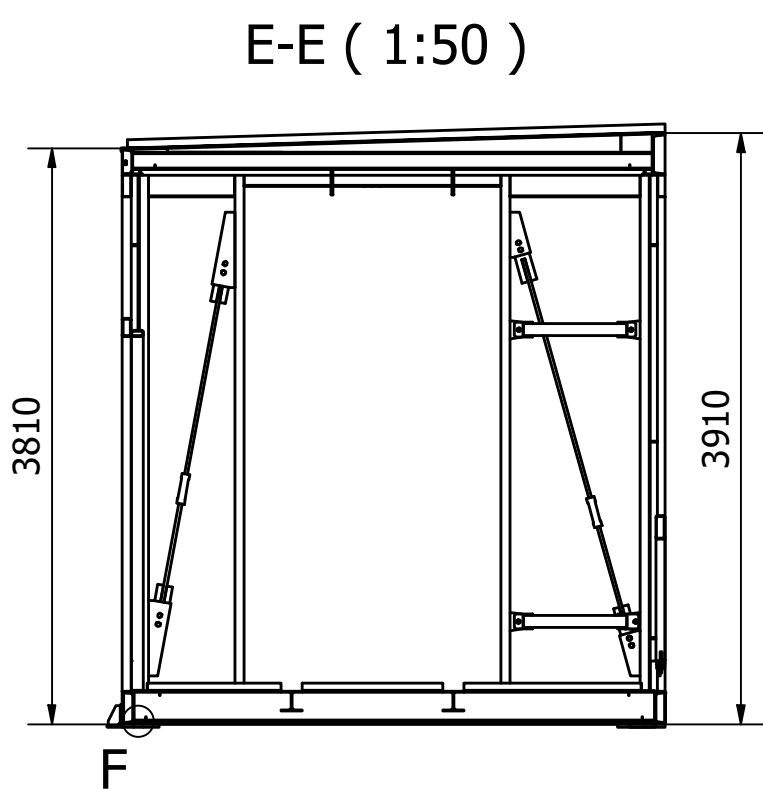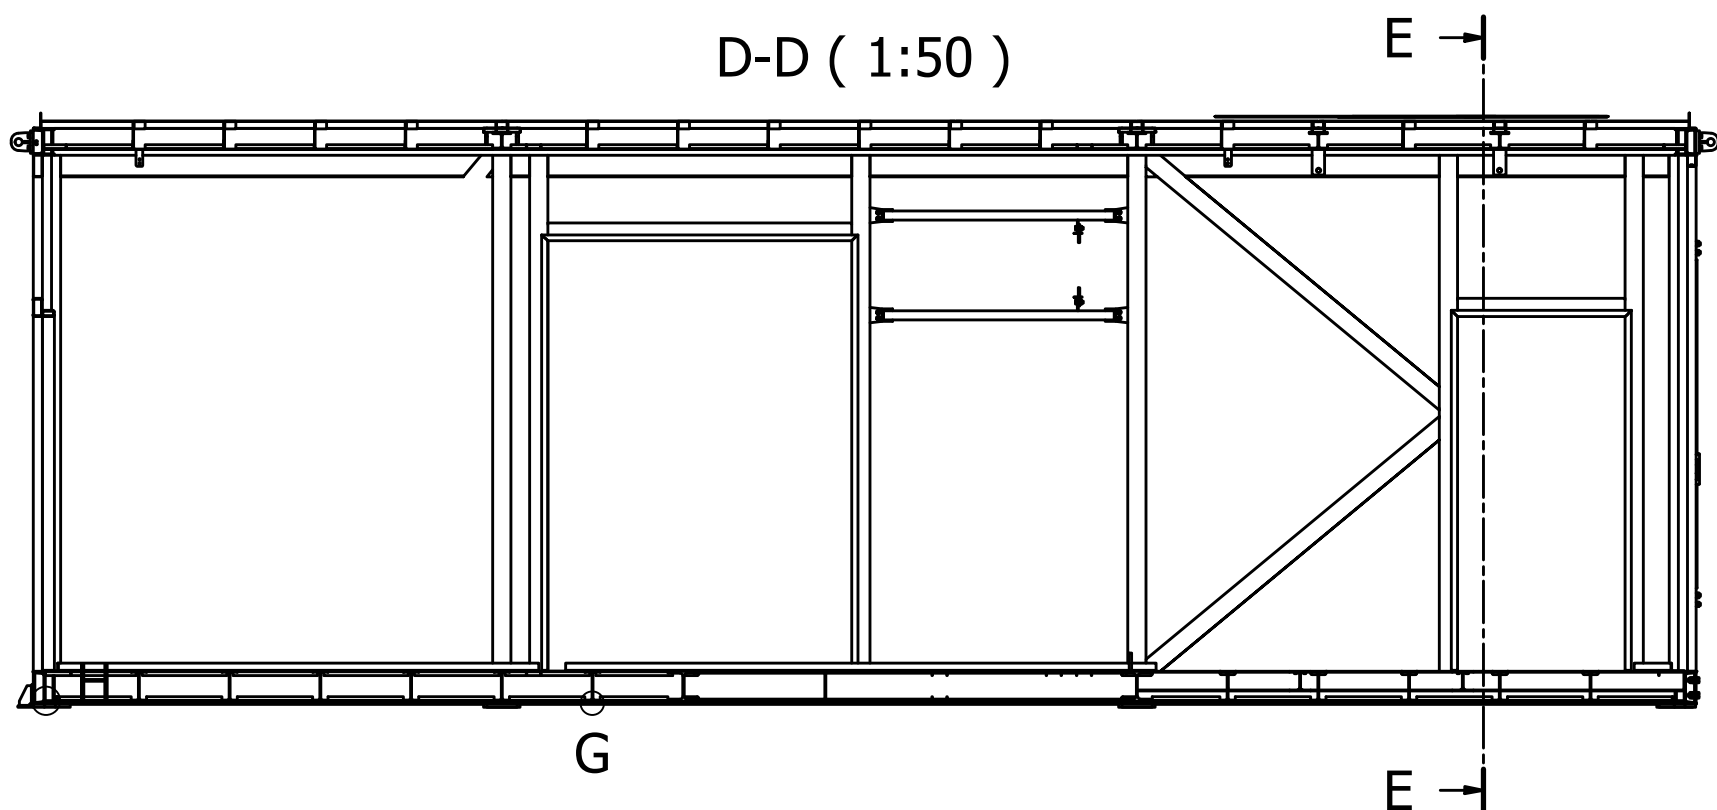

NOTES:

- Detailed cutting should be done during installation
- Minimum overlap between steel sheets 50 mm

REVISION HISTORY		
REV	DESCRIPTION	DATE
R3	FOR MANUFACTURING	3.9.2026.
R2	FOR MANUFACTURING	11.8.2026.
R1	FOR MANUFACTURING	19.5.2026.

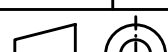	CAD system		Material	Finish	Weight
	Autodesk Inventor				N/A
	Sheet size	Scale	Project name		
	A2	1:50	ECOD DC		
			Drawing name / Description		
EXTERNAL FLOOR LAYOUT					
Prepared (also subject responsible if other)			Document number / Part number		
M. BRATIC			ASI-101-MV-EXTERNAL FLOOR LAYOUT		
Document responsible/Approved			Rev	Date (DD.MM.YY)	Sheet
J.J. CICVARIC			R3	16.6.2026.	1 (1)

External steel sheet information's:
Pre-painted galvanized steel sheet DX51D+Z250.
Sheet thickness in the range of 0,75 to 1 mm, project dependent.
Dimensions (H x W) of the sheets are project dependent.

Installation notes:
Watch the orientation surface of steel sheet (Painted side).
Make sure to flatten the sheet before fixing it to the structure.
Fixing distances should be no more then 650 mm in both directions
of the external sheet plane.