
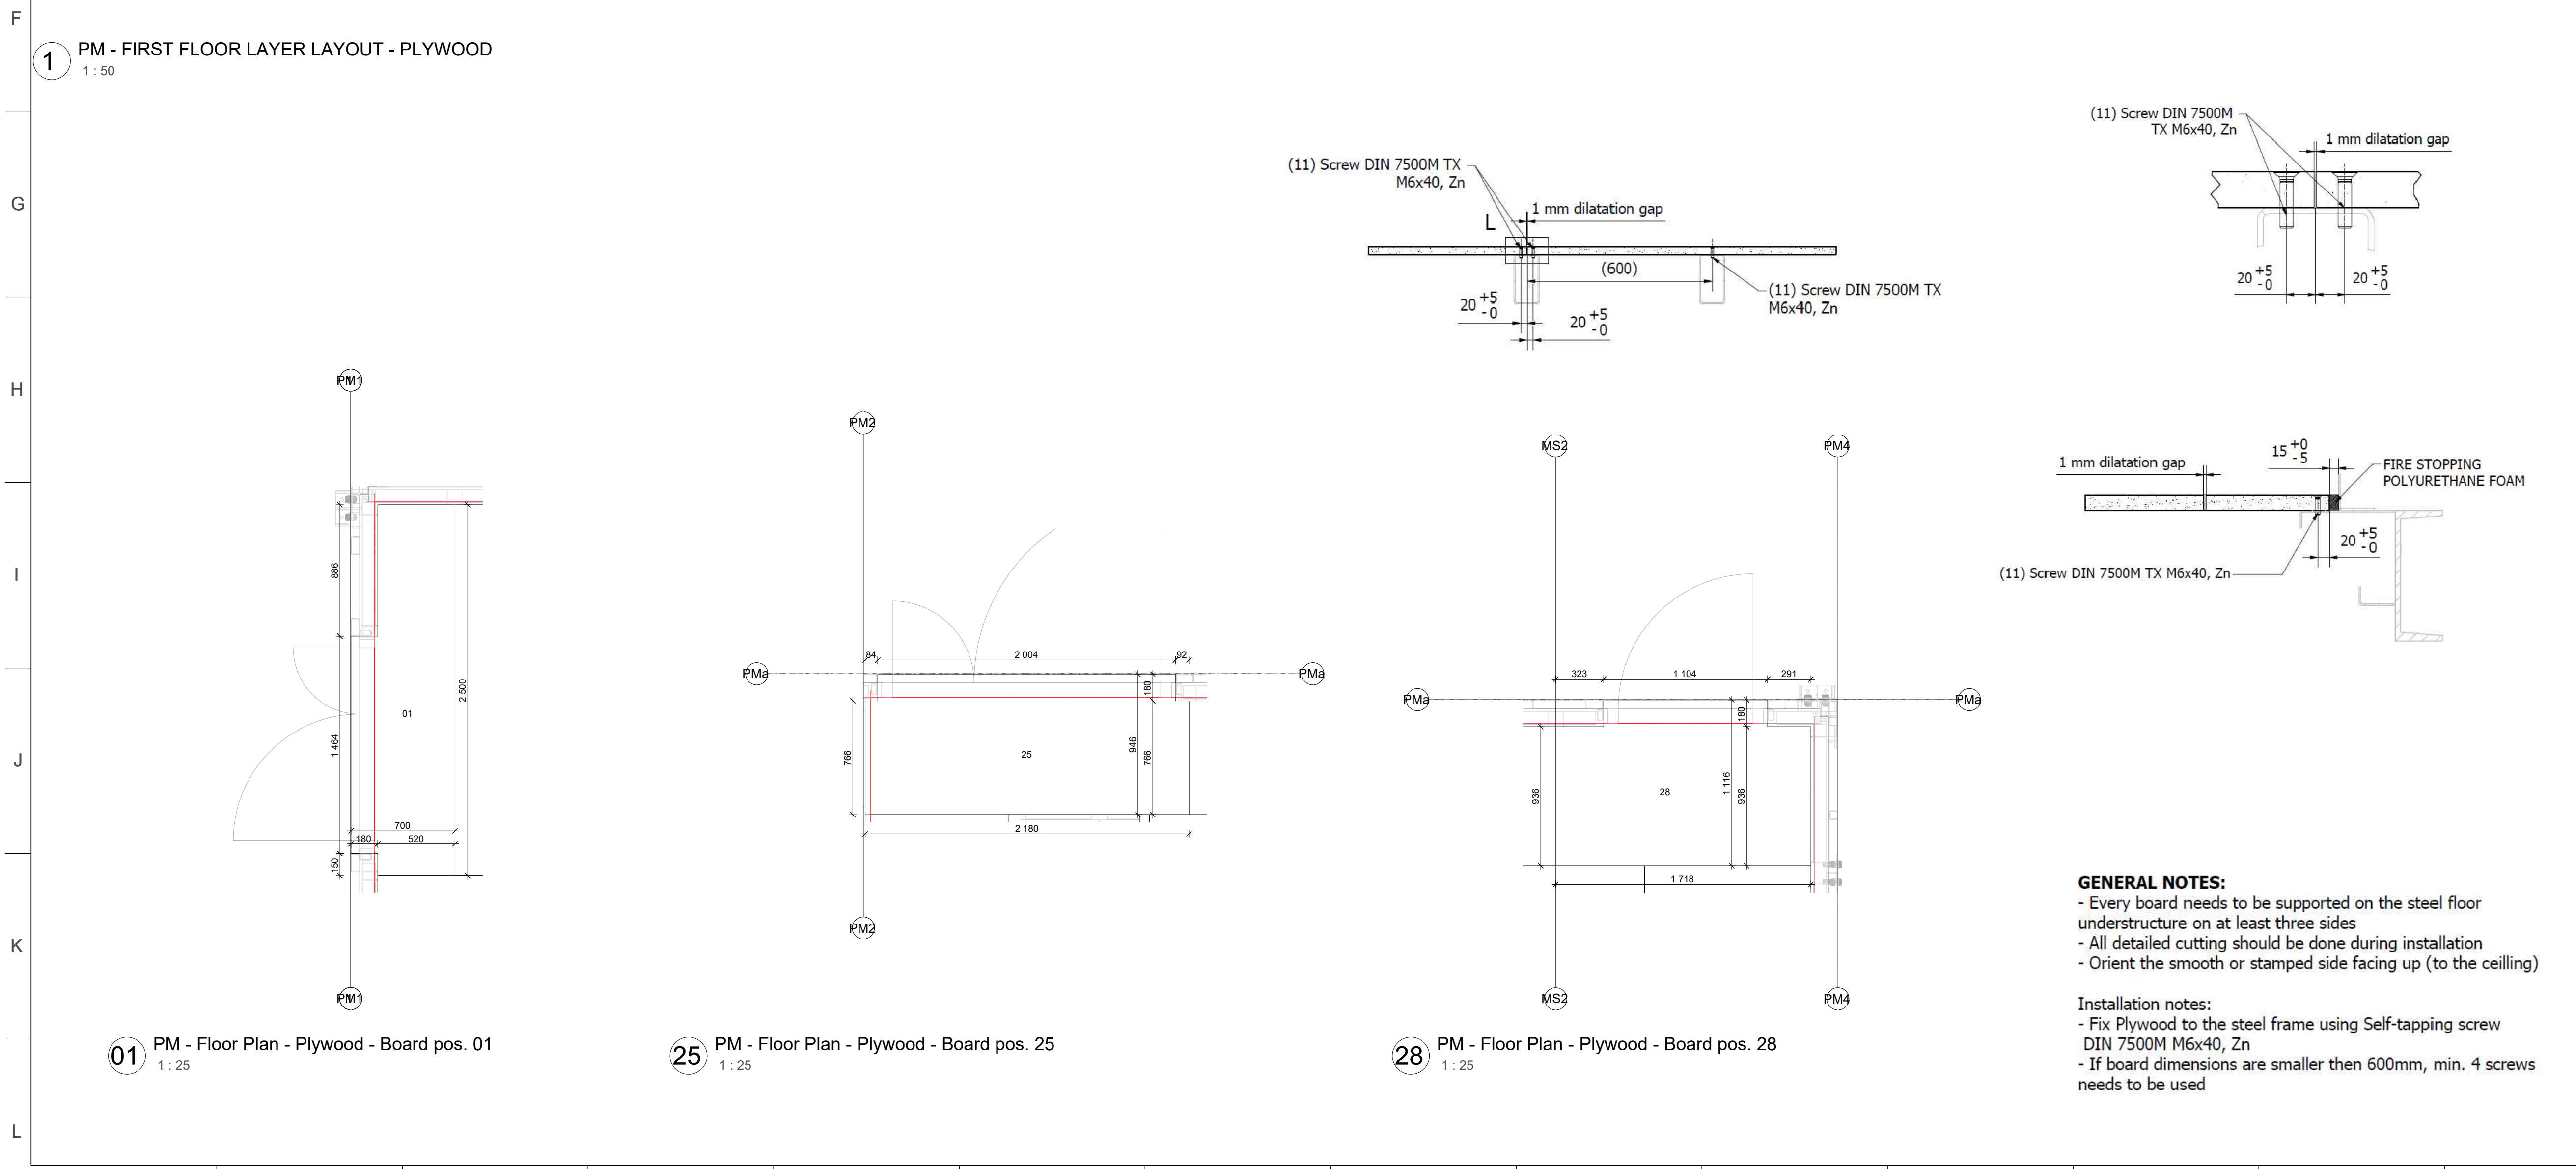


LEGAL DISCLAIMER: THIS DOCUMENT AND THE CONTENTS HEREIN ARE CONFIDENTIAL AND THE SOLE PROPERTY OF VERTIV GROUP CORP. REPRODUCTION, DISTRIBUTION OR UNAUTHORIZED USE OF THIS DOCUMENT OR ANY PARTS WITHIN THIS DOCUMENT ARE FORBIDDEN WITHOUT THE WRITTEN CONSENT OF VERTIV GROUP CORP.

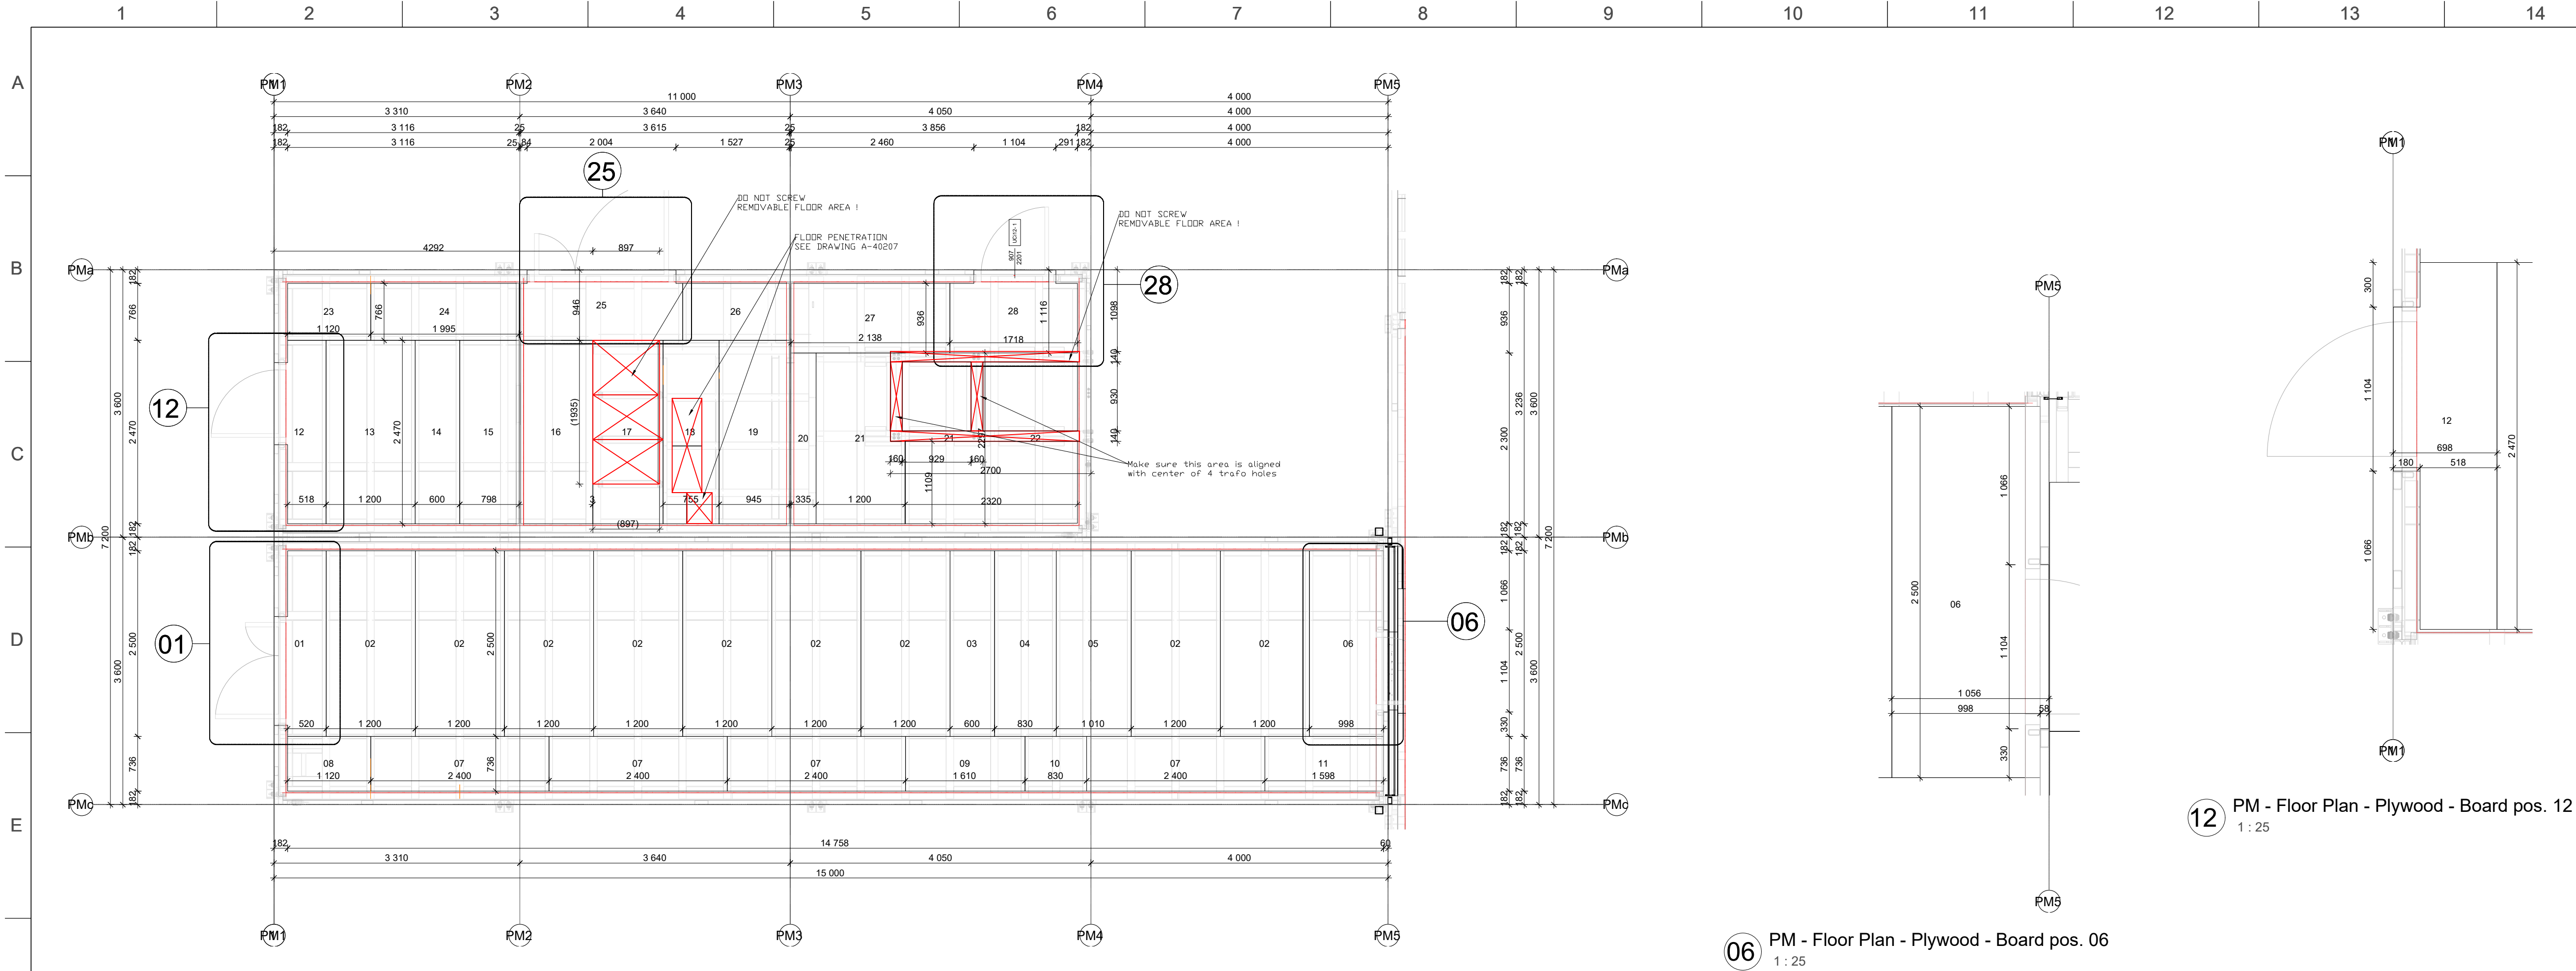

KEYNOTES

ASI - PM PLYWOOD			
Mark	Height Manual [mm]	Width Manual [mm]	Count [pcs]
01	2500	700	1
02	2500	1200	9
03	2500	600	1
04	2500	830	1
05	2500	1010	1
06	2500	1056	1
07	736	2400	4
08	736	1120	1
09	736	1610	1
10	736	830	1
11	736	1598	1
Grand total: 22			

ASI - MV PLYWOOD			
Mark	Height Manual [mm]	Width Manual [mm]	Count [pcs]
12	2470	698	1
13	2470	1200	1
14	2470	600	1
15	2470	798	1
16	2470	970	1
17	2470	945	1
18	2470	765	1
19	2470	945	1
20	2300	336	1
21	2300	1200	2
22	2300	1120	1
23	766	1120	1
24	766	1996	1
25	946	2180	1
26	766	1435	1
27	936	2138	1
28	1116	1718	1
Grand total: 18			

REFERENCE NOTES

KEY PLAN

R04	FOR MANUFACTURING	2026-09-02
R03	FOR MANUFACTURING	2026-08-11
R02	TRAFO CUTOUT ADDED	2026-07-24
R01	FOR MANUFACTURING	2026-05-26
REV.	DESCRIPTION	DATE

PROJECT NAME

ECO DC MONALISA

DRAWING NAME

PM – FIRST FLOOR LAYER LAYOUT – PLYWOOD

PREPARED (ALSO SUBJECT RESPONSIBLE IF OTHER)

I. PUTICA / K. KOZINA / V. SPANIC / M. BRATIC

DOCUMENT RESPONSIBLE / APPROVED

M. PACAK / J. CICVARIC

CAD / BIM SYSTEM

AUTODESK REVIT 2025

DOCUMENT NUMBER

ECODC-VRT-MDC19-00-DR-ASI-102-1

SHEET SIZE

A1

DRAWING SCALE

As indicated

DATE (YYYYMM-DD)

2026-05-26

SHEET 1 OF 1

REVISION

R4