




LEGAL DISCLAIMER: THIS DOCUMENT AND THE CONTENTS HEREIN ARE CONFIDENTIAL AND THE SOLE PROPERTY OF VERTIV GROUP CORP. REPRODUCTION, DISTRIBUTION OR UNAUTHORIZED USE OF THIS DOCUMENT OR ANY PARTS WITHIN THIS DOCUMENT ARE FORBIDDEN WITHOUT THE WRITTEN CONSENT OF VERTIV GROUP CORP.

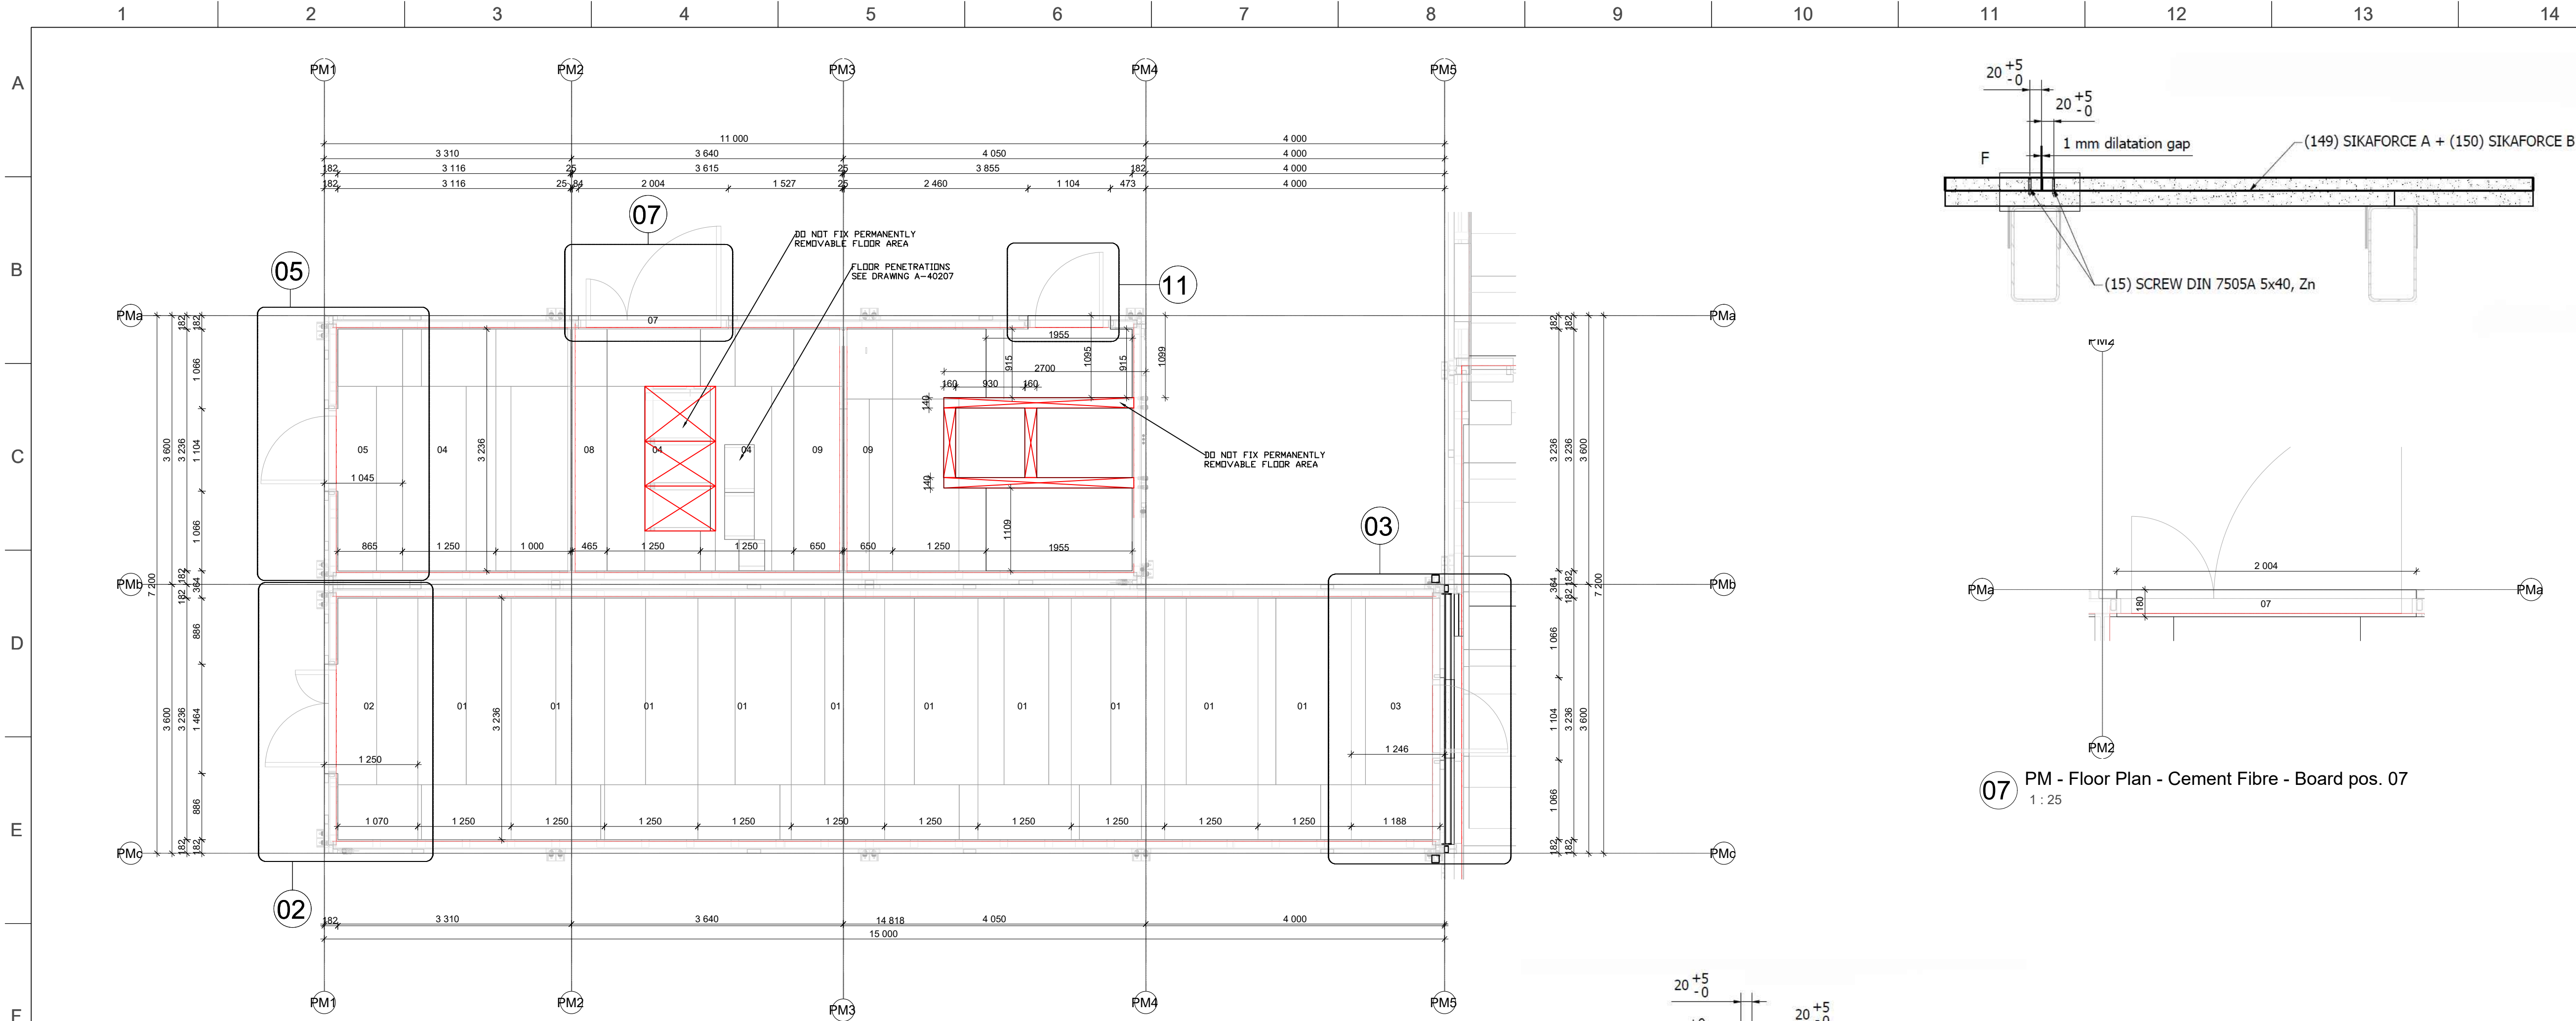


1 PM - FIRST FLOOR LAYER LAYOUT - CEMENT FIBRE
1 : 50

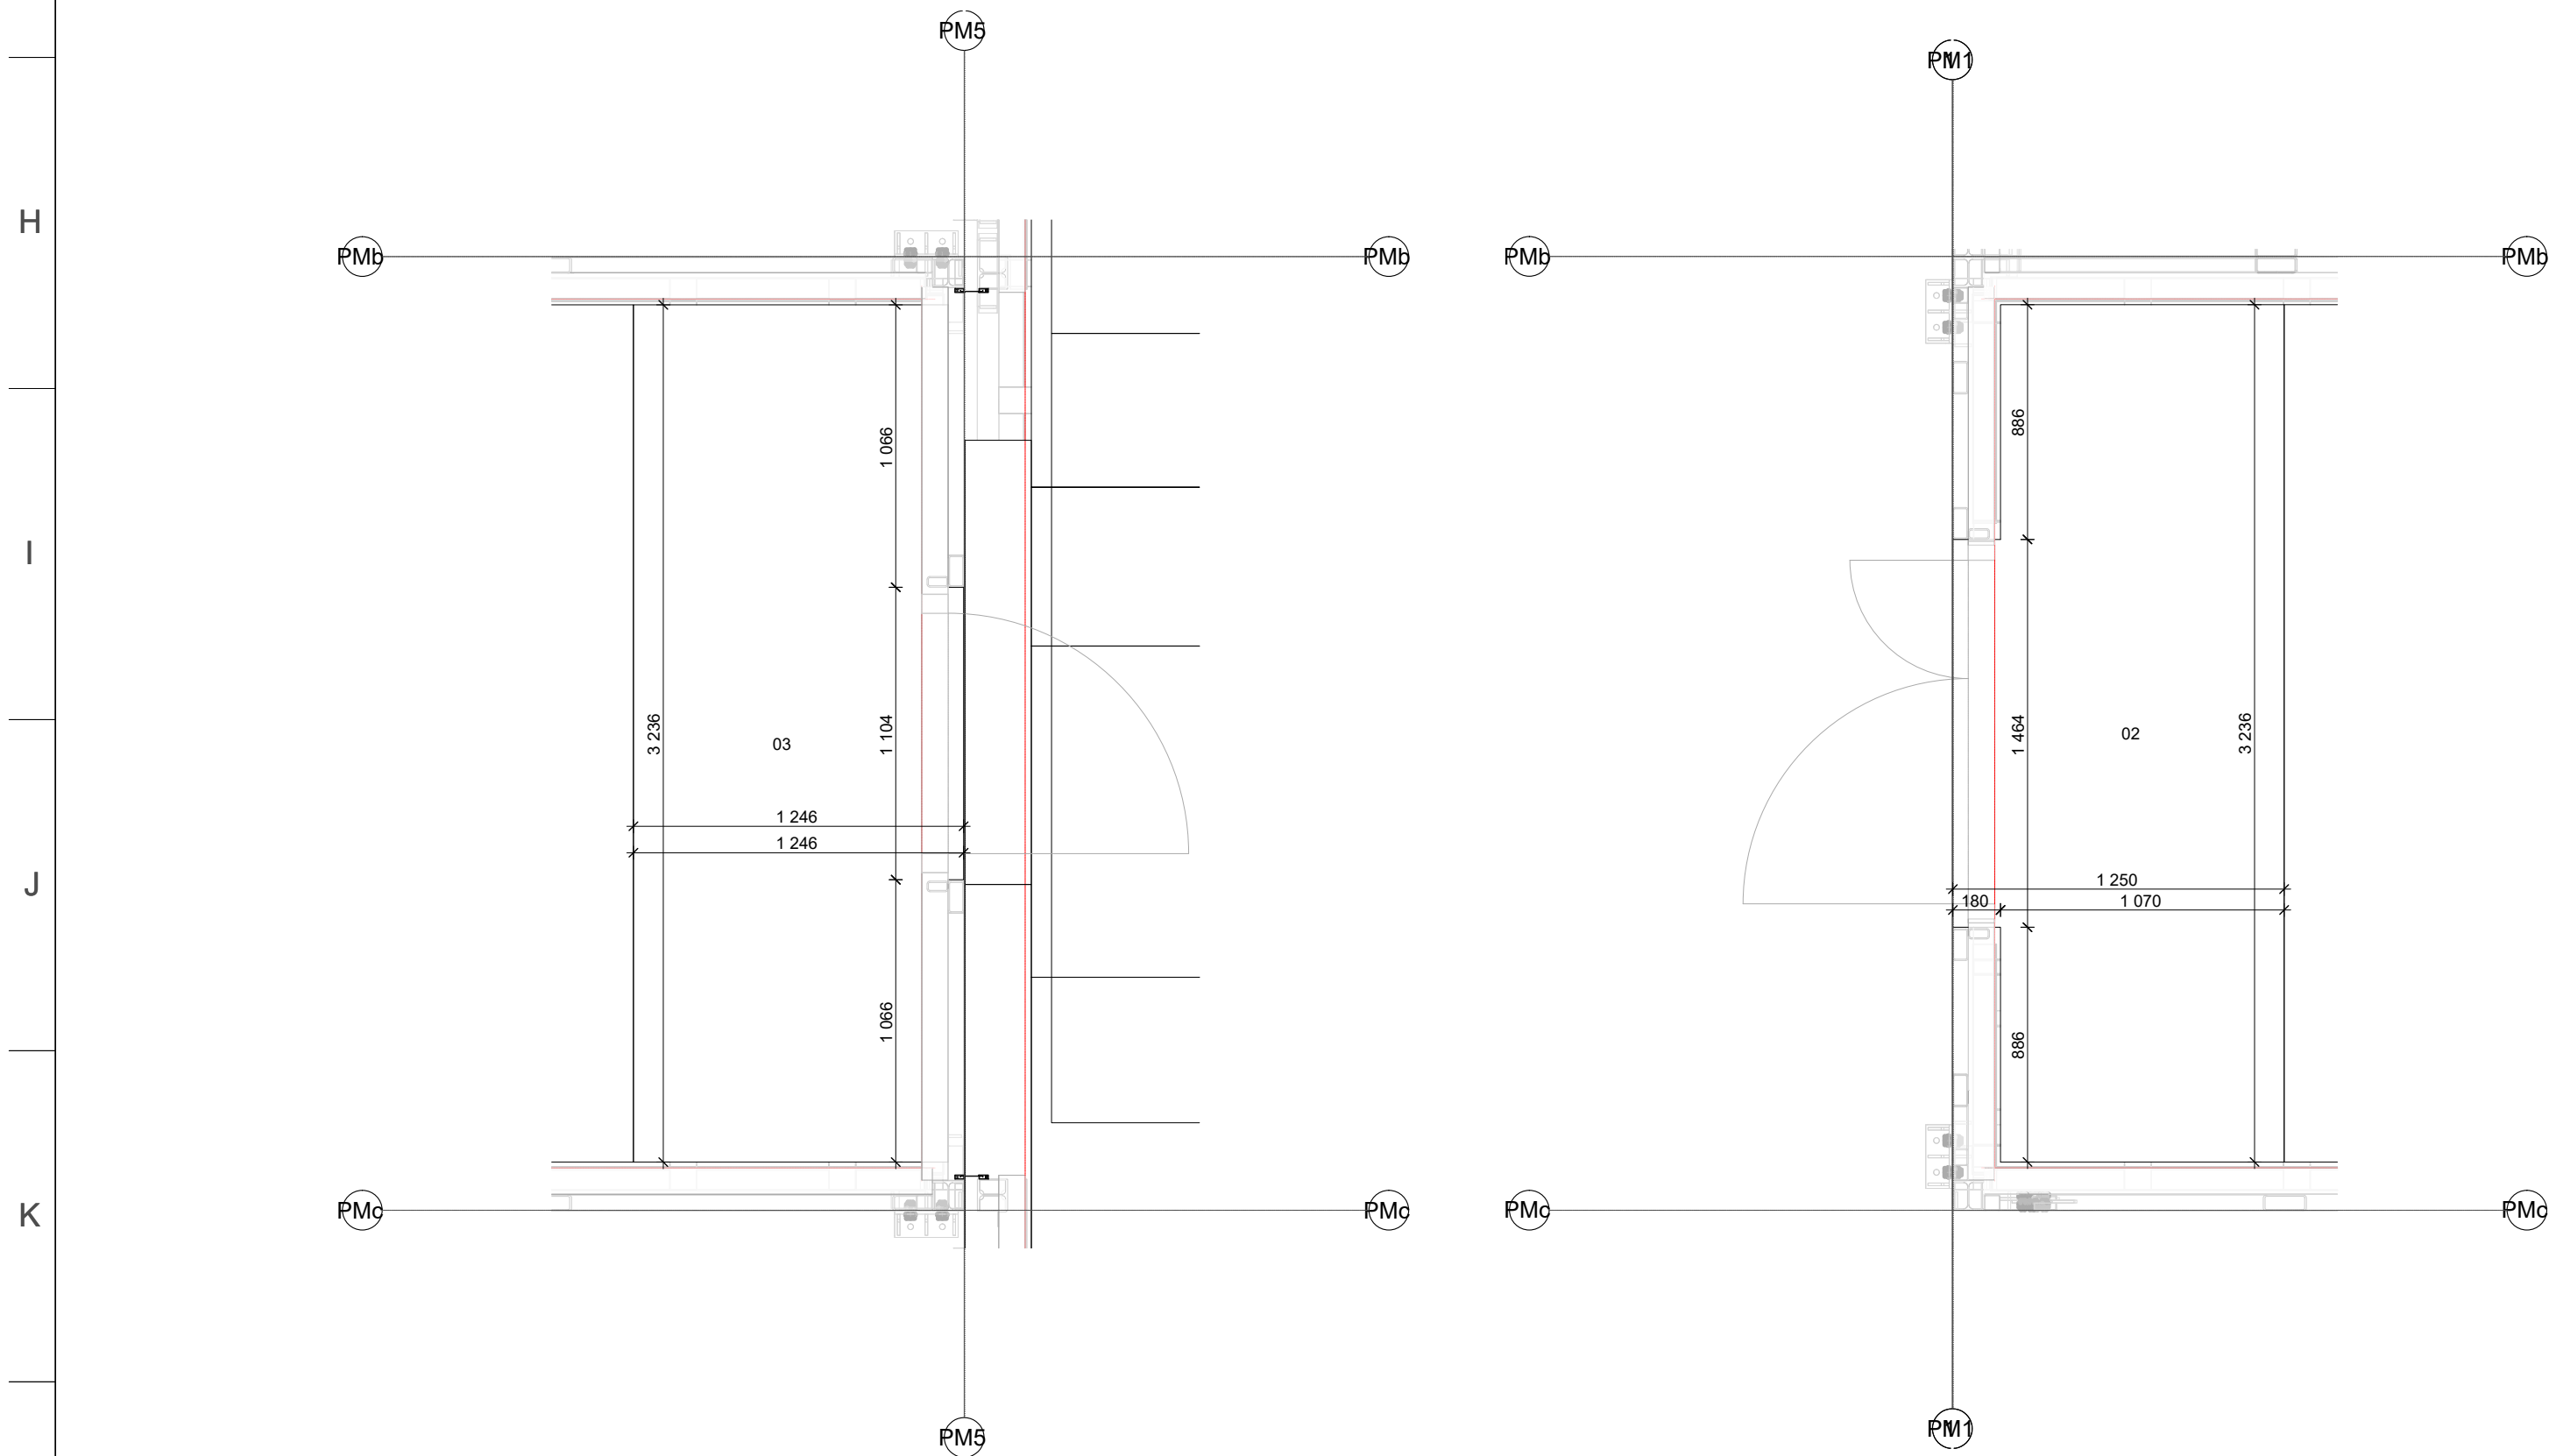


03 PM - Floor Plan - Cement Fibre - Board pos. 03
1 : 25

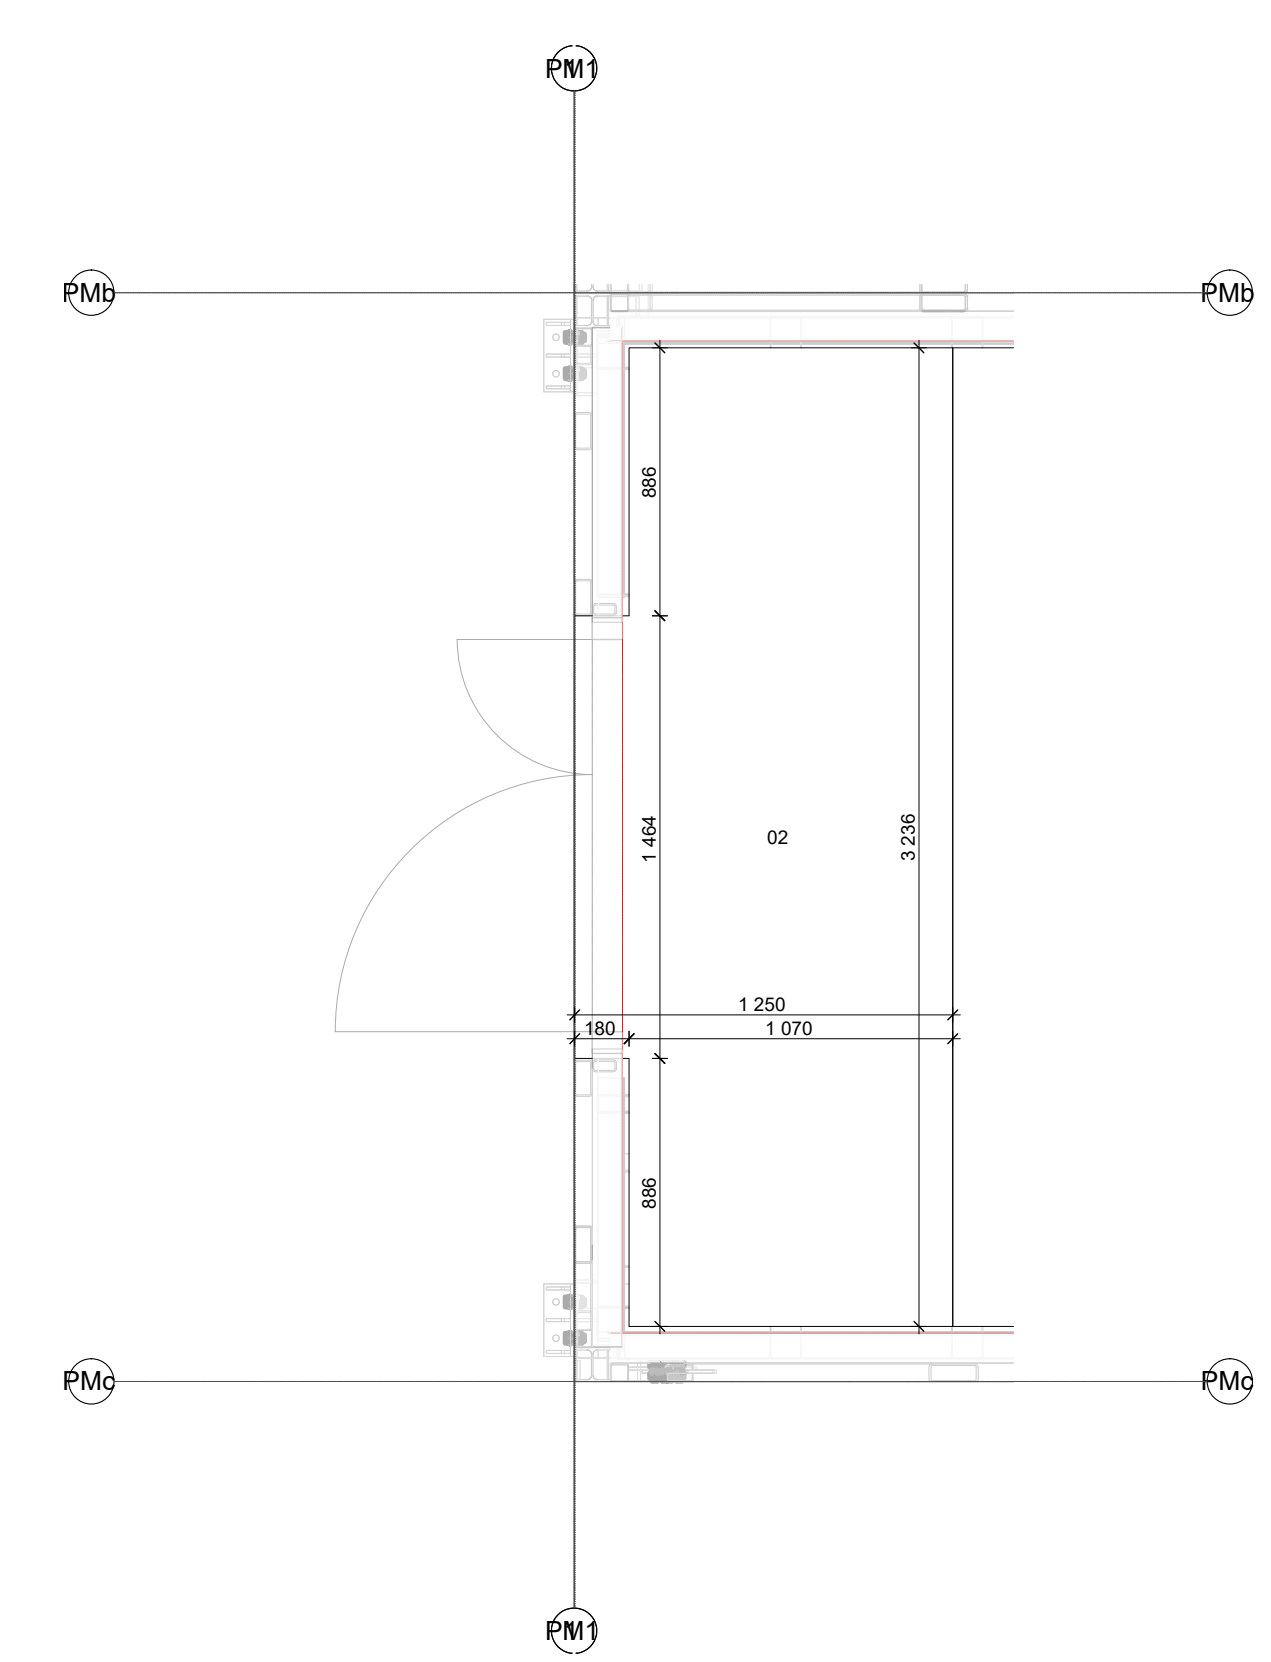




02 PM - Floor Plan - Cement Fibre - Board pos. 02
1 : 25

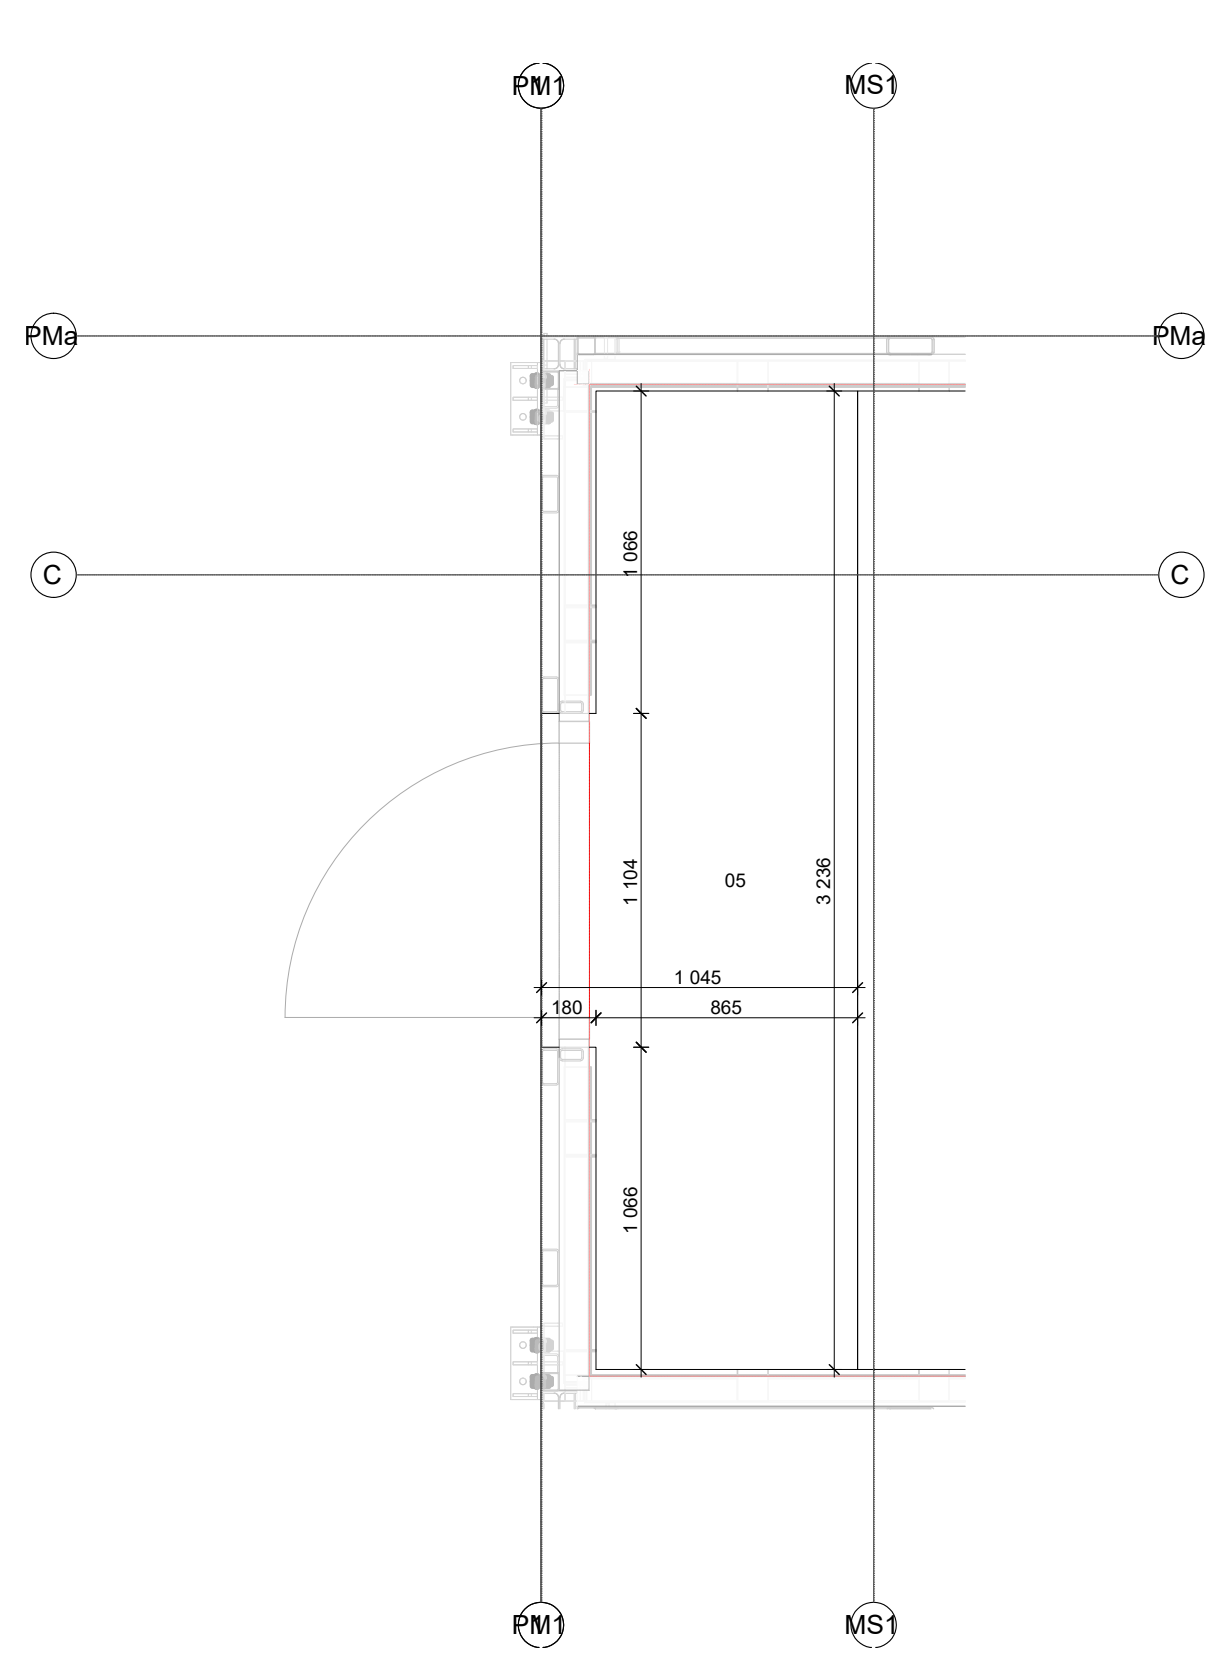

05 PM - Floor Plan - Cement Fibre - Board pos. 05
1 : 25

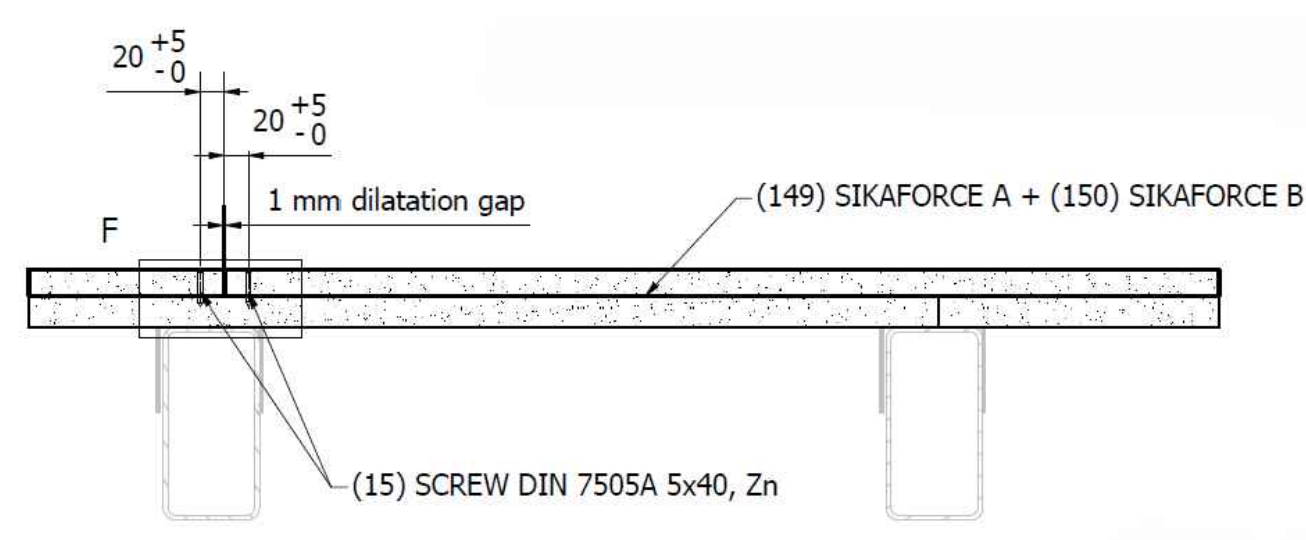

07 PM - Floor Plan - Cement Fibre - Board pos. 07
1 : 25

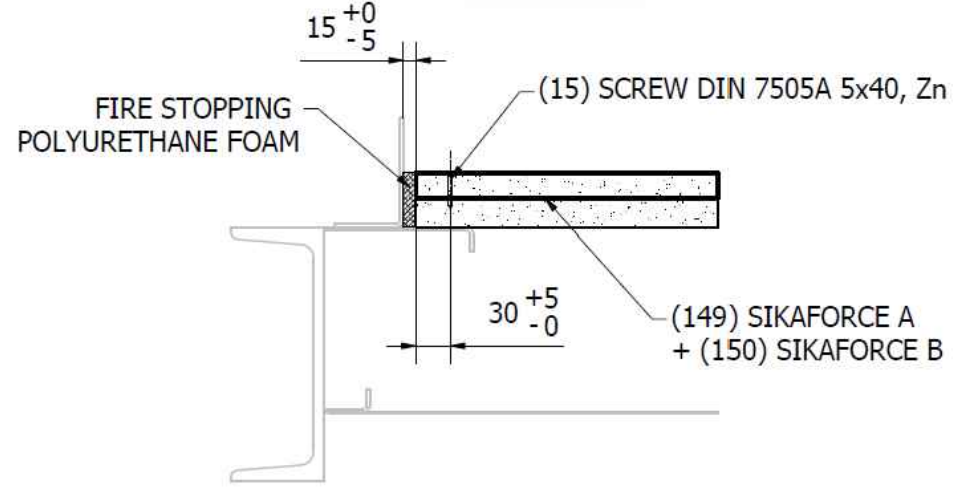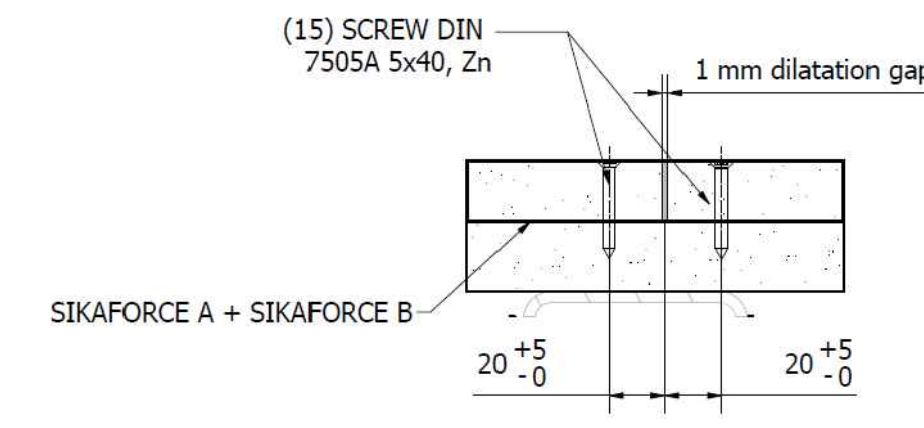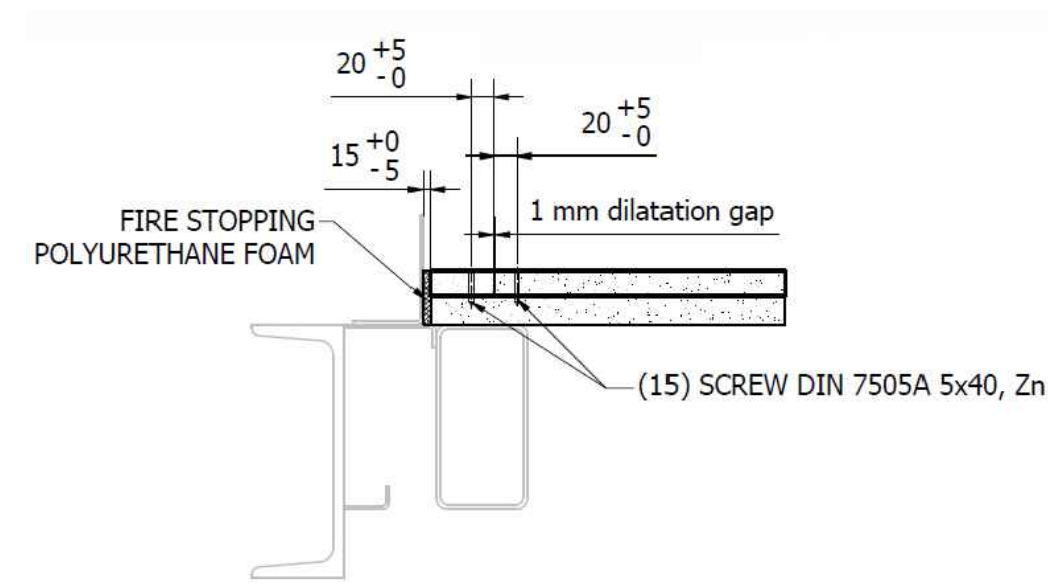

GENERAL NOTES:
- Edges of 2nd layer and 1st layer boards should not overlap - minimal overlap distance is 200 mm
- All detailed cutting should be done during installation
- 2nd layer boards should be 1250 mm across width and cutting should not be required

Installation notes:
- 2nd layer of Cetris board is only fixed in 1st Layer of Cetris board, use Self-taping screw DIN7505A TX 5x40, Zn
- 2nd layer of Cetris board needs to be glued to 1st layer of Cetris board using SIKAFORCE A + SIKAFORCE B - apply according to manufactures instruction
- Use approximately 10 pcs per 1 m² of Cetris board
- If board dimensions are smaller than 600 mm, min. 4 screws needs to be used

KEYNOTES

ASI - PM CEMENT FIBRE BOARD			
Mark	Height Manual [mm]	Width Manual [mm]	Count [pcs]
01	3 236	1 250	10
02	3 236	1 250	1
03	3 236	1 246	1
Grand total: 12			

ASI - MV CEMENT FIBRE BOARD			
Mark	Height Manual [mm]	Width Manual [mm]	Count [pcs]
04	3 236	1 250	5
05	3 236	1 045	1
06	3 236	1 001	1
07	180	2 004	1
08	3 236	465	1
09	3 236	650	2
10	3 236	706	1
11	180	1 104	1
Grand total: 13			

REFERENCE NOTES

KEY PLAN

R04	FOR MANUFACTURING	2026-09-02
R03	FOR MANUFACTURING	2026-08-11
R02	TRAFO CUTOUT ADDED	2026-07-24
R01	FOR MANUFACTURING	2026-05-26
REV.	DESCRIPTION	DATE

PROJECT NAME

ECO DC MONALISA

DRAWING NAME

PM – FIRST FLOOR LAYER LAYOUT – CEMENT FIBRE

PREPARED (ALSO SUBJECT RESPONSIBLE IF OTHER)

I. PUTICA / K. KOZINA / V. SPANIC / M. BRATIC

DOCUMENT RESPONSIBLE/ APPROVED

M. PACAK / J. CICVARIC

CAD / BIMSYSYSTEM

AUTODESK REVIT 2025

DOCUMENT NUMBER

ECODC-VRT-MDC19-00-DR-ASI-102-2

SHEET SIZE

A1

DRAWING SCALE

As Indicated

DATE (YYYYMM.DD)

2026-05-26

SHEET 1 OF 1

REVISION

R04