



LEGAL DISCLAIMER: THIS DOCUMENT AND THE CONTENTS HEREIN ARE CONFIDENTIAL AND THE SOLE PROPERTY OF VERTIV. REPRODUCTION, DISTRIBUTION OR UNAUTHORIZED USE OF THIS DOCUMENT OR ANY PARTS WITHIN THIS DOCUMENT ARE FORBIDDEN WITHOUT THE WRITTEN CONSENT OF VERTIV.


MV MODULE (1 : 100)

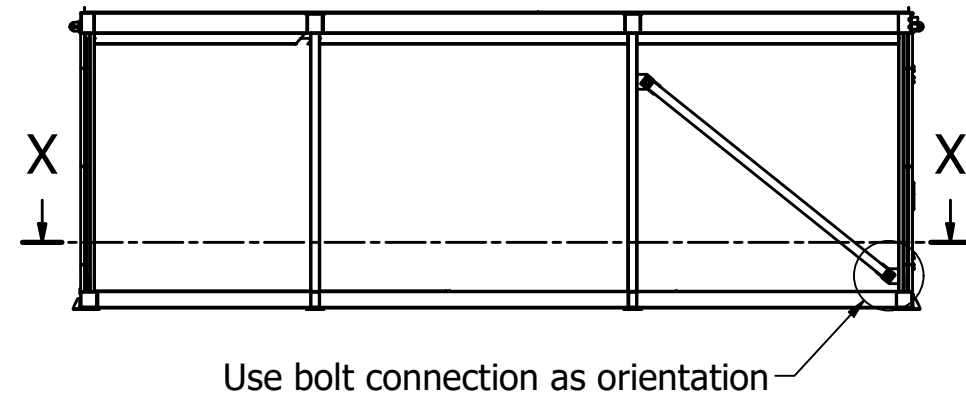


Typical door detail
J (1 : 10)

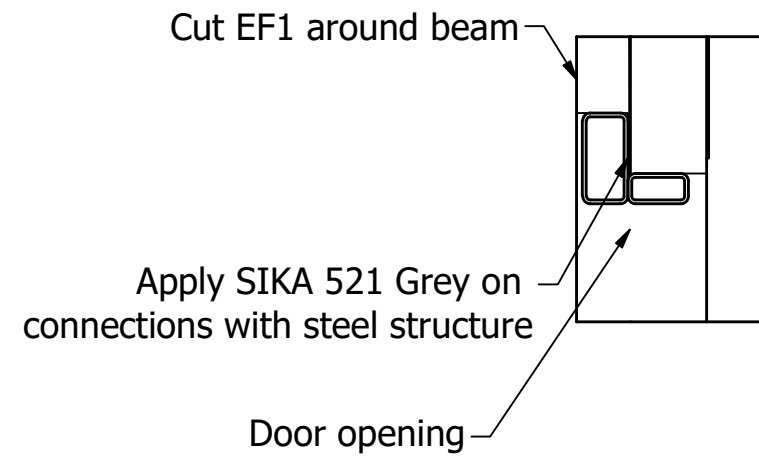


X-X (1 : 100)

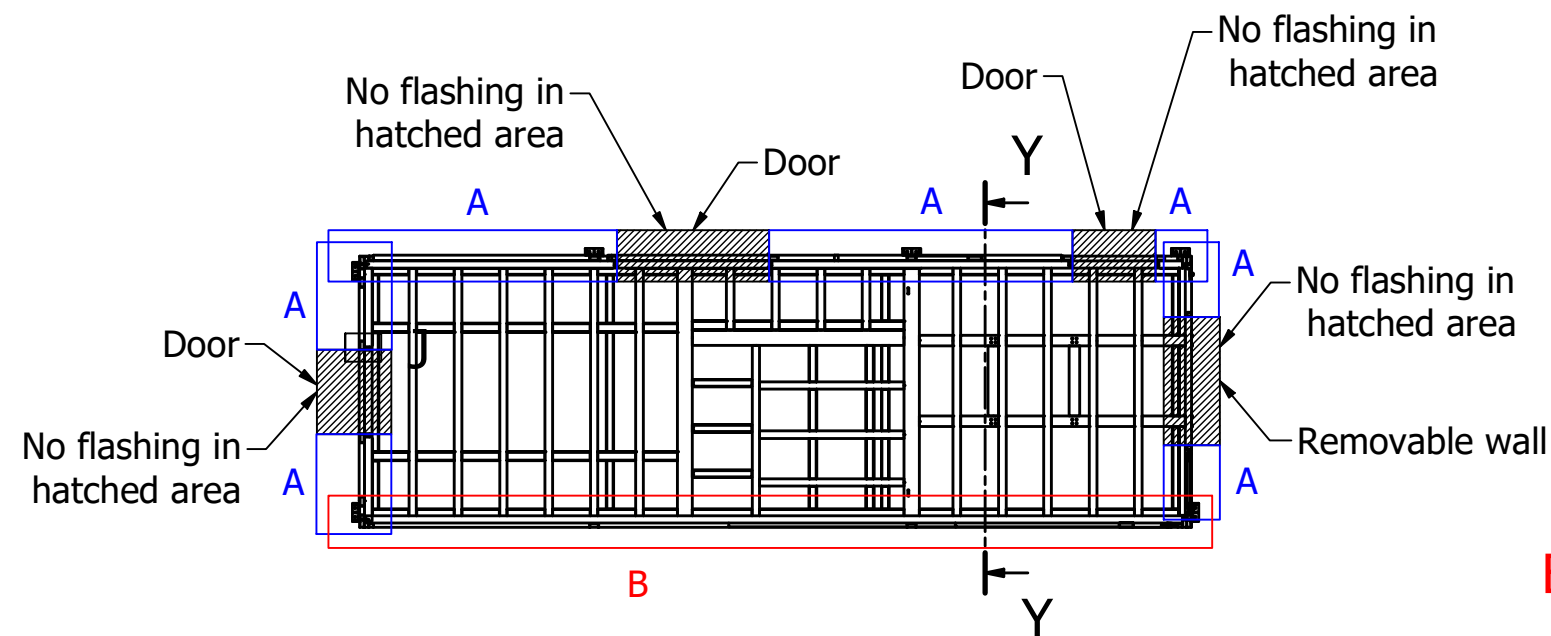


Y-Y (1 : 100)

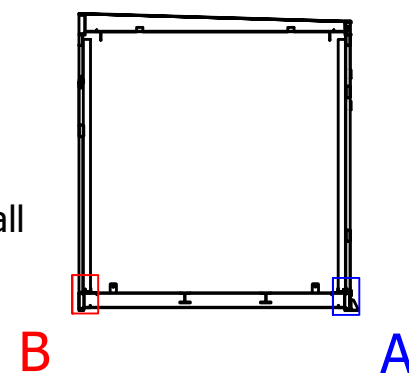

Typical detail
B (1 : 10)

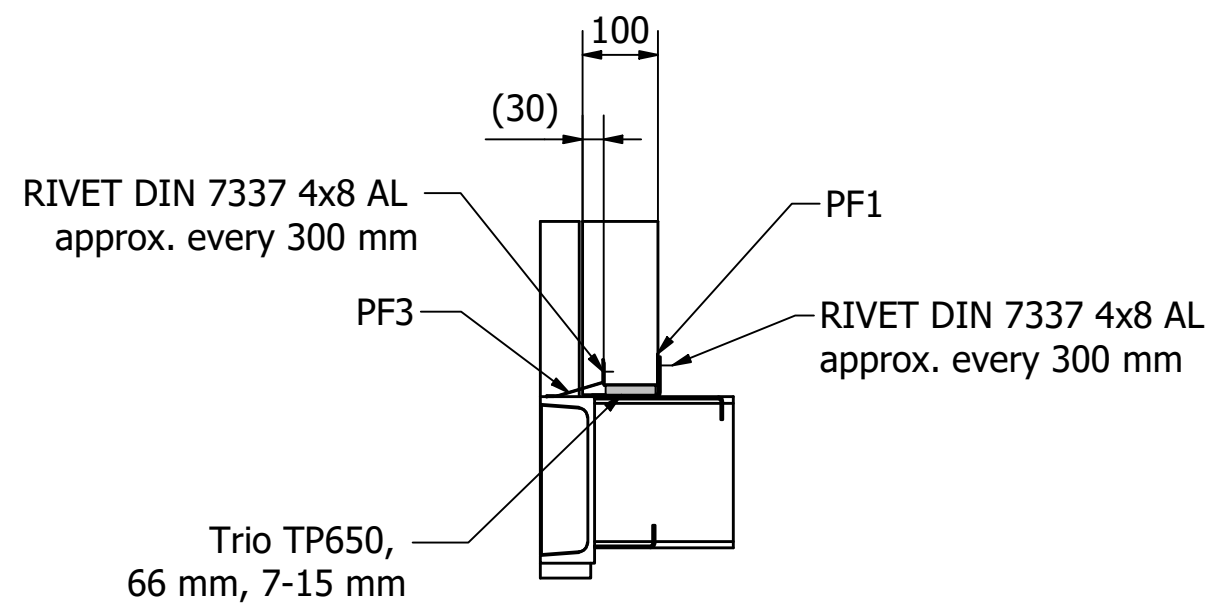


Typical detail
A (1 : 10)

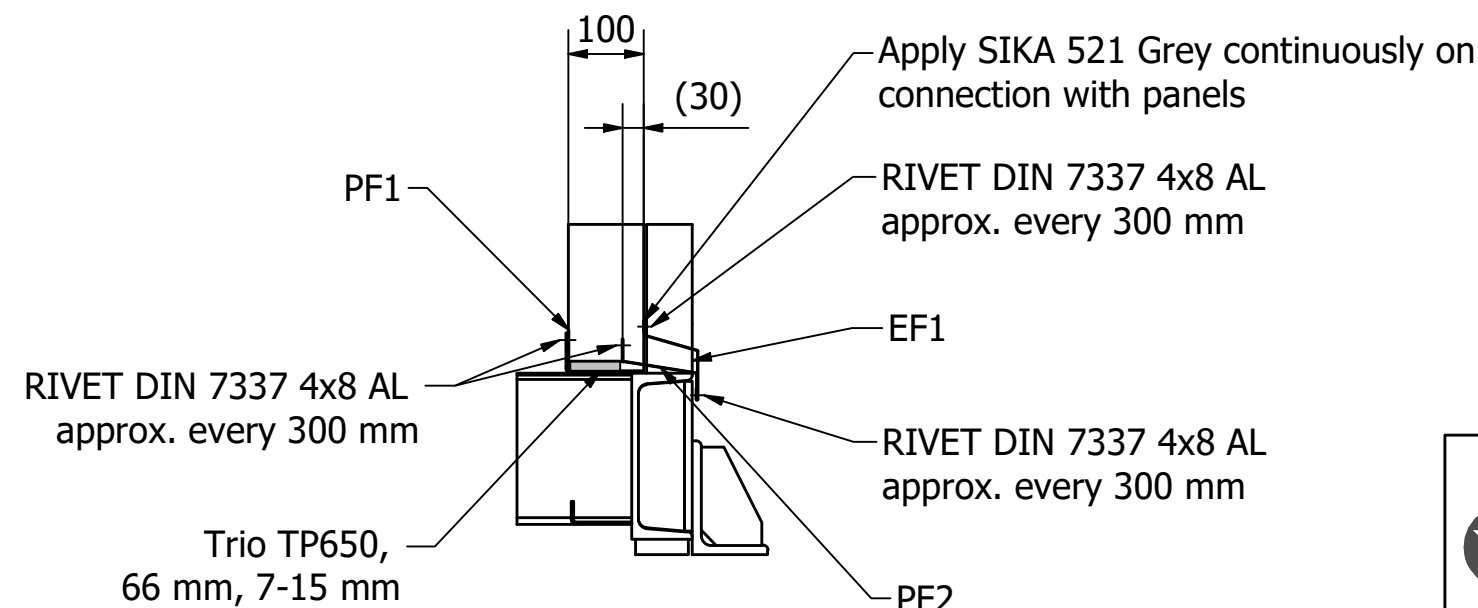


ITEM	PART NUMBER	DESCRIPTION	APPEARANCE	MASS	QTY
1	I00000285520	PF1 - Panel flashing	RAL9002	2,5 kg	10
2	I00000285528	PF2 - Panel flashing	RAL9006	3,1 kg	6
3	I00000286534	EF1 - External flashing 1	RAL9006	3,3 kg	4
4	I00000287836	PF3 - Panel flashing 3	RAL9006	2,1 kg	6
5	/	RIVER DIN 7337 4x8 AL	Al	0 kg	100*
6	/	Illbruck Trio TP650, 66 mm, 7-15 mm, 6 m roll	/	0 kg	28 m*
7	/	SIKA Sikaflex 521 UV Grey	Grey	0 kg	600 ml*


* quantities are indicative

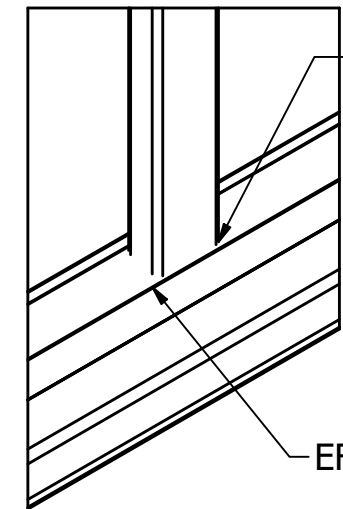

Detailed cutting around beams shall be done during installation, seal all gaps with SIKA 521 Grey

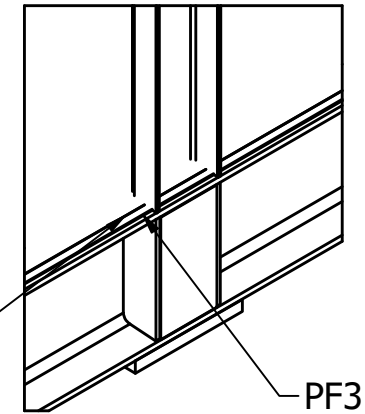


Detailed cutting around beams shall be done during installation, seal all gaps with SIKA 521 Grey

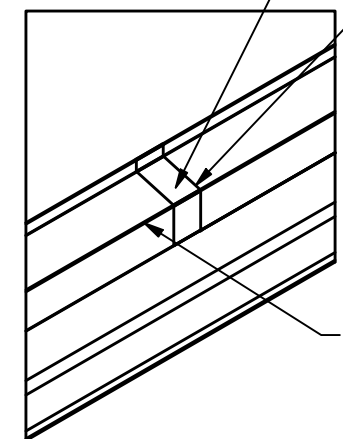

Apply SIKA 521 Grey on overlap and all connections

Overlap external flashing min. 50 mm

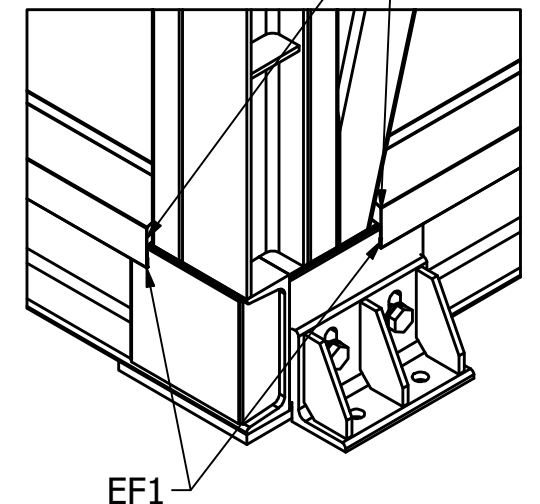

Fill gaps with SIKA 521 Grey


NOTES:

- All flashings are 3000 mm in length, cut to size during installation
- Apply blind rivets approx. every 300 mm
- Seal gaps with SIKA Sikaflex 521 UV Grey



CAD system
Autodesk Inventor

DIMENSIONAL TOLERANCES
FOR WELDED STRUCTURE
DIN EN ISO 13920 UNLESS
OTHERWISE SPECIFIED

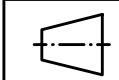

Sheet size

Scale

A2

1 : 100

Prepared (also subject responsible if other)
M. BRATIC

Document responsible/Approved
J.J. CICVARIC

REVISION HISTORY

REV	DESCRIPTION	DATE
R0	FOR CONSTRUCTION	22.5.2026.

Material	Finish	Weight
		N/A

Project name
ECO DC

Drawing name / Description
INSTALLATION FLASHING

Document number / Part number
ASI-104-MV

Rev	Date (DD.MM.YY)	Sheet
R0	21.5.2026.	1 (1)