

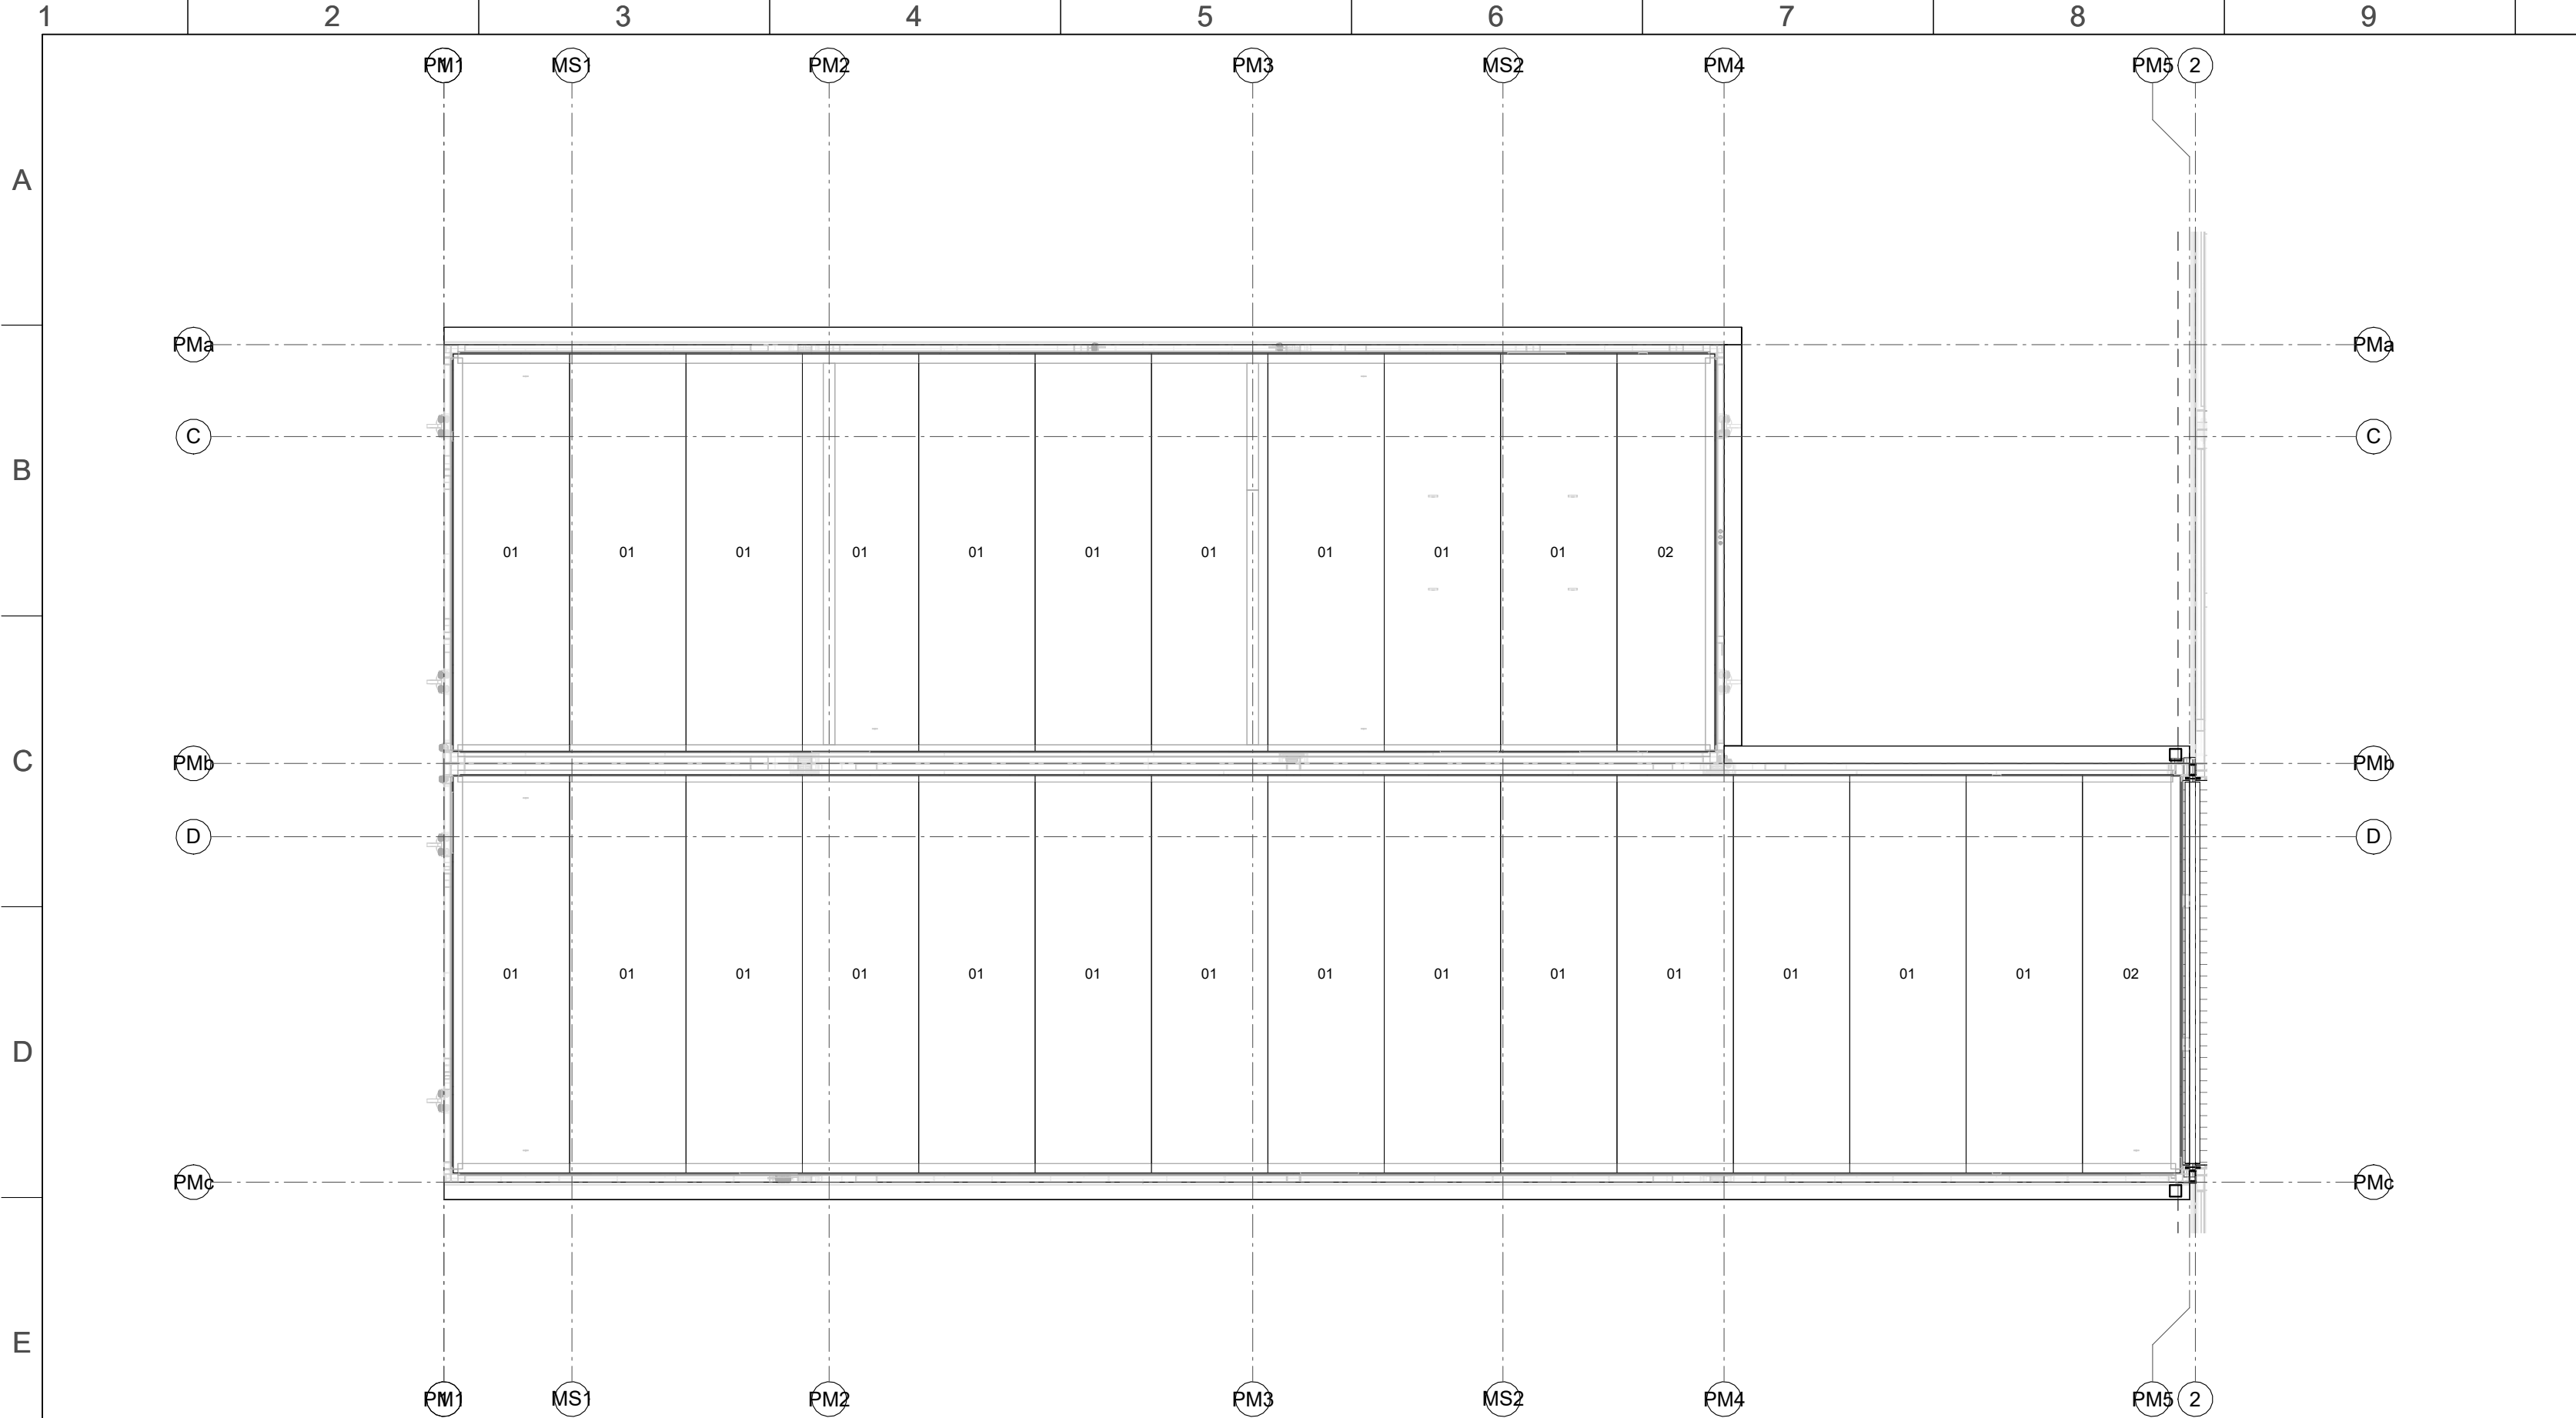
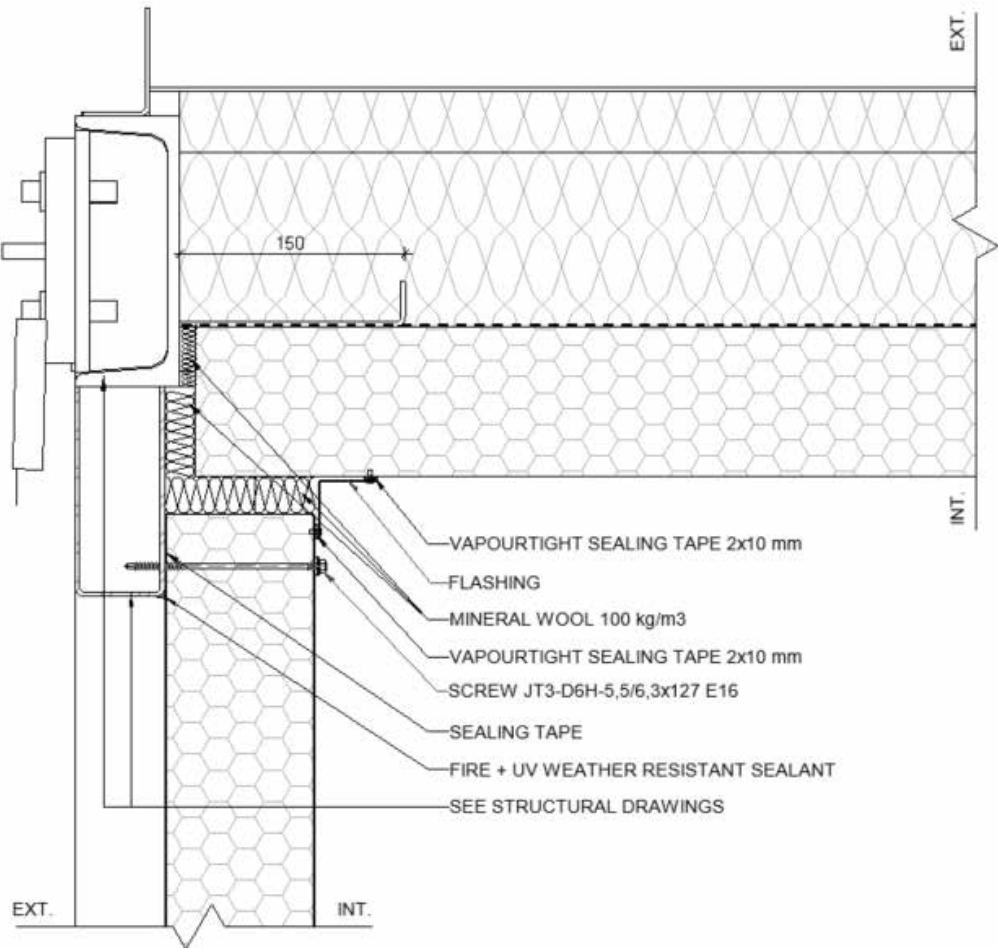


LEGAL DISCLAIMER: THIS DOCUMENT AND THE CONTENTS HEREIN ARE CONFIDENTIAL AND THE SOLE PROPERTY OF VERTIV GROUP CORP. REPRODUCTION, DISTRIBUTION OR UNAUTHORIZED USE OF THIS DOCUMENT OR ANY PARTS WITHIN THIS DOCUMENT ARE FORBIDDEN WITHOUT THE WRITTEN CONSENT OF VERTIV GROUP CORP.

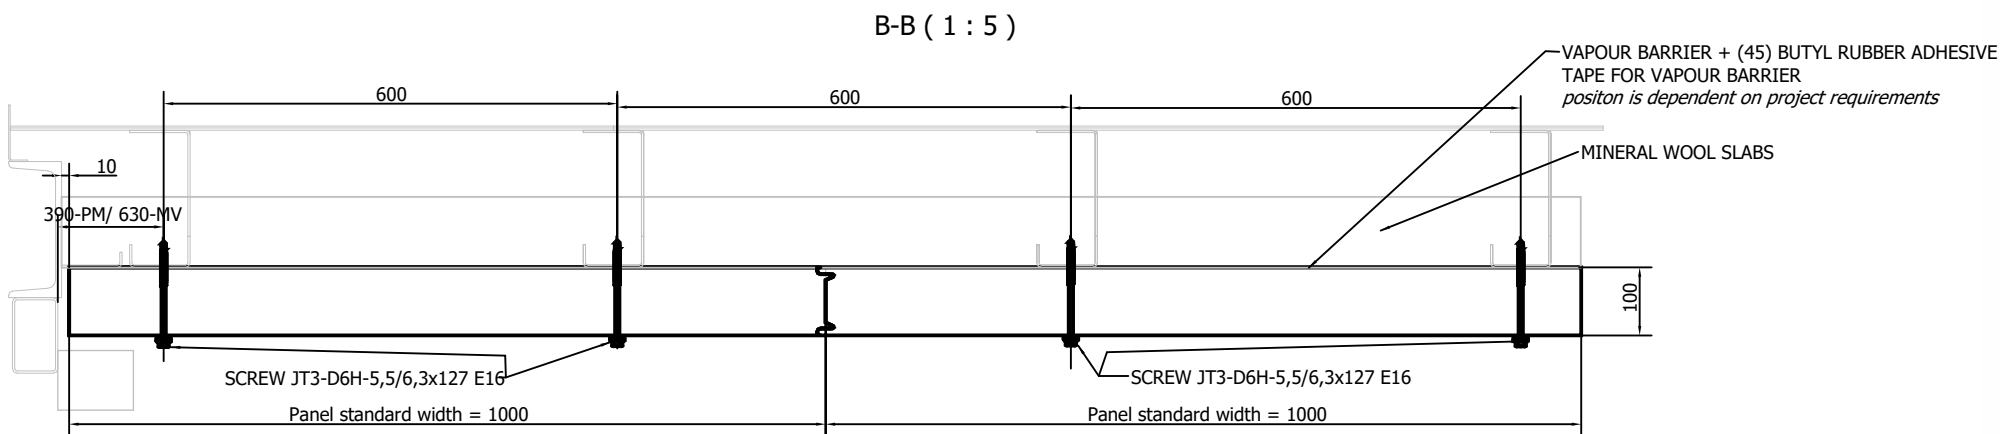

1 PM - Ceiling Layout - Ceiling Panel 100 Copy 2
1 : 50

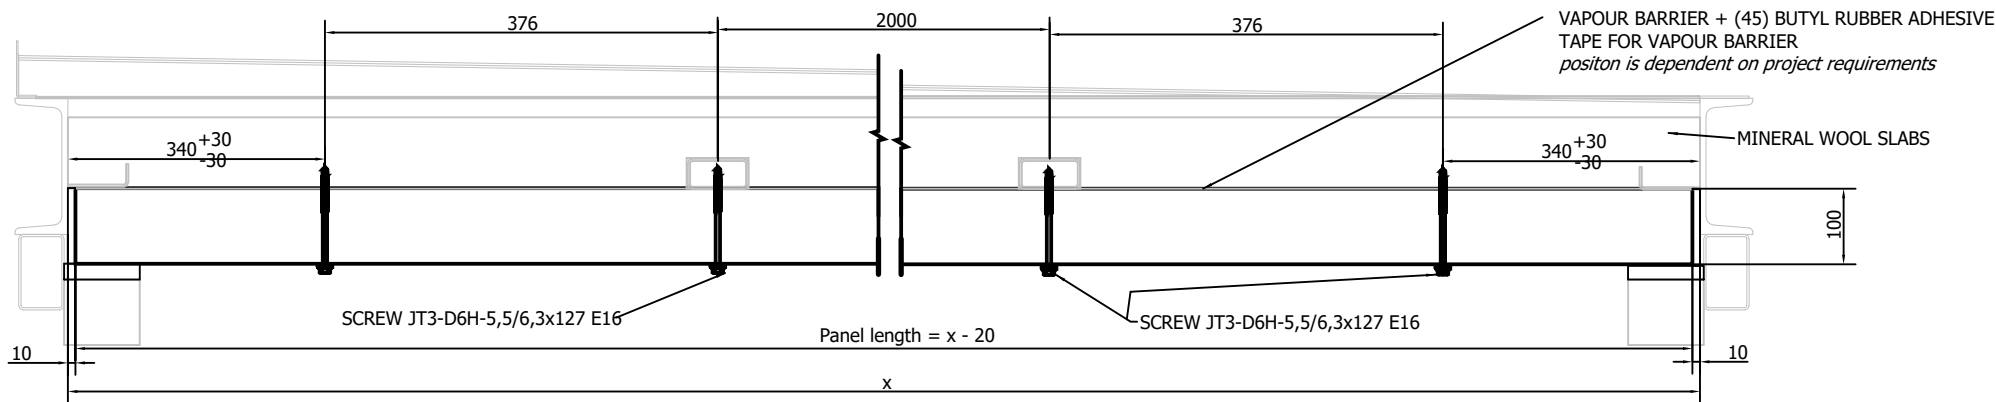

KEYNOTES

ASI - PM CEILING PANEL 100			
Mark	Height Manual [mm]	Width Manual [mm]	Count [pcs]
01	3415	1000	14
02	3415	840	1
Grand total: 15			


ASI - MV CEILING PANEL 100			
Mark	Height Manual [mm]	Width Manual [mm]	Count [pcs]
01	3415	1000	10
02	3415	840	1
Grand total: 11			

REFERENCE NOTES

GENERIC NAME	PRODUCT IN USE	PRODUCT CONSUMPTION
FIRE STOPPING POLYURETHANE FOAM	Promafom-C (or similar)	20 ml/m²
VAPOUR BARRIER	Vapour control layer-Sarnavap1000E, 1 roll is 125 m2	project dependent
(45) BUTYL RUBBER ADHESIVE TAPE FOR VAPOUR BARRIER	Sarnavap tape 20, 20mx15mm double-sided	0,08 pcs/m2**
(37) SCREW JT3-D6H-5,5/6,3x127 E16	Screw JT3-D6H-5,5/6,3x127 E16	5 pcs/m2**
MINERAL WOOL SLABS	project dependent	project dependent

* meter of floor perimeter that needs to be filled.
** meter squared of the project floor area (m2)
all quantities are indicative

KEY PLAN

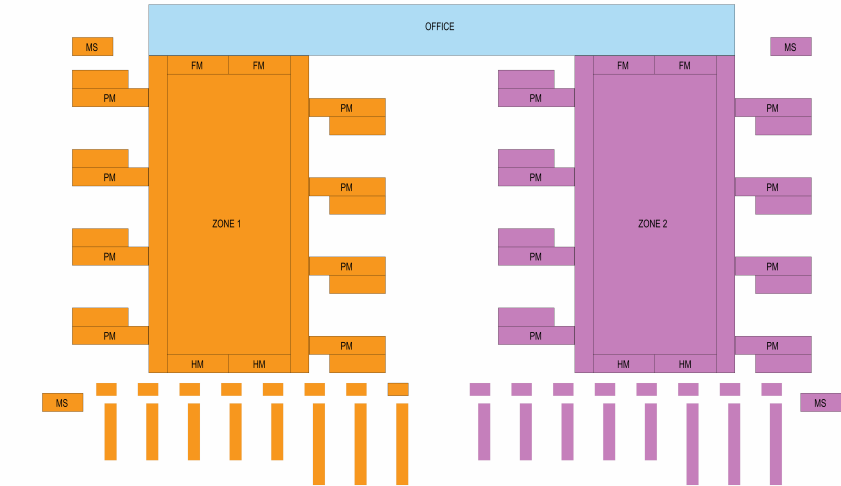

R01	FOR MANUFACTURING	2026-05-26
REV.	DESCRIPTION	DATE



PROJECT NAME

ECO DC MONALISA

DRAWING NAME

PM – CEILING LAYOUT – PANEL 100

PREPARED (ALSO SUBJECT RESPONSIBLE IF OTHER)
I. PUTICA / K. KOZINA / V. SPANIC
DOCUMENT RESPONSIBLE / APPROVED
M. PACAK / J. CICVARIC
CAD / BIM SYSTEM AUTODESK REVIT 2025

DOCUMENT NUMBER ASI-105-PM			SHEET 1 OF 1
SHEET SIZE A2	DRAWING SCALE 1 : 50	DATE (YYYYMM-DD) 2026-05-26	REVISION R01