




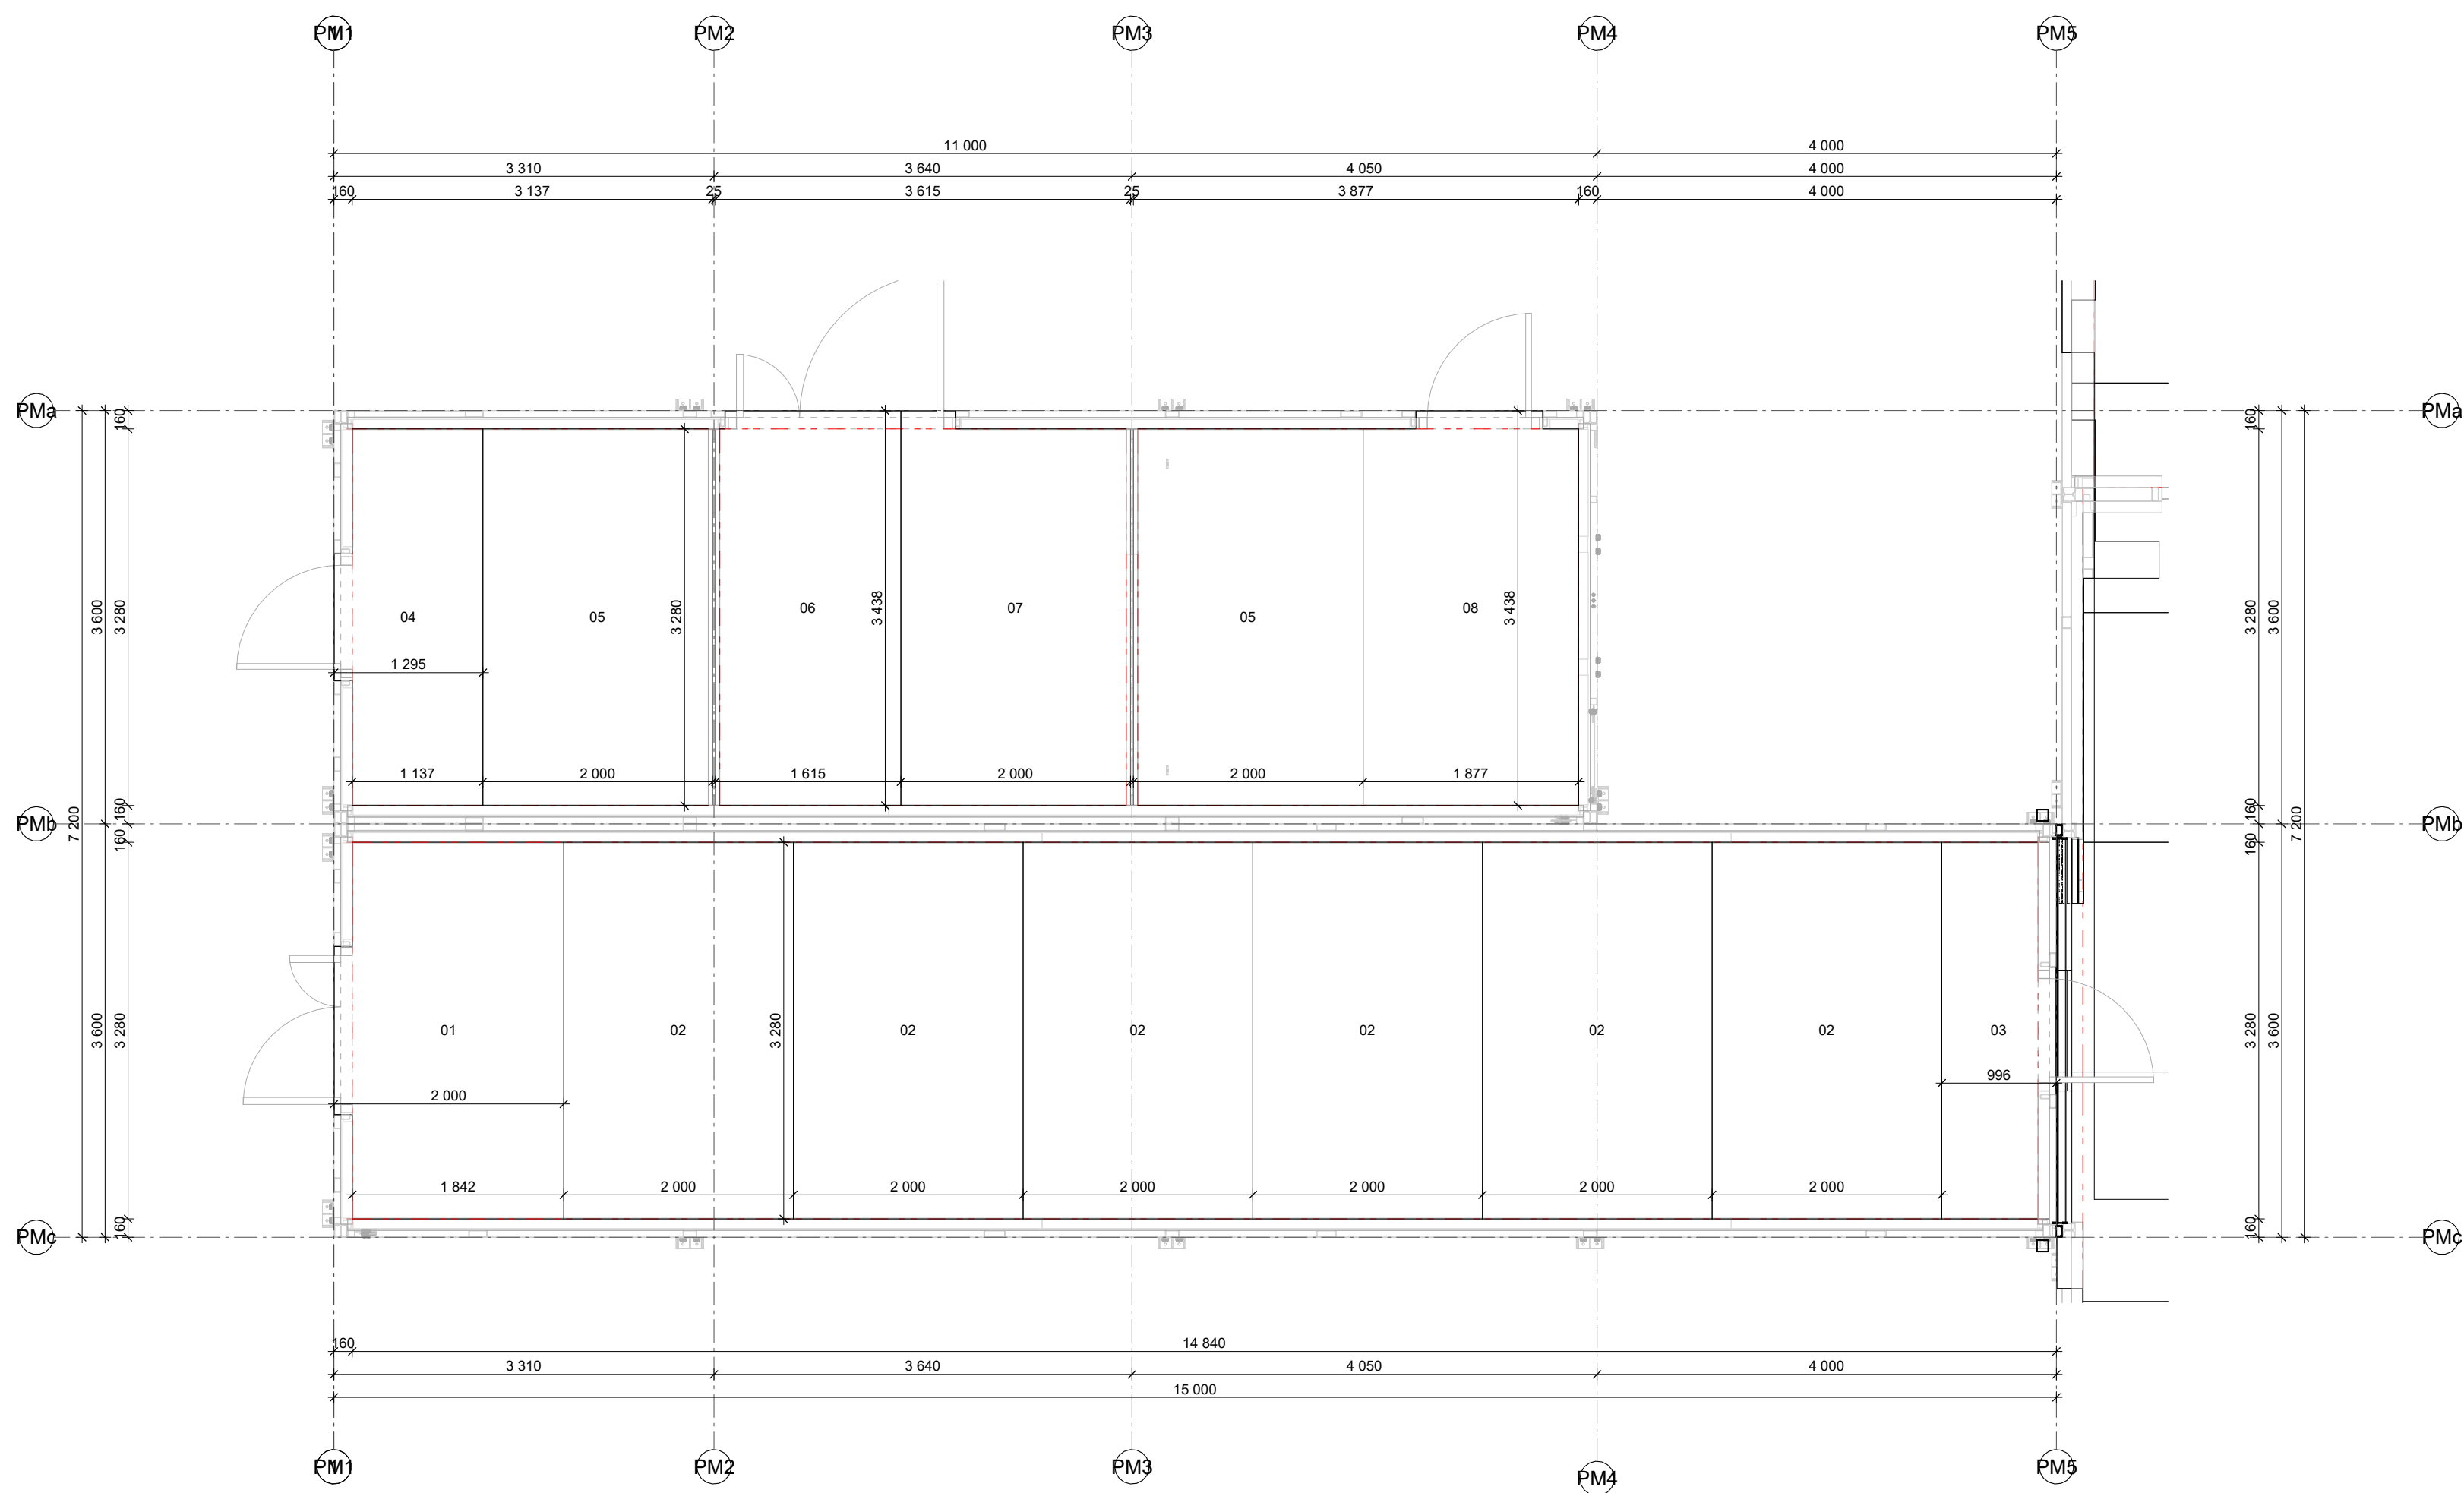


1 PM - FIRST FLOOR LAYER LAYOUT - VINYL
1:50

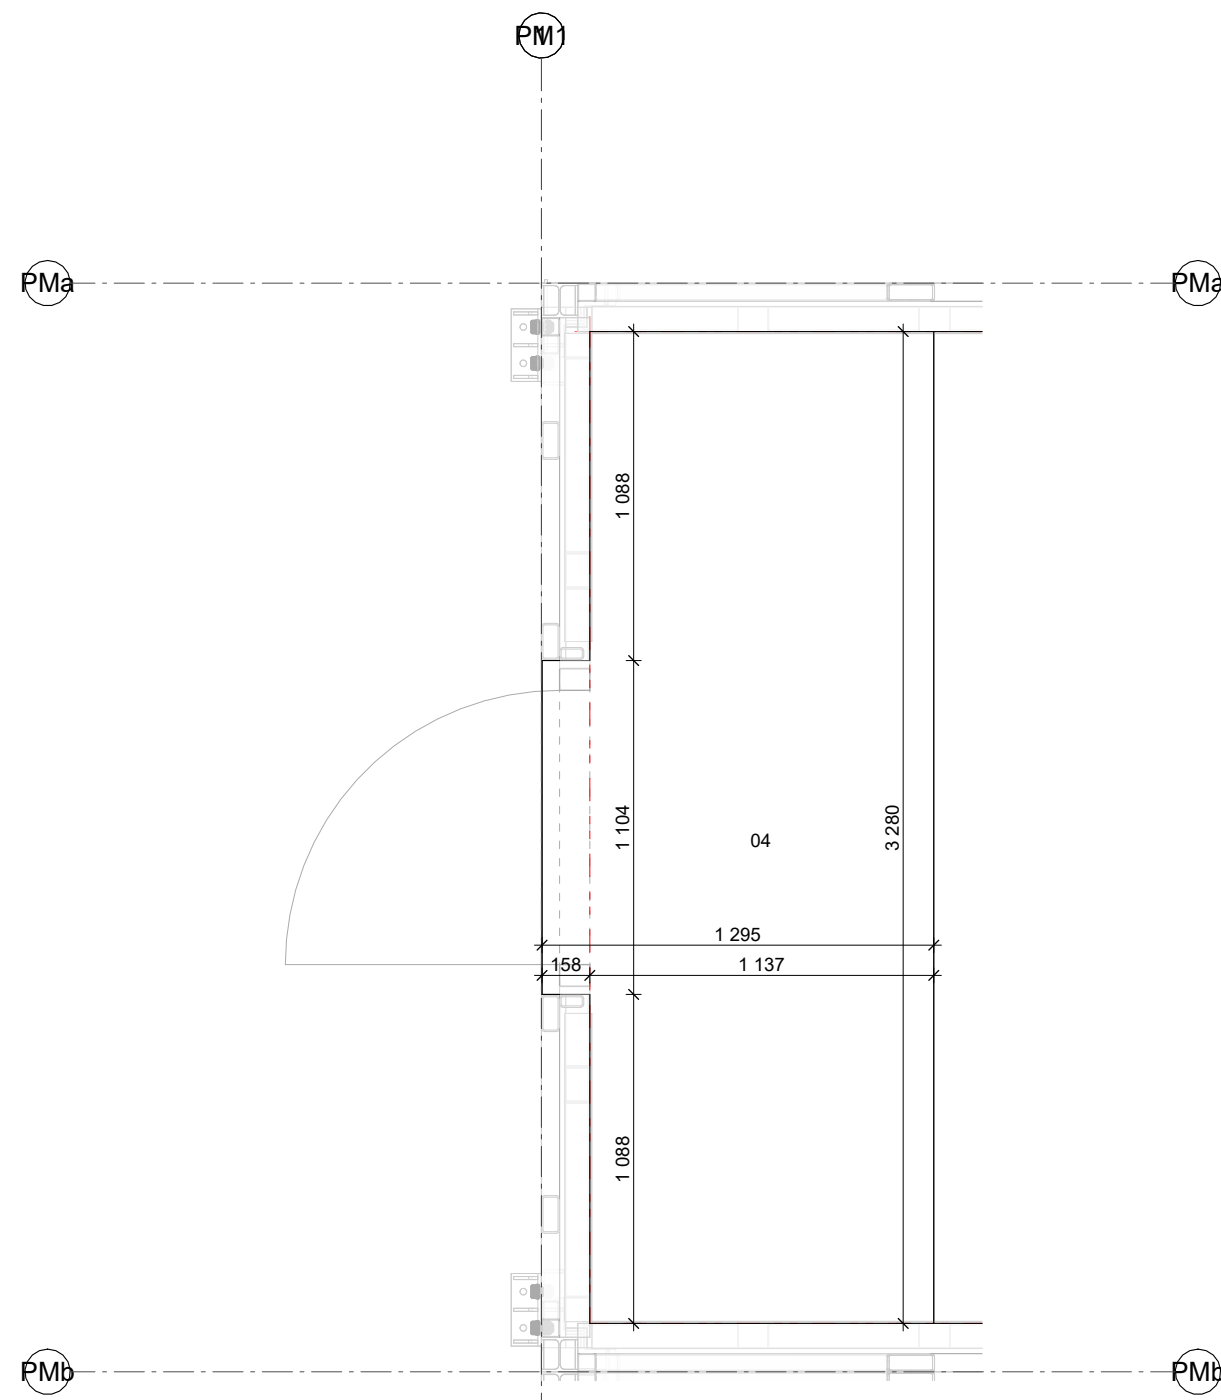


4 PM - Floor Plan - Vinyl - Board pos. 04 Copy 1
1:25

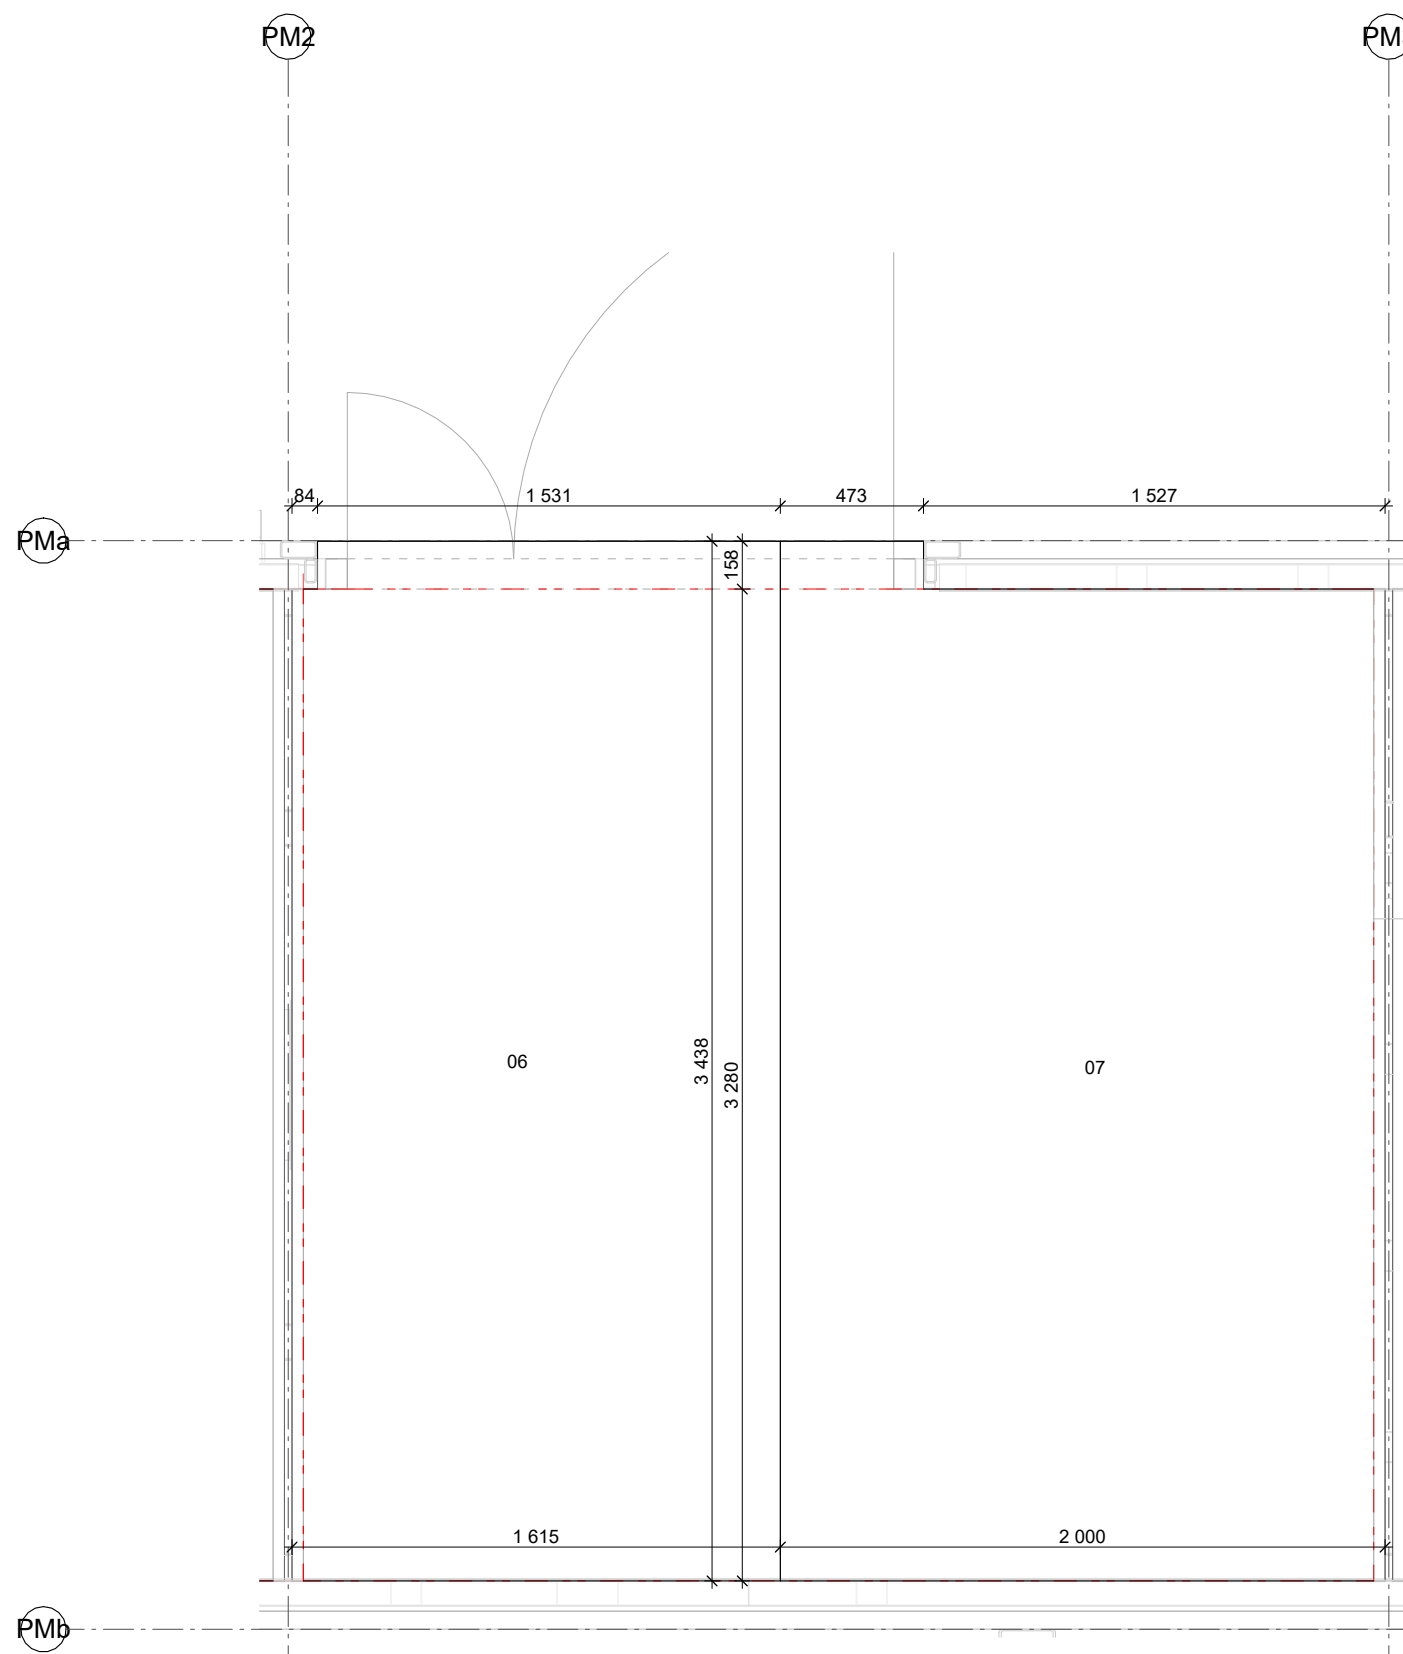


6/7 PM - Floor Plan - Vinyl - Board pos. 06/07 Copy 1
1:25

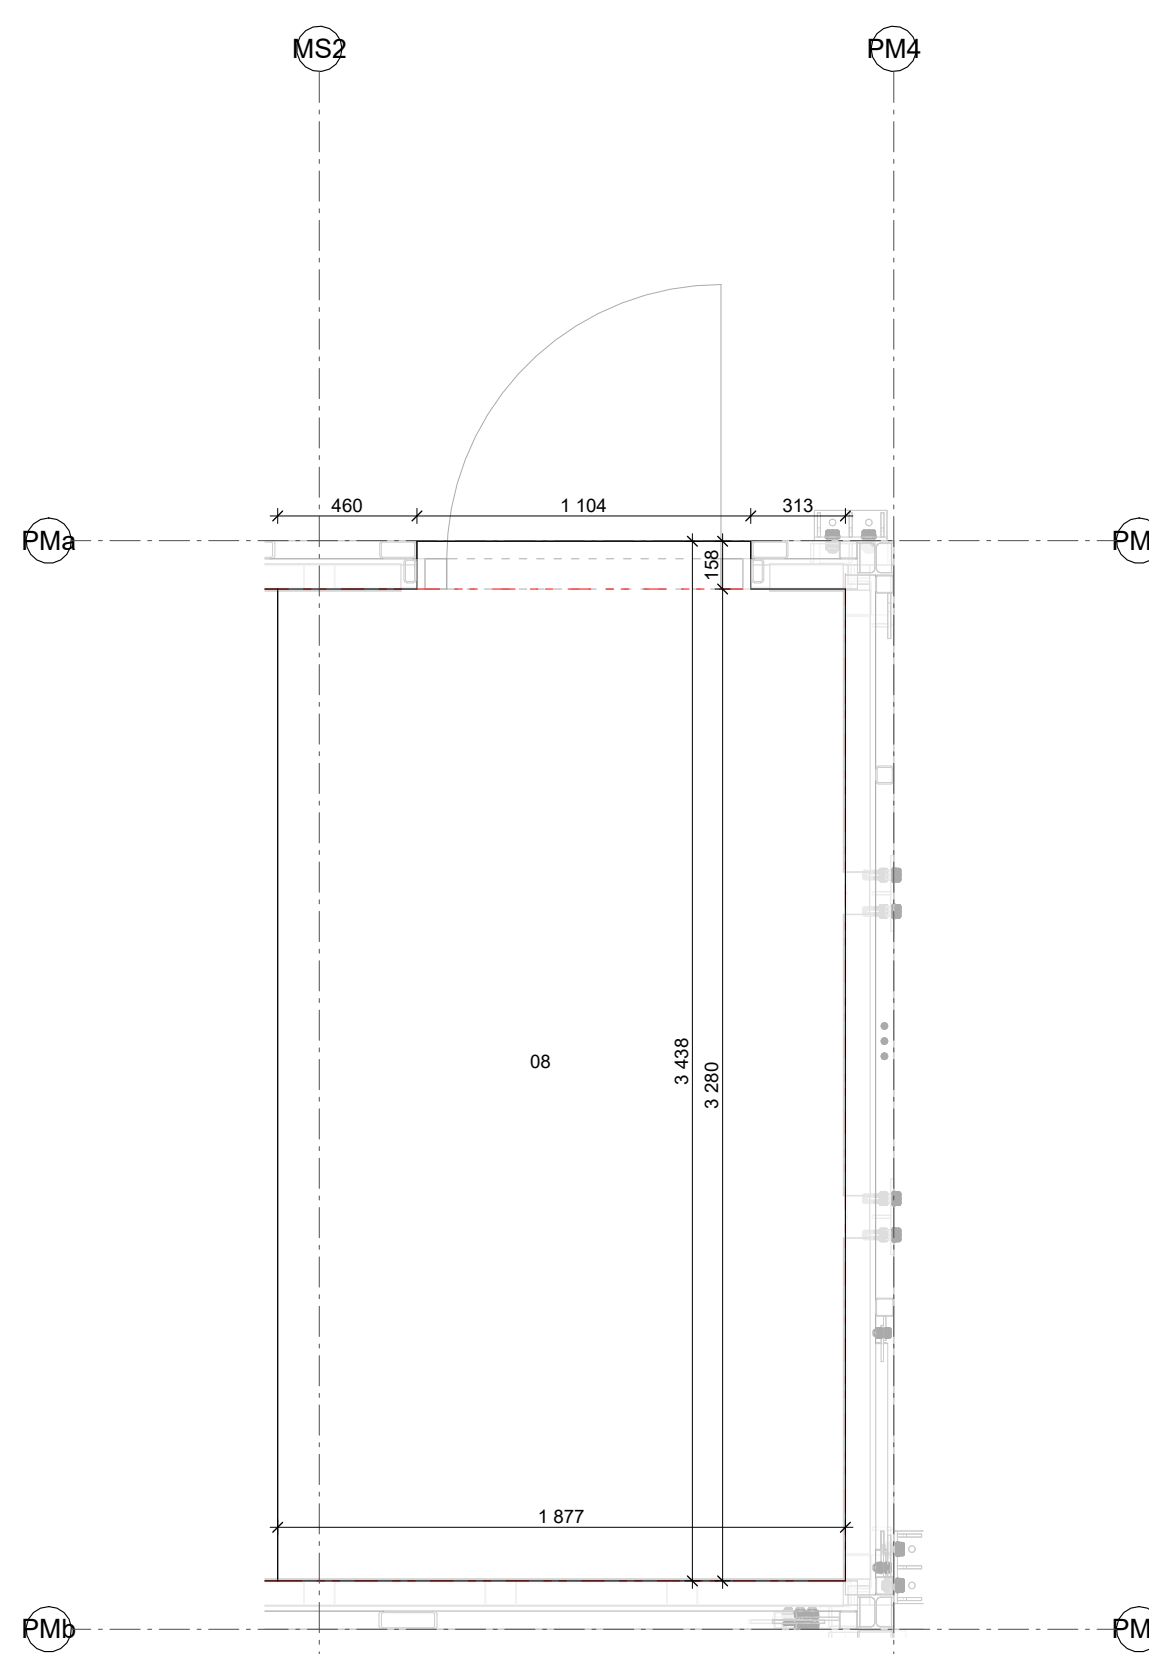

8 PM - Floor Plan - Vinyl - Board pos. 08 Copy 1
1:25



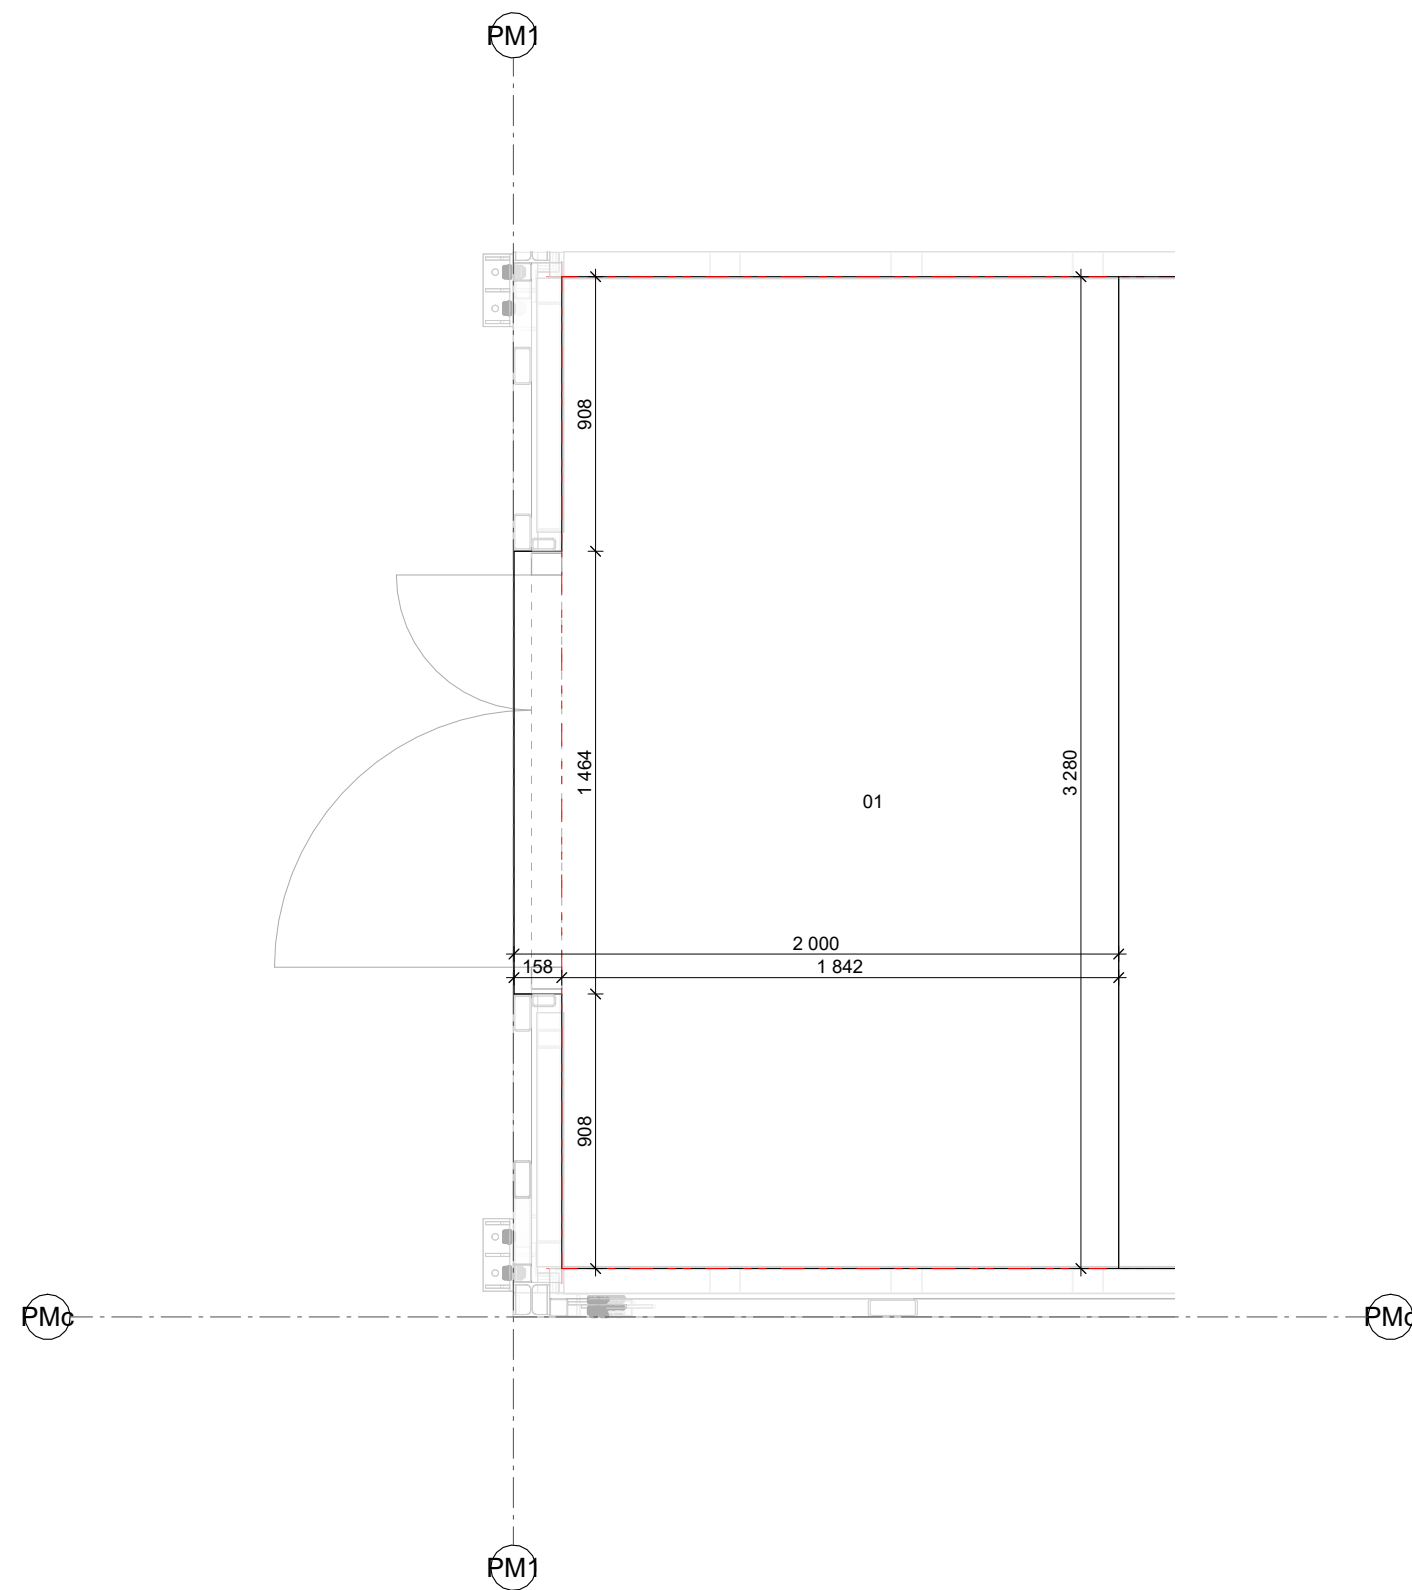


01 PM - Floor Plan - Vinyl - Board pos. 01 Copy 1
1:25

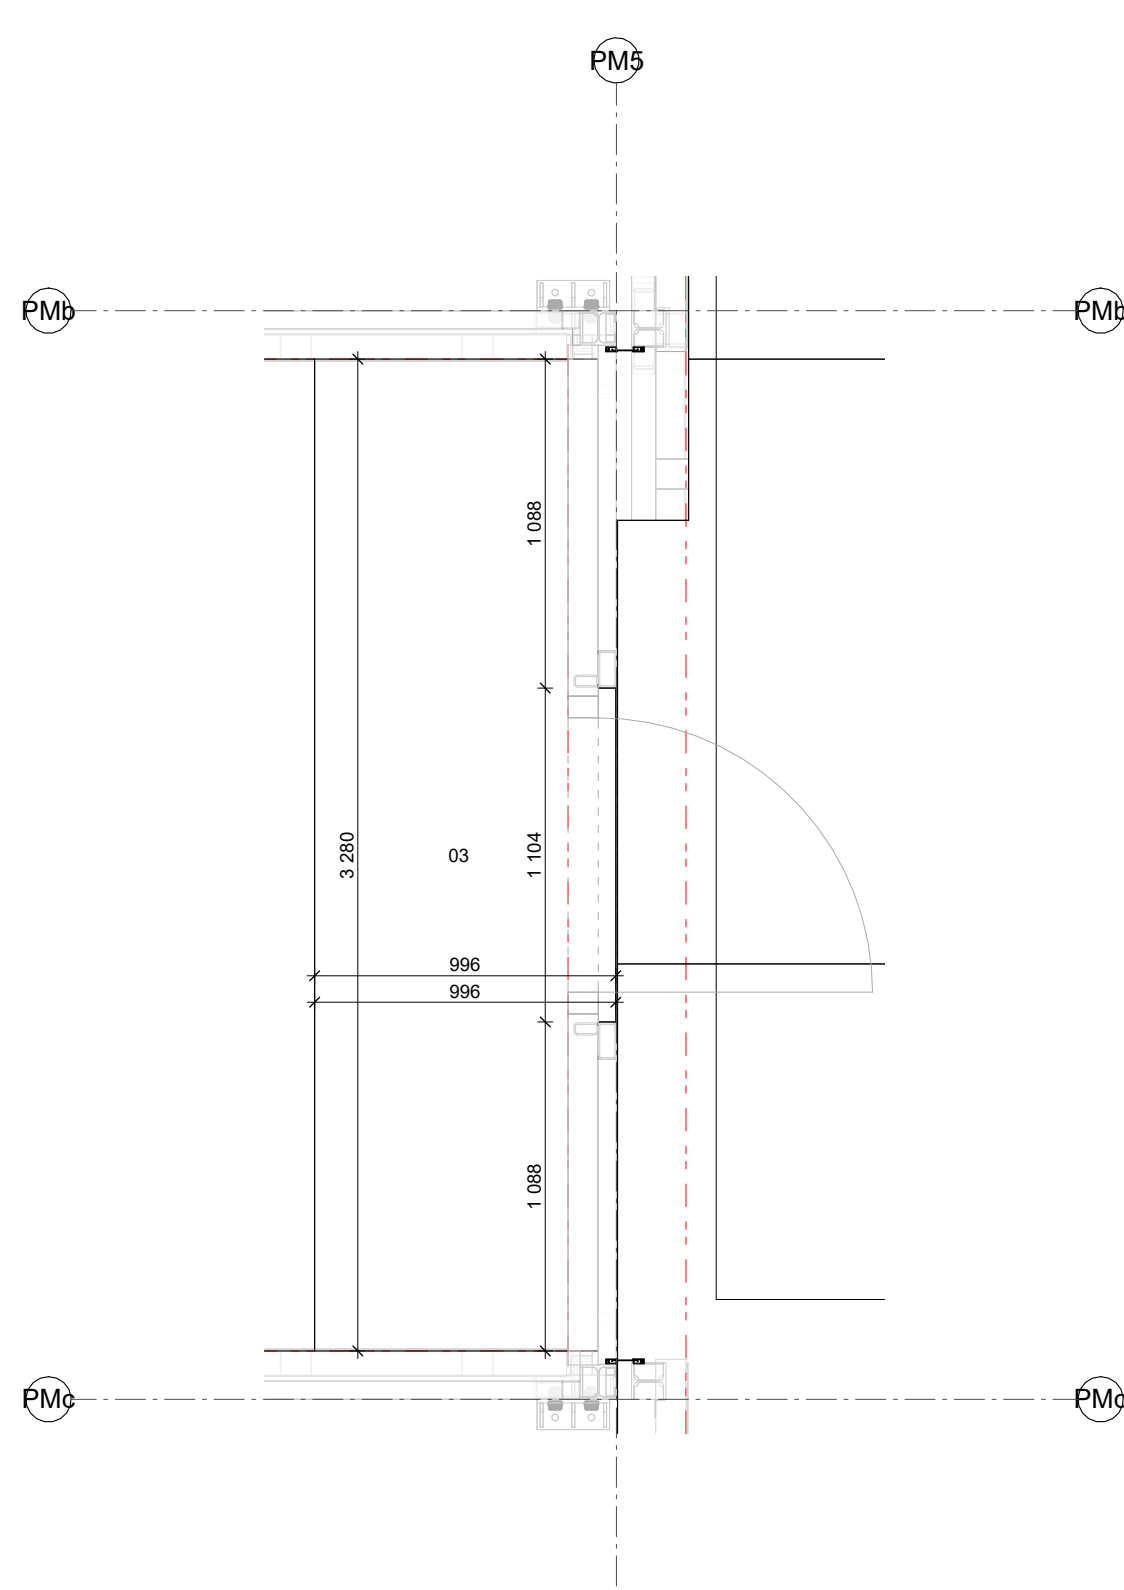


3 PM - Floor Plan - Vinyl - Board pos. 03 Copy 1
1:25

- Room $\leq 40 \text{ m}^2$: a copper strip around the edge of the room, placed 15 cm from the walls, diagonally. This strip should be earthed at both ends.

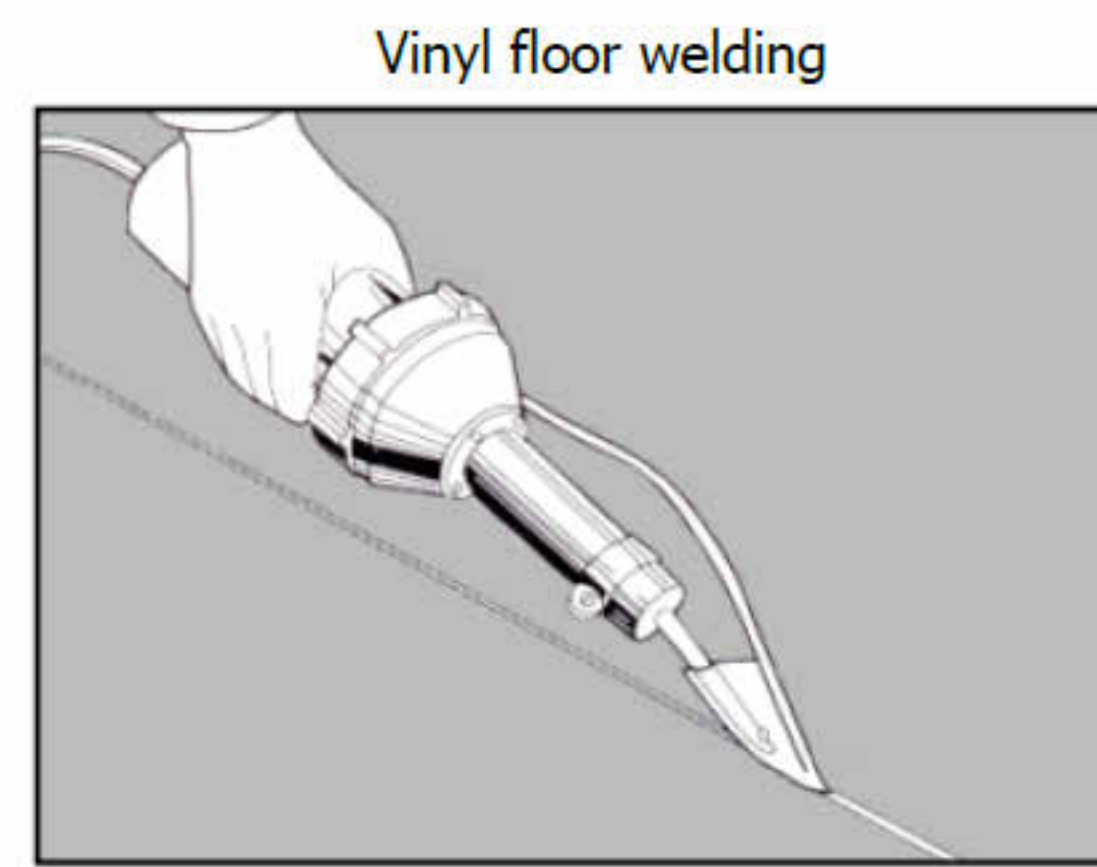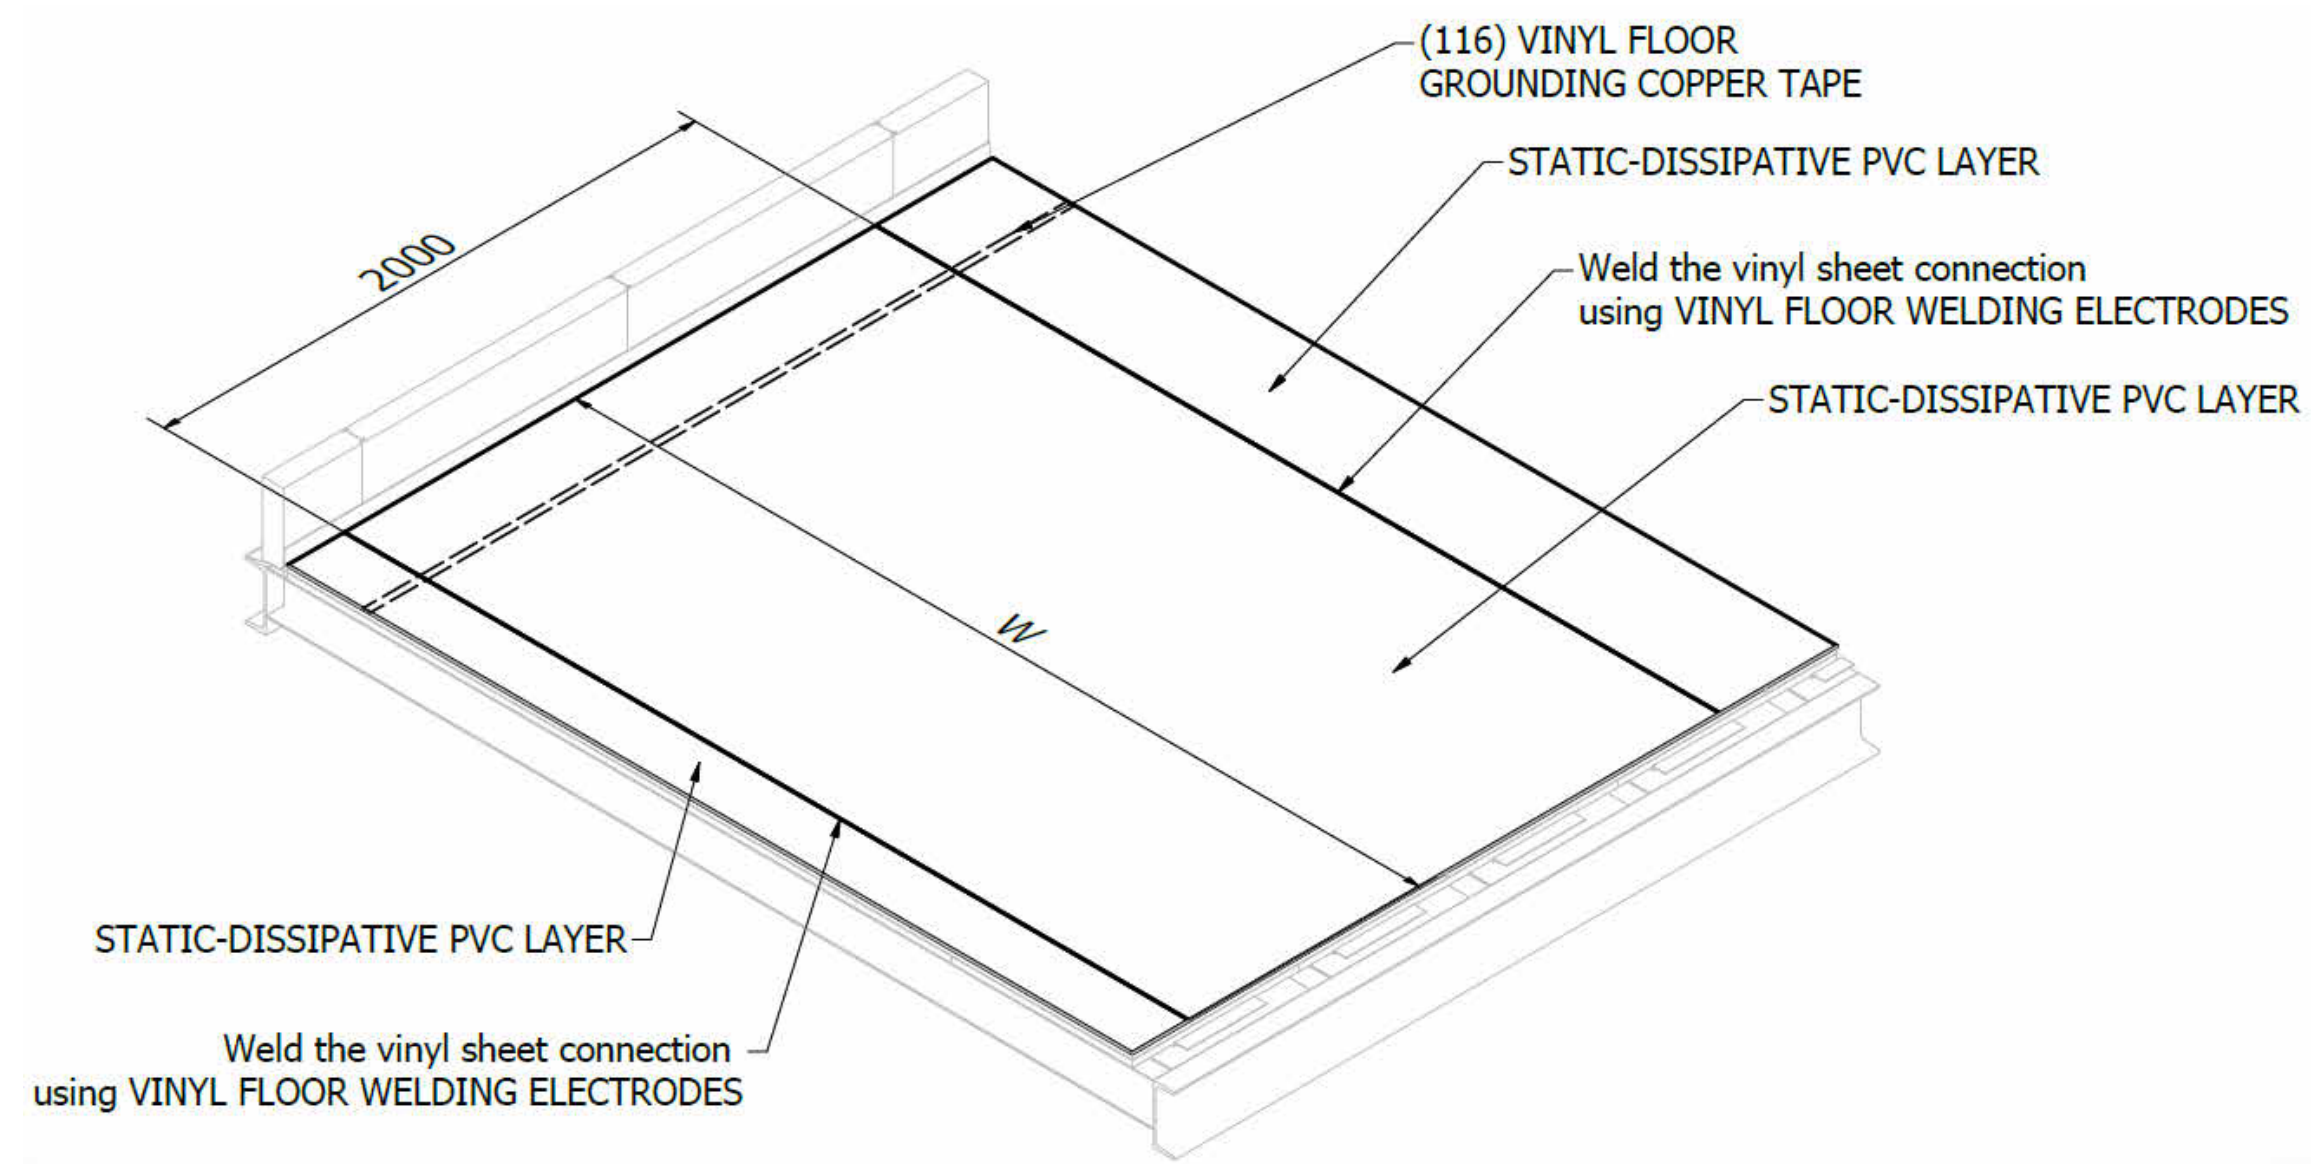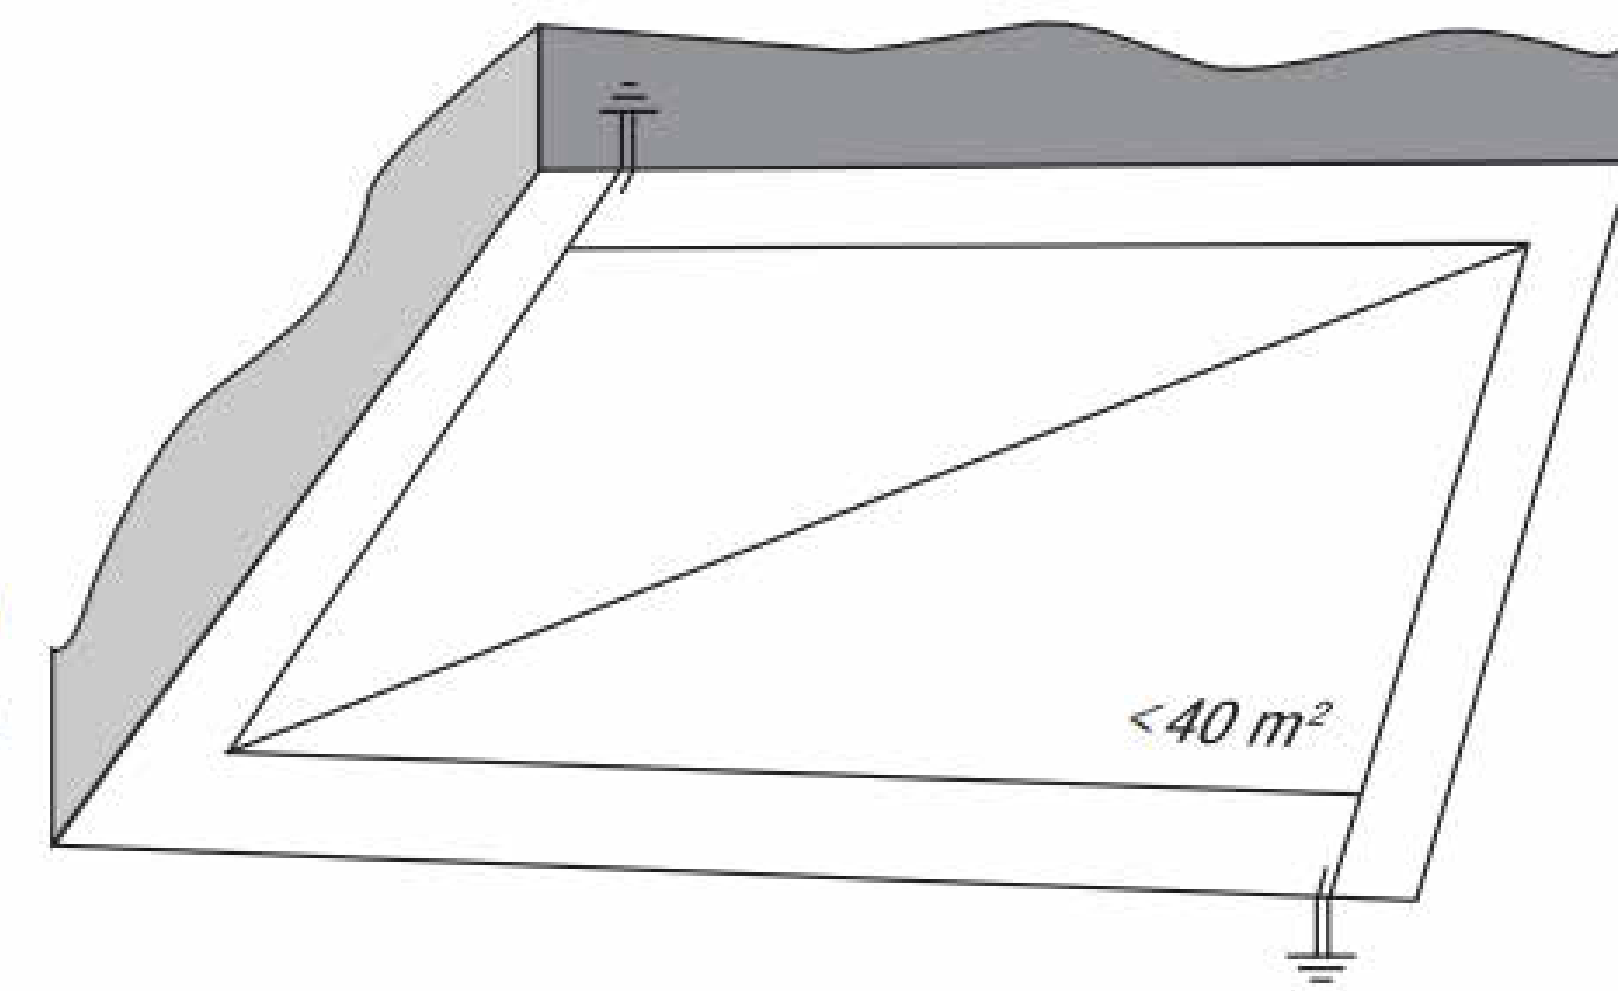


Vinyl floor welding

Carry out a test welding on a leftover piece before commencing work, to adjust speed and temperature

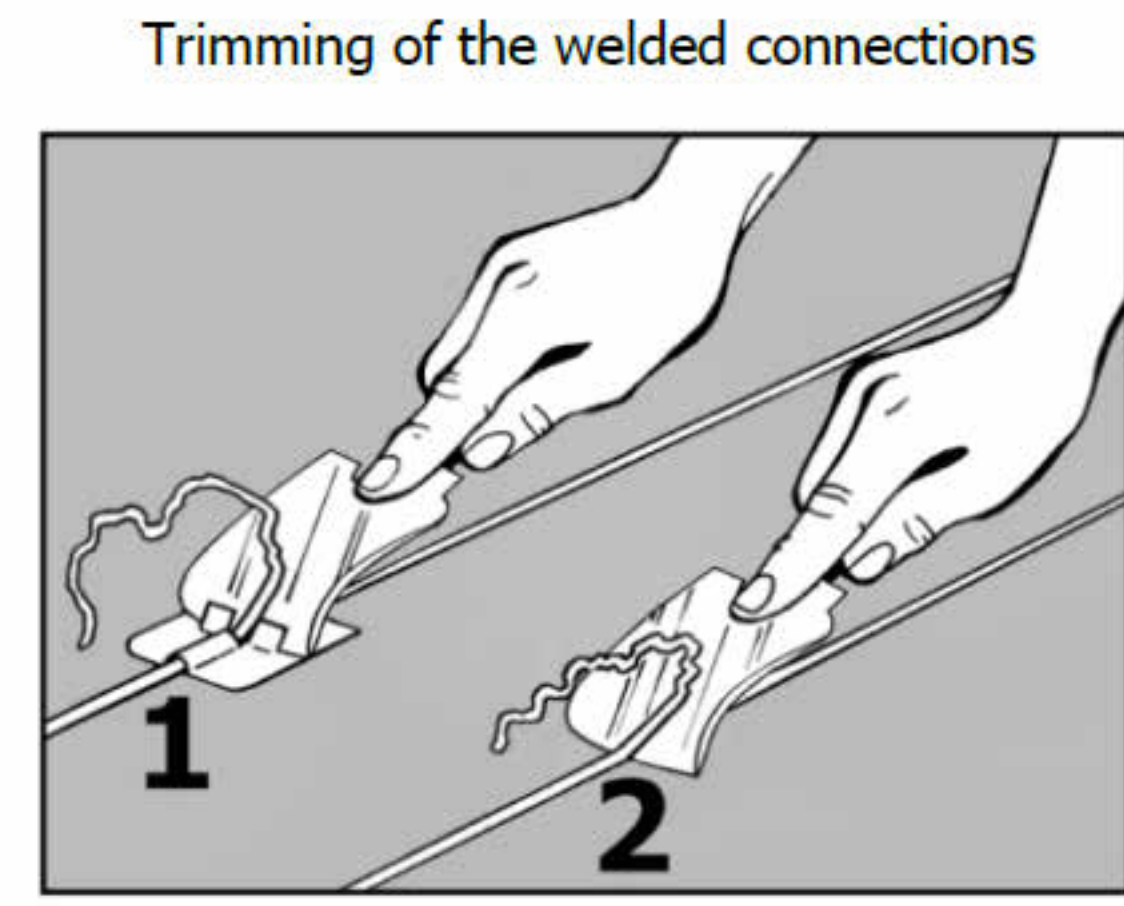

Trimming of the welded connections

Welded seams must cool to room temperature before trimming. Start trimming where you began welding. All trimming of welding thread is recommended in two steps: rough and fine trimming.

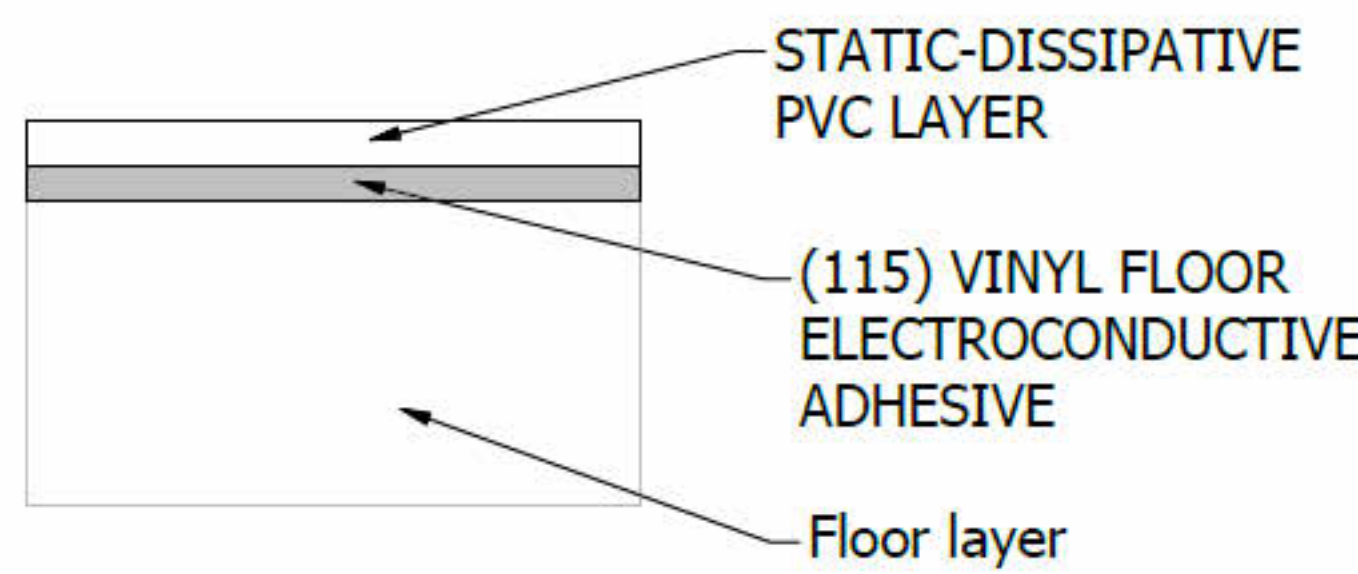

GENERAL NOTES:

- All quantities given in Bill of material table above are indicative and should be checked due to project specific's.

Installation sequence:

- Use SMOOTHING COMPOUND to level an prepare the surface of the layer to which Vinyl floor will be installed.
- Grind the smoothed surface - if needed.
- Cut the sheets to length (equal to dimension W, view K) and lay them out to acclimatize and relax prior to installation.
- Set the (116) COOPER GROUNDING STRIP in by project designated position - strip is self-adhesive, for standard installation detail refer to ASI-1816.
- The sheets are fully adhered with an adhesive approved for specific manufacturers homogeneous vinyl sheet - (115) VINYL FLOOR ELECTROCONDUCTIVE ADHESIVE.
- Weld the sheet connections using (117) VINYL FLOOR WELDING ELECTRODES (detail L)
- Trim the welded seams (detail M)
- Restrict foot traffic for 24 hours after installation.


KEYNOTES

ASI - PM VINYL				
Mark	Height Manual [mm]	Width Manual [mm]	Count [pcs]	
01	3280	2000	1	
02	3280	2000	6	
03	3280	996	1	
Grand total: 8				

ASI - MV VINYL				
Mark	Height Manual [mm]	Width Manual [mm]	Count [pcs]	
04	3280	1200	1	
05	3280	2000	2	
06	3438	1615	1	
07	3438	2000	1	
08	3438	1617	1	
Grand total: 8				

REFERENCE NOTES

KEY PLAN

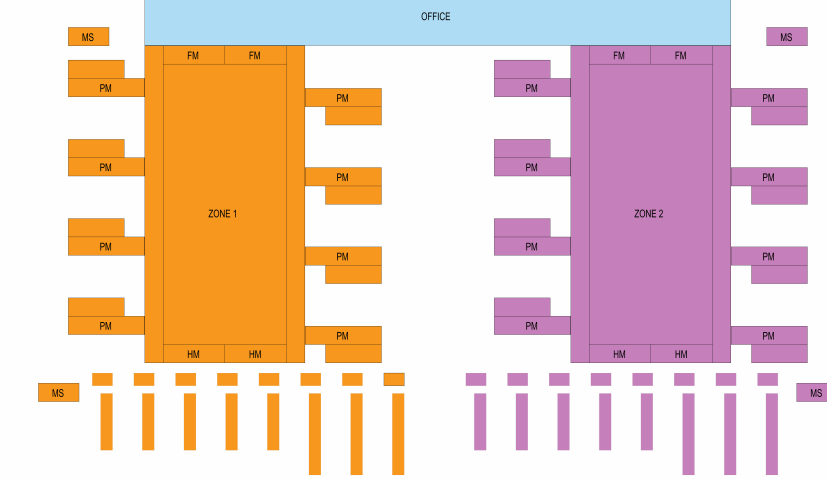

REV.	DESCRIPTION	DATE
R02	FOR MANUFACTURING	2026-09-02
R01	FOR MANUFACTURING	2026-05-26

PROJECT NAME	
ECO DC MONALISA	
DRAWING NAME	
PM - THIRD FLOOR LAYER LAYOUT - VINYL	
PREPARED (ALSO SUBJECT RESPONSIBLE IF OTHER)	
I. PUTICA / K. KOZINA / V. SPANIC	
DOCUMENT RESPONSIBLE APPROVED	
M. PACAK / J. CIOVARIC	
CAD SYSTEM	
AUTODESK REVIT 2025	
DOCUMENT NUMBER	
ASI-107-PM-1-PVC LAYOUT	
SHEET SIZE	
A0	
DRAWING SCALE	
As indicated	
DATE (YYYYMMDD)	
2026-09-02	
REVISION	
R02	