



LEGAL DISCLAIMER: THIS DOCUMENT AND THE CONTENTS HEREIN ARE CONFIDENTIAL AND THE SOLE PROPERTY OF VERTIV. REPRODUCTION, DISTRIBUTION OR UNAUTHORIZED USE OF THIS DOCUMENT OR ANY PARTS WITHIN THIS DOCUMENT ARE FORBIDDEN WITHOUT THE WRITTEN CONSENT OF VERTIV.


PARTS LIST			
ITEM	QTY	PART NUMBER	DESCRIPTION
1	1	MV01	
2	2	I00000328277	MV - added profile 620
3	2	I00000328322	MV - added profile 638
4	2	I00000328457	MV - RMU profile - 480
5	1	I00000328458	MV - RMU profile 440
6	28	SCREW	JT3-12-5,5x40 E16

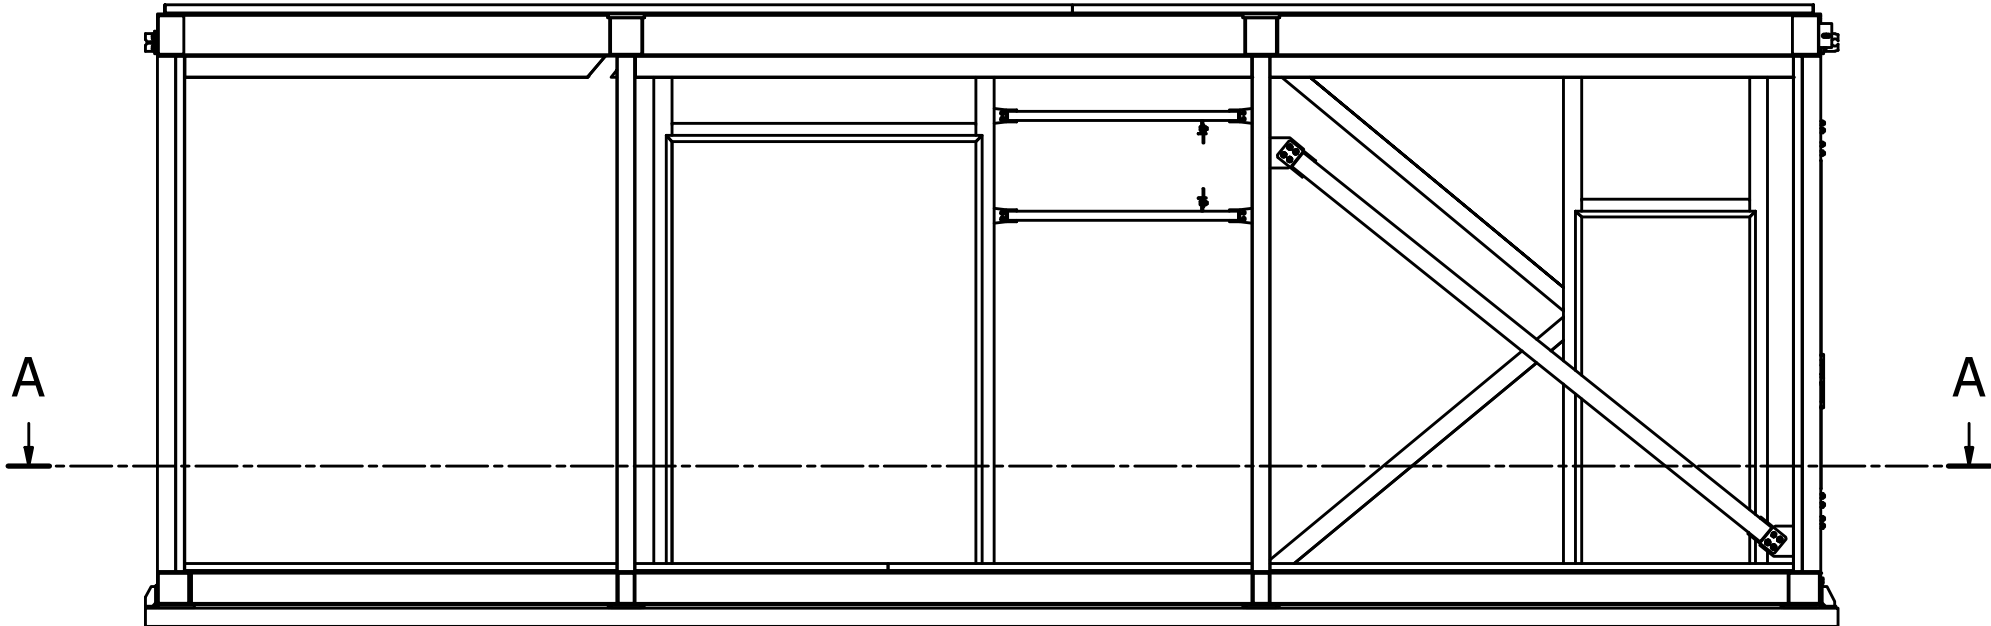


A-A (1:50)

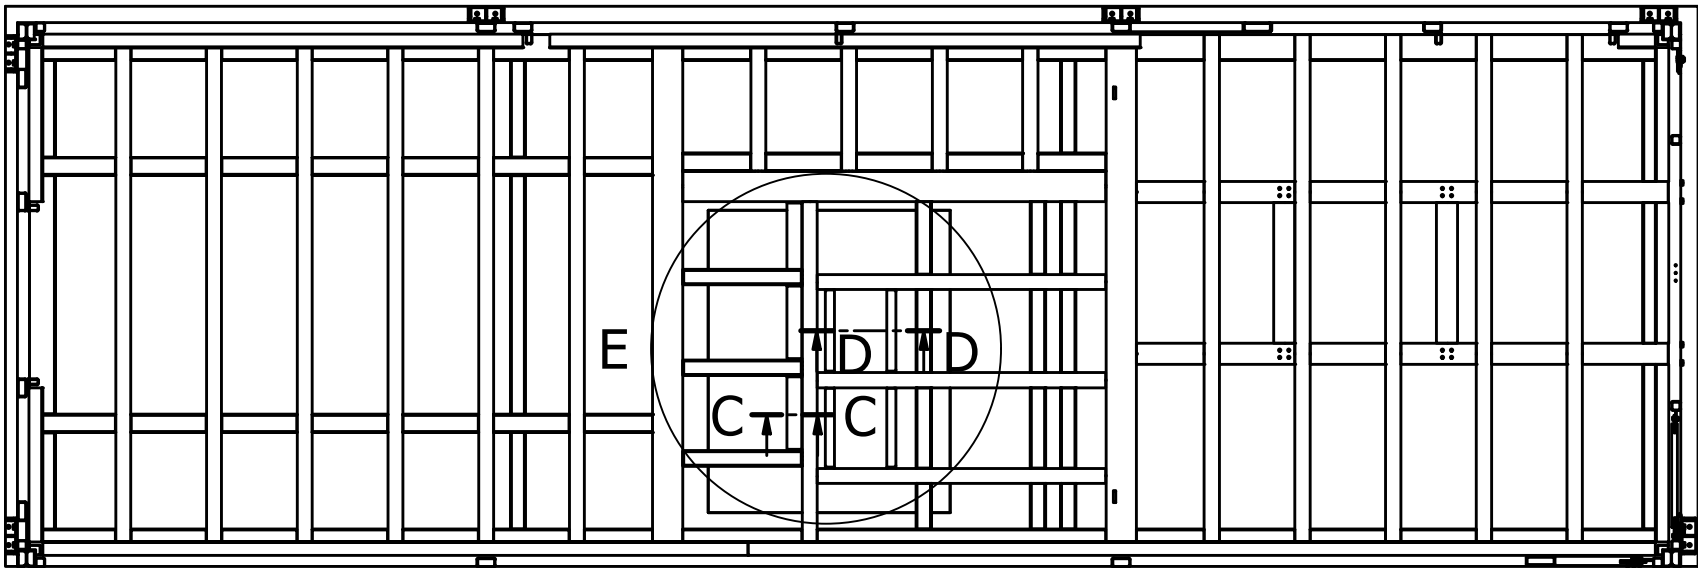


D-D (1:5)

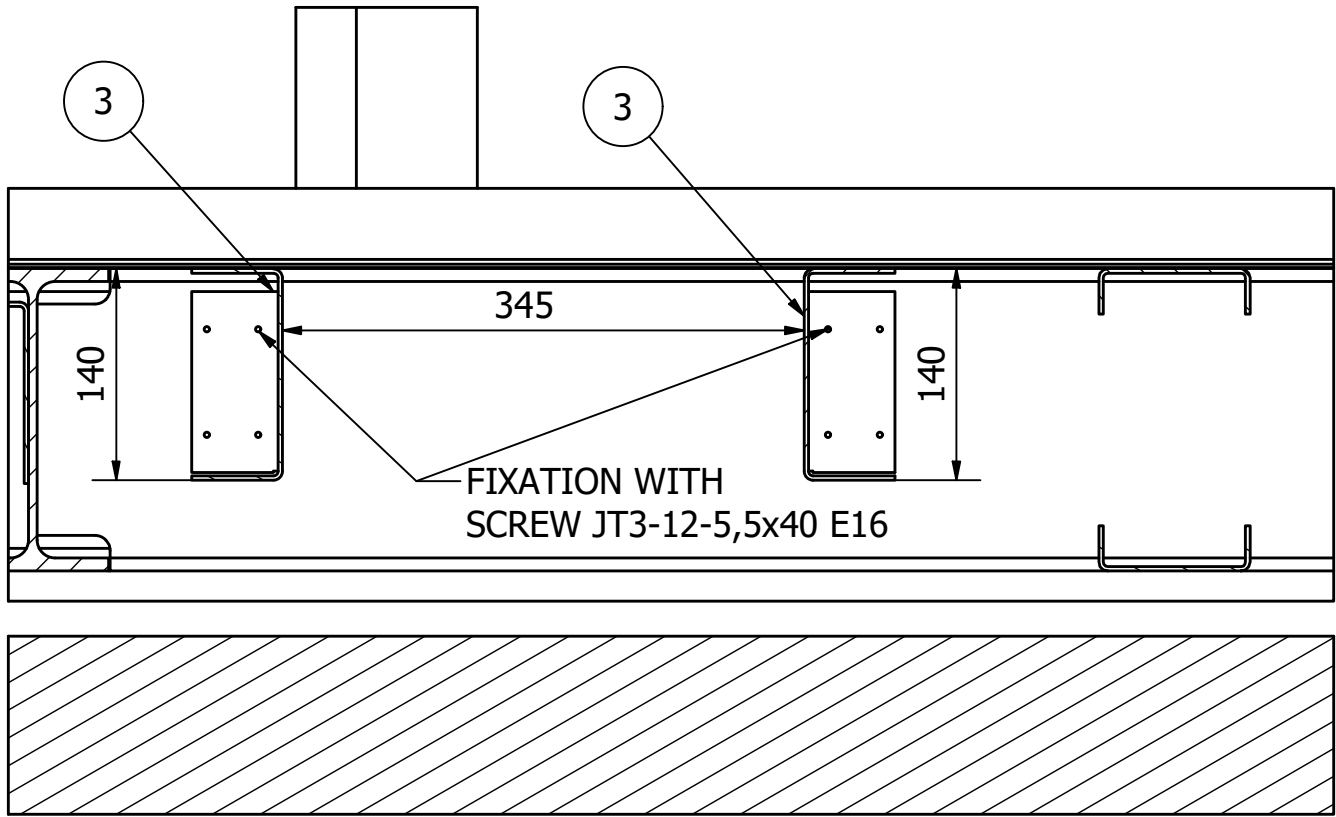


C-C (1:5)

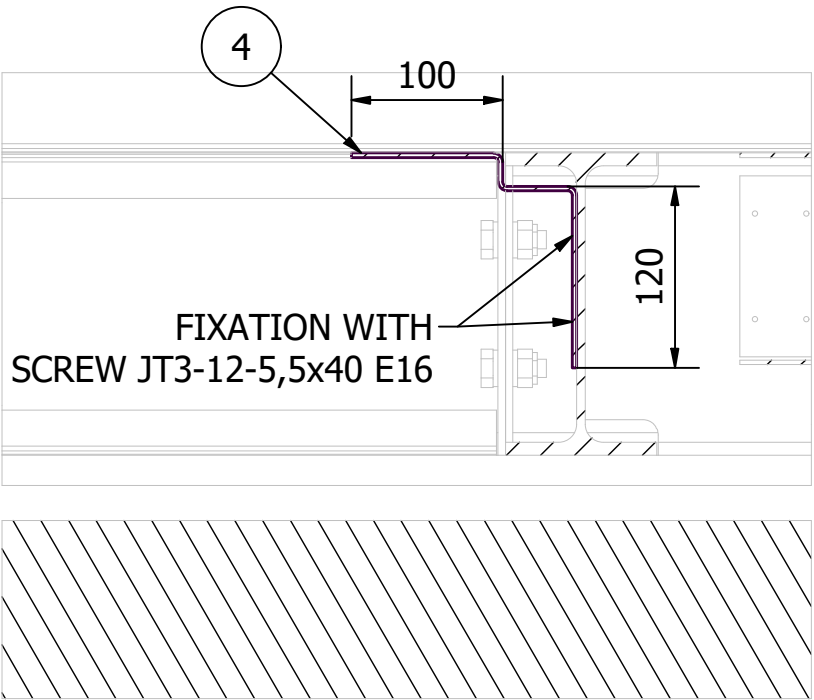

E (1:20)

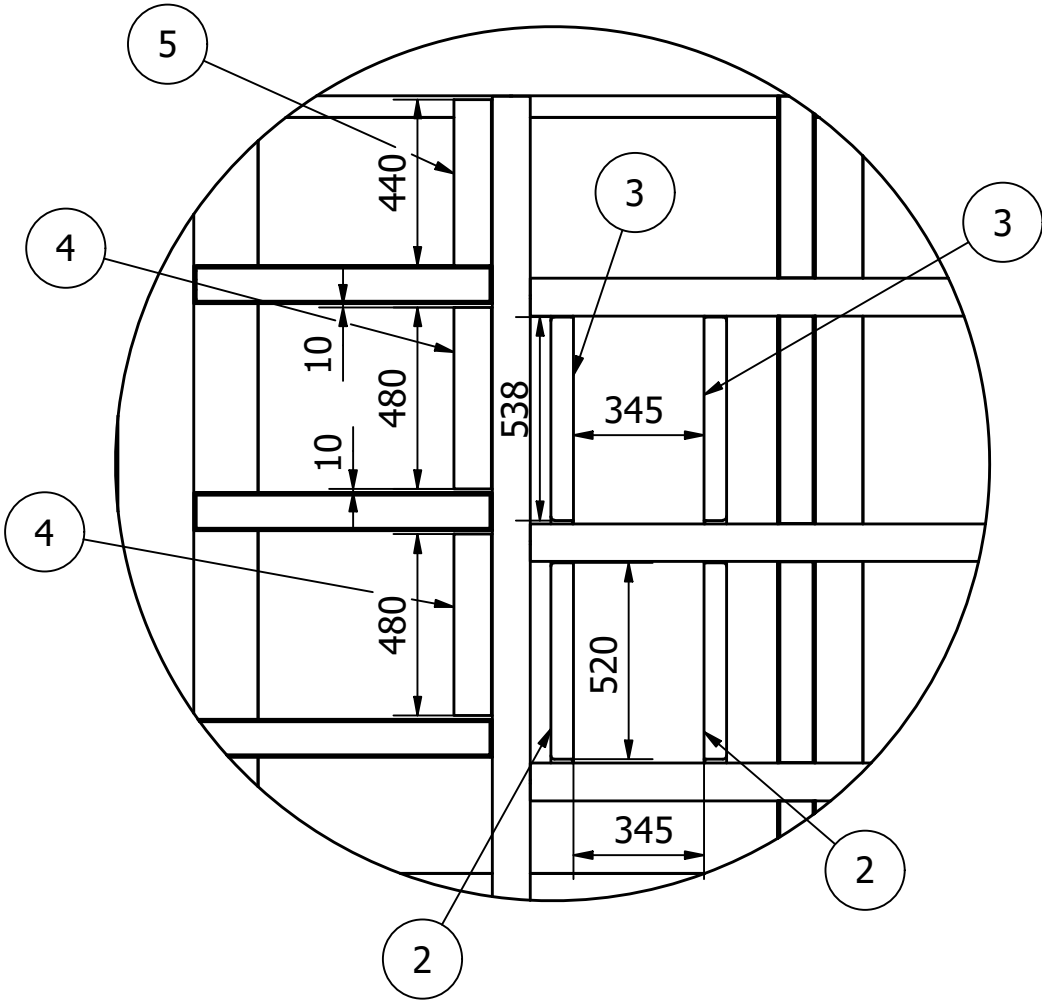

REVISION HISTORY		
REV	DESCRIPTION	DATE
R1	For manufacturing	7.7.2026.

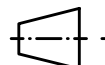	CAD system		Material	Finish	Weight
	Autodesk Inventor				N/A
	DIMENSIONAL TOLERANCES ACCORDING ISO 2768-m UNLESS OTHERWISE SPECIFIED		Project name ECOD DC		
		Sheet size A2	Scale 1:50	Drawing name / Description MV additional profiles - floor openings	
Prepared (also subject responsible if other) V. SPANIC				Document number / Part number ASI-113-MV-floor penetrations-additional profiles	
Document responsible/Approved J.J. CICVARIC				Rev R1	Date (DD.MM.YY) 7.7.2026.
				Sheet 1 (1)	