


LEGAL DISCLAIMER: THIS DOCUMENT AND THE CONTENTS HEREIN ARE CONFIDENTIAL AND THE SOLE PROPERTY OF VERTIV GROUP CORP. REPRODUCTION, DISTRIBUTION OR UNAUTHORIZED USE OF THIS DOCUMENT OR ANY PARTS WITHIN THIS DOCUMENT ARE FORBIDDEN WITHOUT THE WRITTEN CONSENT OF VERTIV GROUP CORP.

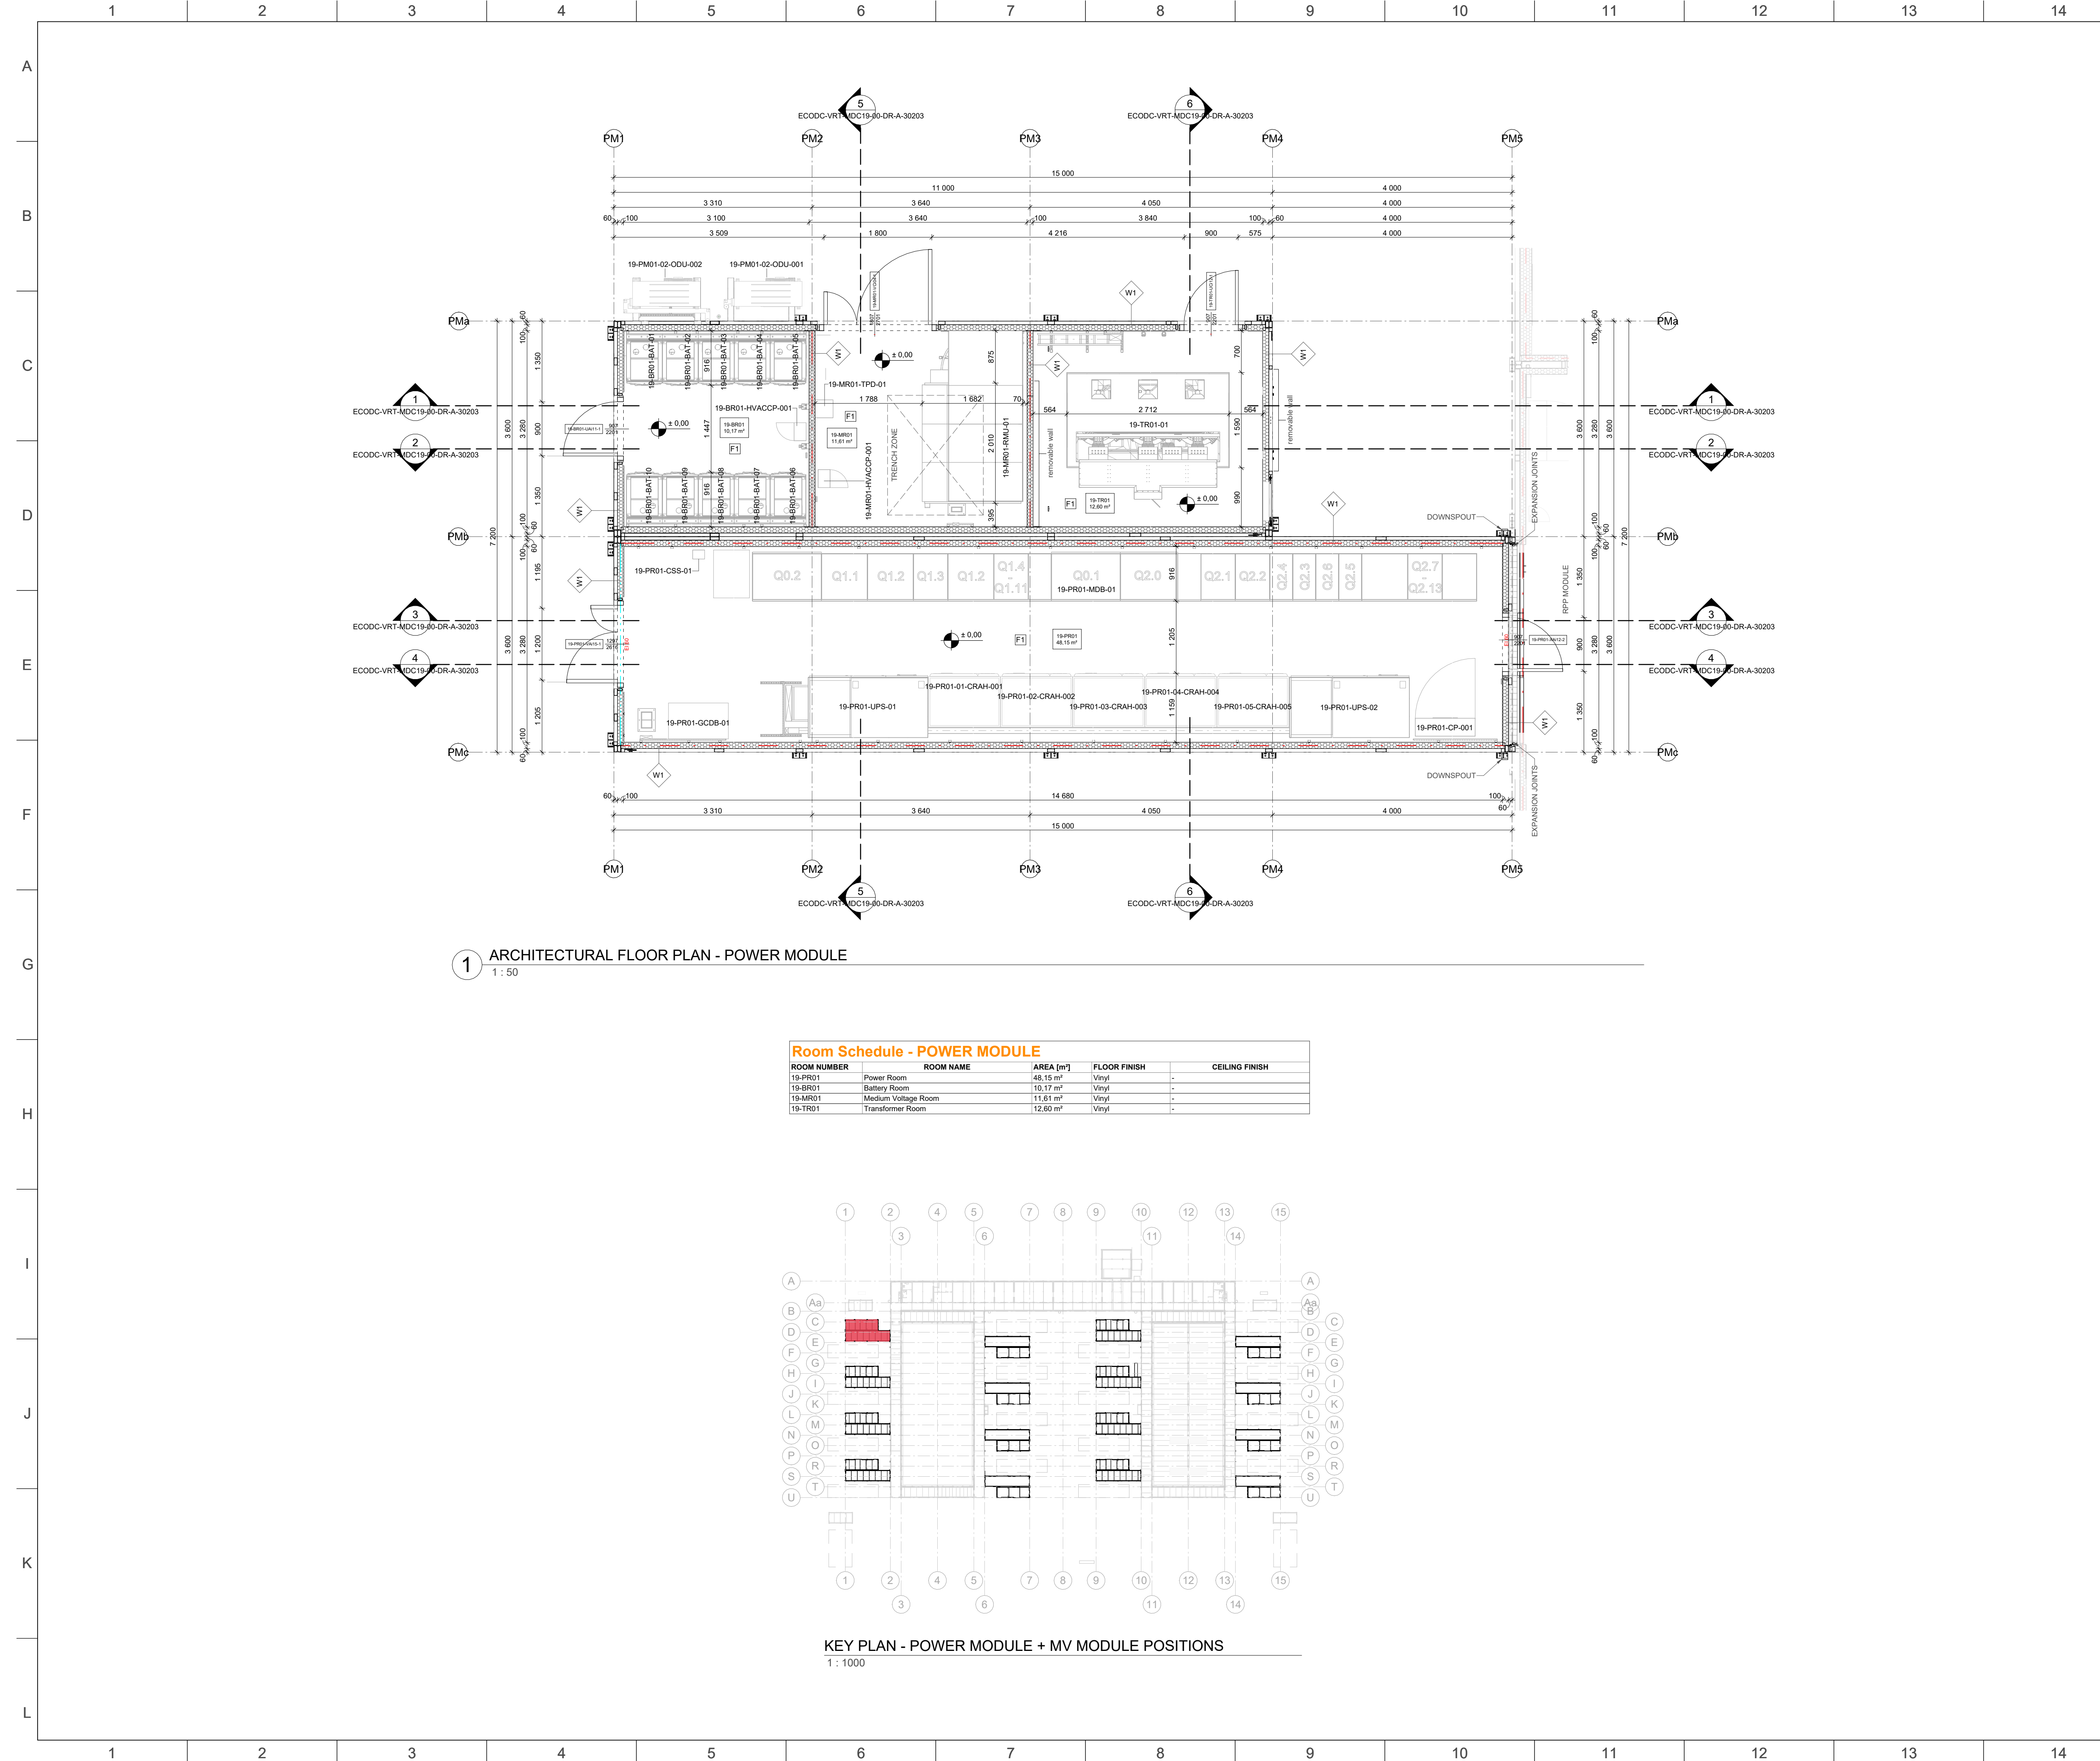

1 ARCHITECTURAL FLOOR PLAN - POWER MODULE
1 : 50

Room Schedule - POWER MODULE				
ROOM NUMBER	ROOM NAME	AREA [m²]	FLOOR FINISH	CEILING FINISH
19-PR01	Power Room	48.15 m²	Vinyl	-
19-BR01	Battery Room	10.17 m²	Vinyl	-
19-MR01	Medium Voltage Room	11.61 m²	Vinyl	-
19-TR01	Transformer Room	12.60 m²	Vinyl	-



KEY PLAN - POWER MODULE + MV MODULE POSITIONS
1 : 1000

FLOOR SCHEDULE - POWER MODULE

Type Mark	Description	Fire Rating
F1	inside to outside: - VINYL 2mm - CEMENT FIBRE BOARD 22mm - PLYWOOD 18mm - FLOOR STRUCTURE with MINERAL WOOL INFILL 200mm - VAPOUR CONTROL LAYER 0.2mm - STEEL SHEET 0.8mm U=0,16 W/m2K	<varies>

ROOF SCHEDULE - POWER MODULE

Type Mark	Description	Fire Rating
R2	inside to outside: - PREFABRICATED SANDWICH PANEL, TRIMOTERM PERFORM C FTV, RAL 9006 (EXT), RAL 9002 (INT) 100mm - VAPOUR CONTROL LAYER 0.2mm - THERMAL INSULATION (fully infilled gap 140-240mm) - STEEL SHEET 5mm U=0,15 W/m2K	N/A

WALL SCHEDULE - POWER MODULE

Type Mark	Keynote Description	Fire Rating
W1	- PREFABRICATED SANDWICH PANEL, TRIMOTERM PERFORM C FTV, RAL 9006 (EXT), RAL 9002 (INT) 100mm U=0,40 W/m2K	EI 60 (where indicated)

GENERAL NOTE

- ARCHITECTURAL LAYERS ARE LISTED FROM INSIDE TO OUTSIDE

- VERTIV RESERVES THE RIGHT TO INSTALL ANY OTHER BRAND OF SANDWICH PANEL, MINERAL WOOL OF EQUAL CHARACTERISTICS AND QUALITY, INSTEAD OF THE PRODUCT SPECIFIED IN THE KEYNOTES, DEPENDING ON THE AVAILABILITY OF THE PRODUCT IN THE MOMENT OF ORDERING

- WHERE WALL IS REQUIRED TO PROVIDE FIRE RESISTANCE FROM BOTH SIDES, AND WHERE STRUCTURE LACKS ALTERNATIVE FIRE PROTECTION, INTUMESCENT COATING SHALL BE APPLIED TO THE STRUCTURAL ELEMENTS

- ALL FACADE PANELS ARE INSTALLED VERTICALLY UNLESS OTHERWISE SPECIFIED

- THIS DRAWING SHOWS A SINGLE POWER MODULE AND IS TYPICAL FOR ALL POWER MODULES IN THE PROJECT. EACH MODULE, ALONG WITH ITS CORRESPONDING EQUIPMENT, PENETRATIONS, AND MEP SERVICES, IS IDENTIFIED BY A UNIQUE TAG.

- BUILDING LAYERS AND STRUCTURE SURFACE COLOUR:
RAL 9006 EXTERIOR
RAL 9002 INTERIOR

- ANTICORROSION LEVEL:
C4M EXTERIOR
C2M INTERIOR

LEGEND

FIRE COMPARTMENT BORDER REIM 60

FIRE COMPARTMENT BORDER EI 60

FIRE COMPARTMENT BORDER EI 30

TRANSPORT COLUMNS

OUT OF VERTIV SCOPE

SELF-SUPPORTING CEILING

KEY PLAN

R02	CD SET - FOR INFORMATION	2026-07-24
R01	DD SET - FOR INFORMATION	2026-05-20
REV.	DESCRIPTION	DATE

VERTIV™

PROJECT NAME

ECO DC MONALISA

DRAWING NAME

ARCHITECTURAL FLOOR PLAN
- POWER MODULE

PREPARED (ALSO SUBJECT RESPONSIBLE IF OTHER)

L. MAVREK / K. KOZINA

DOCUMENT RESPONSIBLE / APPROVED

M. PACAK

DOCUMENT NUMBER

ECODC-VRT-MDC19-00-DR-A-10206

CAD / BIM SYSTEM

AUTODESK REVIT 2025

SHEET SIZE	DRAWING SCALE	DATE (YYYYMM-DD)	SHEET 1 OF 1
A1	1 : 50	2026-07-24	REVISION R02