




LEGAL DISCLAIMER: THIS DOCUMENT AND THE CONTENTS HEREIN ARE CONFIDENTIAL AND THE SOLE PROPERTY OF VERTIV GROUP CORP. REPRODUCTION, DISTRIBUTION OR UNAUTHORIZED USE OF THIS DOCUMENT OR ANY PARTS WITHIN THIS DOCUMENT ARE FORBIDDEN WITHOUT THE WRITTEN CONSENT OF VERTIV GROUP CORP.

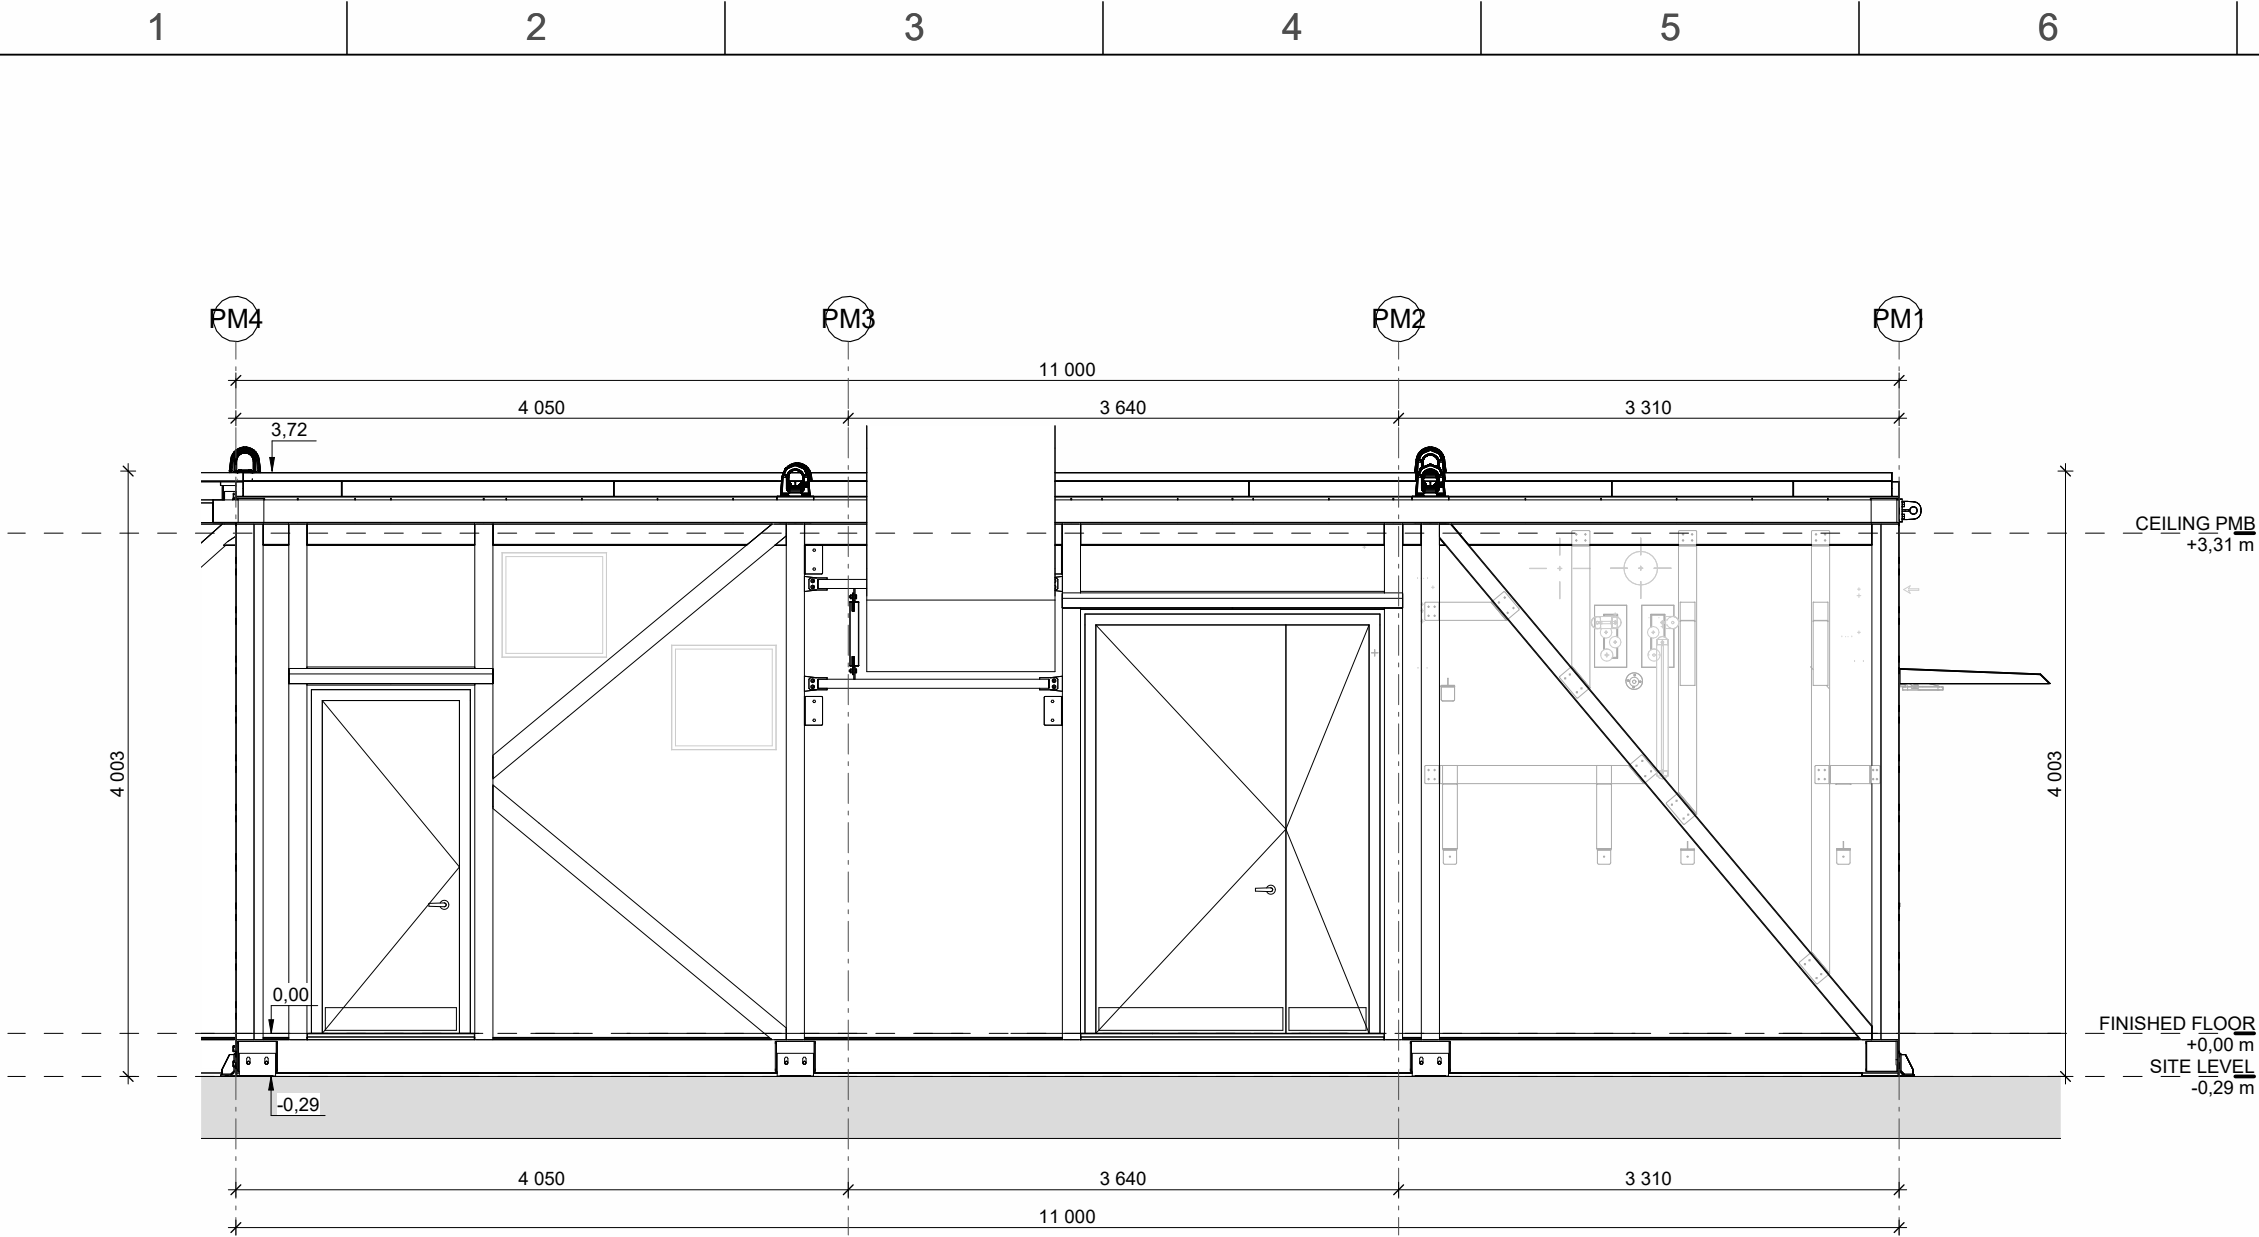


1 MV - ELEVATION NORTH
1 : 50

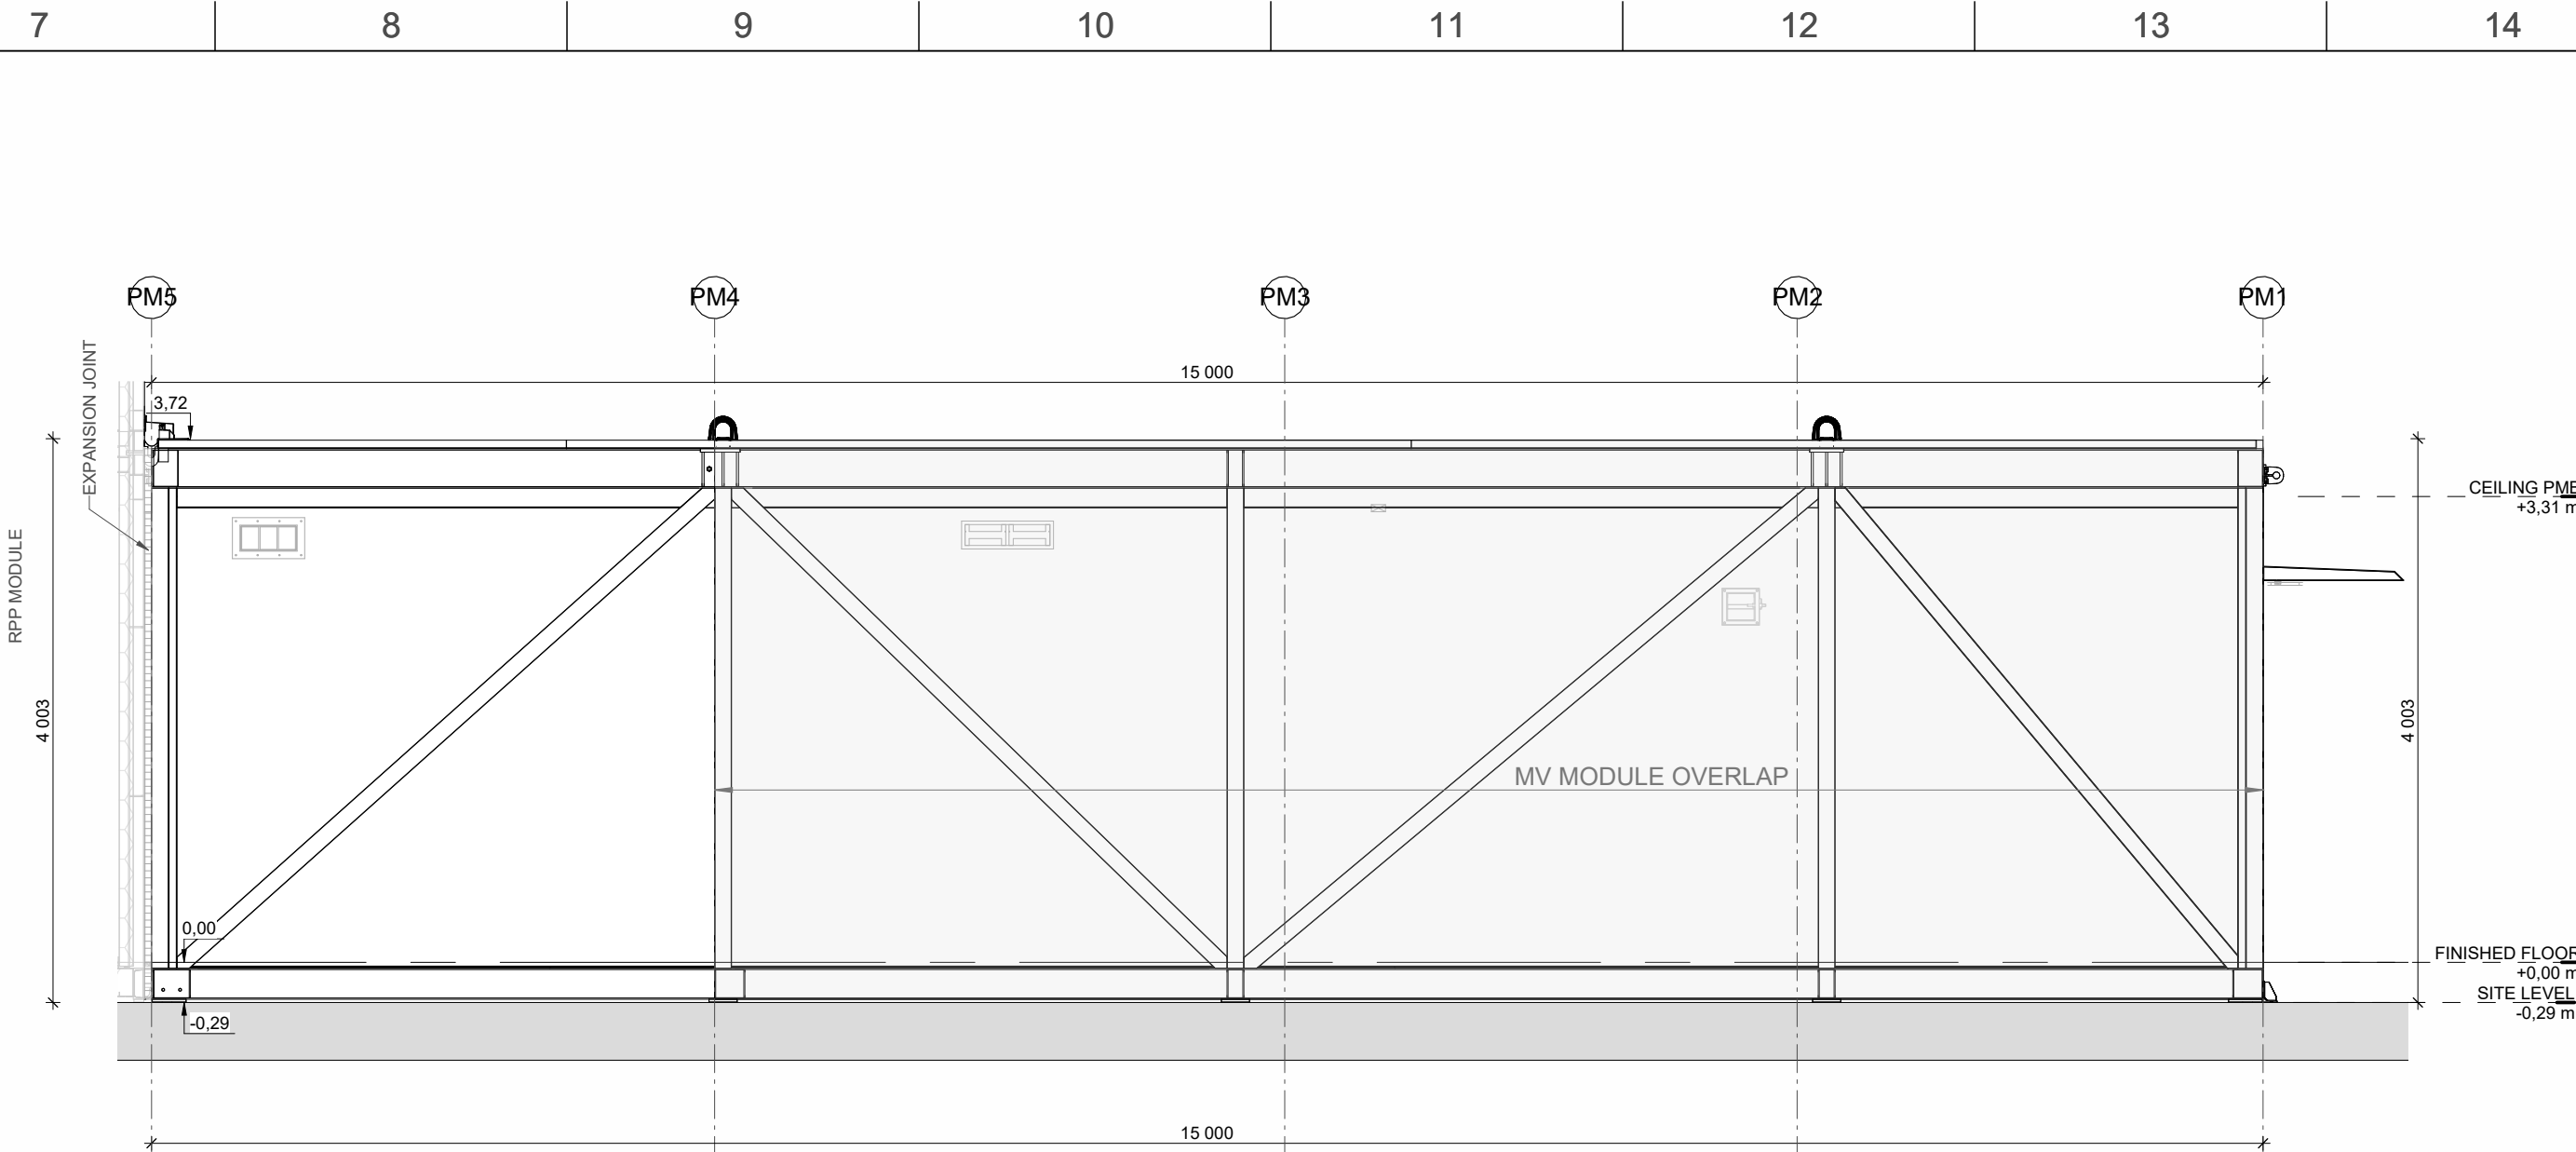


2 PM - ELEVATION NORTH
1 : 50

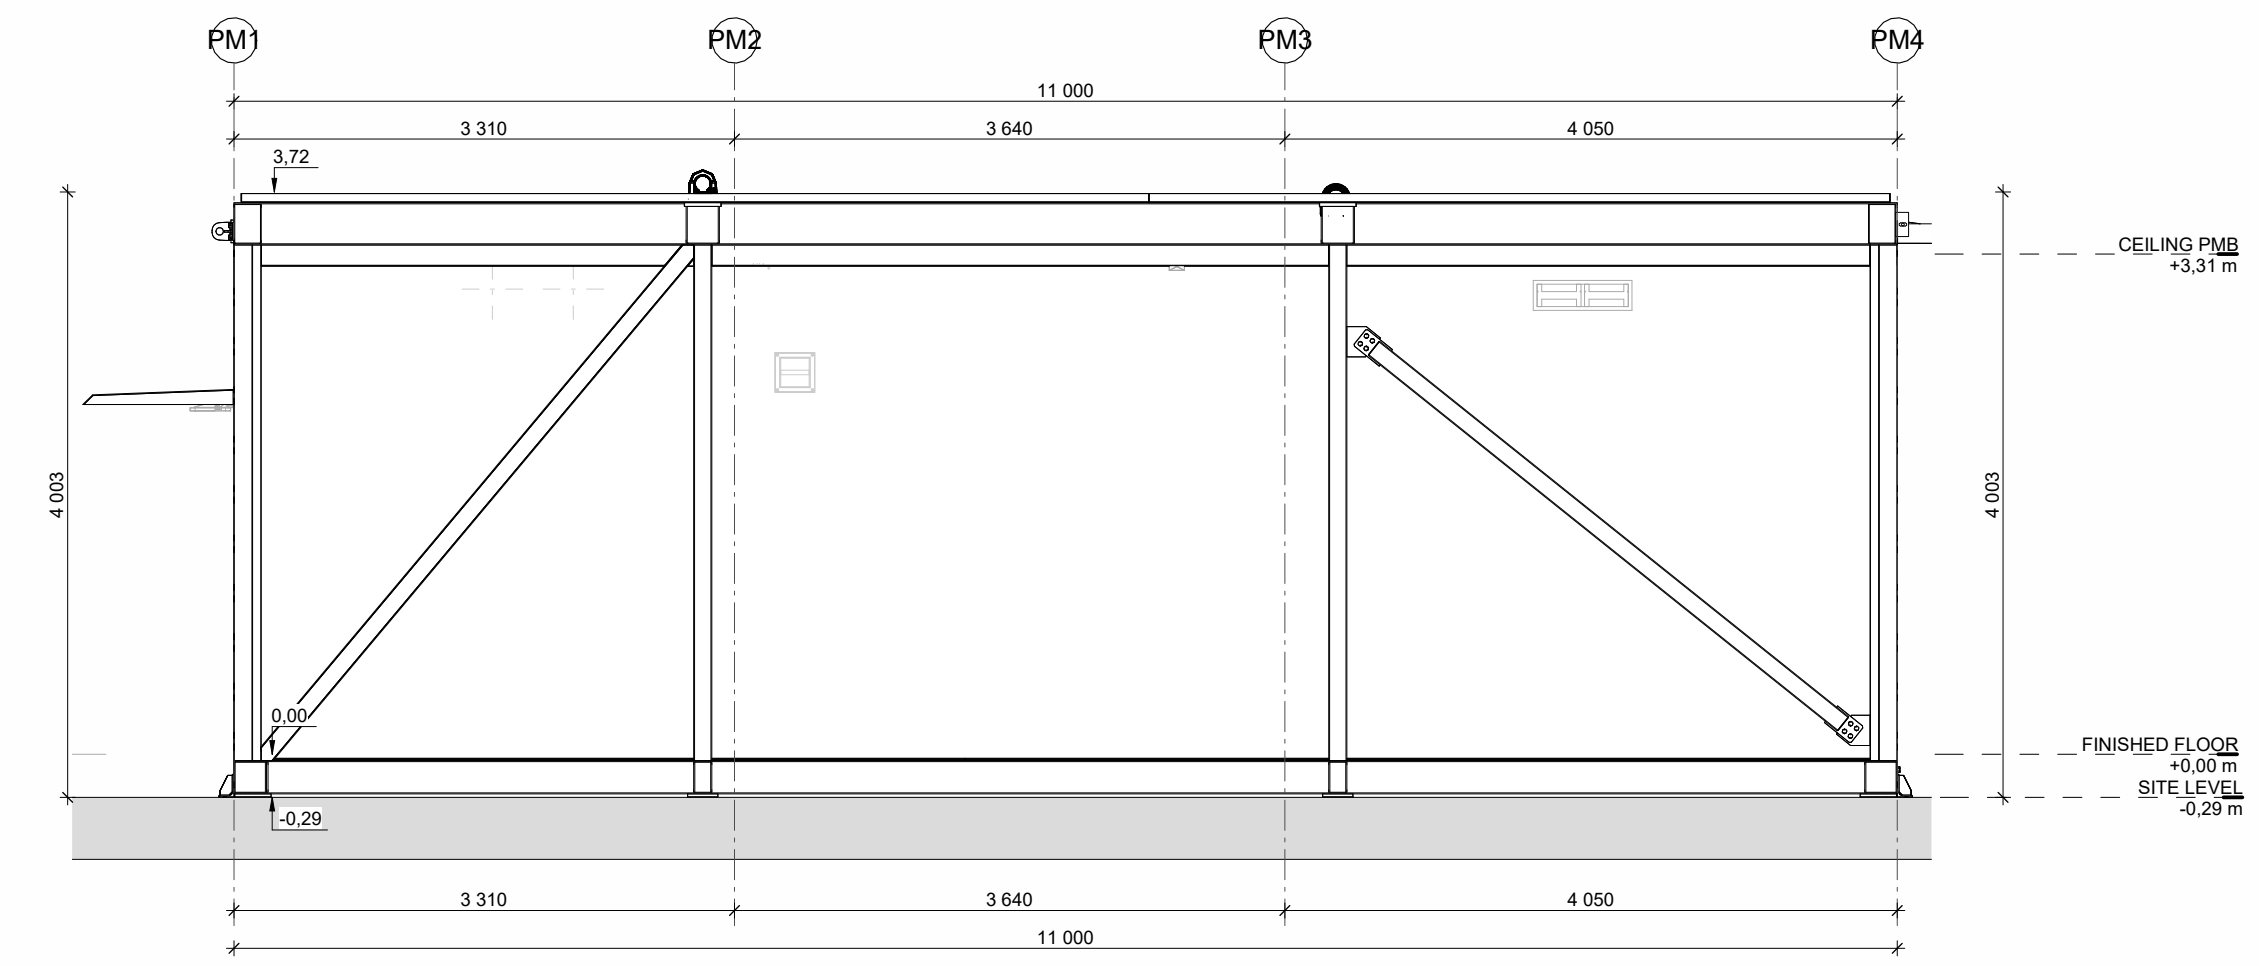


3 MV - ELEVATION SOUTH
1 : 50

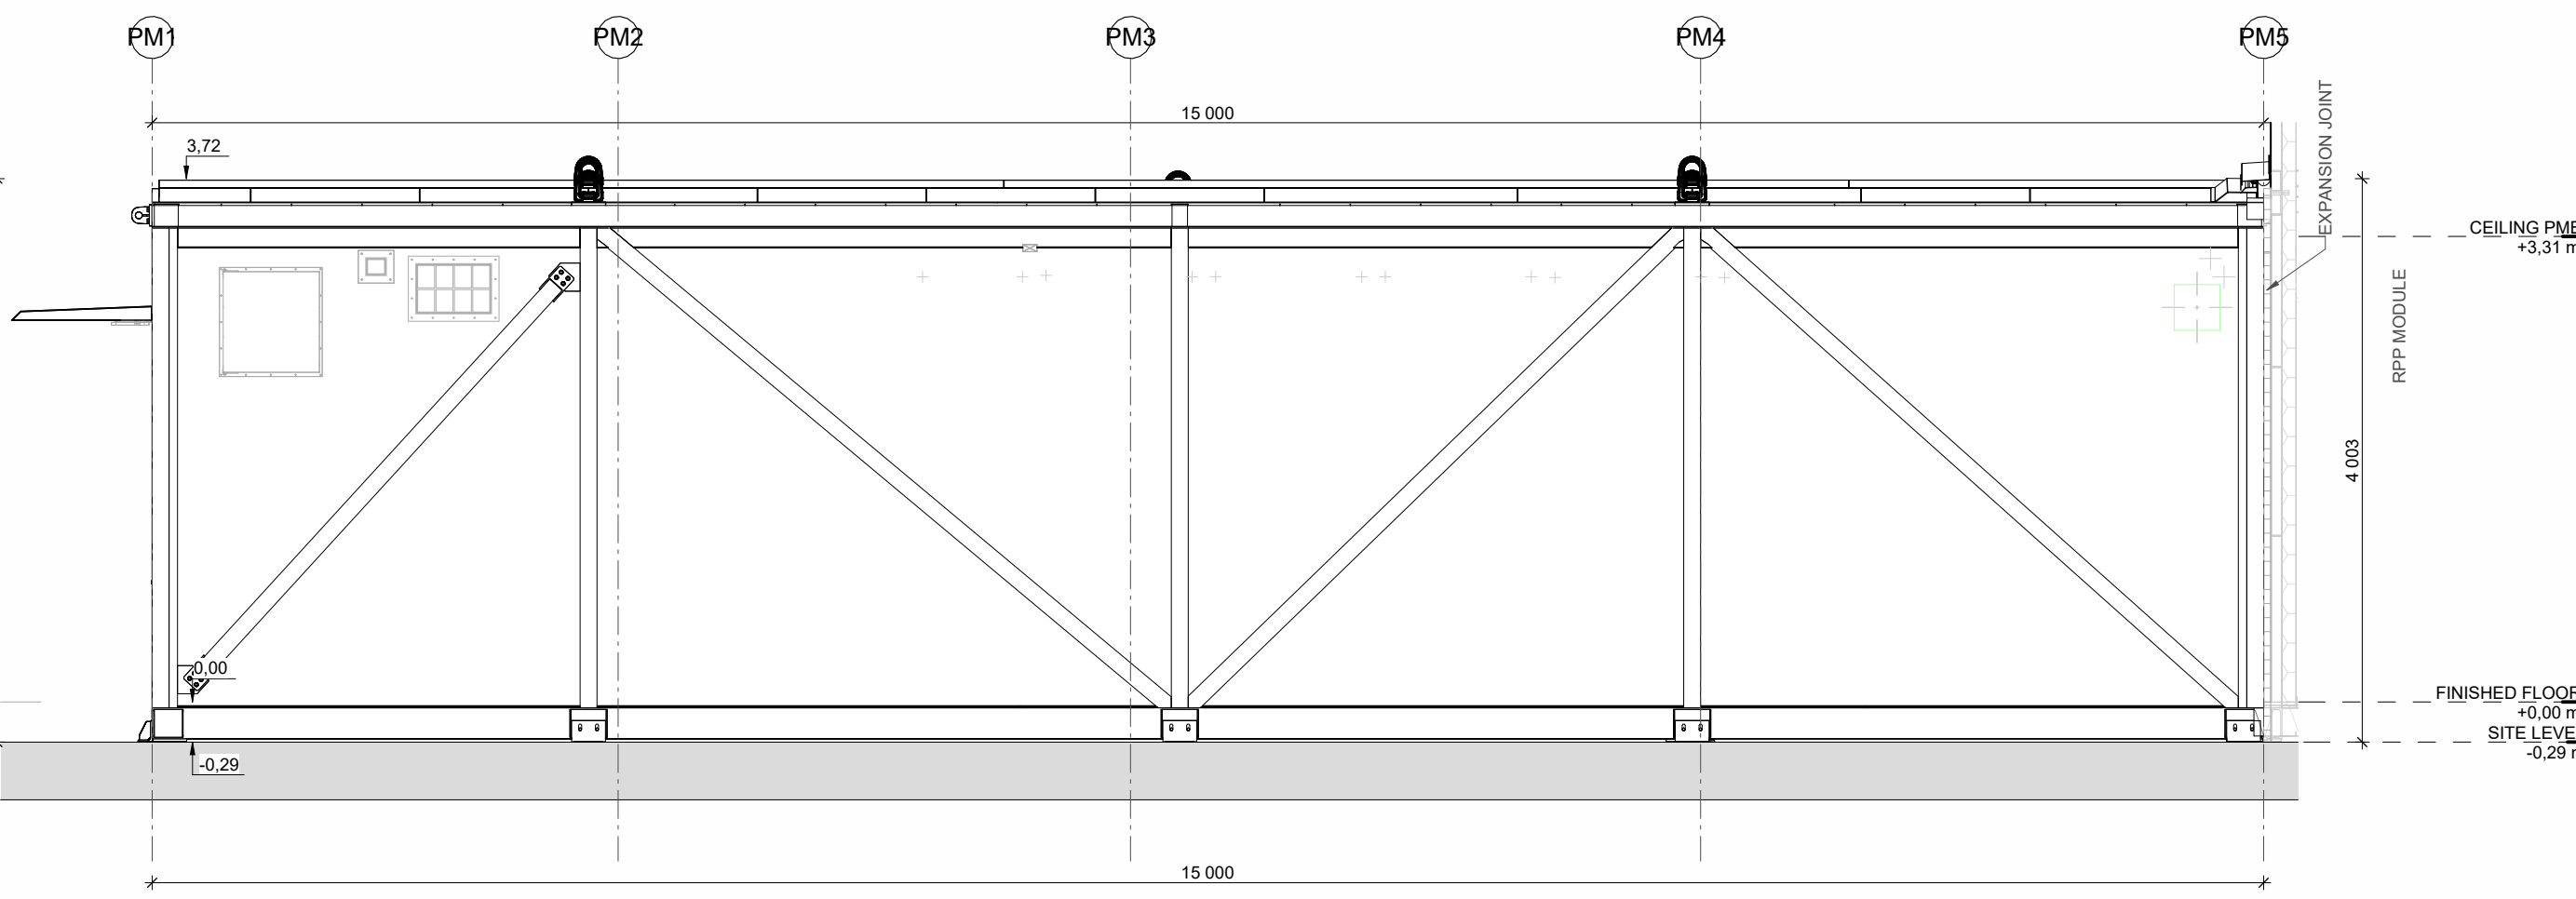


4 PM - ELEVATION SOUTH
1 : 50

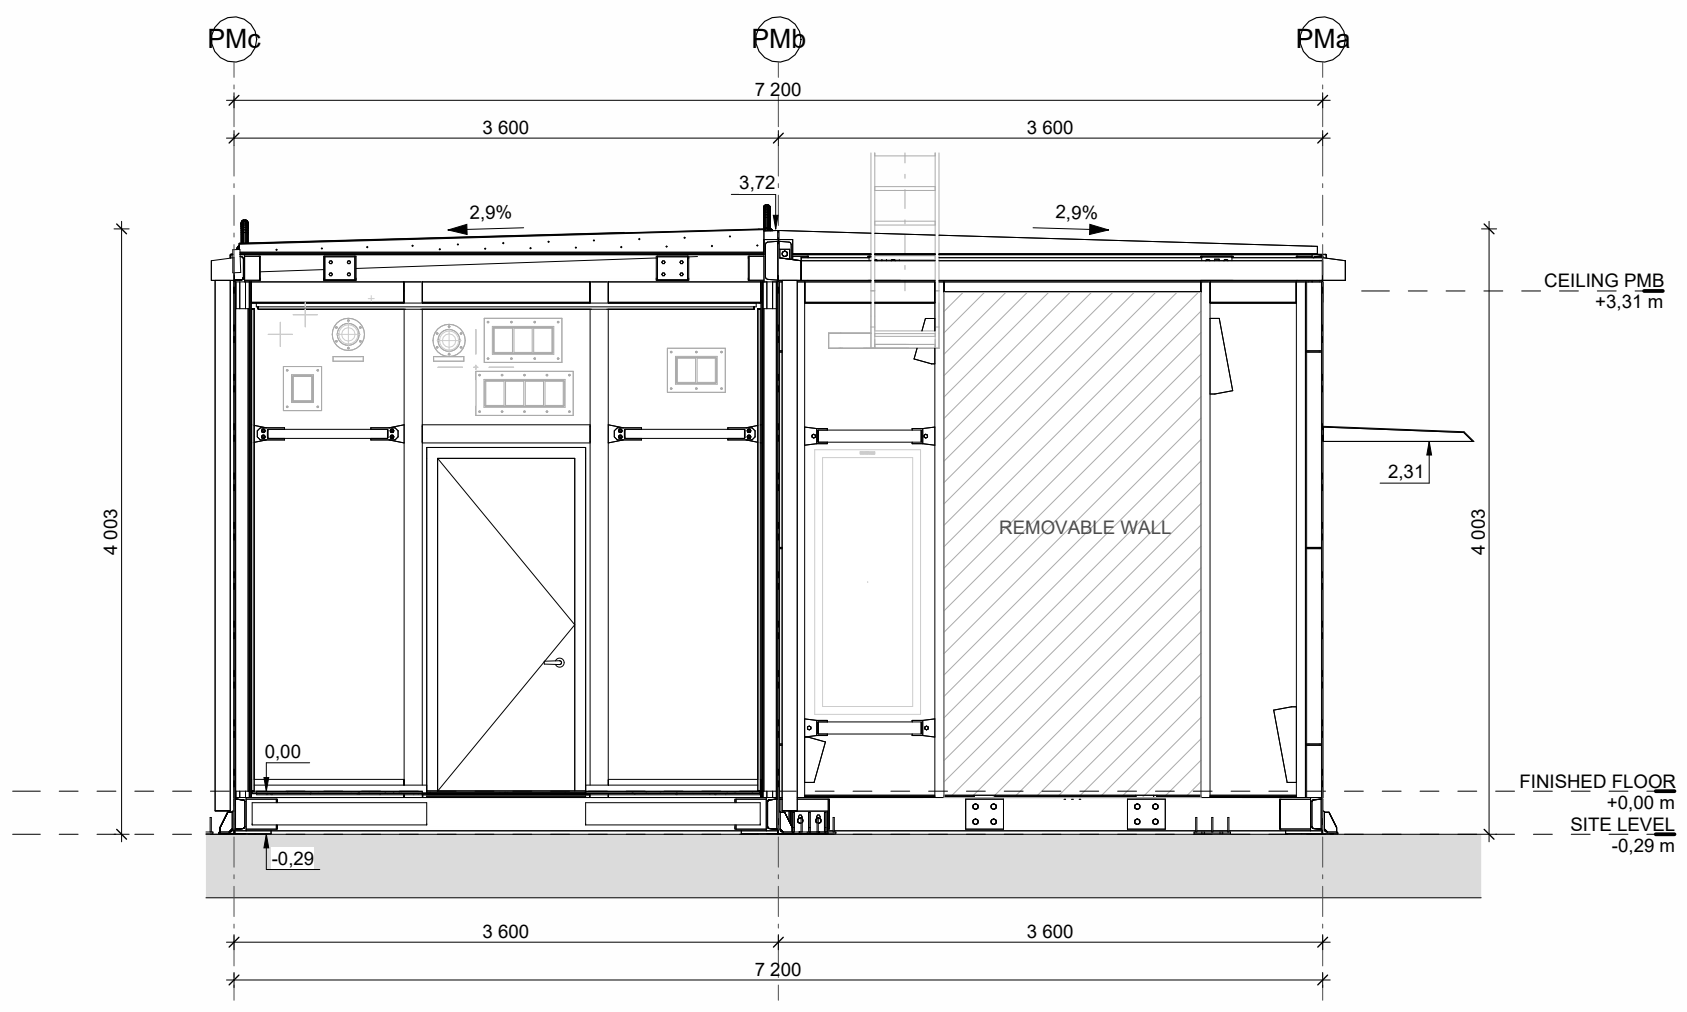

5 PM+MV - ELEVATION EAST
1 : 50

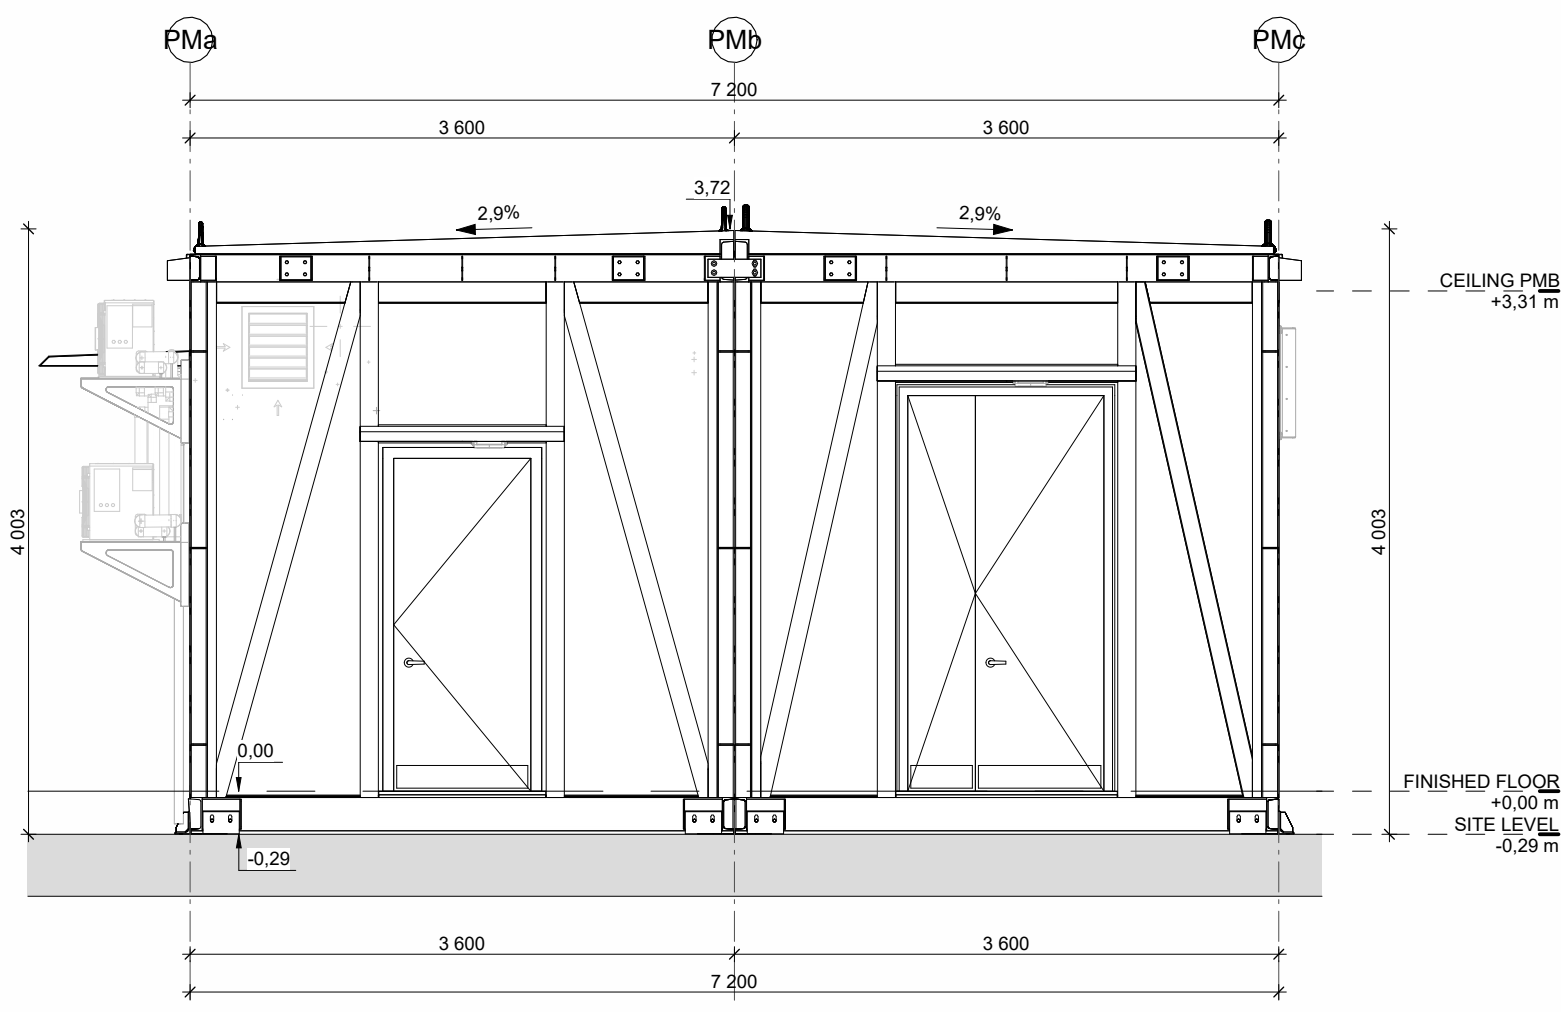

6 PM+MV - ELEVATION WEST
1 : 50

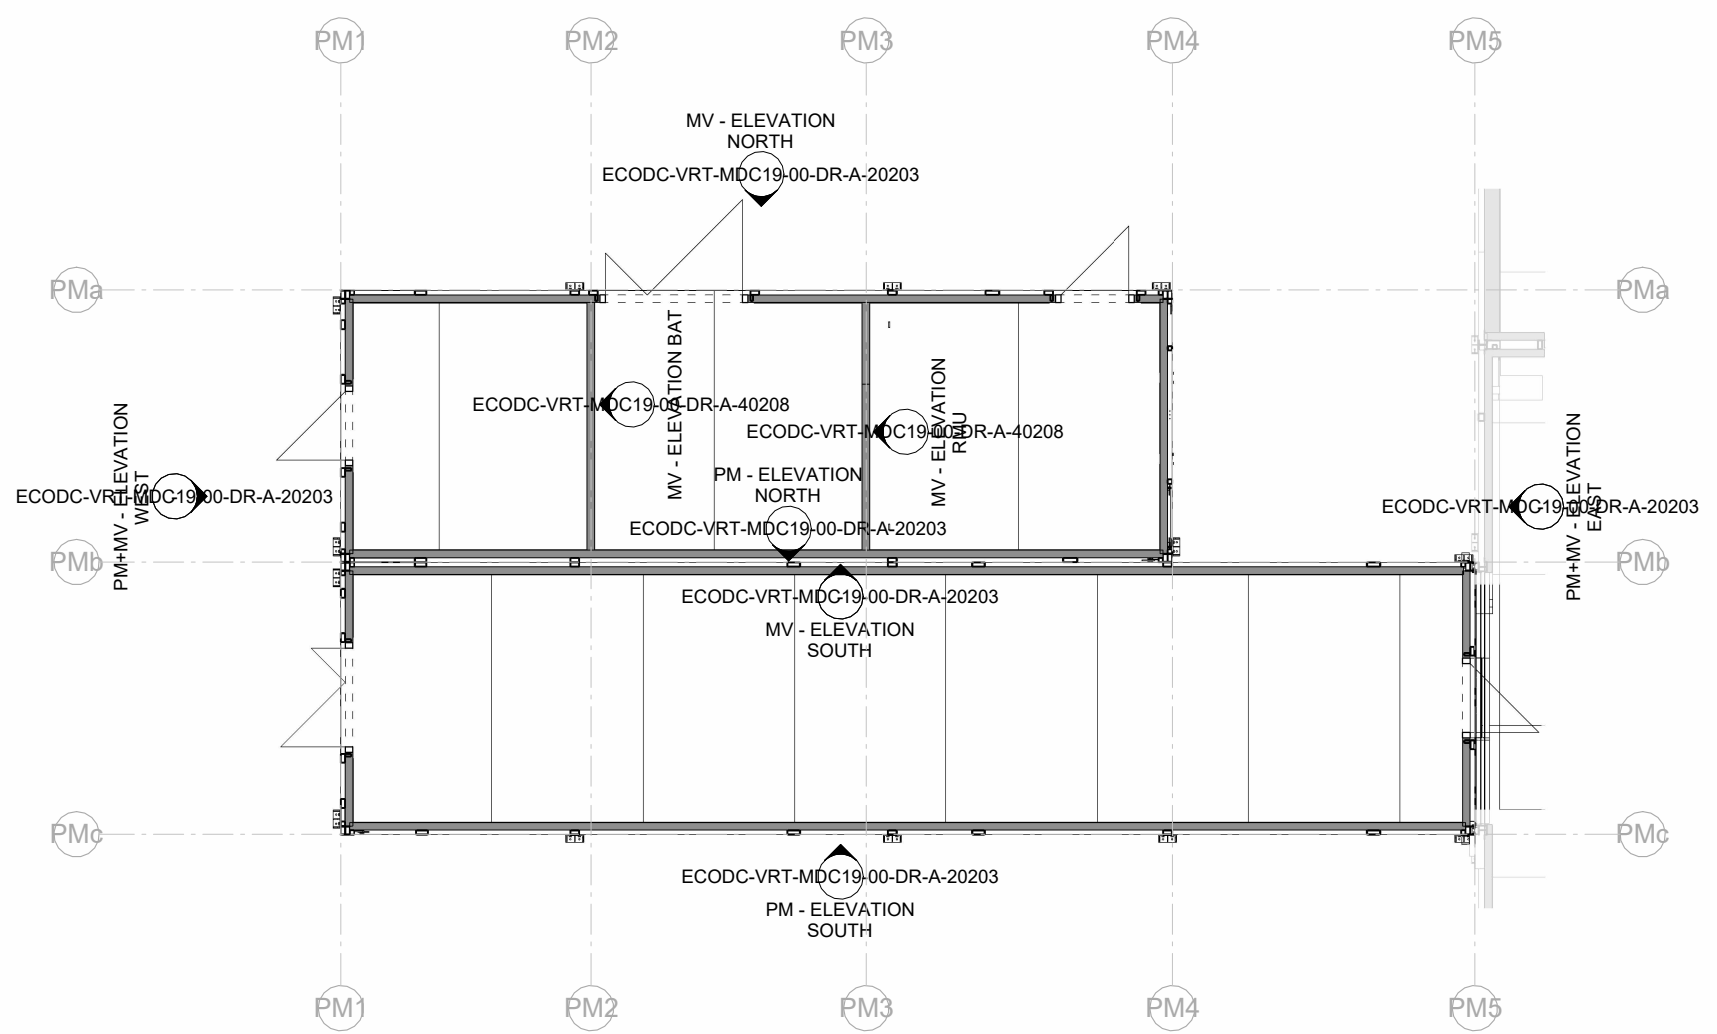

KEY PLAN - POWER MODULE ELEVATION POSITIONS
1 : 100


KEYNOTES

GENERAL NOTE

- ARCHITECTURAL LAYERS ARE LISTED FROM INSIDE TO OUTSIDE
- VERTIV RESERVES THE RIGHT TO INSTALL ANY OTHER BRAND OF SANDWICH PANEL, MINERAL WOOL OF EQUAL CHARACTERISTICS AND QUALITY, INSTEAD OF THE PRODUCT SPECIFIED IN THE KEYNOTES, DEPENDING ON THE AVAILABILITY OF THE PRODUCT IN THE MOMENT OF ORDERING
- WHERE WALL IS REQUIRED TO PROVIDE FIRE RESISTANCE FROM BOTH SIDES, AND WHERE STRUCTURE LACKS ALTERNATIVE FIRE PROTECTION, INTUMESCENT COATING SHALL BE APPLIED TO THE STRUCTURAL ELEMENTS
- ALL FACADE PANELS ARE INSTALLED VERTICALLY UNLESS OTHERWISE SPECIFIED
- THIS DRAWING SHOWS A SINGLE POWER MODULE AND IS TYPICAL FOR ALL POWER MODULES IN THE PROJECT. EACH MODULE, ALONG WITH ITS CORRESPONDING EQUIPMENT, PENETRATIONS, AND MEP SERVICES, IS IDENTIFIED BY A UNIQUE TAG.
- BUILDING LAYERS AND STRUCTURE SURFACE COLOUR:
 - RAL 9005 EXTERIOR
 - RAL 9002 INTERIOR
- ANTICORROSION LEVEL:
 - C4M EXTERIOR
 - C2M INTERIOR
- LIFELINE, SNOW GUARD AND LIGHTNING PROTECTION SYSTEMS ARE CURRENTLY BEING DETAILED AND WILL BE DEFINED AFTER THE CD SET IS COMPLETED

LEGEND

- REMOVABLE WALL
- EXPANSION JOINTS

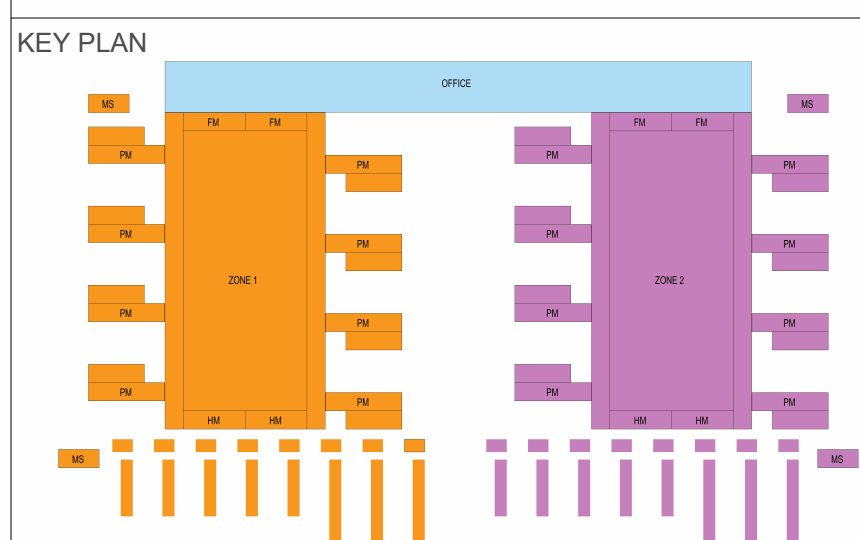

R02	CD SET - FOR INFORMATION	2026-07-24
R01	DD SET - FOR INFORMATION	2026-05-20
REV.	DESCRIPTION	DATE



PROJECT NAME

ECO DC MONALISA

DRAWING NAME

**ARCHITECTURAL BUILDING ELEVATIONS
- POWER MODULE**

PREPARED (ALSO SUBJECT RESPONSIBLE IF OTHER) L. MAVREK / K. KOZINA		
DOCUMENT RESPONSIBLE / APPROVED M. PACAK		
CAD / BIM SYSTEM AUTODESK REVIT 2025		
DOCUMENT NUMBER ECODC-VRT-MDC19-00-DR-A-20203		SHEET 1 OF 1
SHEET SIZE A1	DRAWING SCALE 1 : 50	DATE (YYYYMM-DD) 2026-07-24
		REVISION R02