


LEGAL DISCLAIMER: THIS DOCUMENT AND THE CONTENTS HEREIN ARE CONFIDENTIAL AND THE SOLE PROPERTY OF VERTIV GROUP CORP. REPRODUCTION, DISTRIBUTION OR UNAUTHORIZED USE OF THIS DOCUMENT OR ANY PARTS WITHIN THIS DOCUMENT ARE FORBIDDEN WITHOUT THE WRITTEN CONSENT OF VERTIV GROUP CORP.

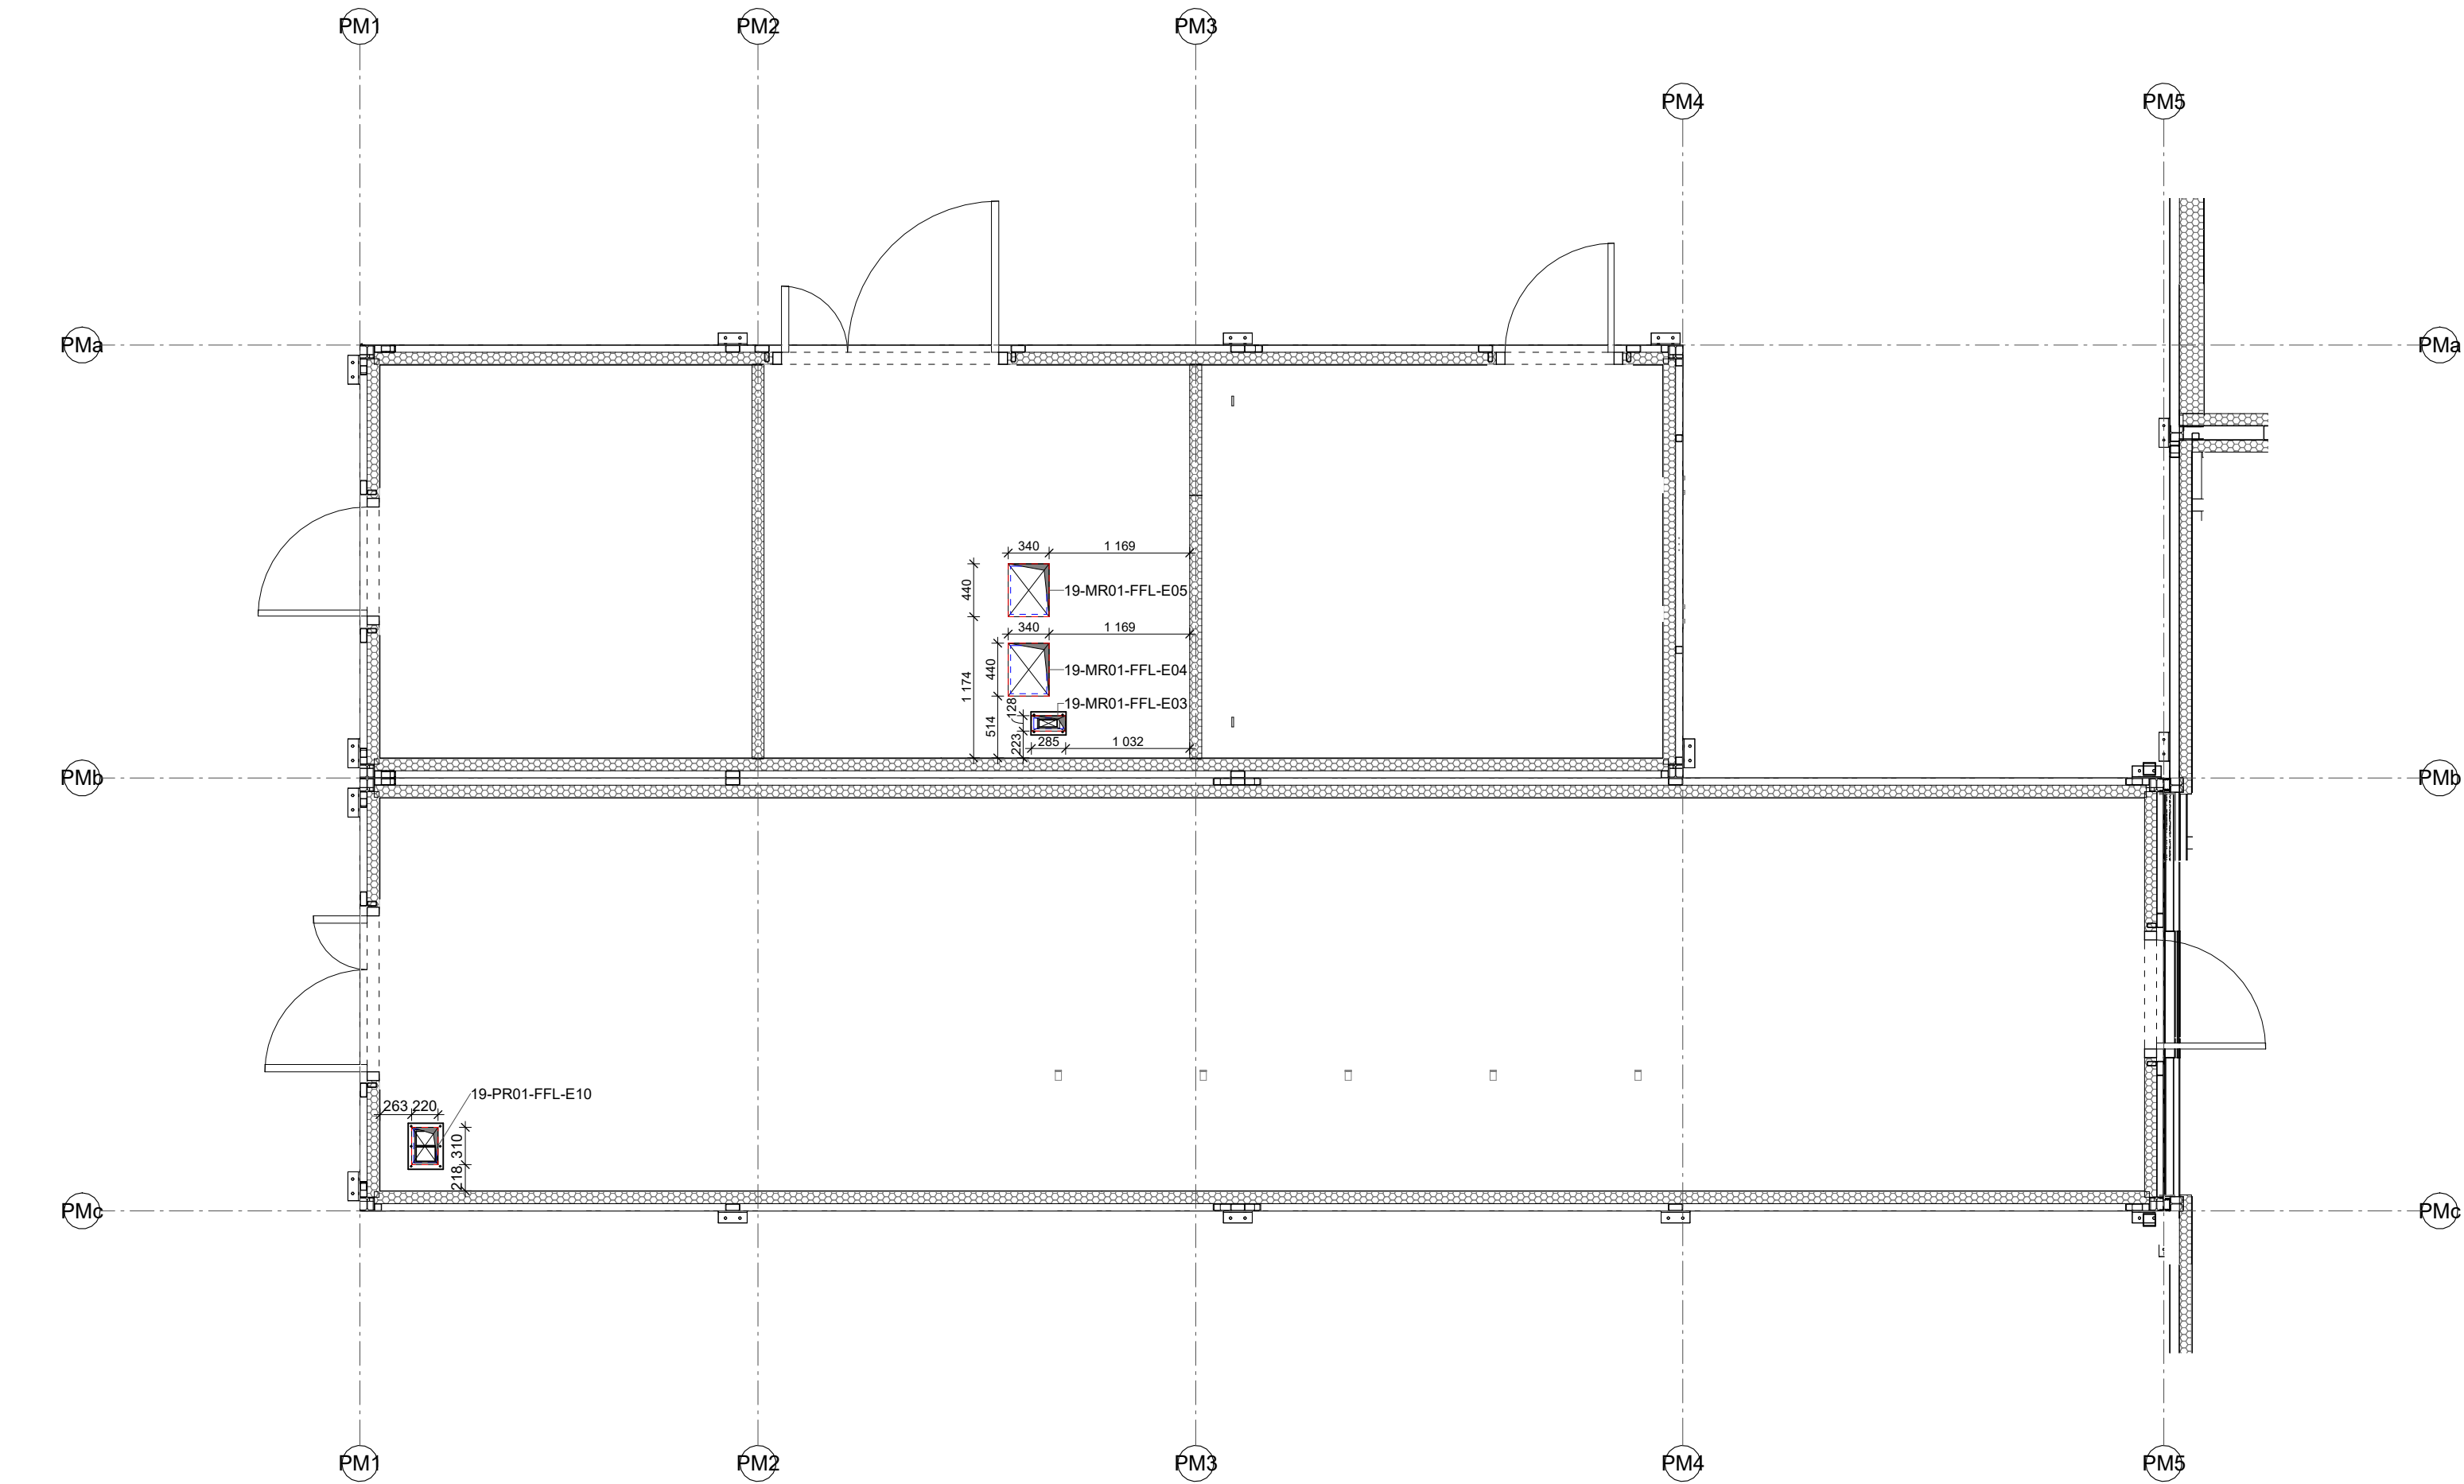


1 ARCHITECTURAL BUILDING PENETRATIONS – POWER MODULE – FLOOR PLAN
1 : 50

PENETRATION SCHEDULE - POWER MODULE FLOOR PLAN									
BUILDING NUMBER	ROOM NUMBER	GRID	PENETRATION MARK	PENETRATION TYPE	PENETRATION DESCRIPTION	PENETRATION DETAIL TYPE	FINAL OPENING DIAMETER	FINAL OPENING HEIGHT	FINAL OPENING WIDTH
19	PR01	FFL	E10	Roxtec GH 4x2 GALV.	CSB Power Room Cables	P03		220	310

PENETRATION SCHEDULE - MV MODULE FLOOR PLAN									
BUILDING NUMBER	ROOM NUMBER	GRID	PENETRATION MARK	PENETRATION TYPE	PENETRATION DESCRIPTION	PENETRATION DETAIL TYPE	FINAL OPENING DIAMETER	FINAL OPENING HEIGHT	FINAL OPENING WIDTH
19	MR01	FFL	E03	Roxtec GHM 3x1 GALV.	MVS GPL	P03		285	128
19	MR01	FFL	E04	Hilti	MV Ring	P15		340	440
19	MR01	FFL	E05	Hilti	MV Ring	P15		340	440

KEYNOTES

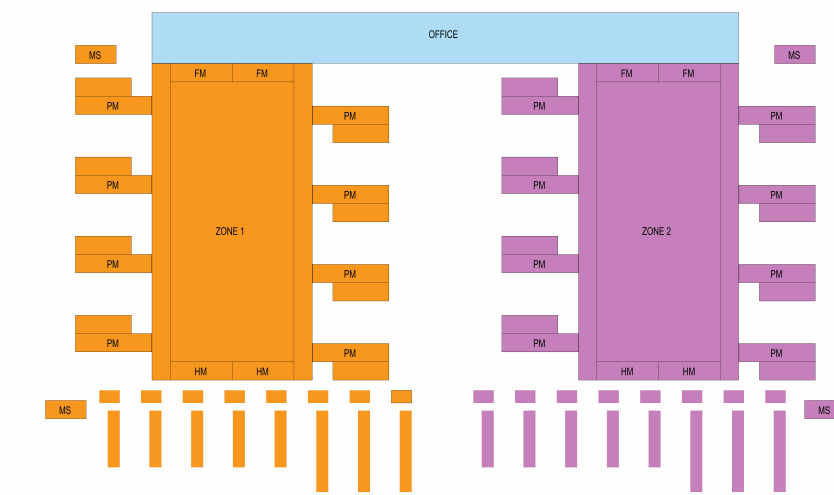

R01	CD SET - FOR INFORMATION	2026-07-24
REV.	DESCRIPTION	DATE



PROJECT NAME

ECO DC MONALISA

DRAWING NAME

ARCHITECTURAL BUILDING PENETRATIONS – POWER MODULE – FLOOR PLAN

PREPARED (ALSO SUBJECT RESPONSIBLE IF OTHER)
L. MAVREK / K. KOZINA

DOCUMENT RESPONSIBLE / APPROVED
M. PACAK

CAD / BIM SYSTEM AUTODESK REVIT 2025

DOCUMENT NUMBER	SHEET 1 OF 1
ECODC-VRT-MDC19-00-DR-A-40207	REVISION
SHEET SIZE A1	DATE (YYYYMM-DD) 2026-07-24
DRAWING SCALE 1:50	R01