




LEGAL DISCLAIMER: THIS DOCUMENT AND THE CONTENTS HEREIN ARE CONFIDENTIAL AND THE SOLE PROPERTY OF VERTIV GROUP CORP. REPRODUCTION, DISTRIBUTION OR UNAUTHORIZED USE OF THIS DOCUMENT OR ANY PARTS WITHIN THIS DOCUMENT ARE FORBIDDEN WITHOUT THE WRITTEN CONSENT OF VERTIV GROUP CORP.

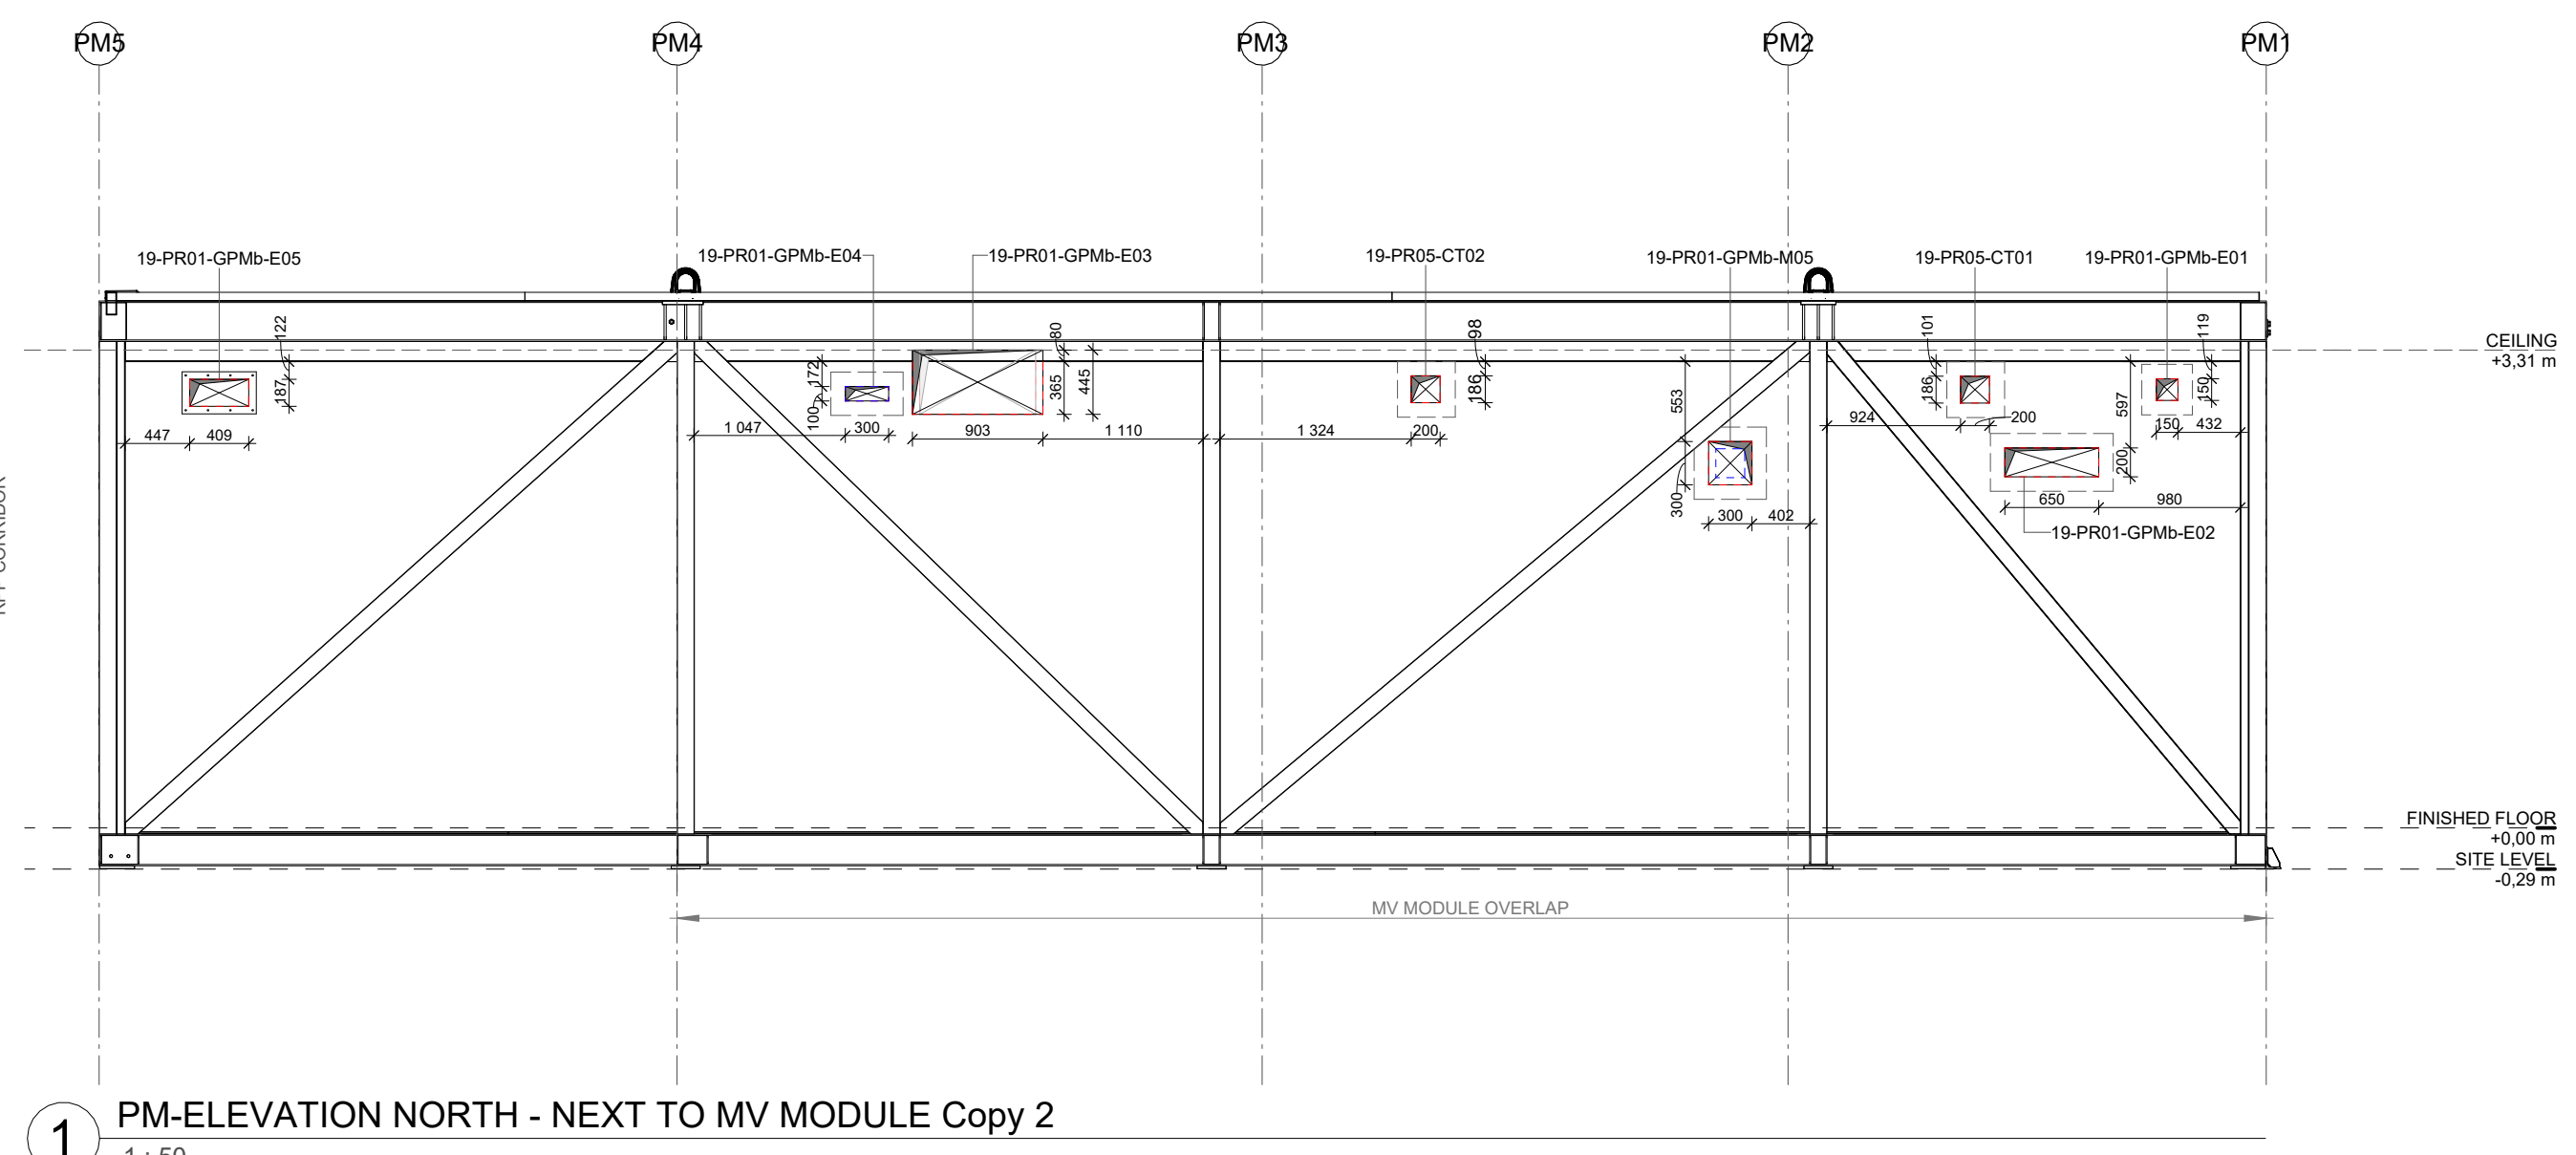


1 PM-ELEVATION NORTH - NEXT TO MV MODULE Copy 2
1 : 50

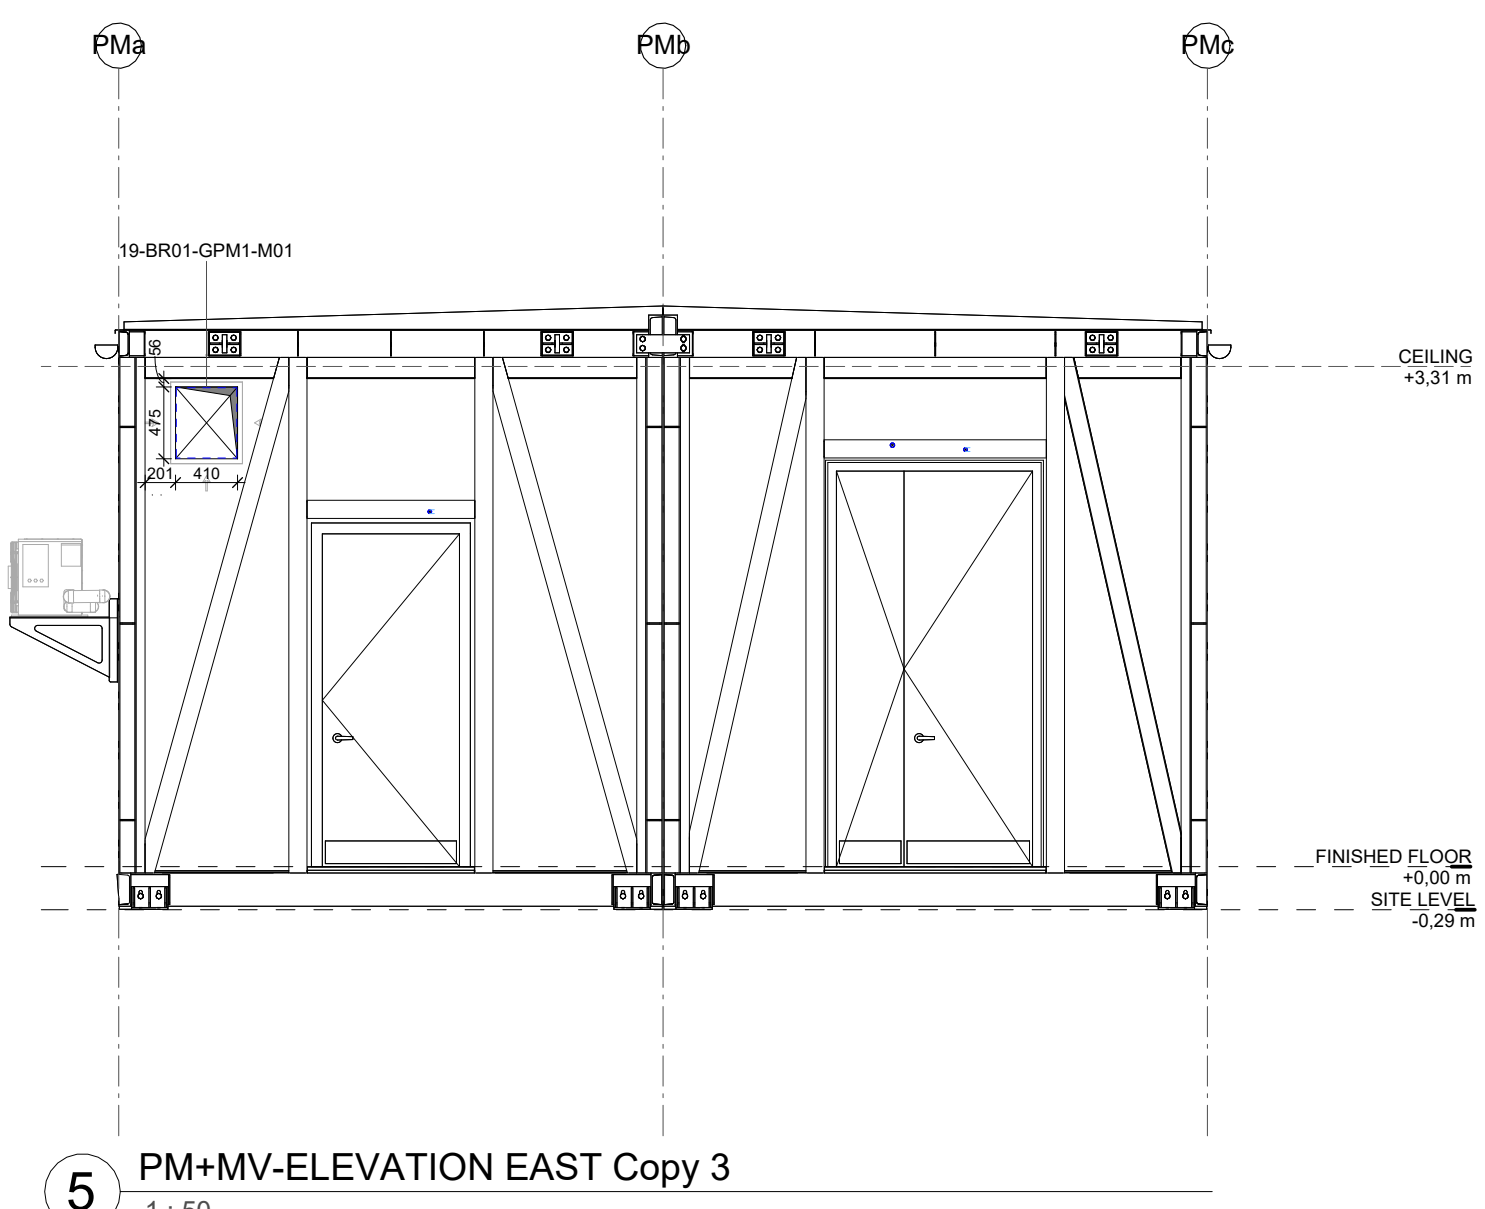


5 PM+MV-ELEVATION EAST Copy 3
1 : 50

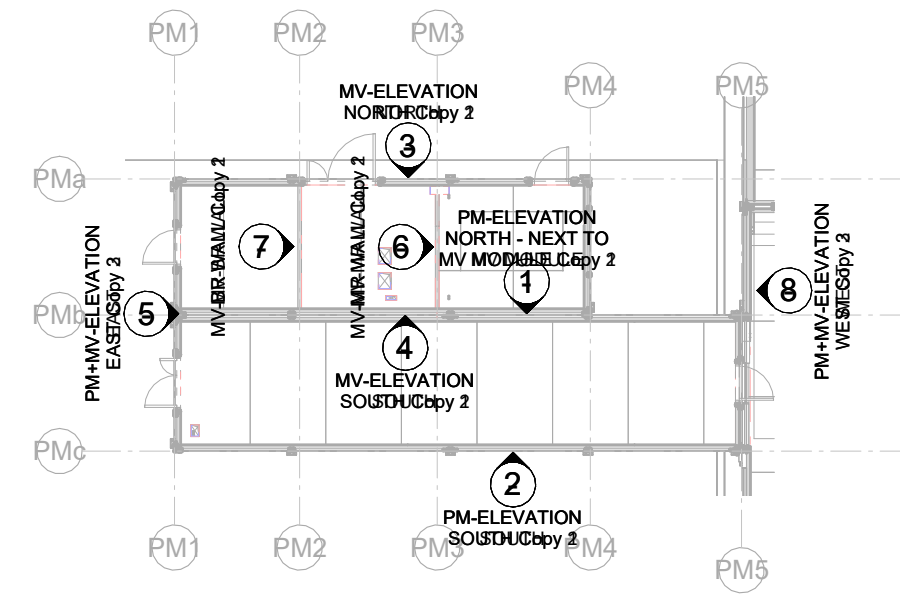


KEYPLAN – POWER MODULE – PEN ELEVATION POSITIONS Copy 3

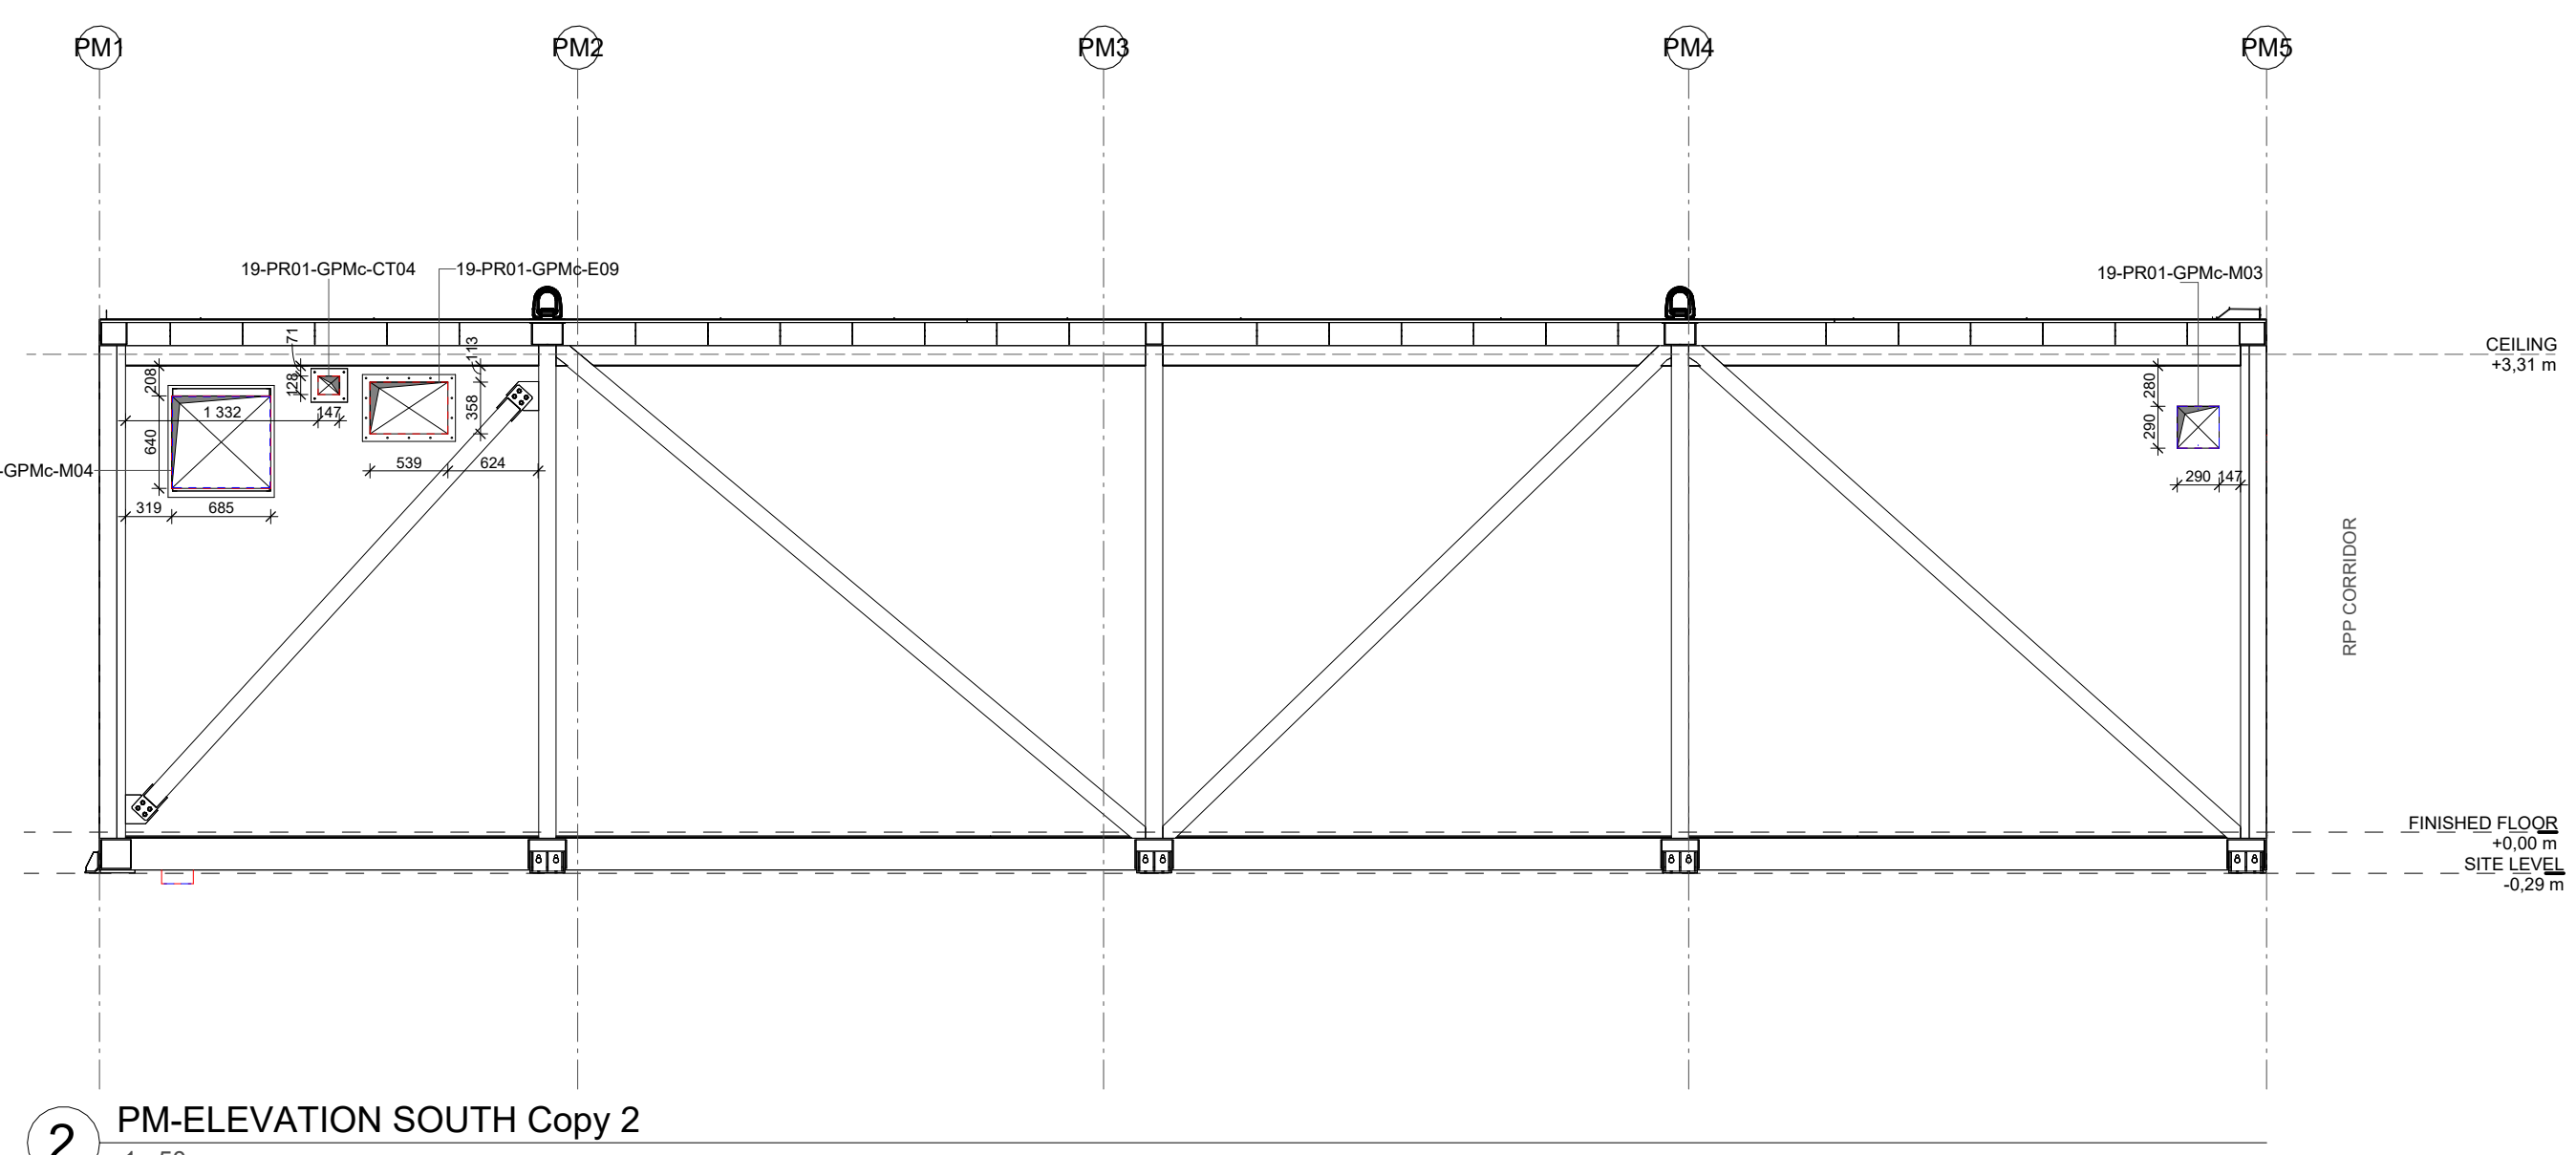


2 PM-ELEVATION SOUTH Copy 2
1 : 50

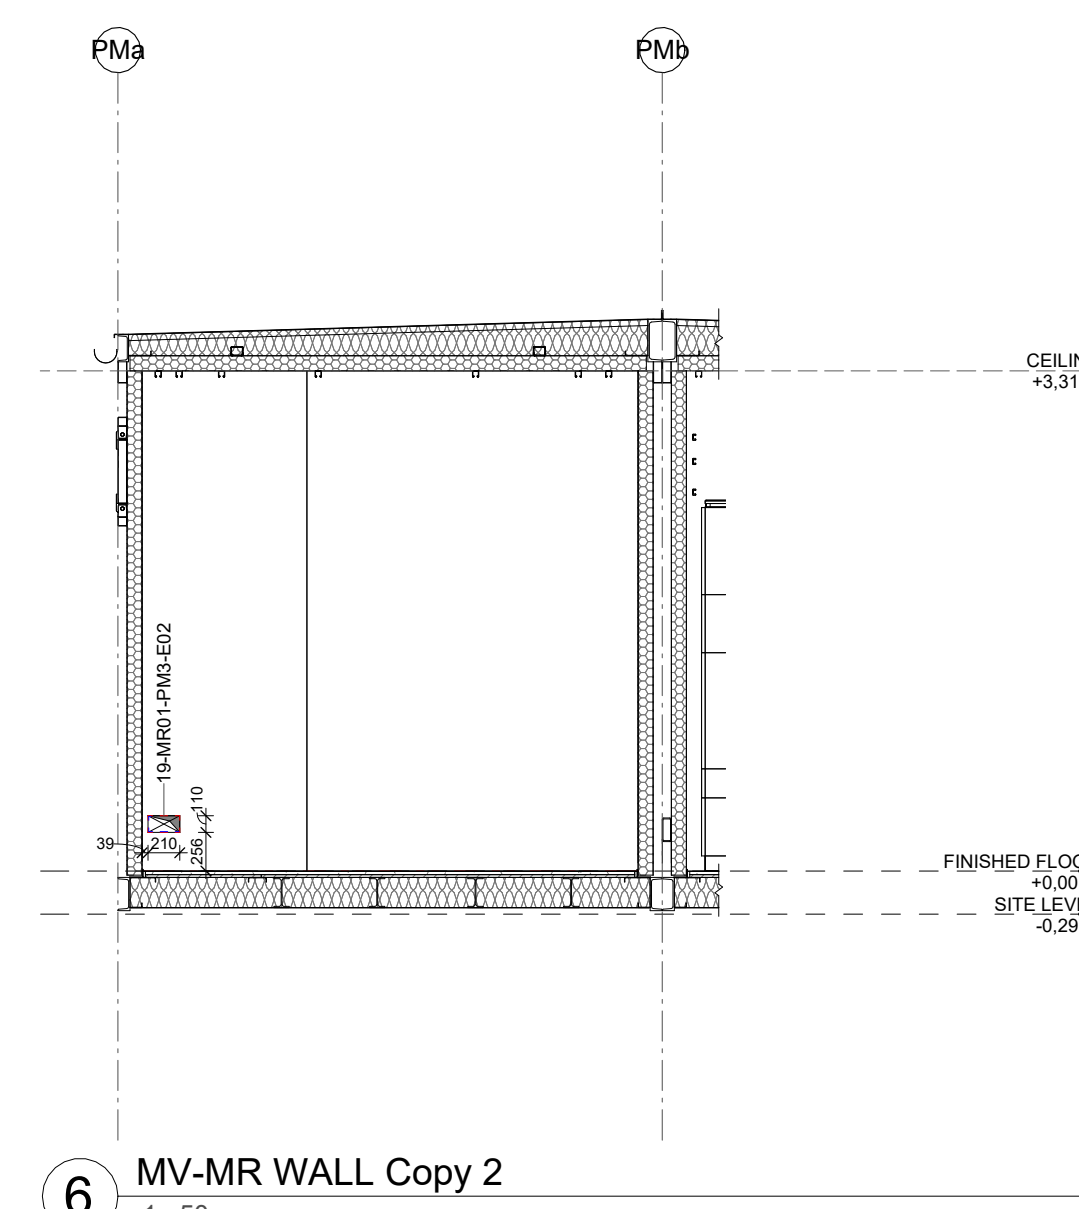


6 MV-MR WALL Copy 2
1 : 50

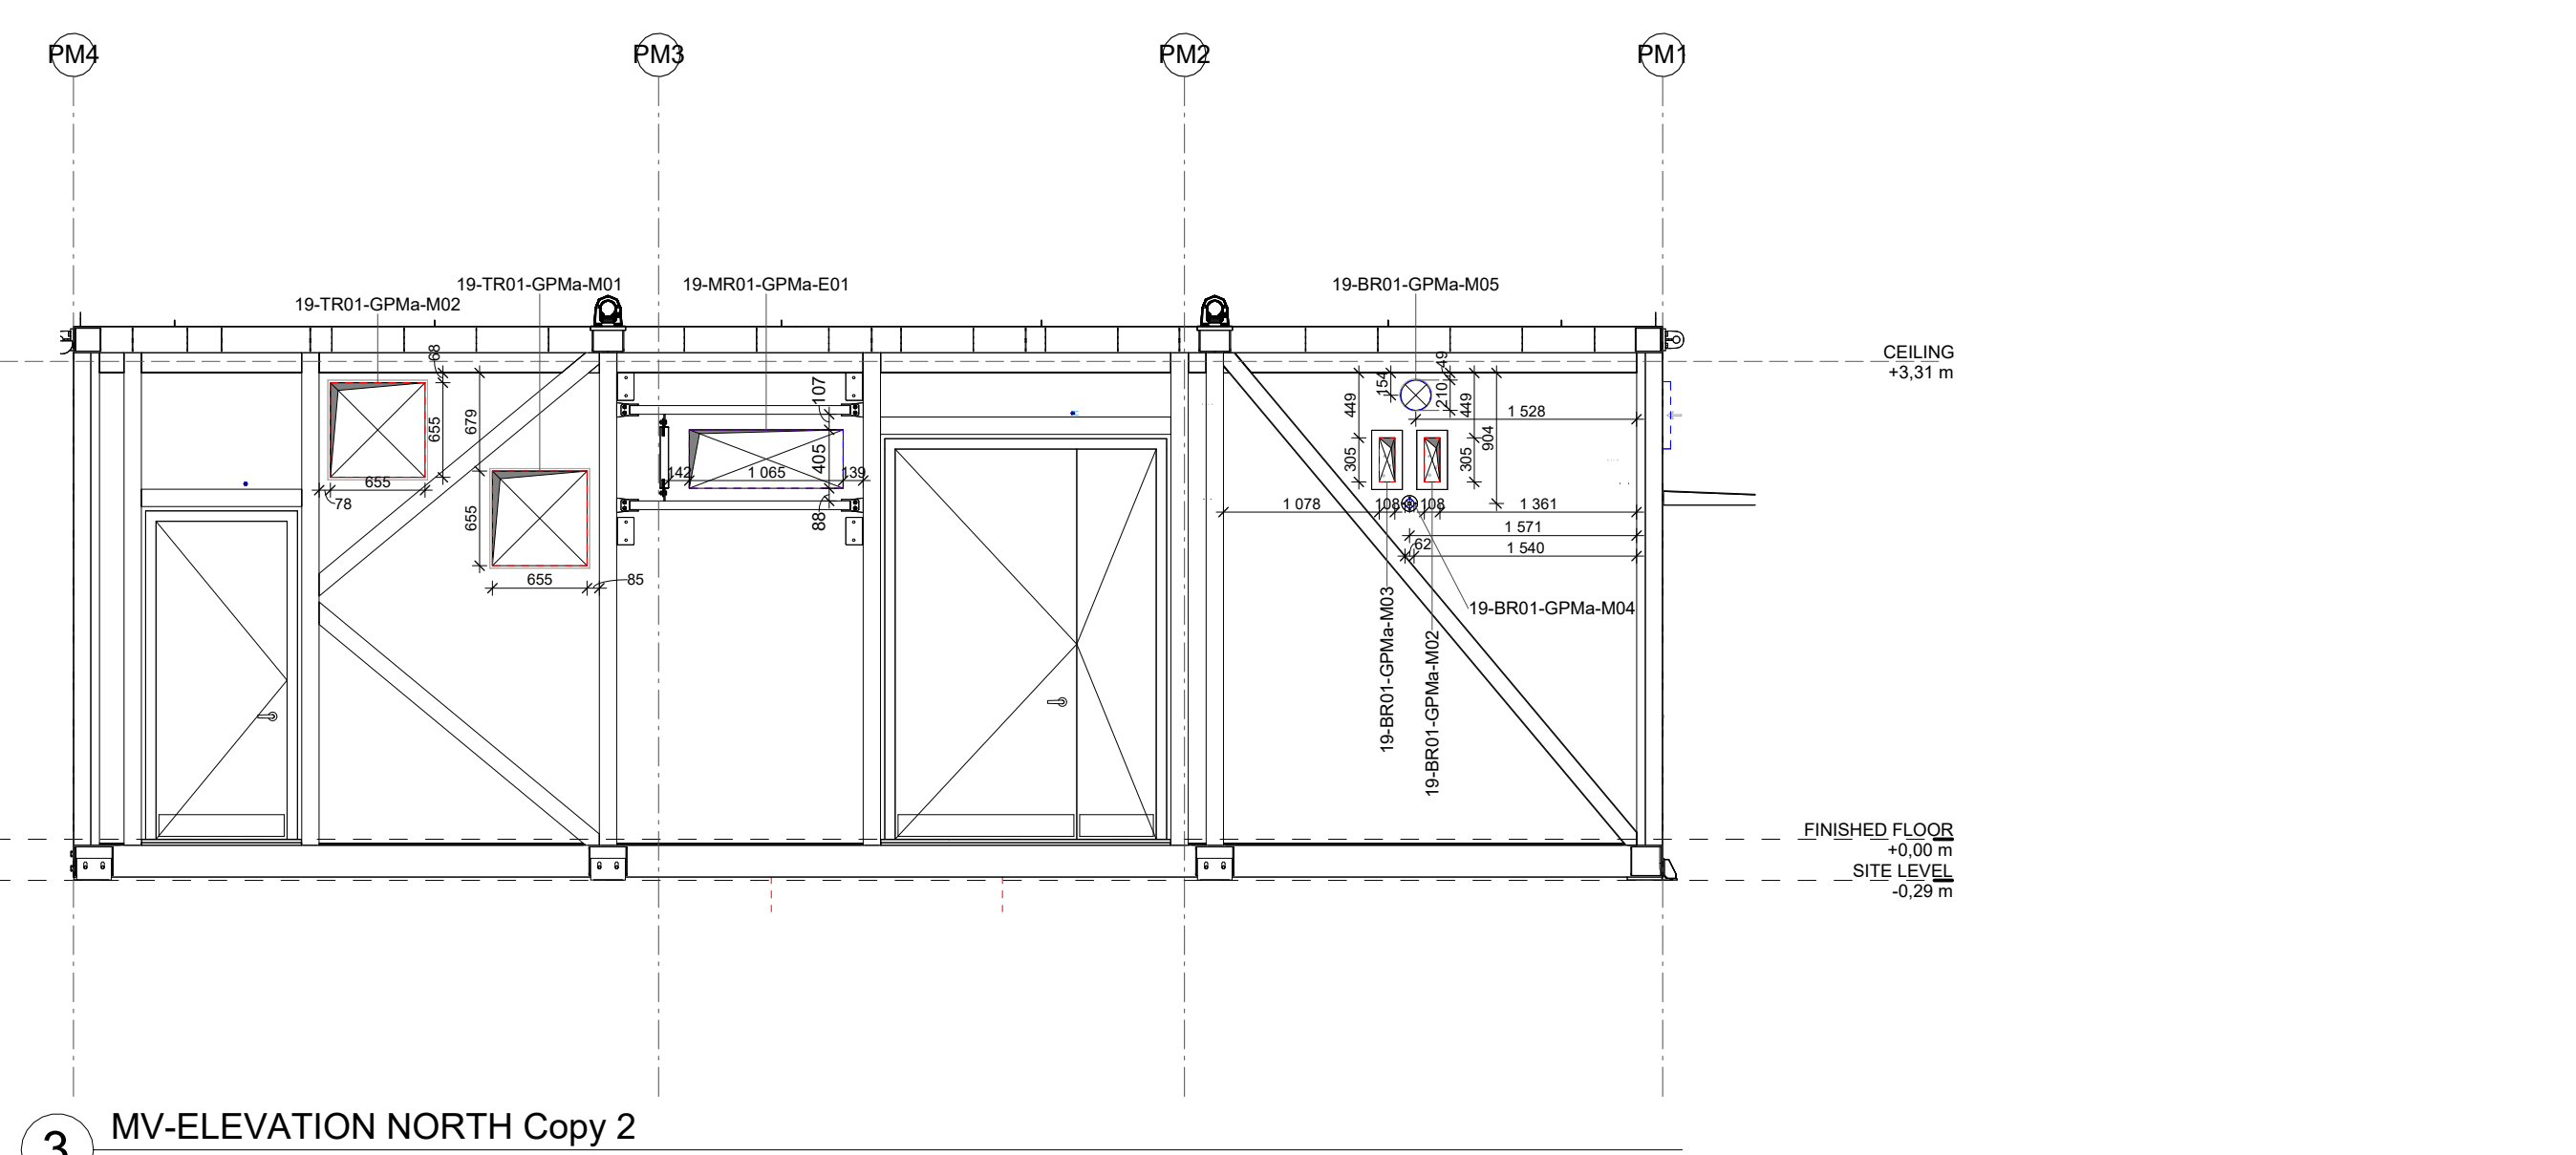


3 MV-ELEVATION NORTH Copy 2
1 : 50

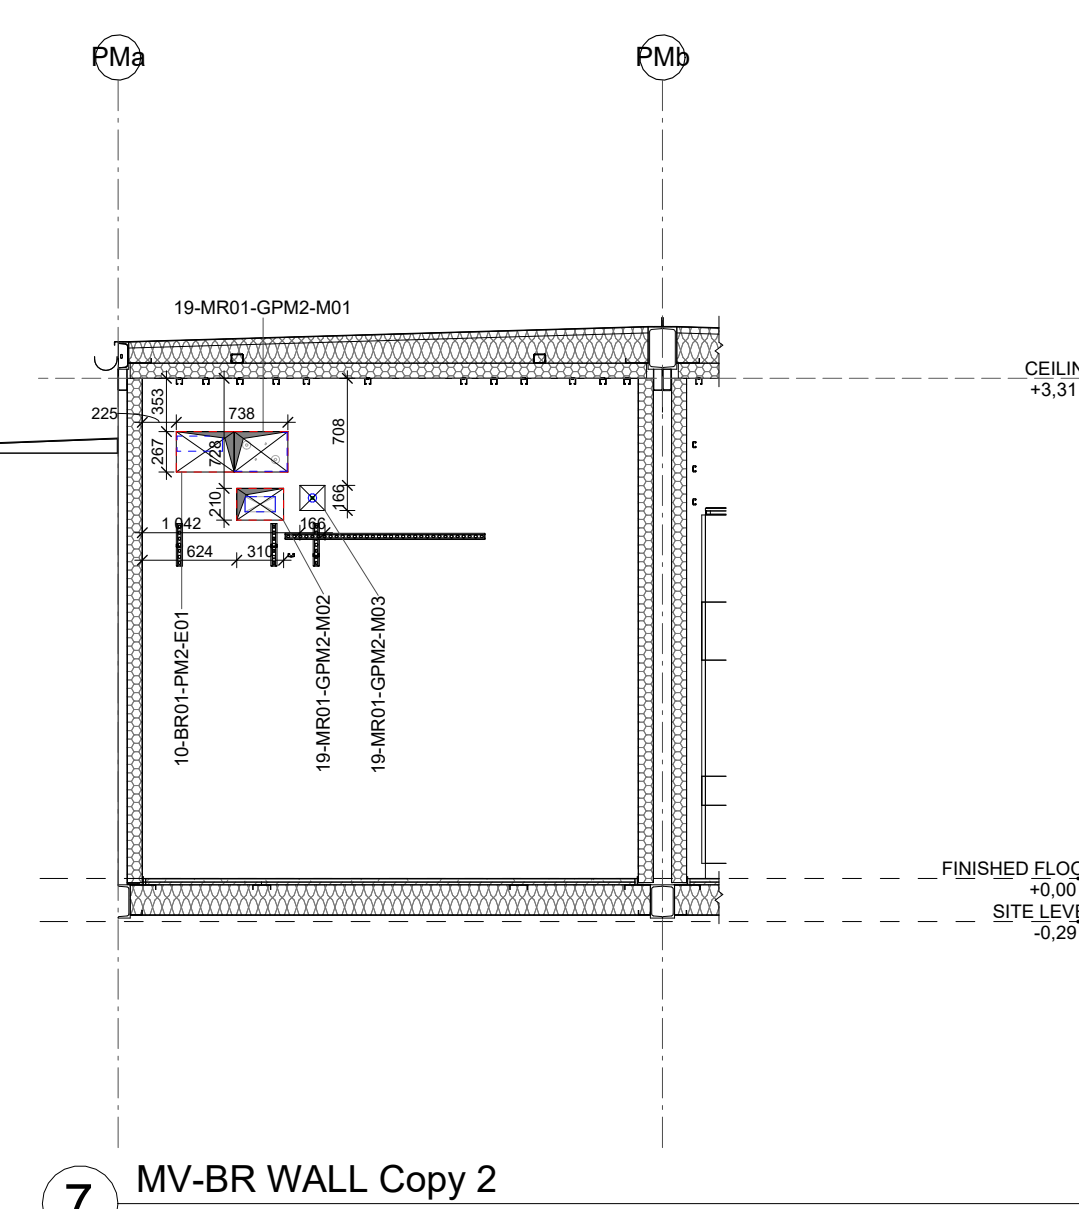

7 MV-BR WALL Copy 2
1 : 50

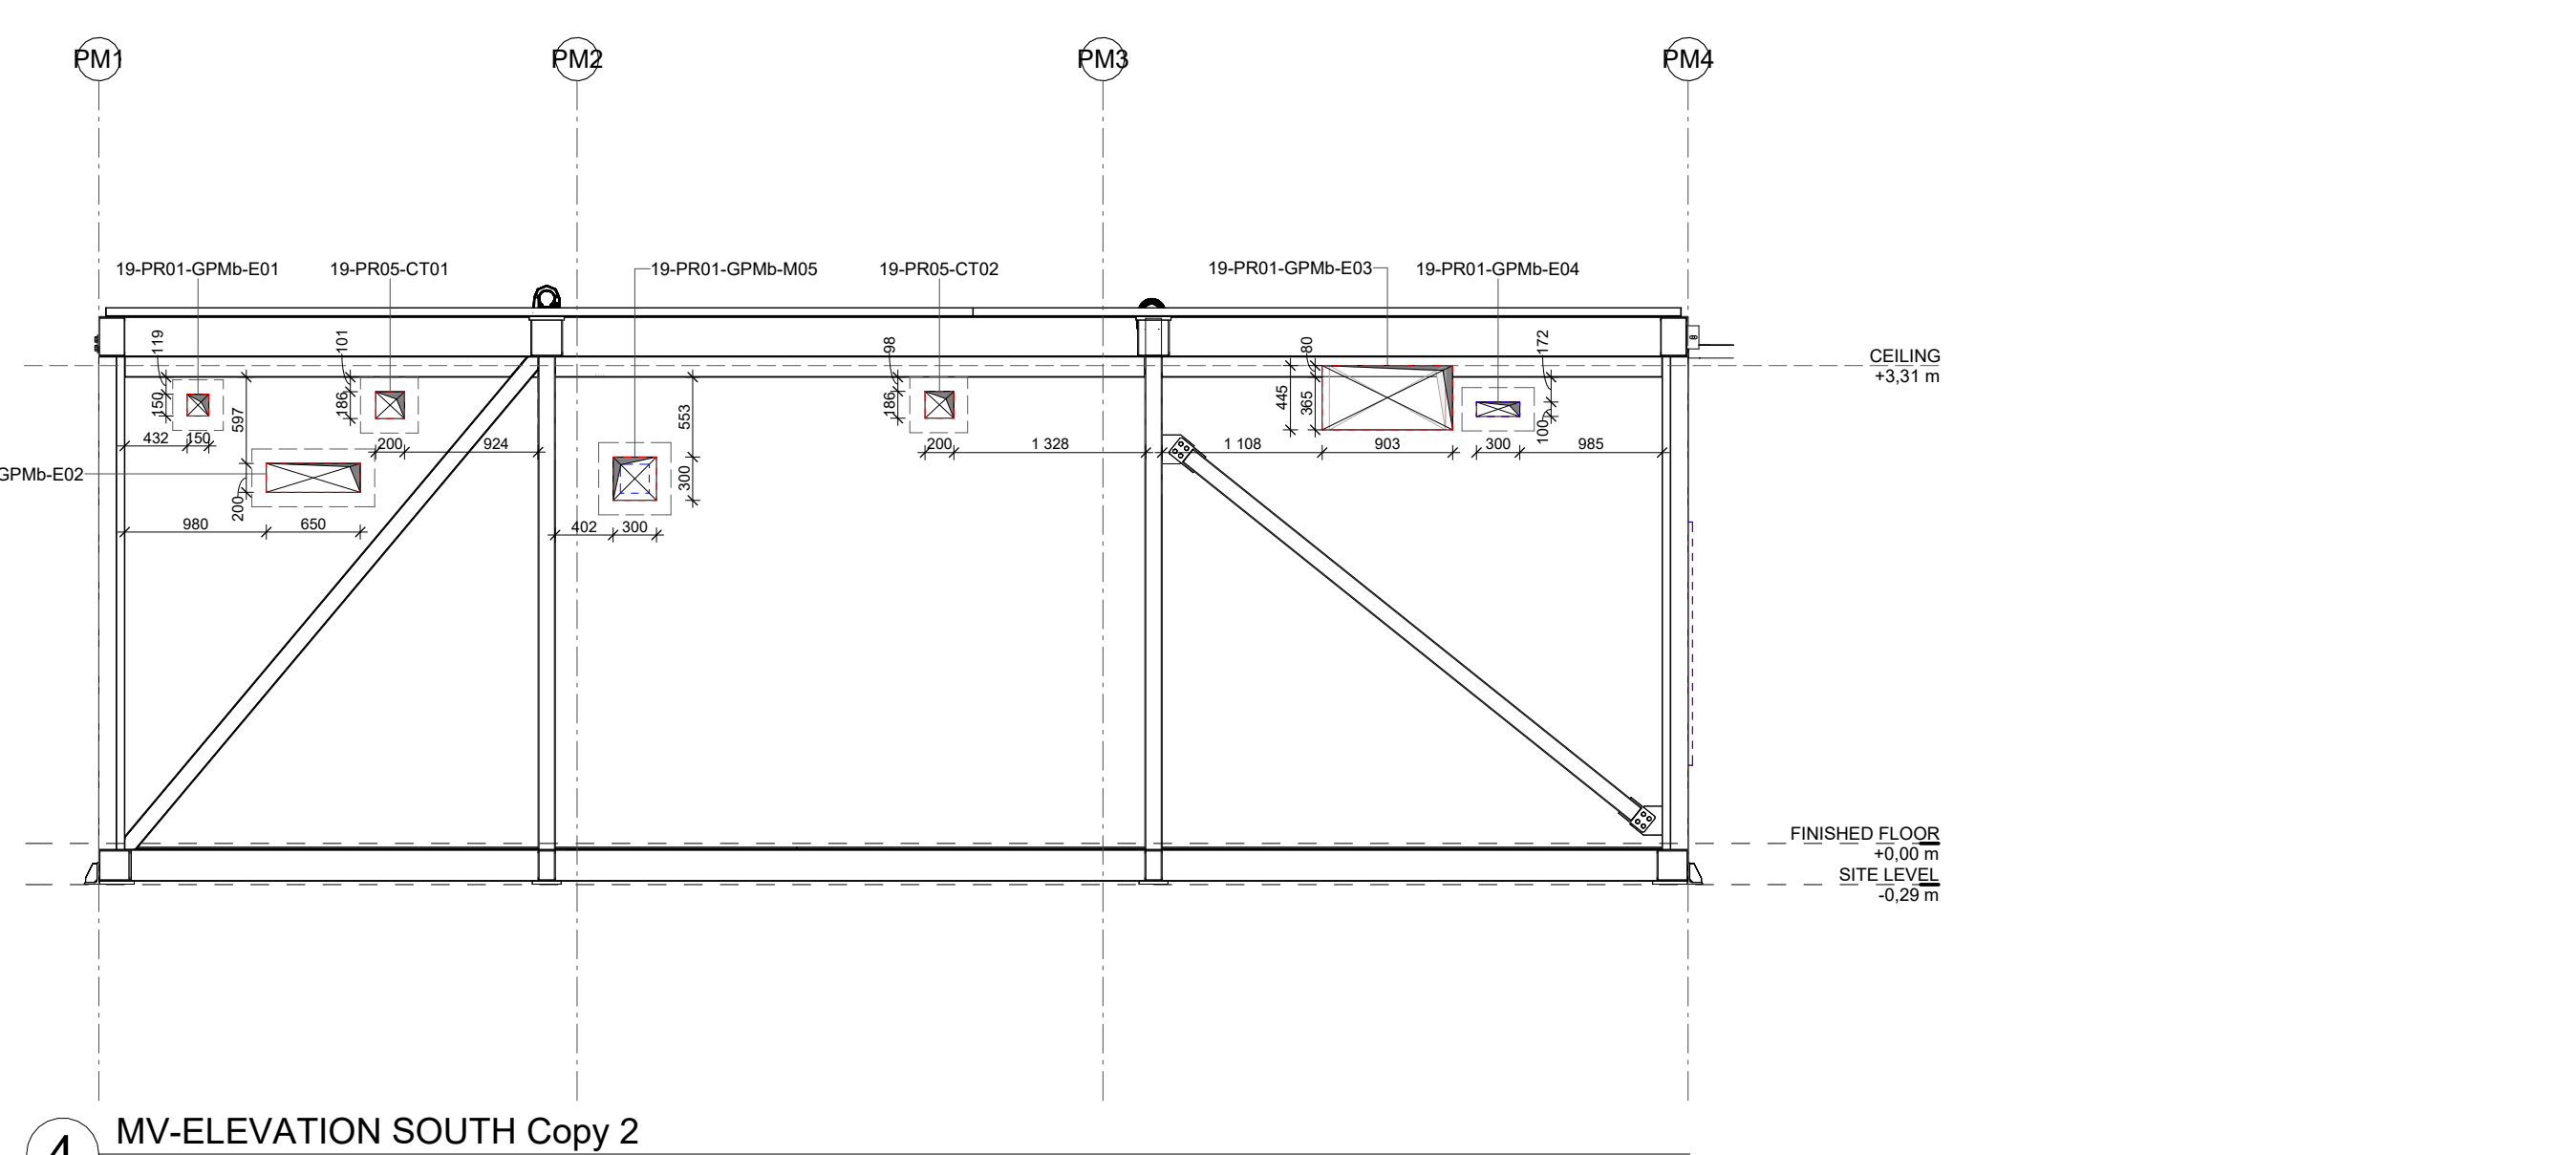

4 MV-ELEVATION SOUTH Copy 2
1 : 50

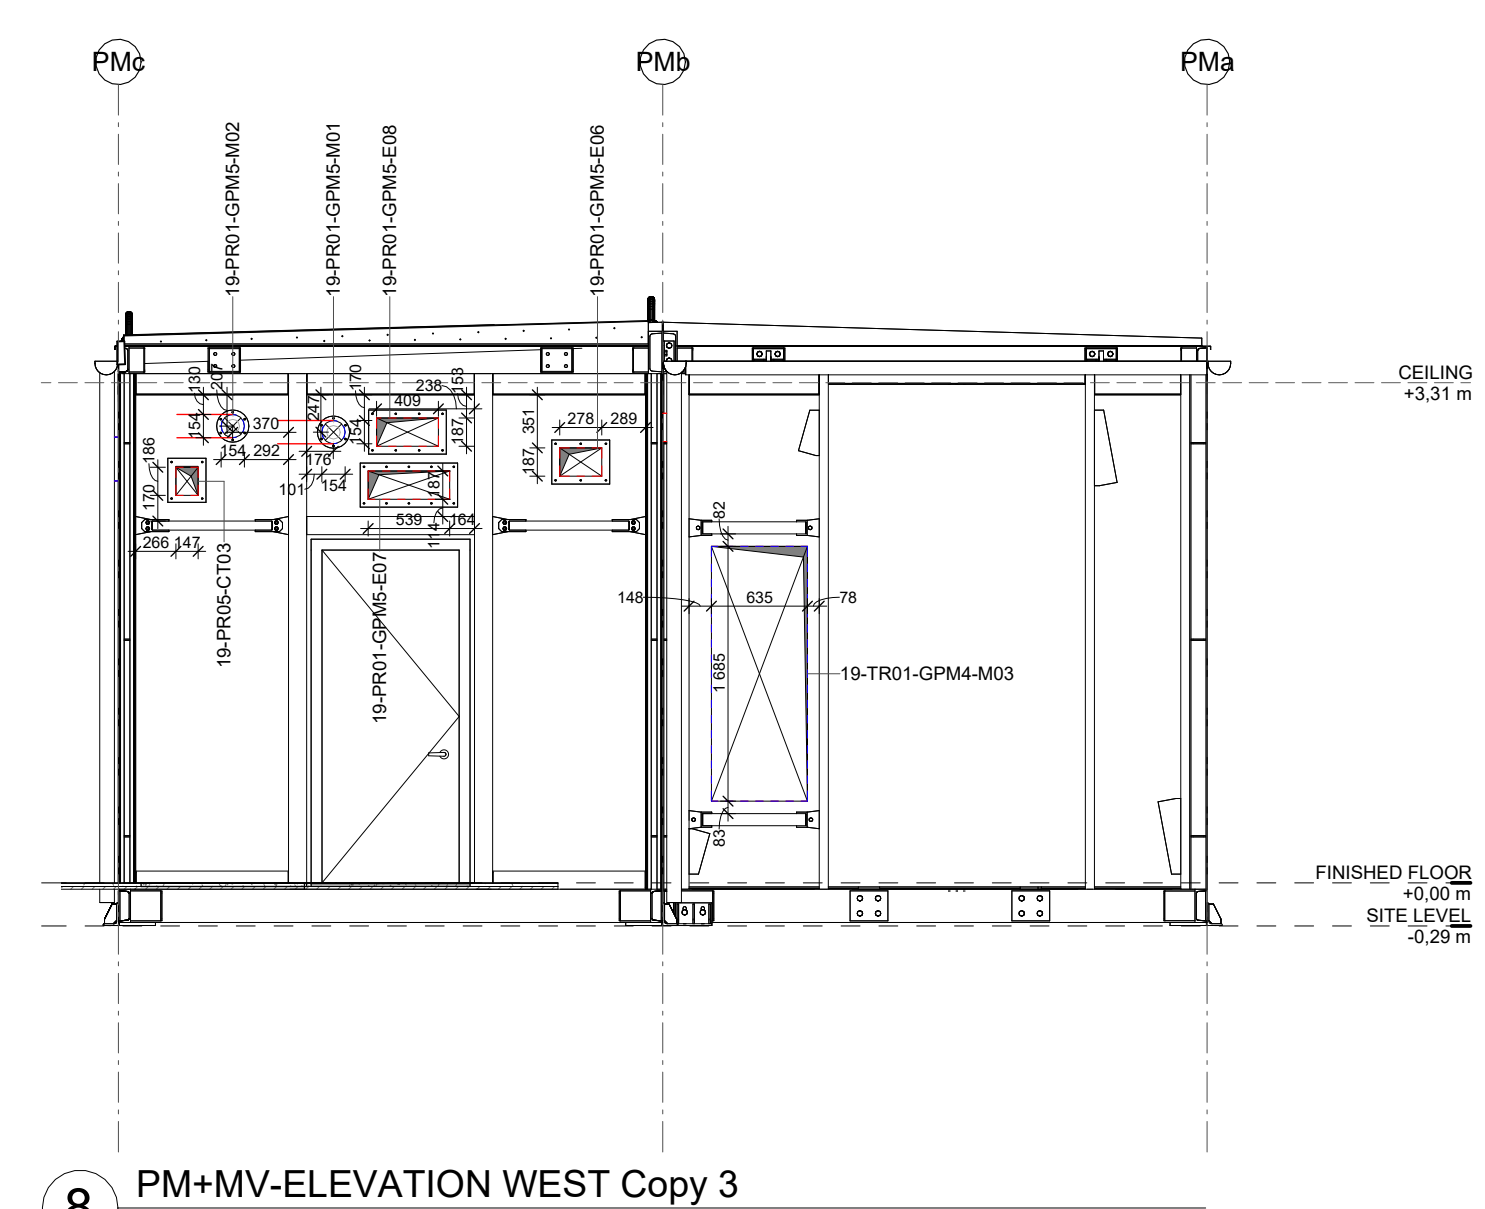


8 PM+MV-ELEVATION WEST Copy 3
1 : 50

PENETRATION SCHEDULE - POWER MODULE									
BUILDING NUMBER	ROOM NUMBER	GRID	PENETRATION MARK	PENETRATION TYPE	PENETRATION DESCRIPTION	PENETRATION DETAIL TYPE	FINAL OPENING DIAMETER	FINAL OPENING HEIGHT	FINAL OPENING WIDTH
19	PR01	GPmb	CT01	Hill	Controls Cables	P04		186	200
19	PR01	GPmb	CT02	Hill	Controls Cables	P04		186	200
19	PR01	GPm5	CT03	Roxtec GHM 4x1 GALV.	Controls Cables	P01		128	147
19	PR01	GPmc	CT04	Roxtec GHM 2x1 GALV.	Controls Cables	P01		128	147
19	PR01	GPmb	E01	Hill	GPL - Battery Room	P04		150	150
19	PR01	GPmb	E02	Hill	DC Cables	P04		200	650
19	PR01	<varies>	E03	Hill	Busbar	P09		445	<varies>
19	PR01	<varies>	E04	Hill	GPL + Controls - Transformer Room	P04		100	<varies>
19	PR01	GPmb	E05	Roxtec GH 4x3 GALV.	Chiller	P01		187	408
19	PR01	GPm5	E06	Roxtec GH 4x2 AISI 316	Q2.7 - Q2.13 Cables	P01		187	278
19	PR01	GPm5	E07	Roxtec GH 4x4 AISI 316	Q2.7 - Q2.13 Cables	P01		187	539
19	PR01	GPm5	E08	Roxtec GH 4x3 AISI 316	RPP (2x) + Q1.4-Q1.11	P01		187	409
19	PR01	GPmc	E09	Roxtec GH 4+4x4 AISI 316	Generator Cables	P01		358	539
19	PR01	GPm5	M01	Roxtec RS + SLFRS 125	Roxtec	P02	154		
19	PR01	GPm5	M02	Roxtec RS + SLFRS 125	Roxtec	P02	154		
19	PR01	GPmc	M03	TROX FKRS-EU	Fire damper	P08	290	290	
19	PR01	GPmc	M04	BSV 675x630 EV500 SGHD ASM	Pressure Relief Damper + intrusion protection	P10b	640	685	
19	PR01	GPmb	M05	TROX FKA2-EU	Fire damper	P08	300	300	

PENETRATION SCHEDULE - BATTERY ROOM									
BUILDING NUMBER	ROOM NUMBER	GRID	PENETRATION MARK	PENETRATION TYPE	PENETRATION DESCRIPTION	PENETRATION DETAIL TYPE	FINAL OPENING DIAMETER	FINAL OPENING HEIGHT	FINAL OPENING WIDTH
19	BR01	PM2	E01	Hill	GPL - RMU Room	P05	267	383	
19	BR01	GPm1	M01	Klimasoprema	AFZV Weather Louvre	P11	475	410	
19	BR01	GPma	M02	Roxtec GHM80 8x1 AISI	Roxtec	P01	305	108	
19	BR01	GPma	M03	Roxtec GHM80 8x1 AISI	Roxtec	P01	305	108	
19	BR01	GPma	M04	RS 43 AISI316	Roxtec	P02	62		
19	BR01	GPma	M05	Systemair IGC 200	IGC Weather Louvre	P16	210		

PENETRATION SCHEDULE - MV ROOM									
BUILDING NUMBER	ROOM NUMBER	GRID	PENETRATION MARK	PENETRATION TYPE	PENETRATION DESCRIPTION	PENETRATION DETAIL TYPE	FINAL OPENING DIAMETER	FINAL OPENING HEIGHT	FINAL OPENING WIDTH
19	MR01	GPma	E01	Opening	Arc Blast Channel	P13	405	1065	
19	MR01	PM3	E02	Hill	MV Cables	P05	110	210	
19	MR01	GPm2	M01	Hill	DX Pipes	P05	267	355	
19	MR01	GPm2	M02	TROX FKA2-EU	Fire damper	P07	210	310	
19	MR01	GPm2	M03	Hill	Condensate Pipe	P05	56		

PENETRATION SCHEDULE - TRANSFORMER ROOM									
BUILDING NUMBER	ROOM NUMBER	GRID	PENETRATION MARK	PENETRATION TYPE	PENETRATION DESCRIPTION	PENETRATION DETAIL TYPE	FINAL OPENING DIAMETER	FINAL OPENING HEIGHT	FINAL OPENING WIDTH
19	TR01	GPma	M01	Systemair WAK 60 Louvre	Louvre	P12	655	655	
19	TR01	GPma	M02	Systemair WAK 60 Louvre	Louvre	P12	655	655	
19	TR01	GPm4	M03	TROX WG-AL Louvre 600x1650	Louvre + intrusion protection	P11b	1685	635	

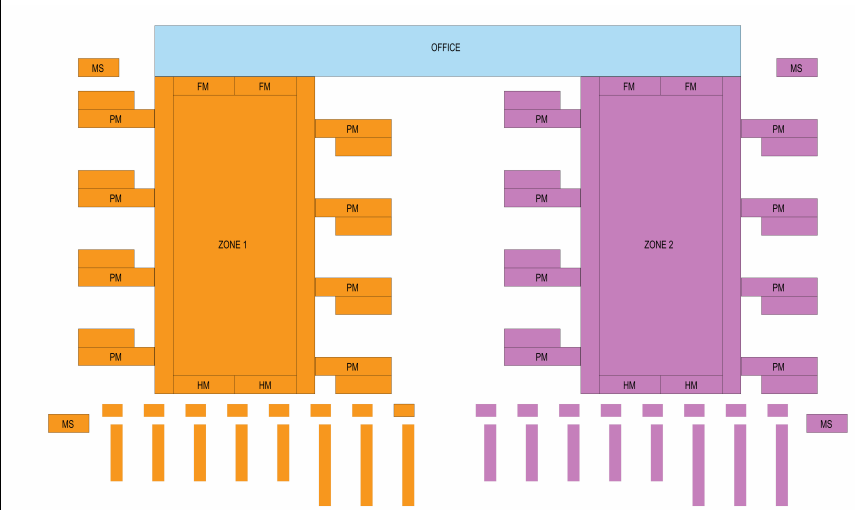

PE01	FOR INFORMATION	2026-09-15
R02	CD SET - FOR INFORMATION	2026-09-11
R01	CD SET - FOR INFORMATION	2026-07-24

REV.	DESCRIPTION	DATE
------	-------------	------



PROJECT NAME
ECO DC MONALISA

DRAWING NAME
ARCHITECTURAL BUILDING PENETRATIONS – POWER MODULE – ELEVATIONS

PREPARED (ALSO SUBJECT RESPONSIBLE IF OTHER)
L. MAVREK / K. KOZINA

DOCUMENT RESPONSIBLE (APPROVED)
M. PACAK

CAD / BIM SYSTEMS
AUTODESK REVIT 2025

DOCUMENT NUMBER		SHEET 1 OF 1	
ECODC-VRT-MDC19-00-DR-A-40208		REVISION	
SHEET SIZE A0	DRAWING SCALE 1:50	DATE (YYYYMMDD) 2026-09-15	PE01