




LEGAL DISCLAIMER: THIS DOCUMENT AND THE CONTENTS HEREIN ARE CONFIDENTIAL AND THE SOLE PROPERTY OF VERTIV GROUP CORP. REPRODUCTION, DISTRIBUTION OR UNAUTHORIZED USE OF THIS DOCUMENT OR ANY PARTS WITHIN THIS DOCUMENT ARE FORBIDDEN WITHOUT THE WRITTEN CONSENT OF VERTIV GROUP CORP.

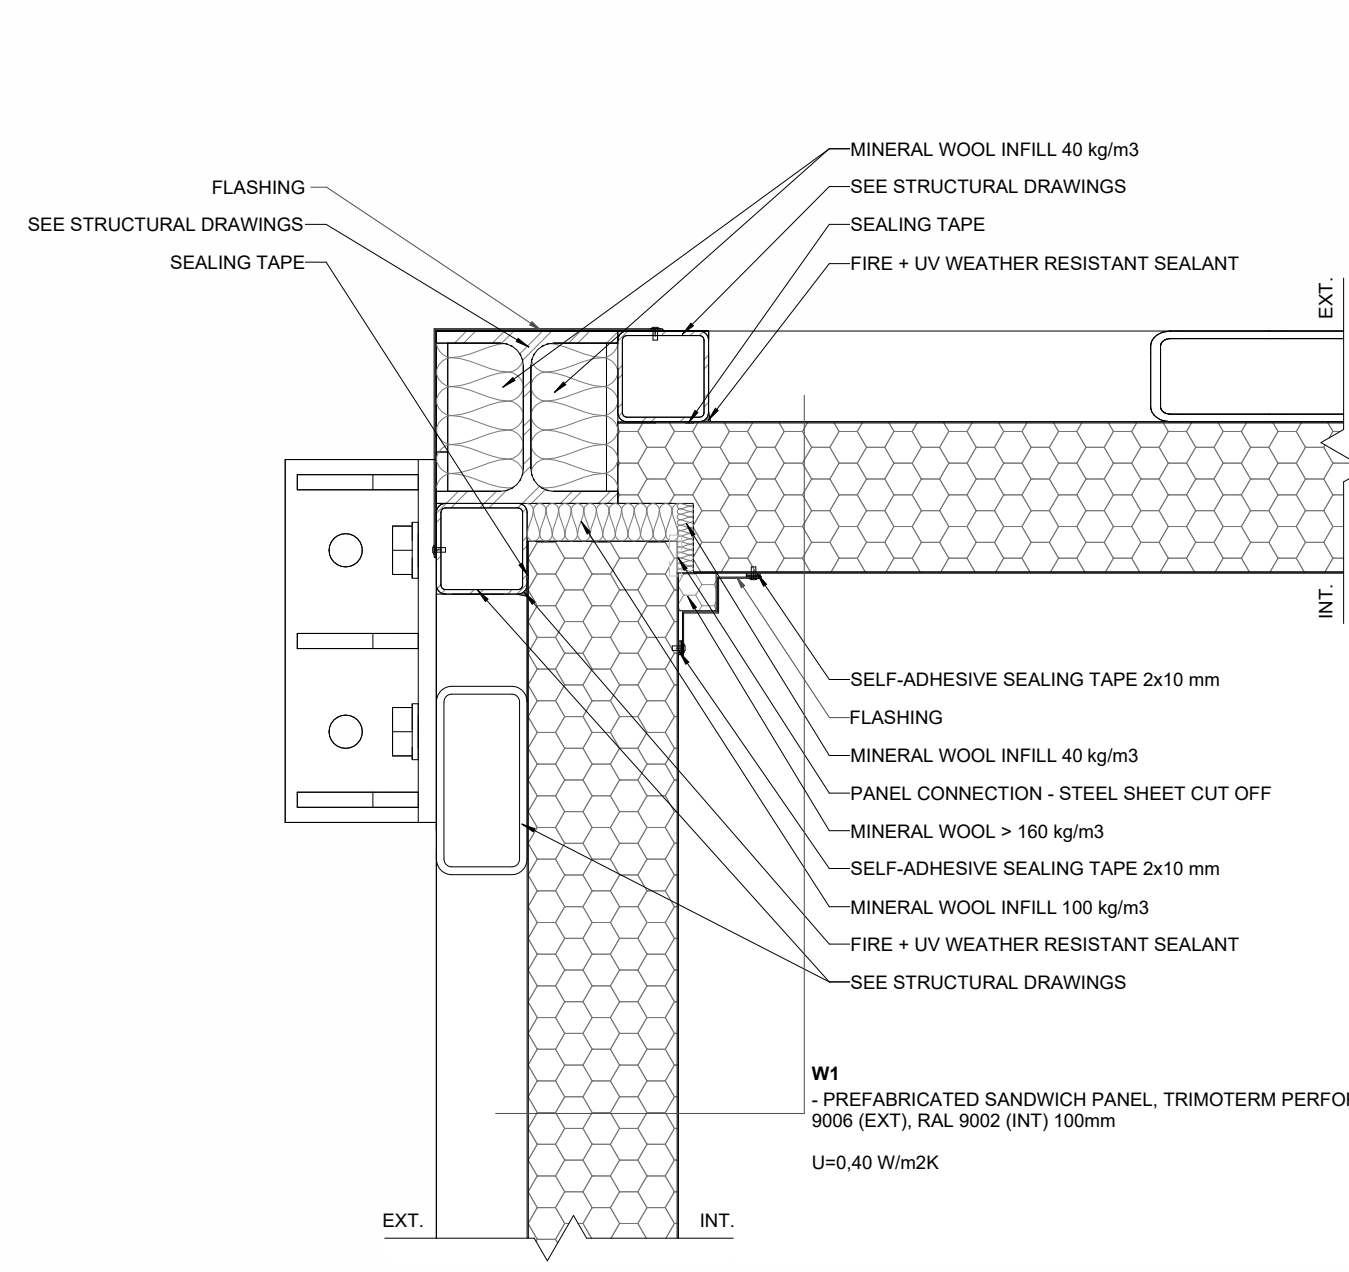


H01 MV/MS - MODULE CORNER
1:5

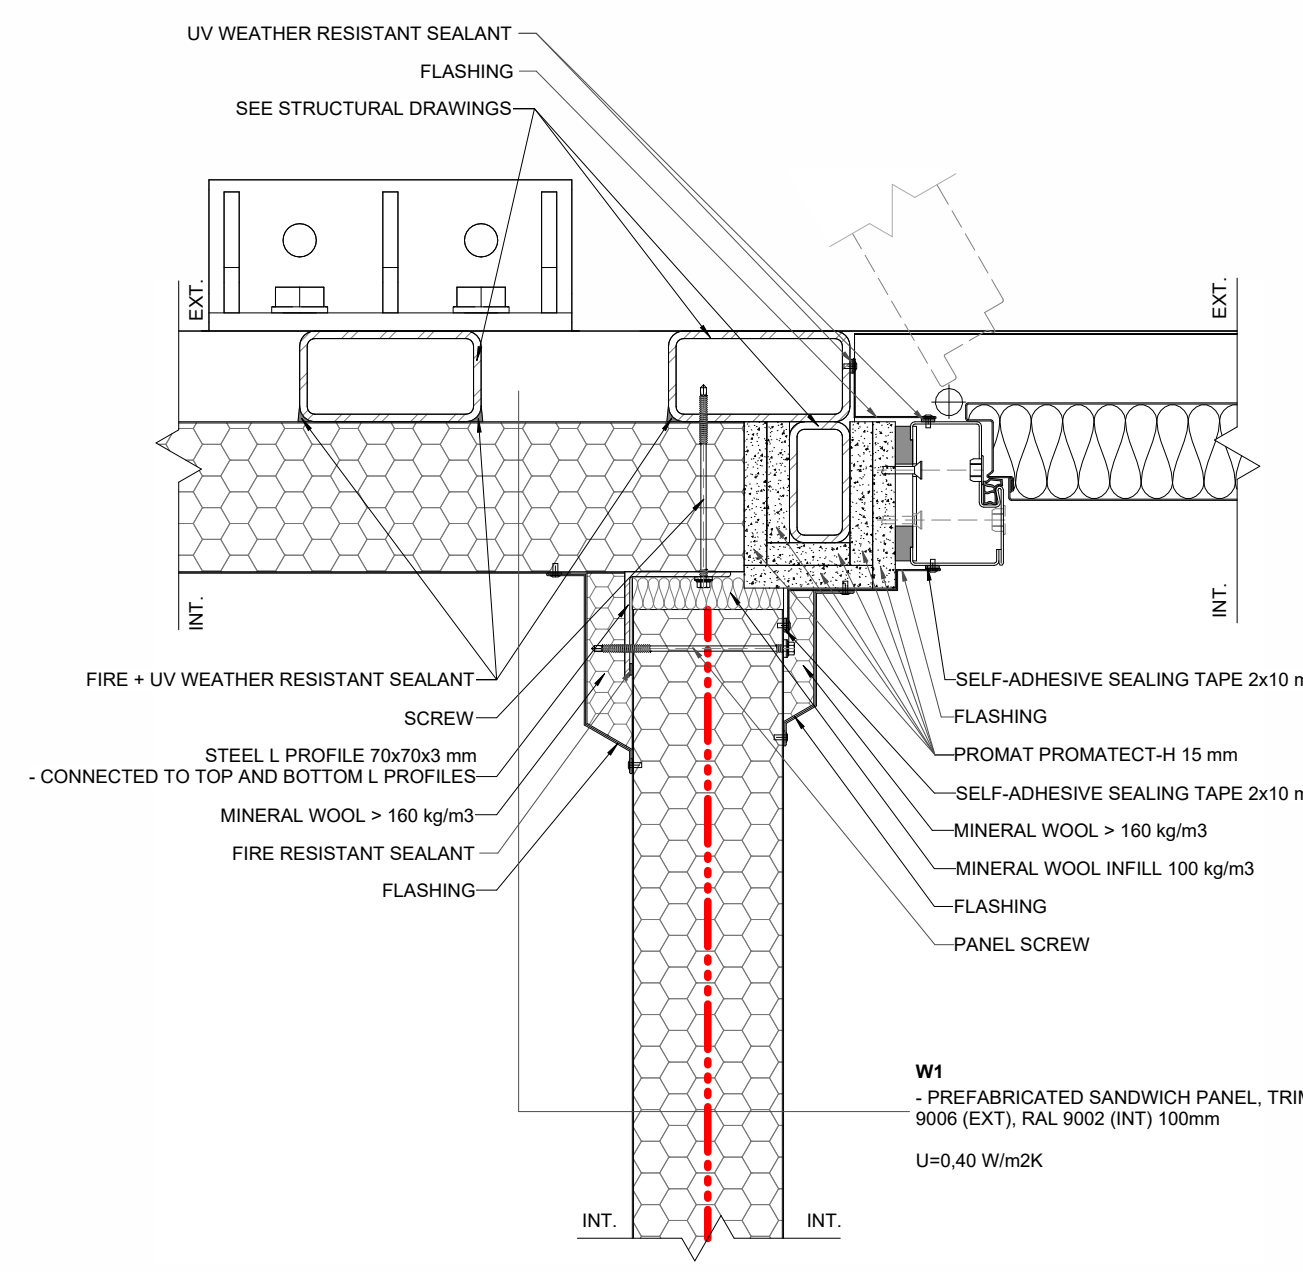


H02 MV - INT./EXT. WALL CONNECTION
1:5

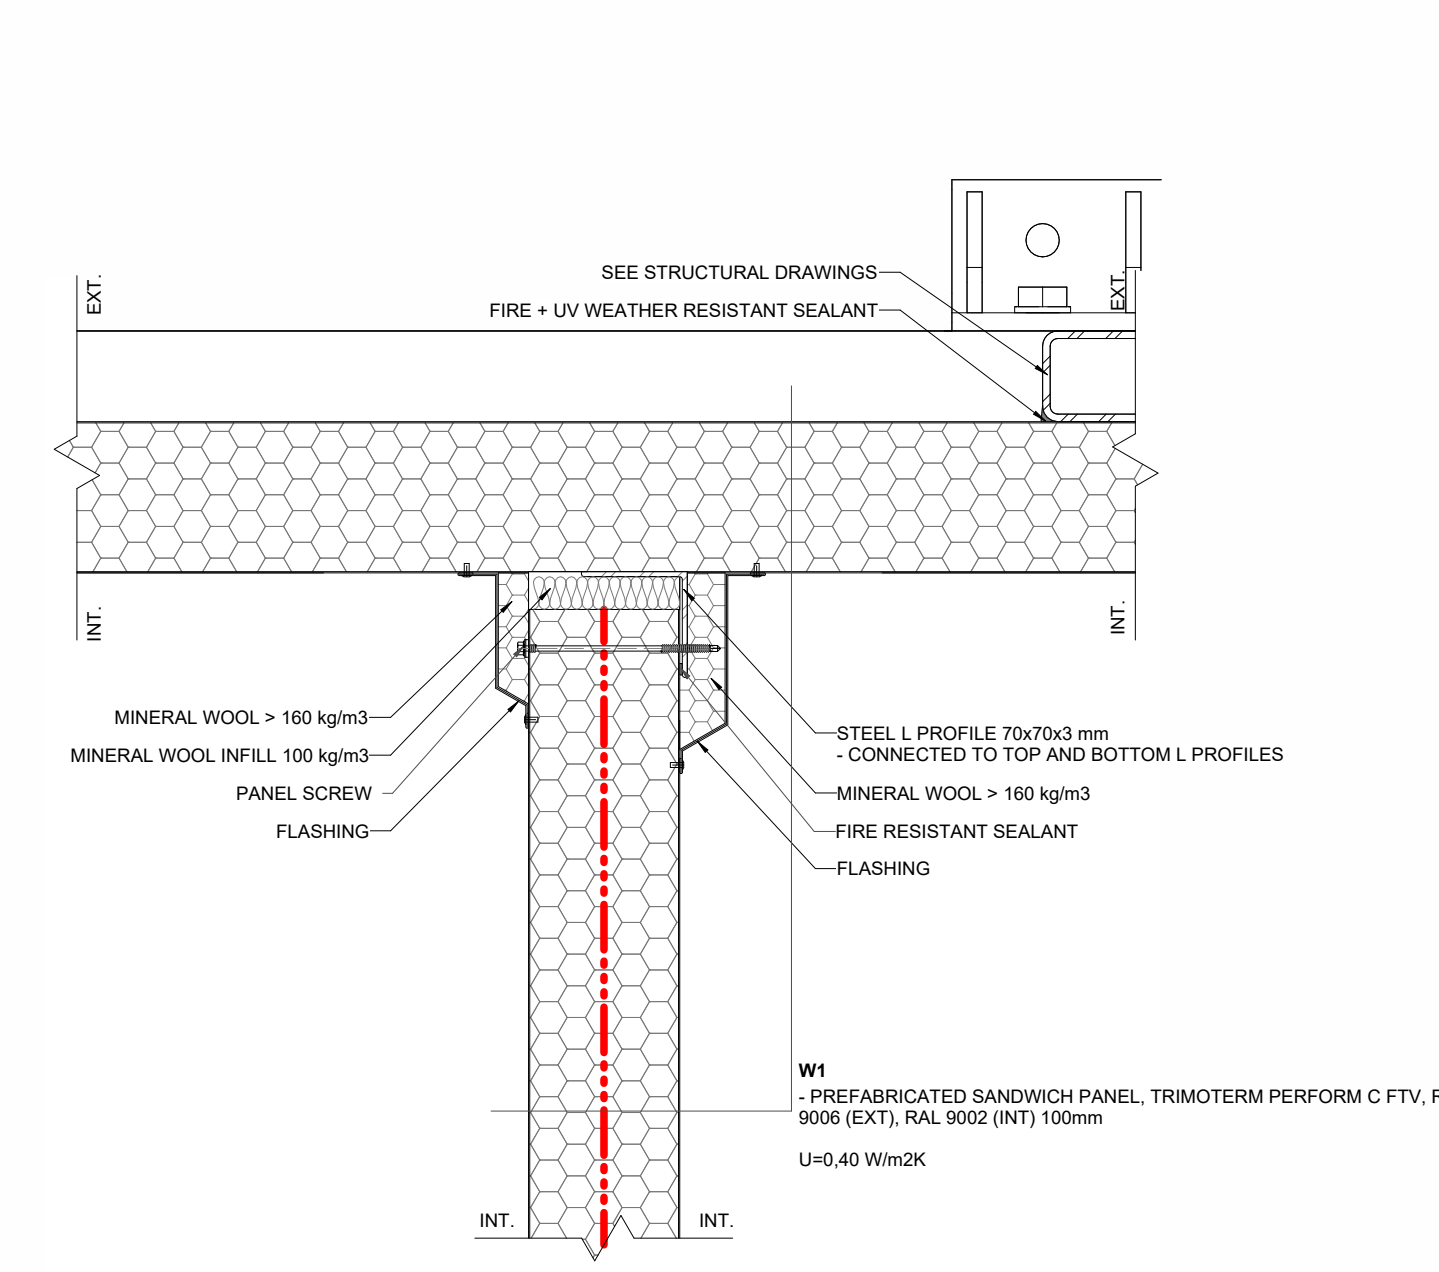


H03 MV - INT./EXT. WALL CONNECTION
1:5

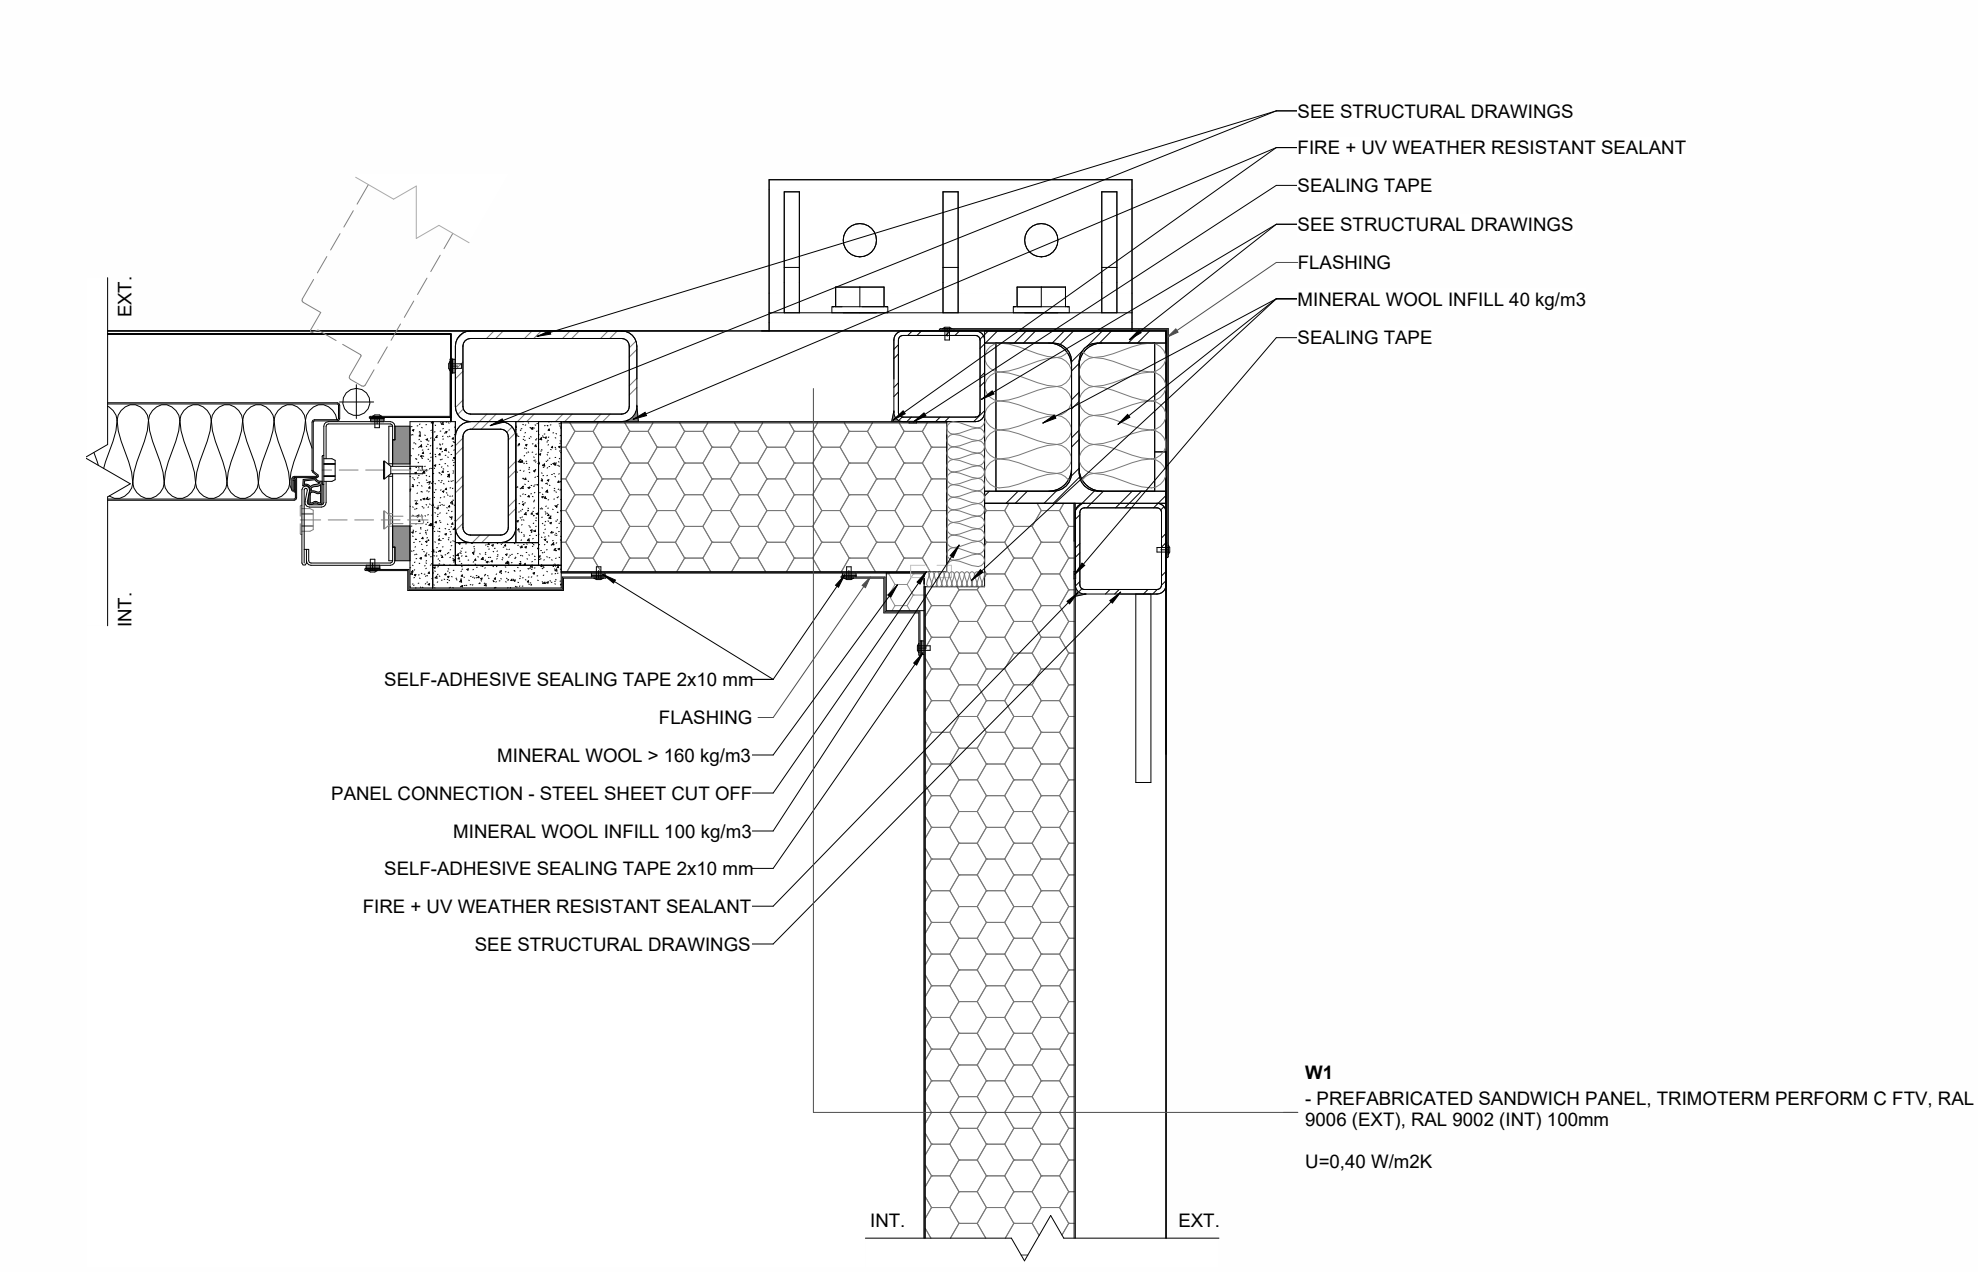


H04 MV - MODULE CORNER
1:5

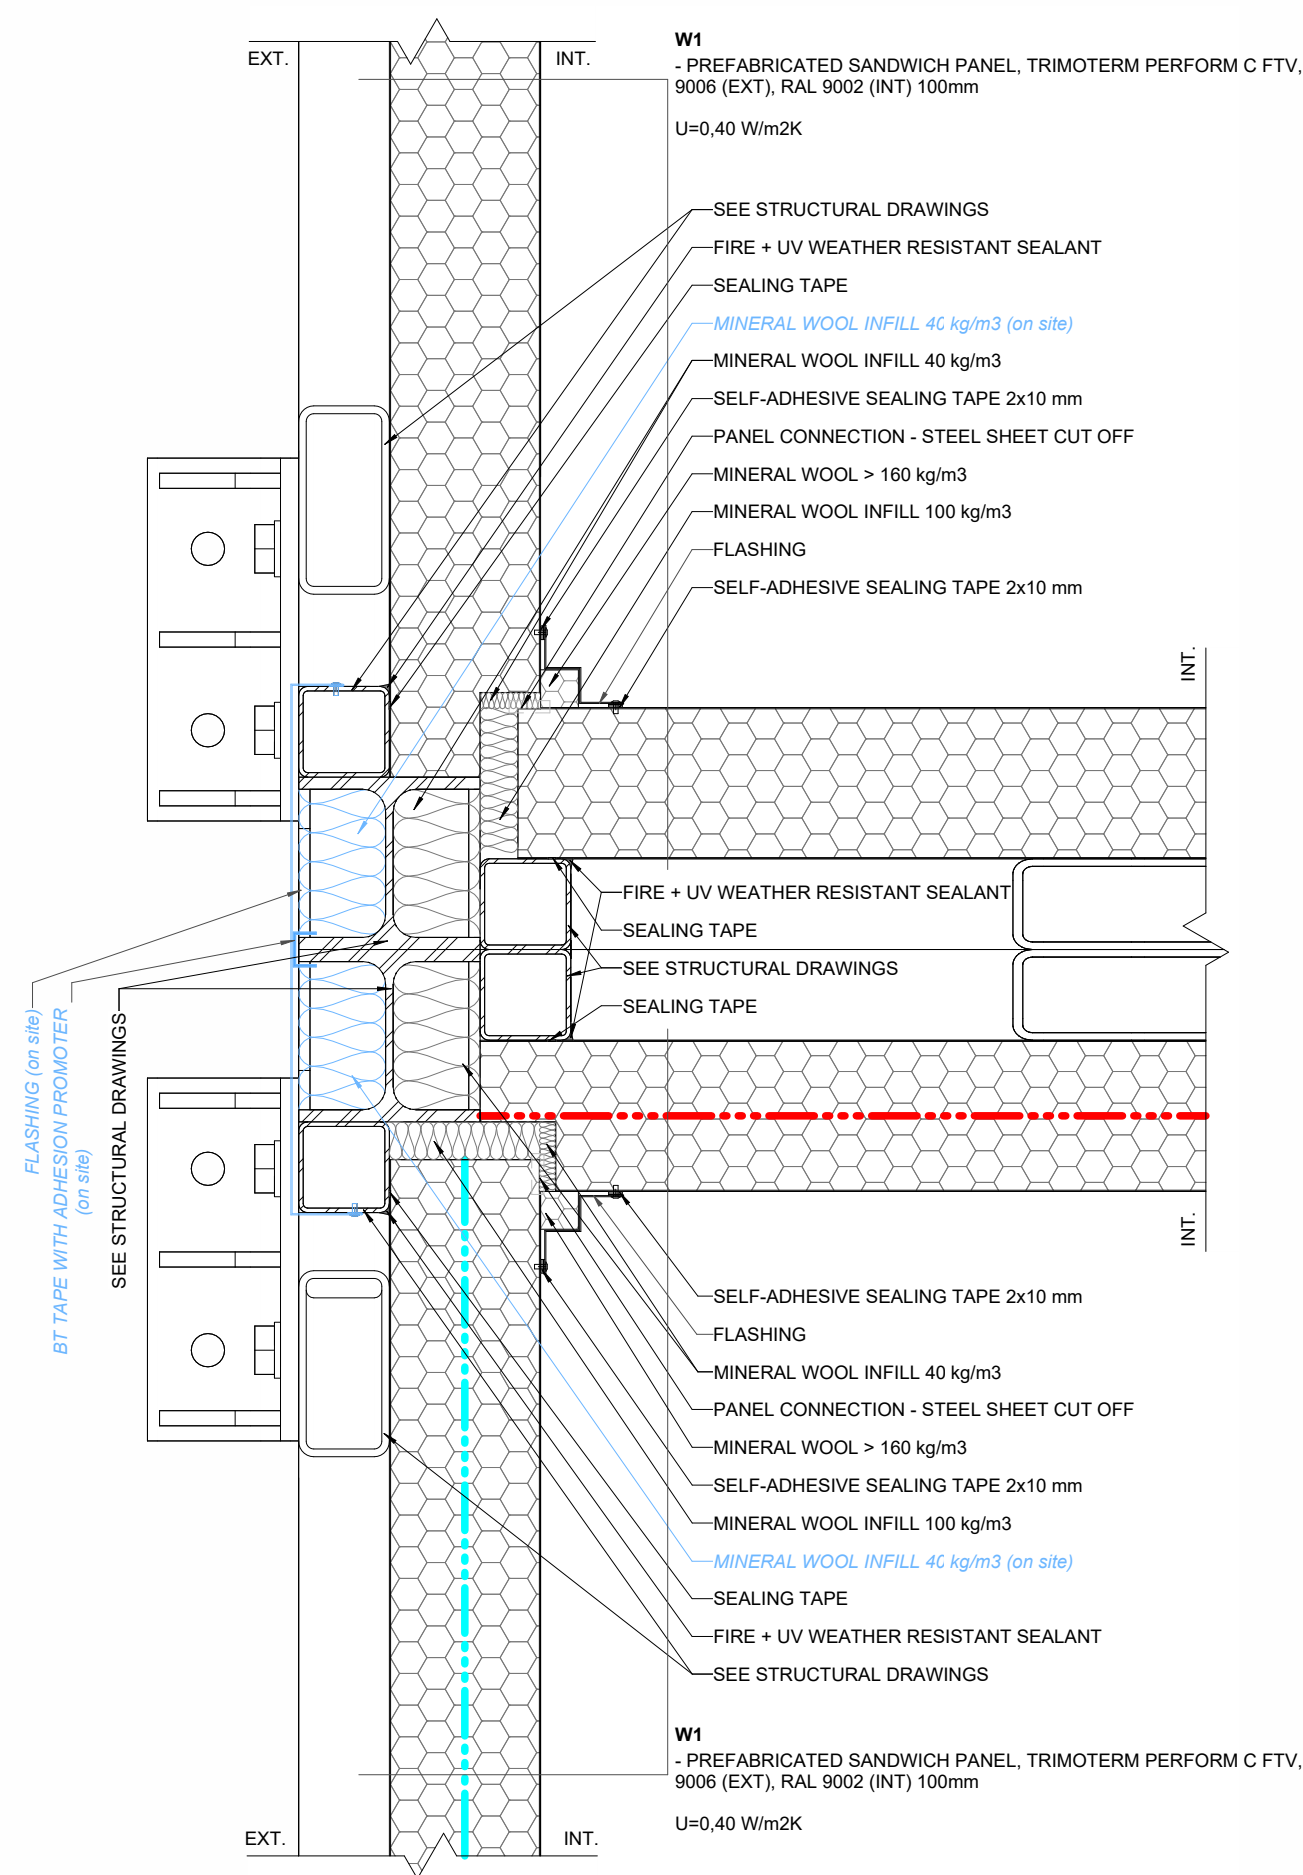


H05 PM/MV - MODULE CONNECTION
1:5

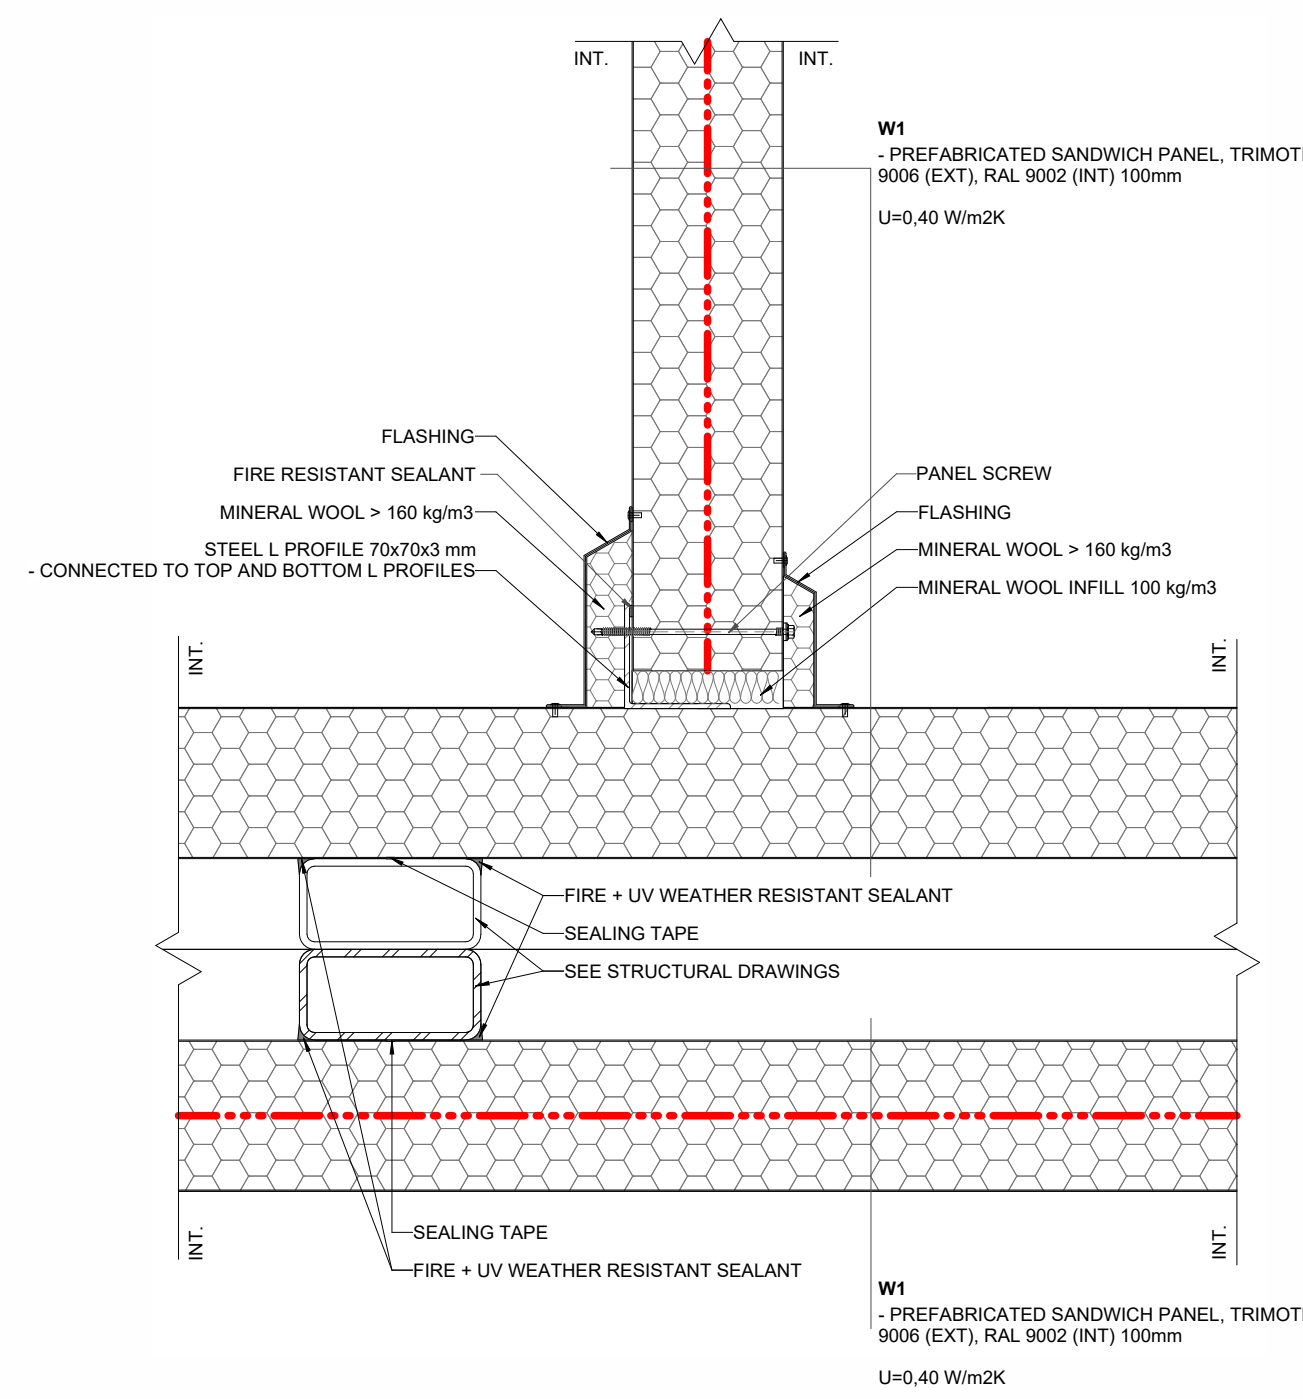


H06 MV - INT./EXT. WALL CONNECTION
1:5

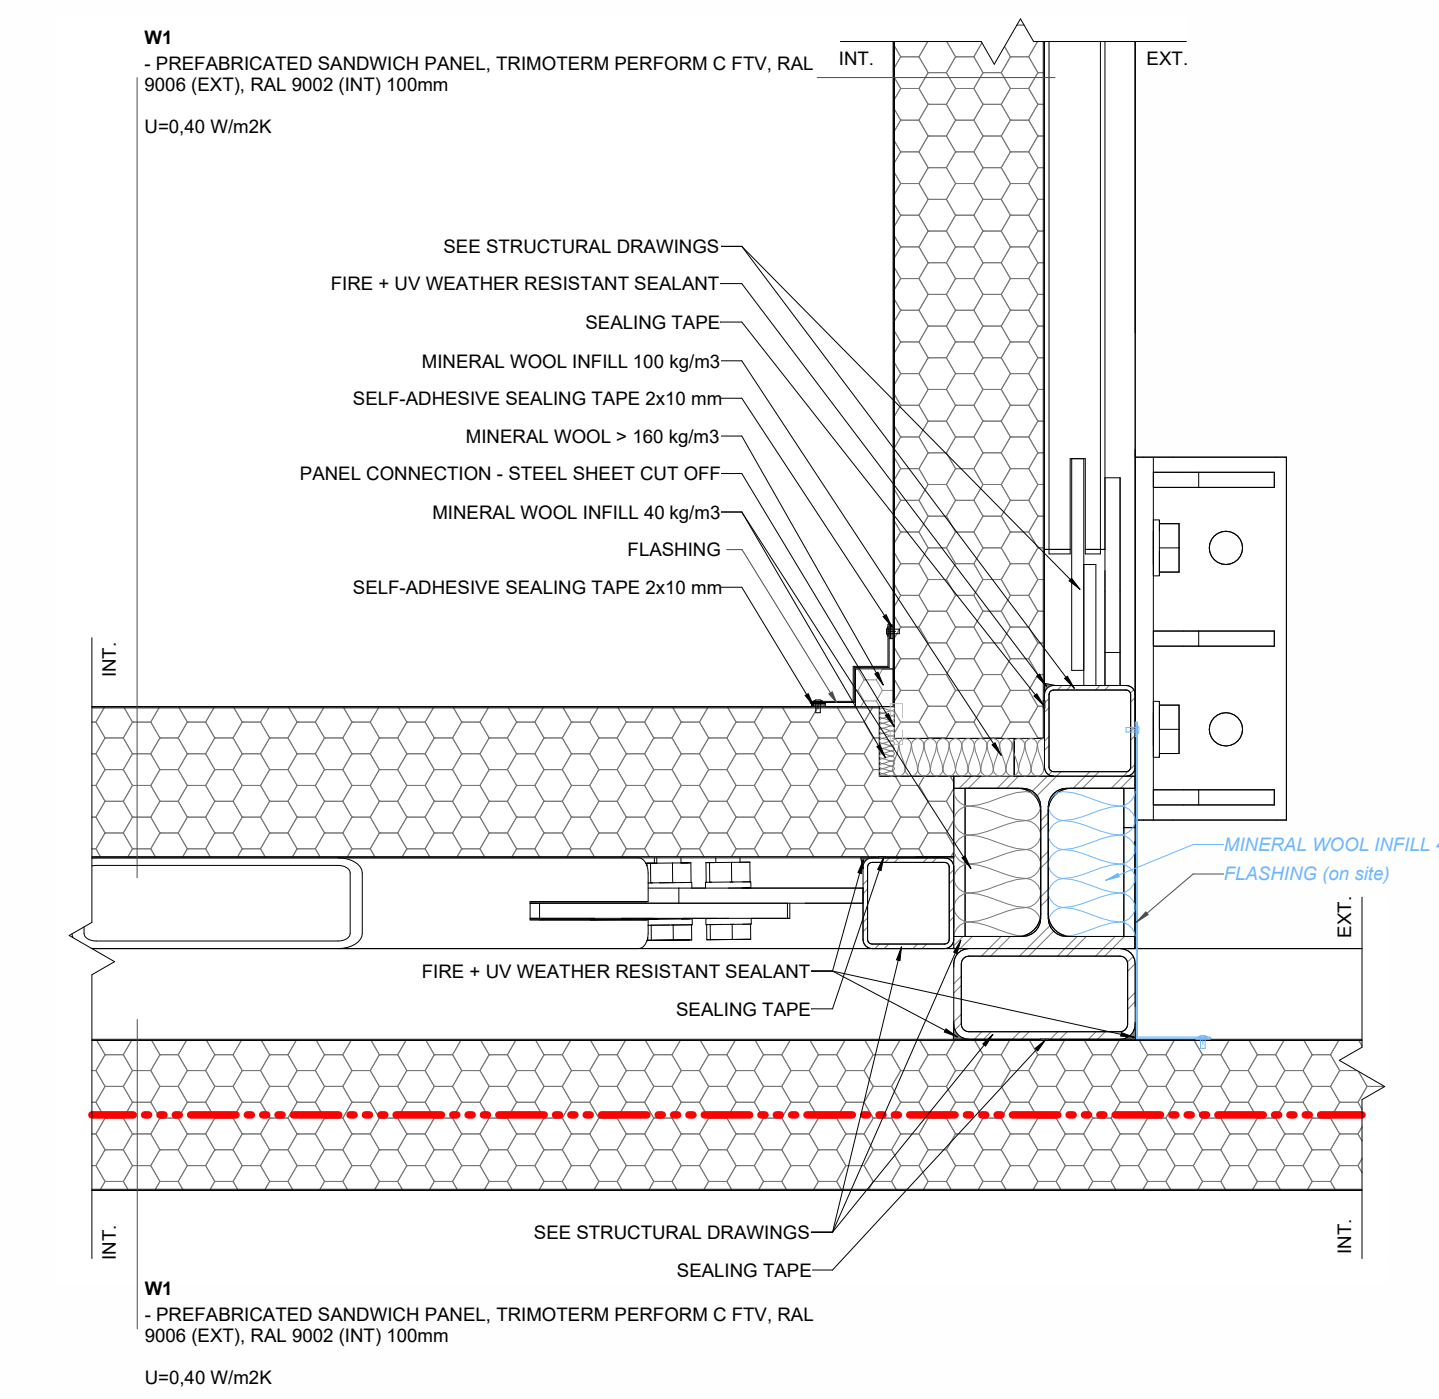


H07 MV - MODULE CORNER, PM MODULE CONNECTION
1:5

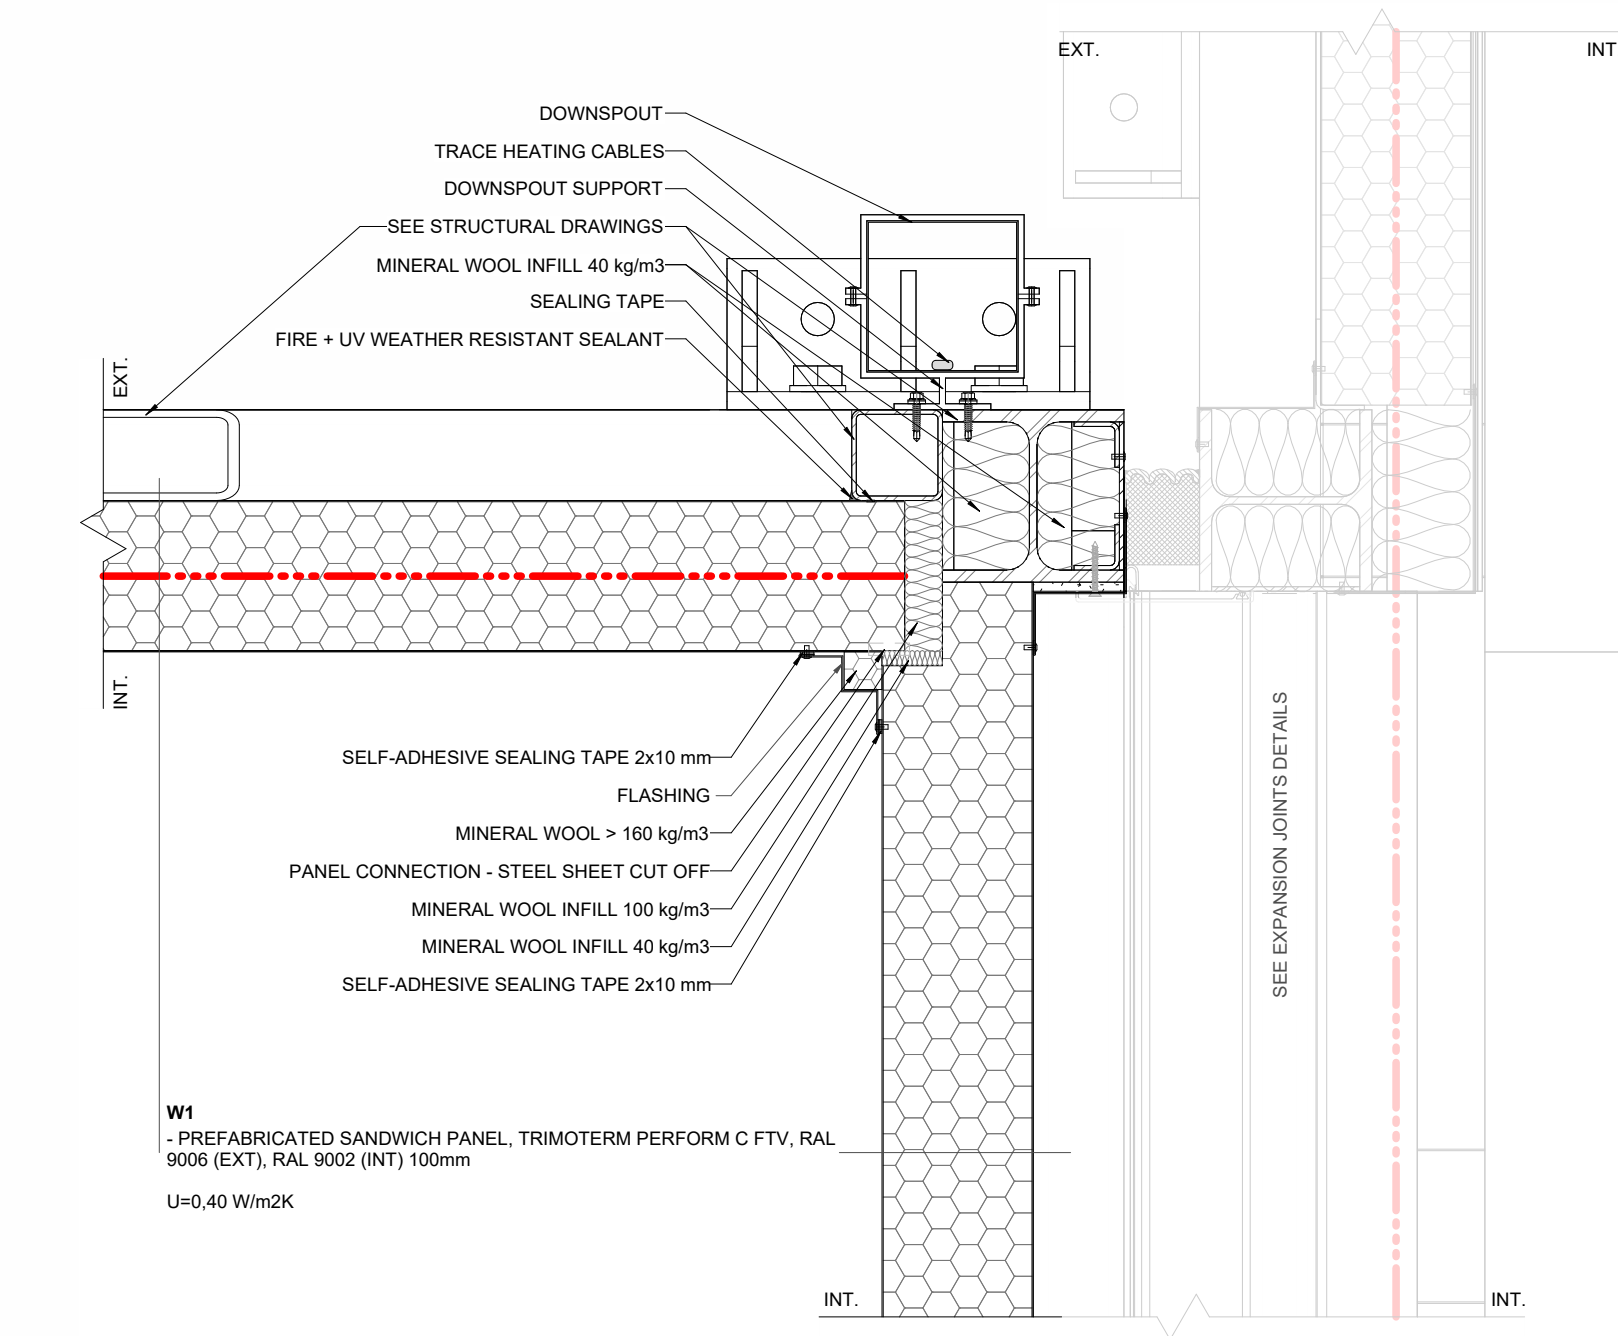


H08 PM - MODULE CORNER, RPP MODULE CONNECTION
1:5

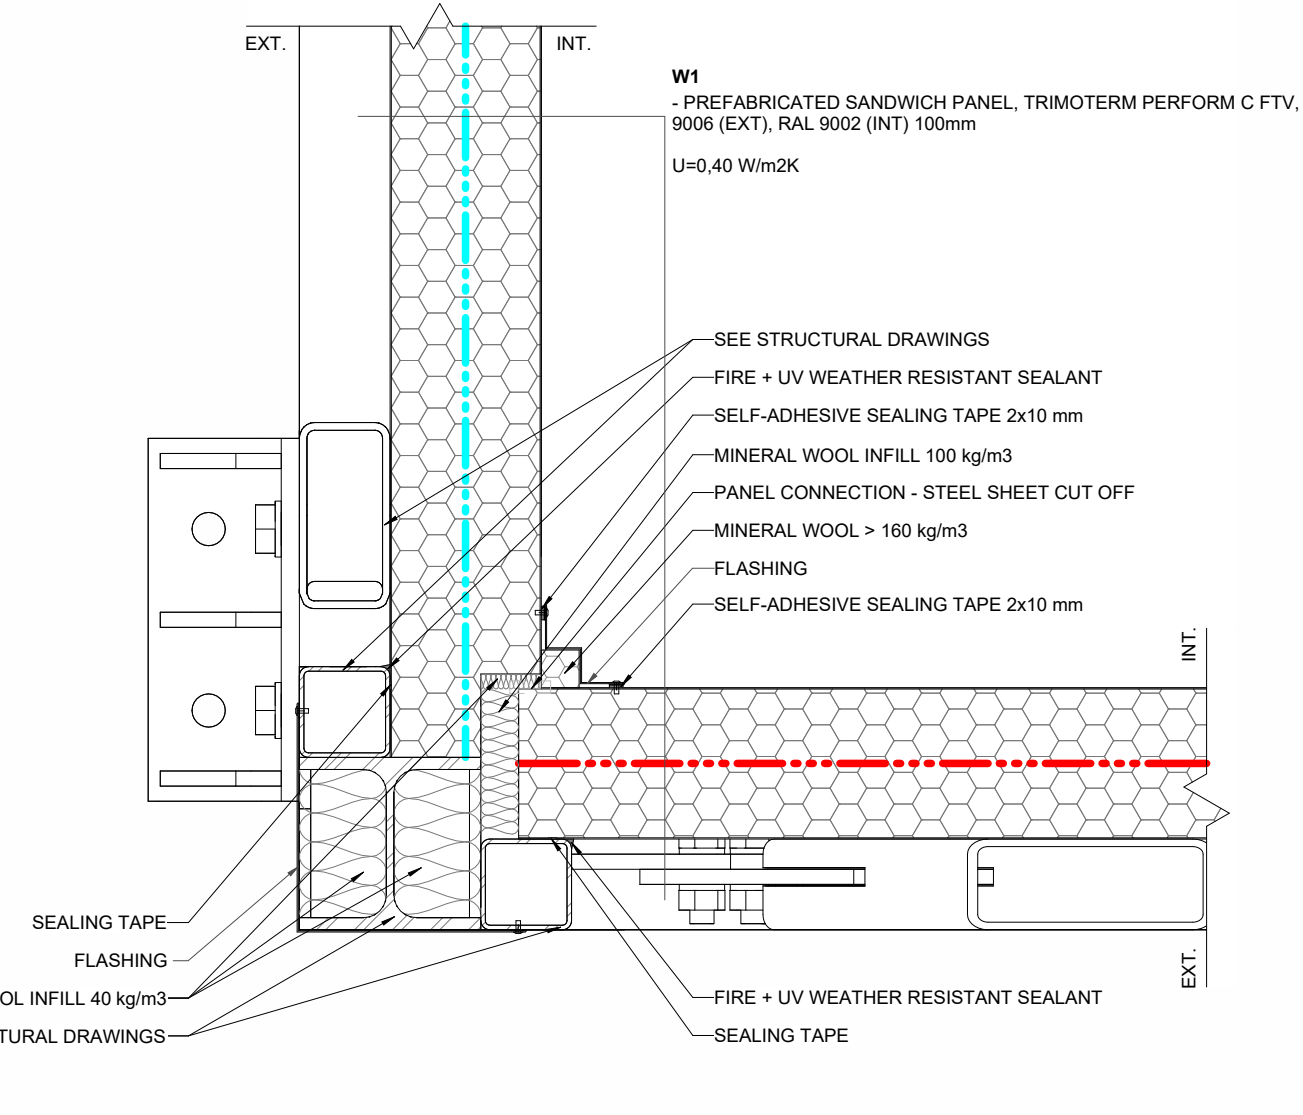

H09 PM/MS - MODULE CORNER
1:5

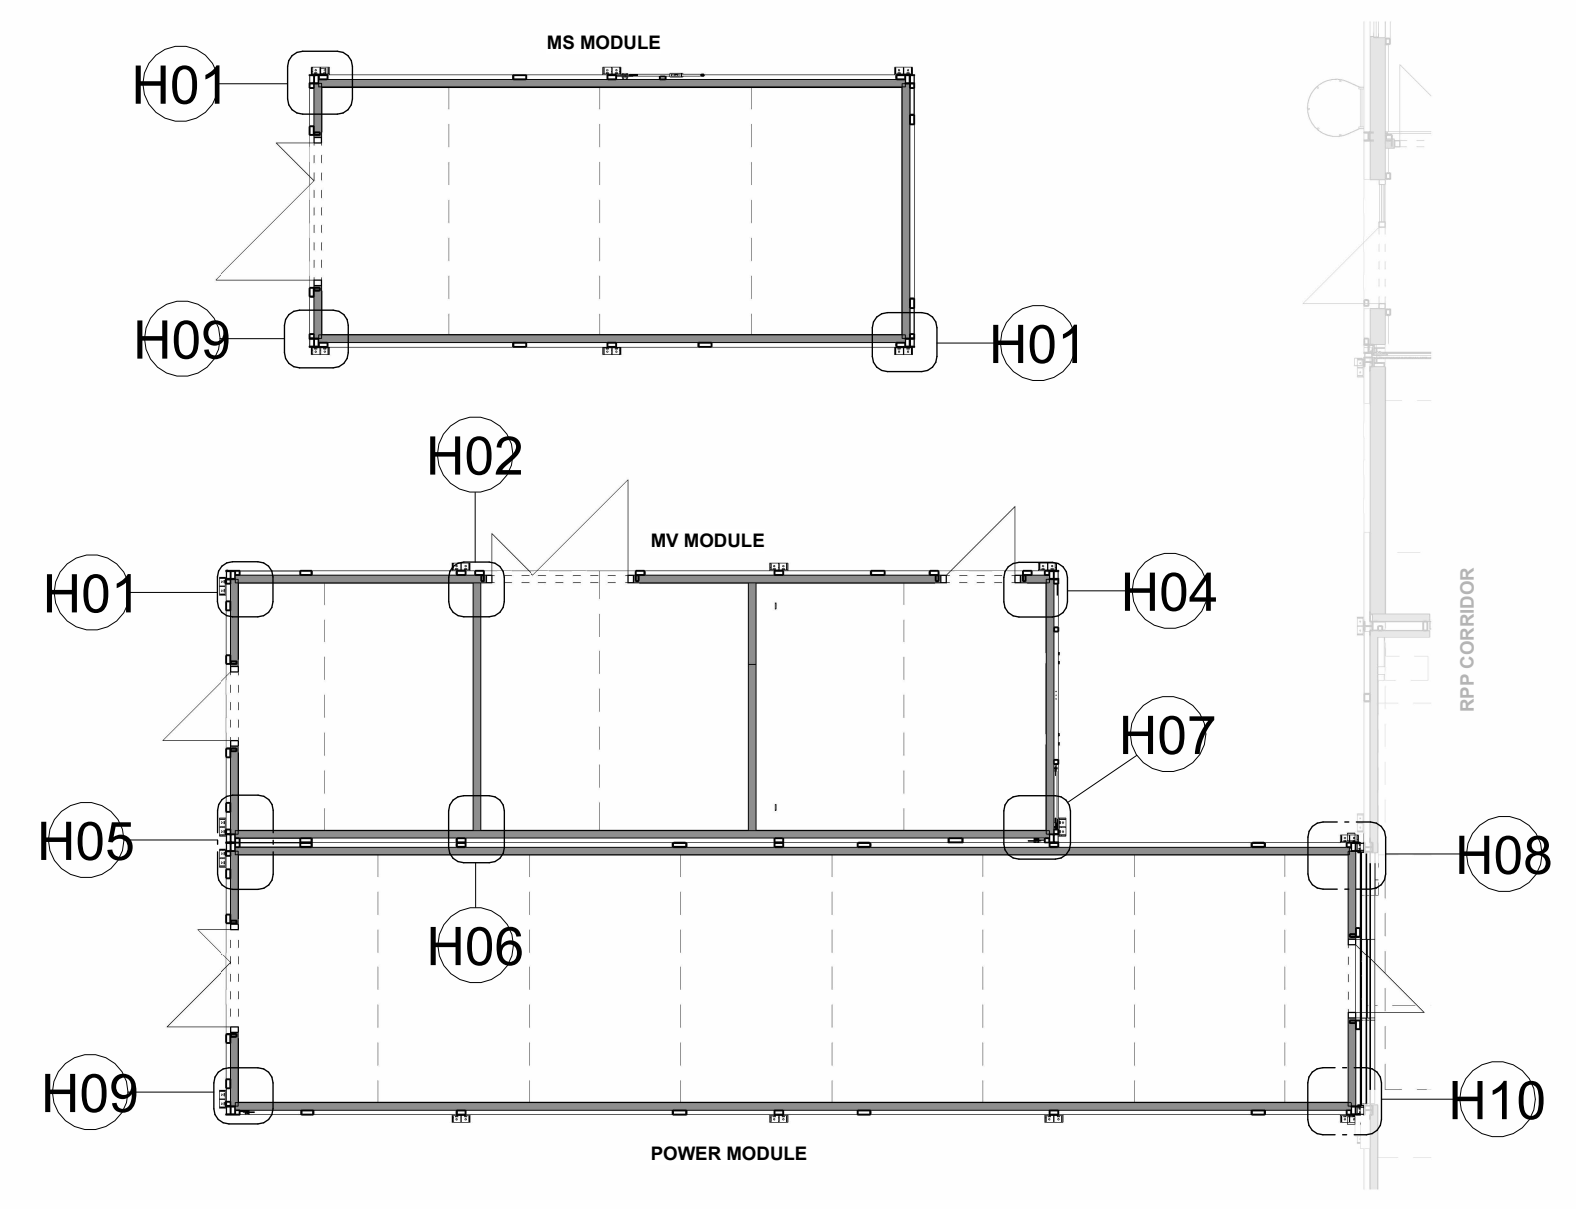

KEY PLAN - PM/MV/MS MODULE DETAIL POSITIONS - HORIZONTAL VIEWS

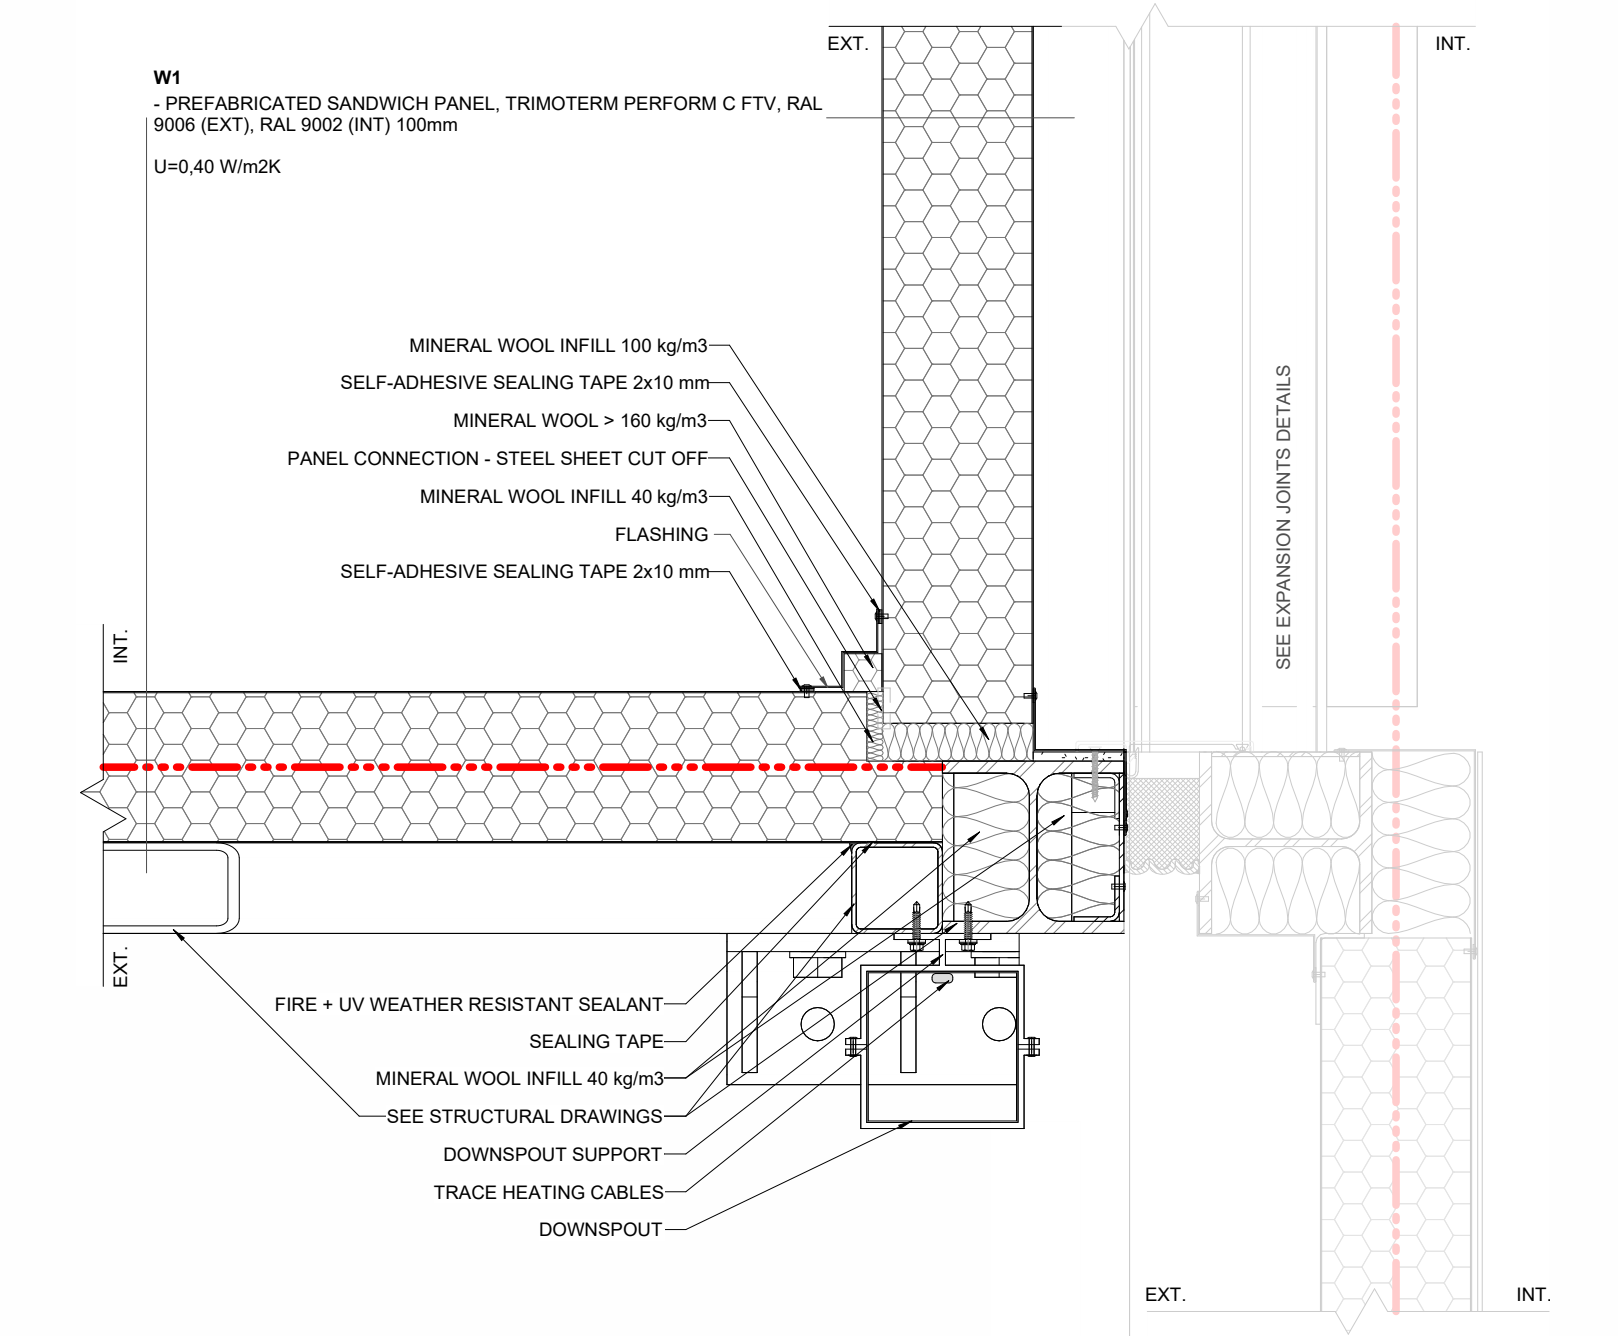


H10 PM - MODULE CORNER, RPP MODULE CONNECTION
1:5

KEYNOTES

---	---	---
---	---	---
---	---	---

LEGEND:

---	---	---
---	---	---
---	---	---

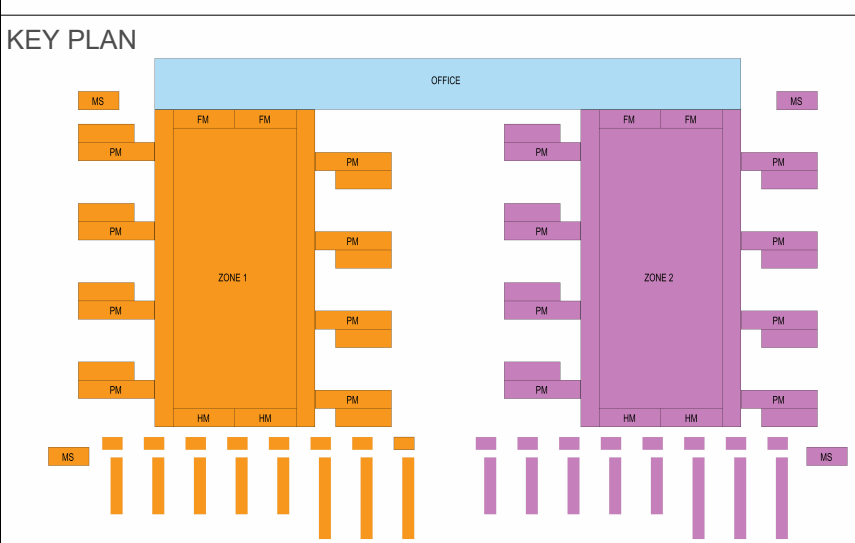

R01 CD SET - FOR INFORMATION 2026-07-24

REV.	DESCRIPTION	DATE
------	-------------	------



PROJECT NAME
ECO DC MONALISA

DRAWING NAME
**ARCHITECTURAL DETAILS
- PREFABRICATED MODULES
- HORIZONTAL VIEWS - PM - MV - MS**

PREPARED (ALSO SUBJECT RESPONSIBLE IF OTHER)
L. MAVREK / K. KOZINA
DOCUMENT RESPONSIBLE (APPROVED)
M. PACAK
CAD / BIM SYSTEM
AUTODESK REVIT 2025

DOCUMENT NUMBER ECODC-VRT-MDC19-00-DR-A-50101	SHEET SIZE A0	DRAWING SCALE 1:5	DATE (YYYYMMDD) 2026-07-24	SHEET 1 OF 1 R01
---	-------------------------	-----------------------------	--------------------------------------	----------------------------