



LEGAL DISCLAIMER: THIS DOCUMENT AND THE CONTENTS HEREIN ARE CONFIDENTIAL AND THE SOLE PROPERTY OF VERTIV GROUP CORP. REPRODUCTION, DISTRIBUTION OR UNAUTHORIZED USE OF THIS DOCUMENT OR ANY PARTS WITHIN THIS DOCUMENT ARE FORBIDDEN WITHOUT THE WRITTEN CONSENT OF VERTIV GROUP CORP.

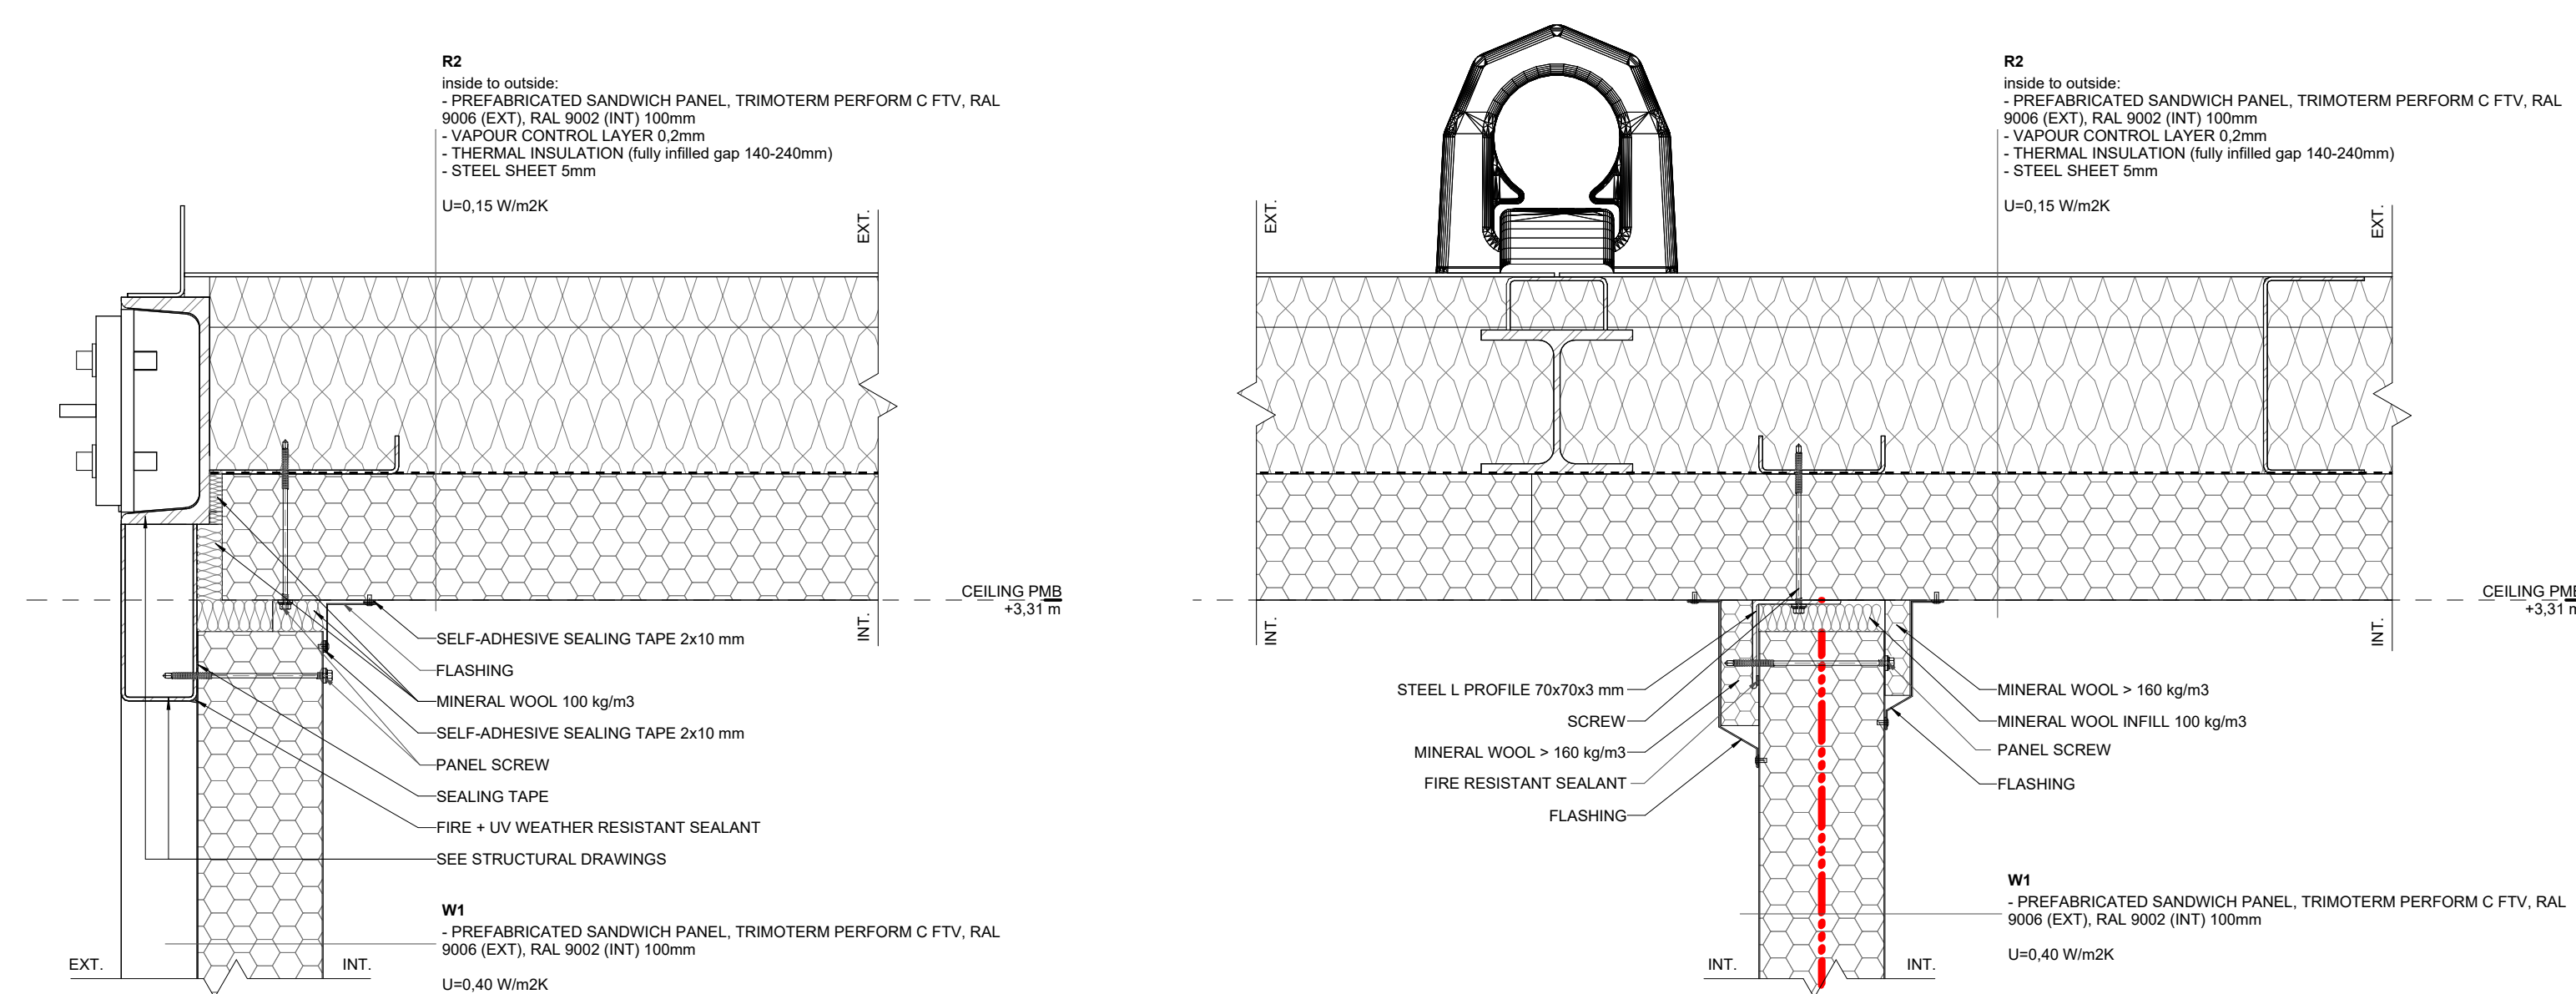


V01 PM/MV/MS - EXT. WALL/ROOF CONNECTION
1:5


V03 MV - INT. WALL/ROOF CONNECTION
1:5

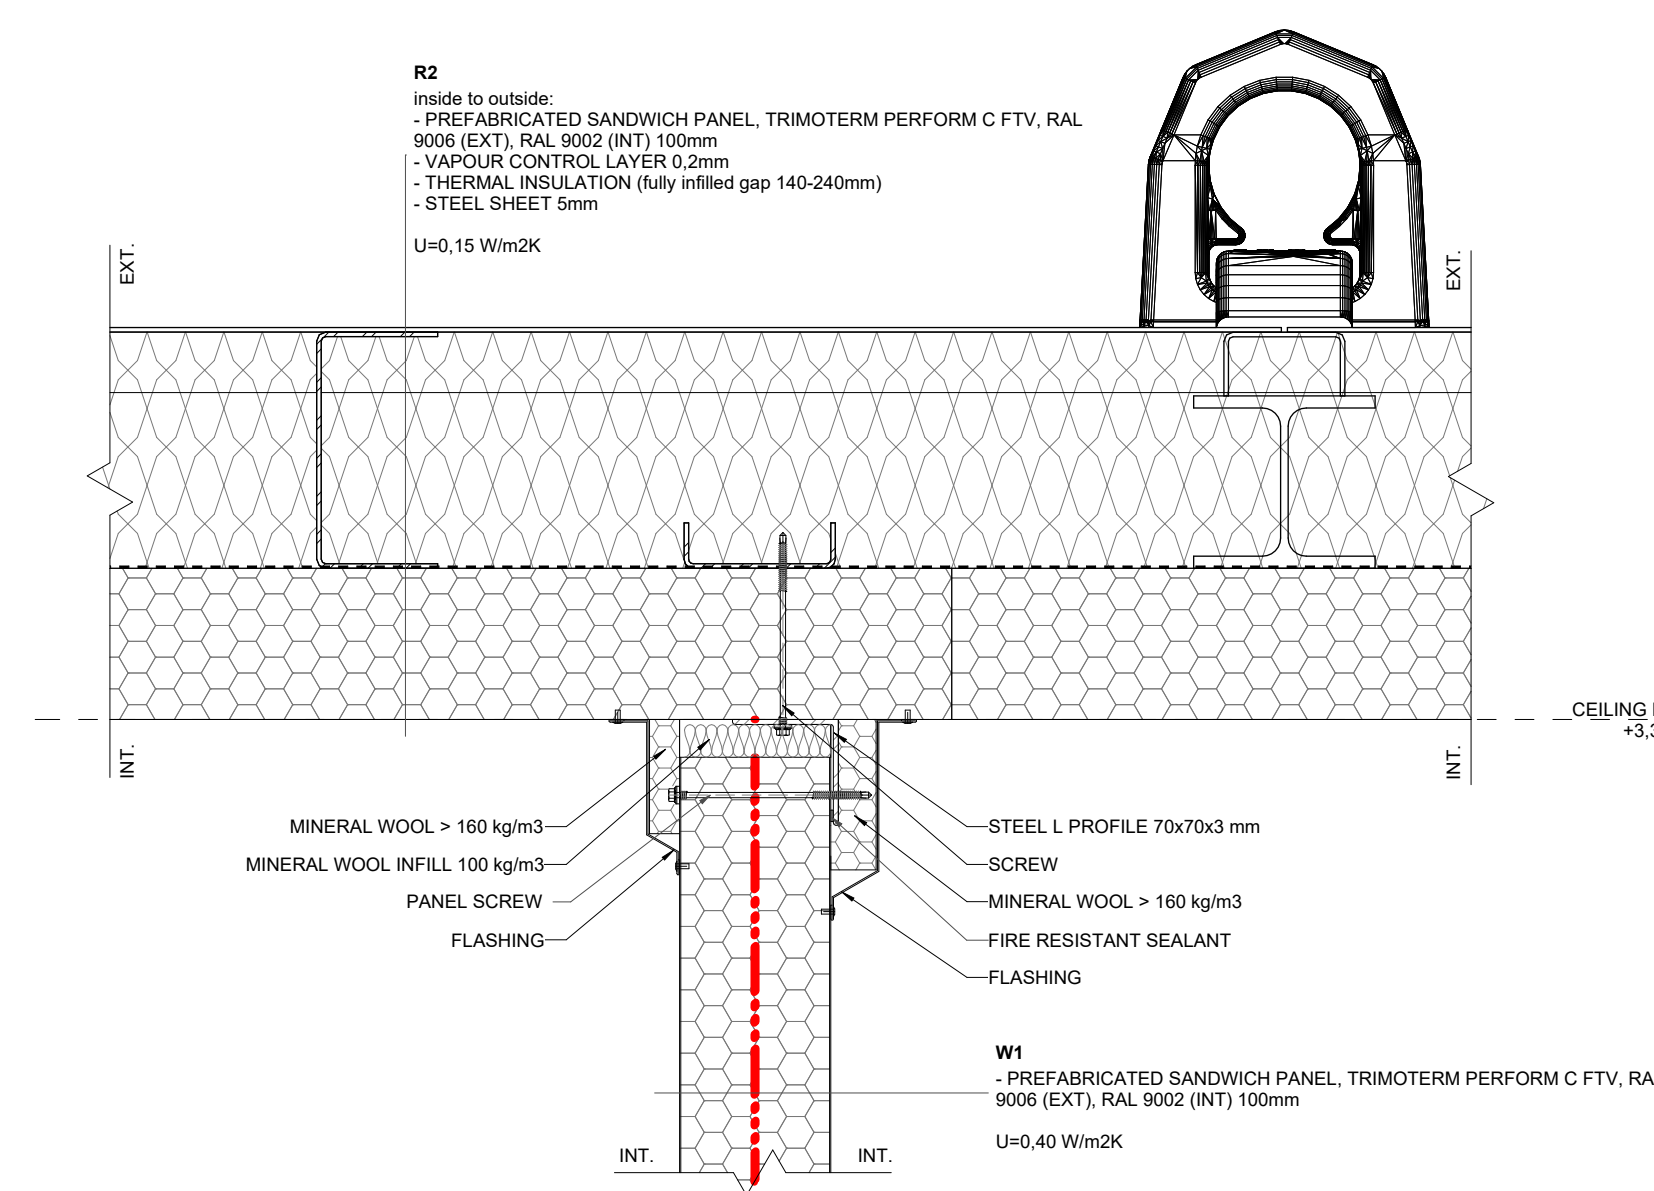


V05 MV - INT. WALL/ROOF CONNECTION
1:5

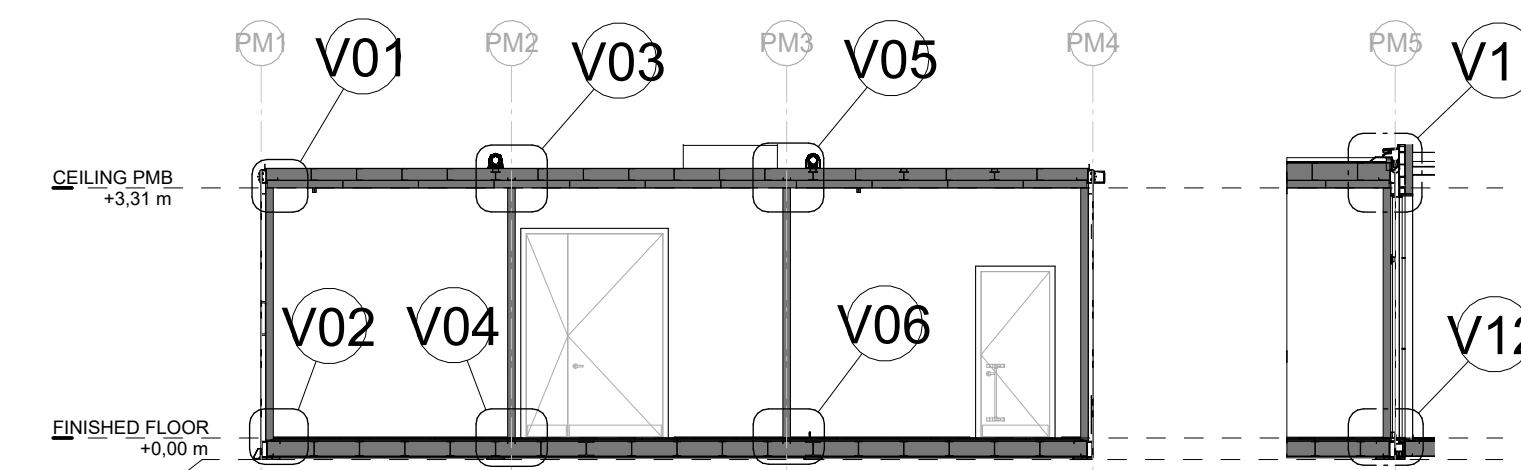


LONGITUDINAL SECTION
KEY PLAN - PM/MV/MS MODULE DETAIL POSITIONS - VERTICAL VIEWS

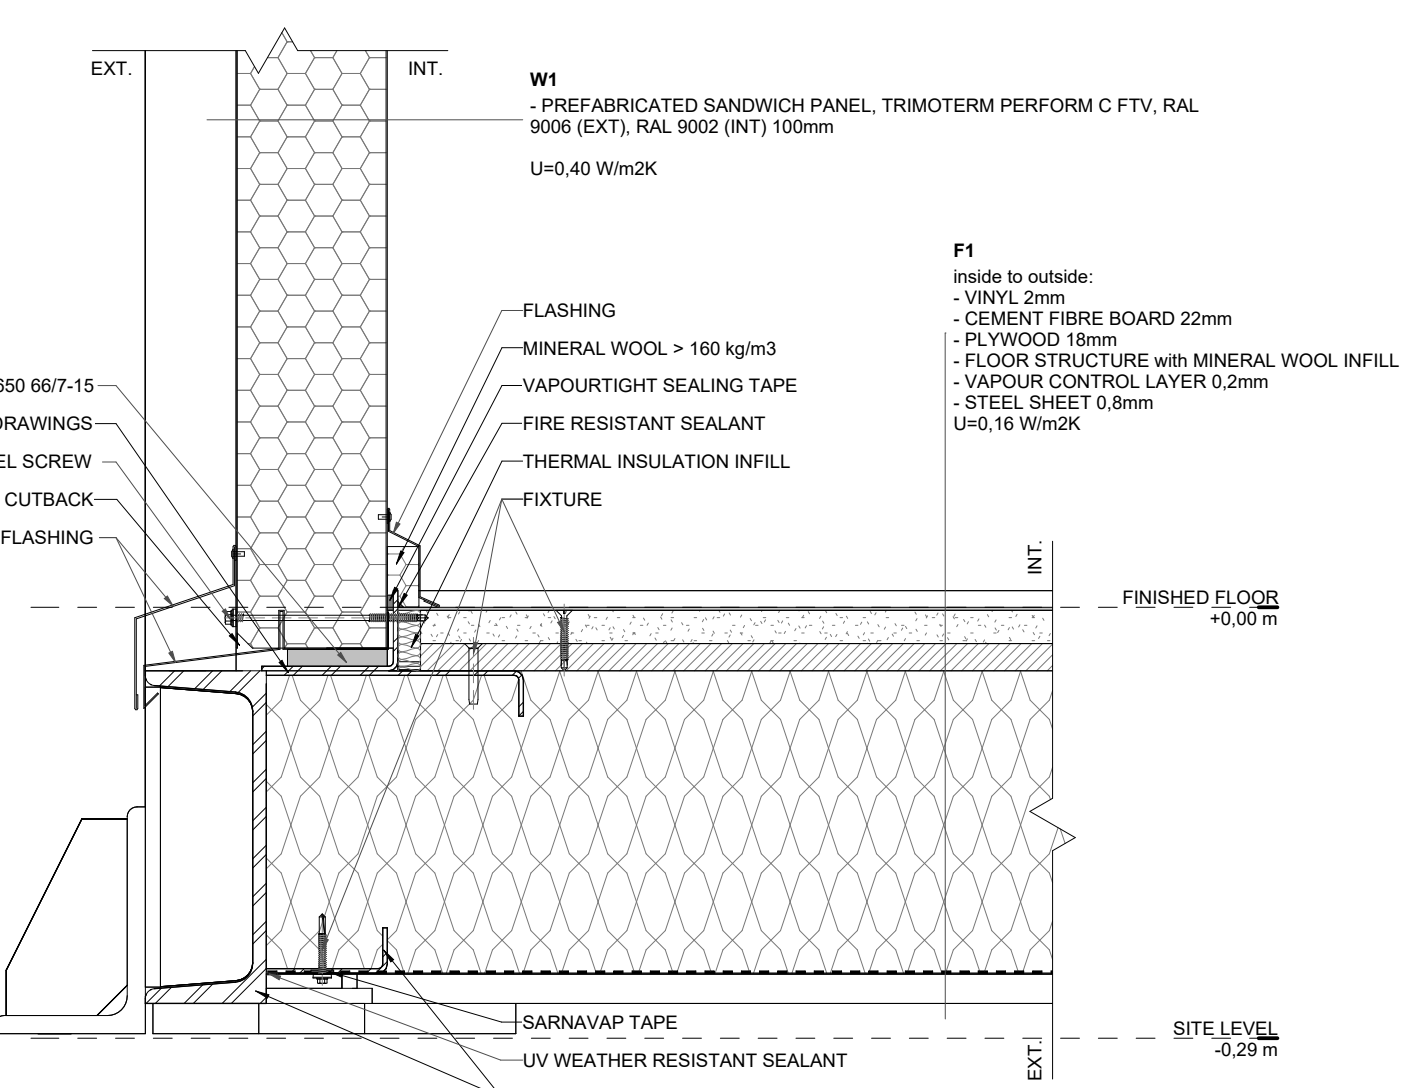


V02 PM/MV/MS - EXT. WALL/FLOOR CONNECTION
1:5

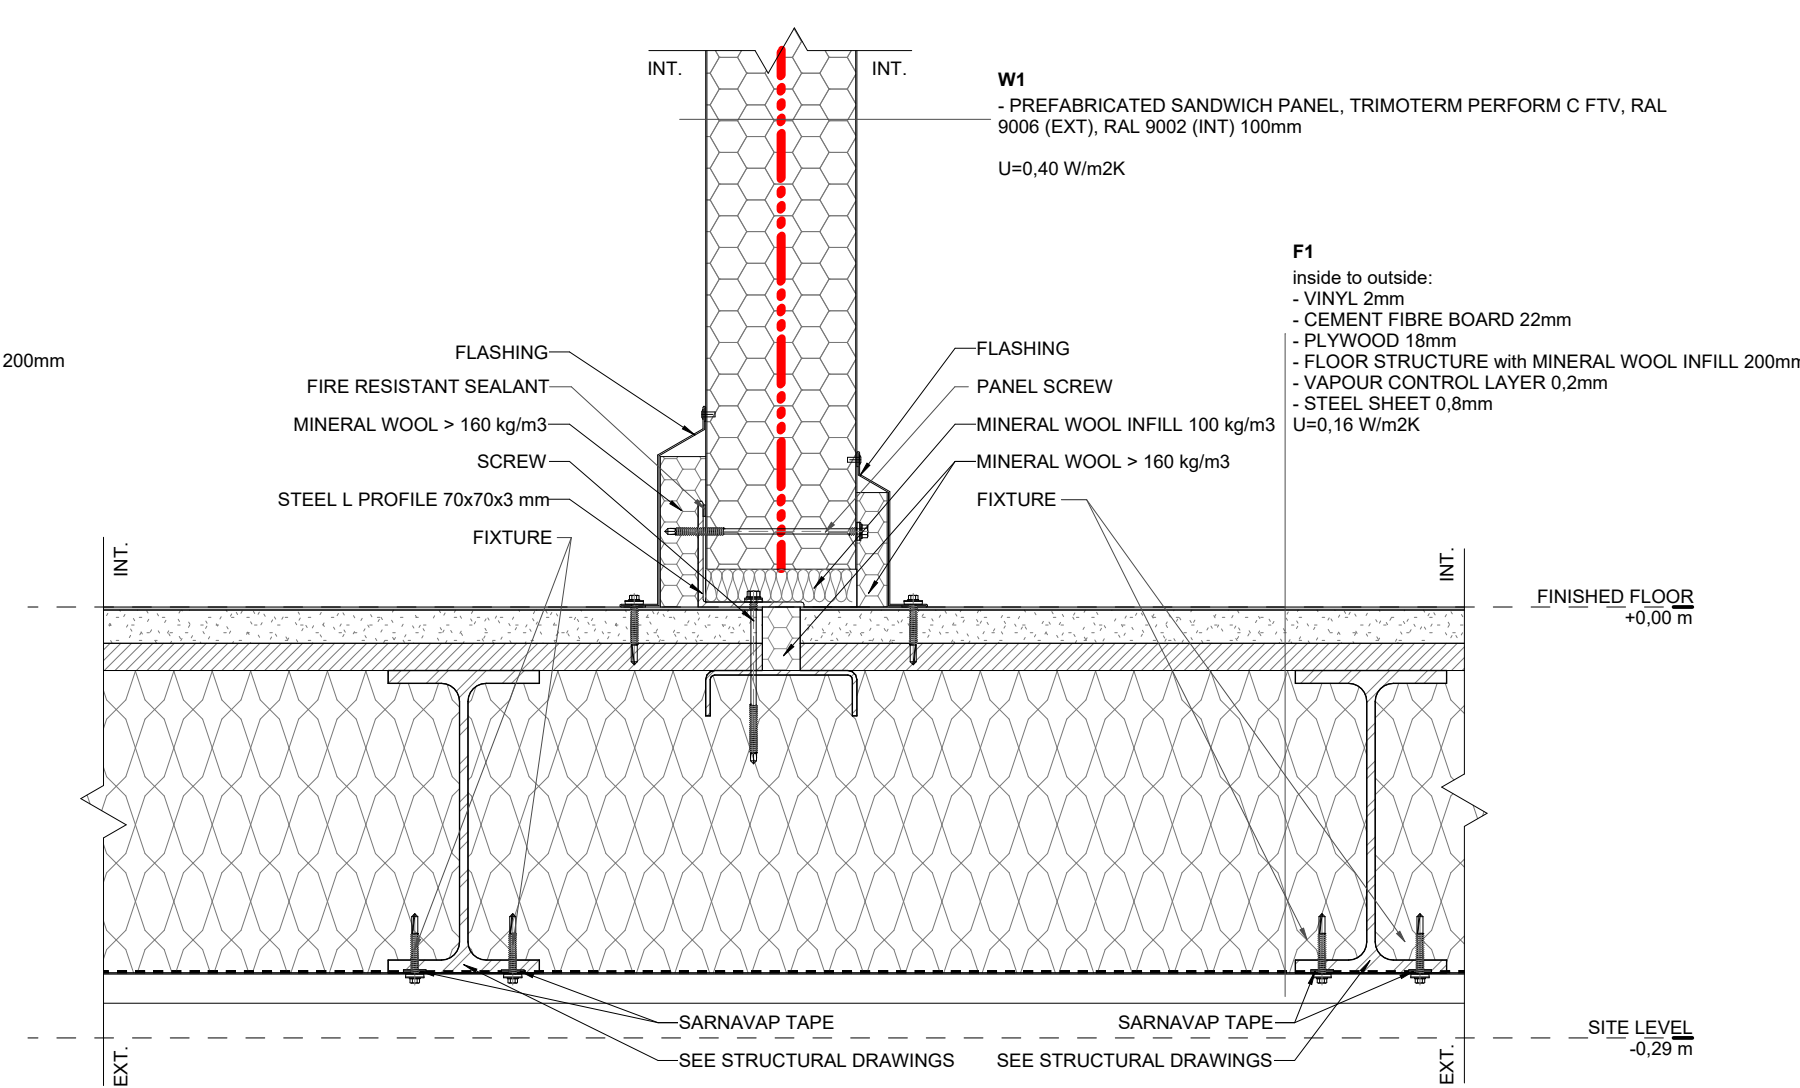

V04 MV - INT. WALL/FLOOR CONNECTION
1:5

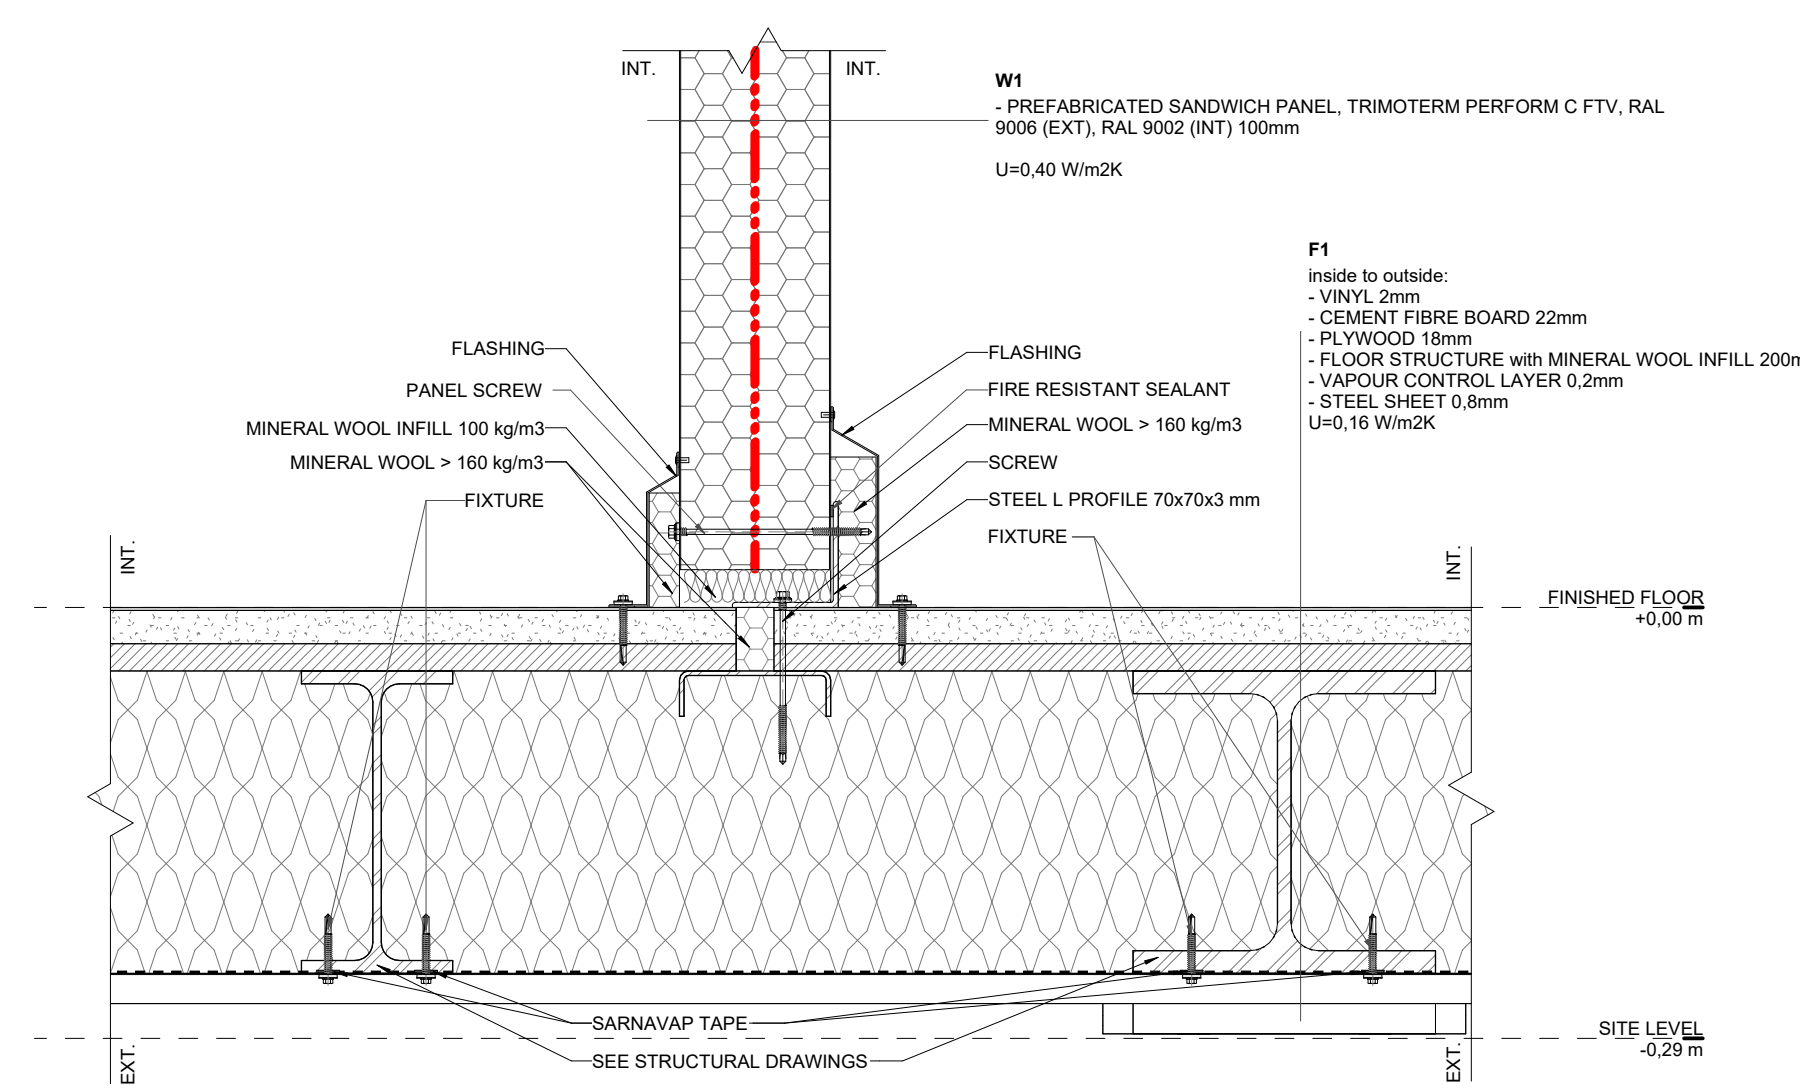


V06 MV - INT. WALL/FLOOR CONNECTION
1:5

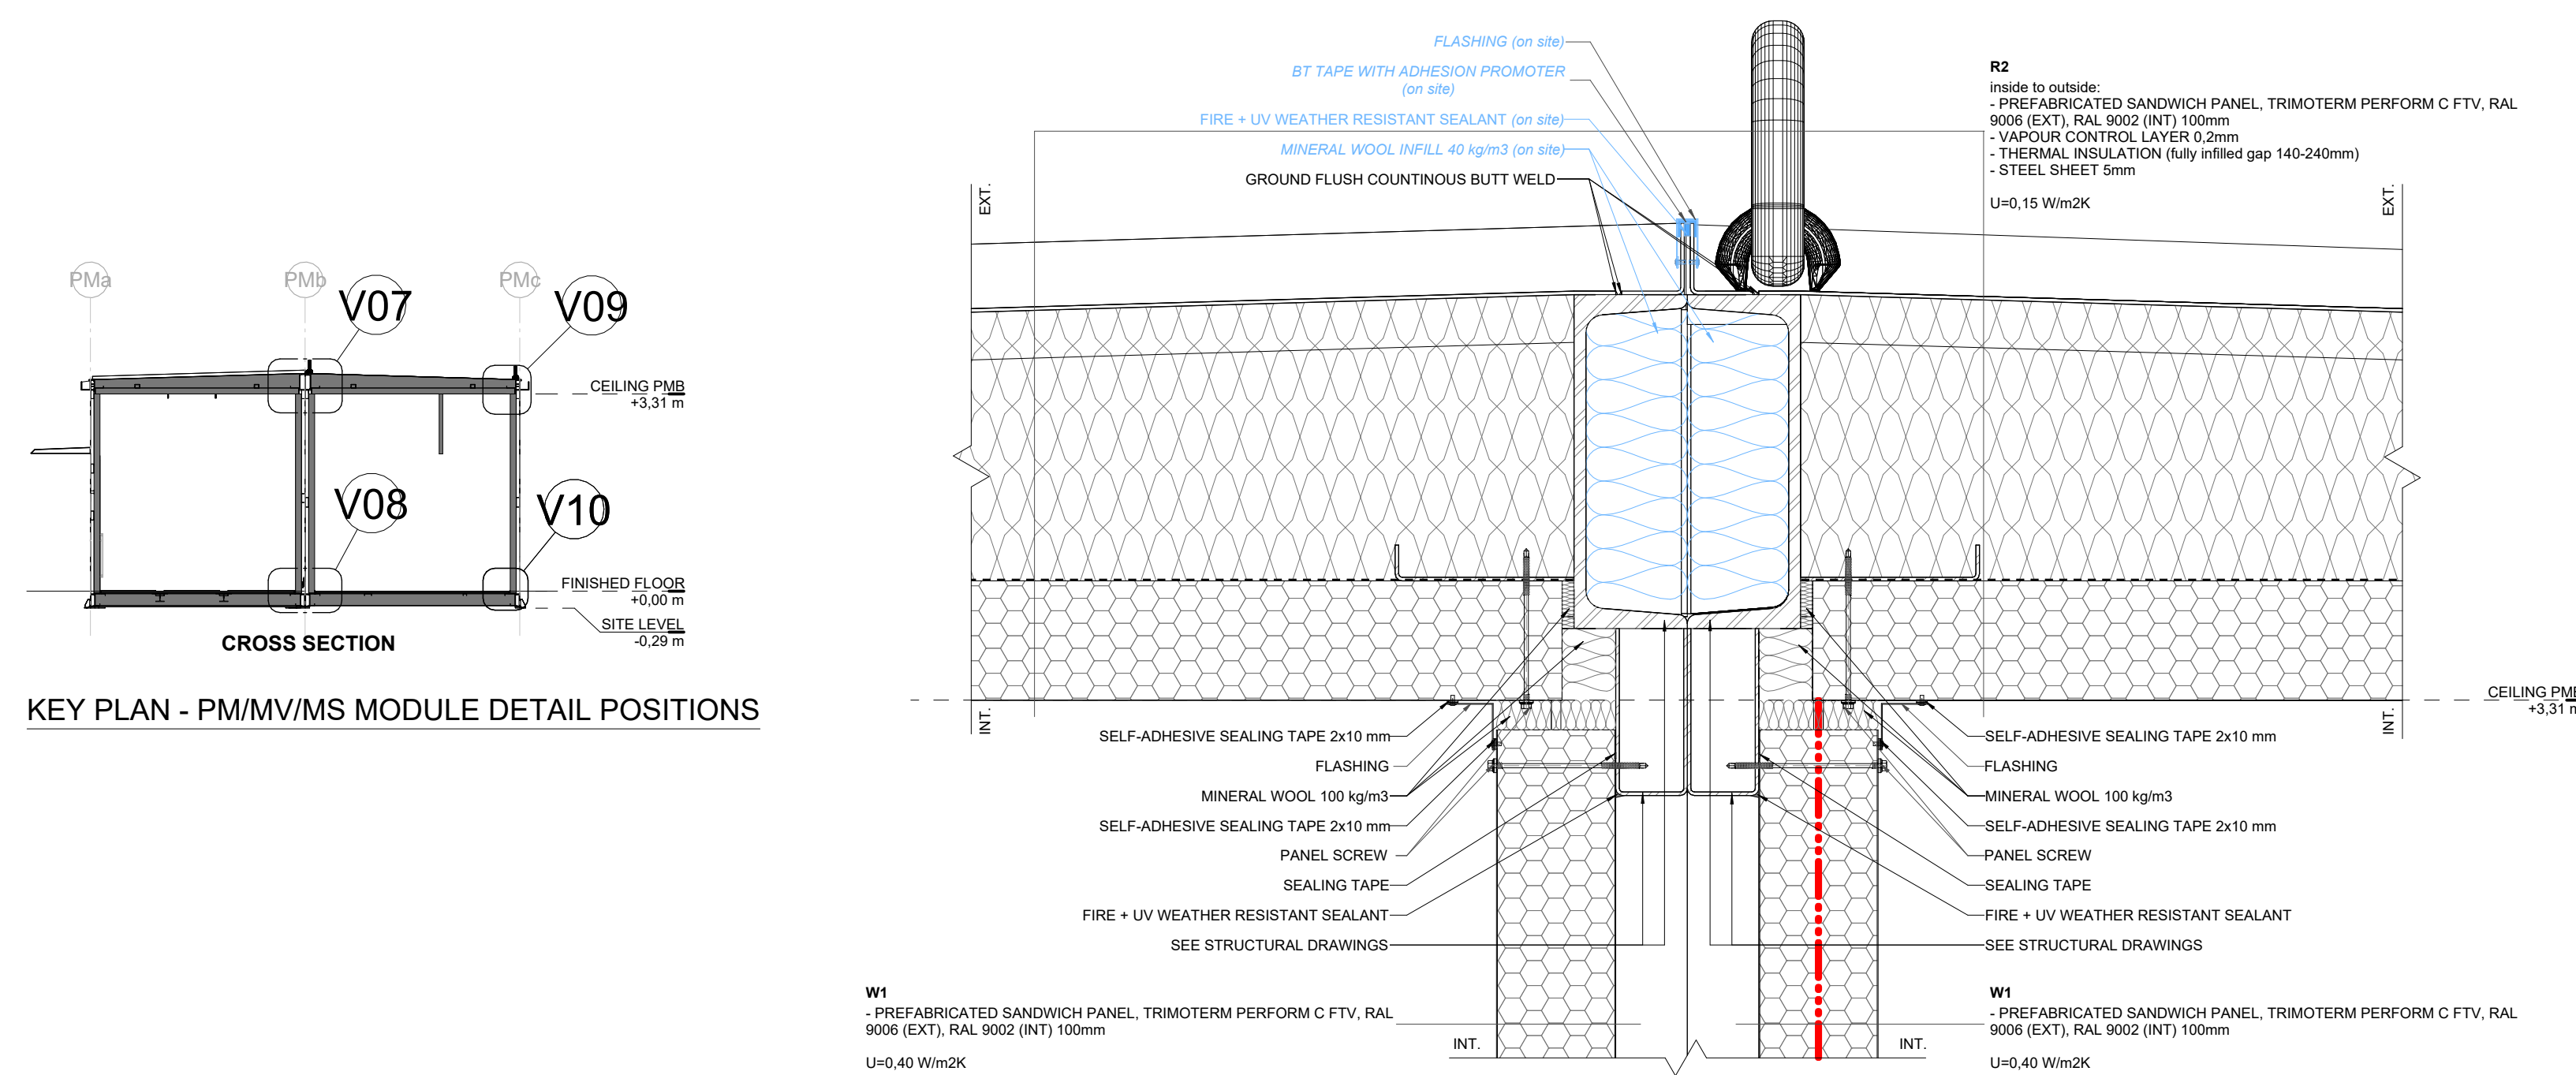


KEY PLAN - PM/MV/MS MODULE DETAIL POSITIONS


V07 PM/MV - MODULE CONNECTION-ROOF
1:5

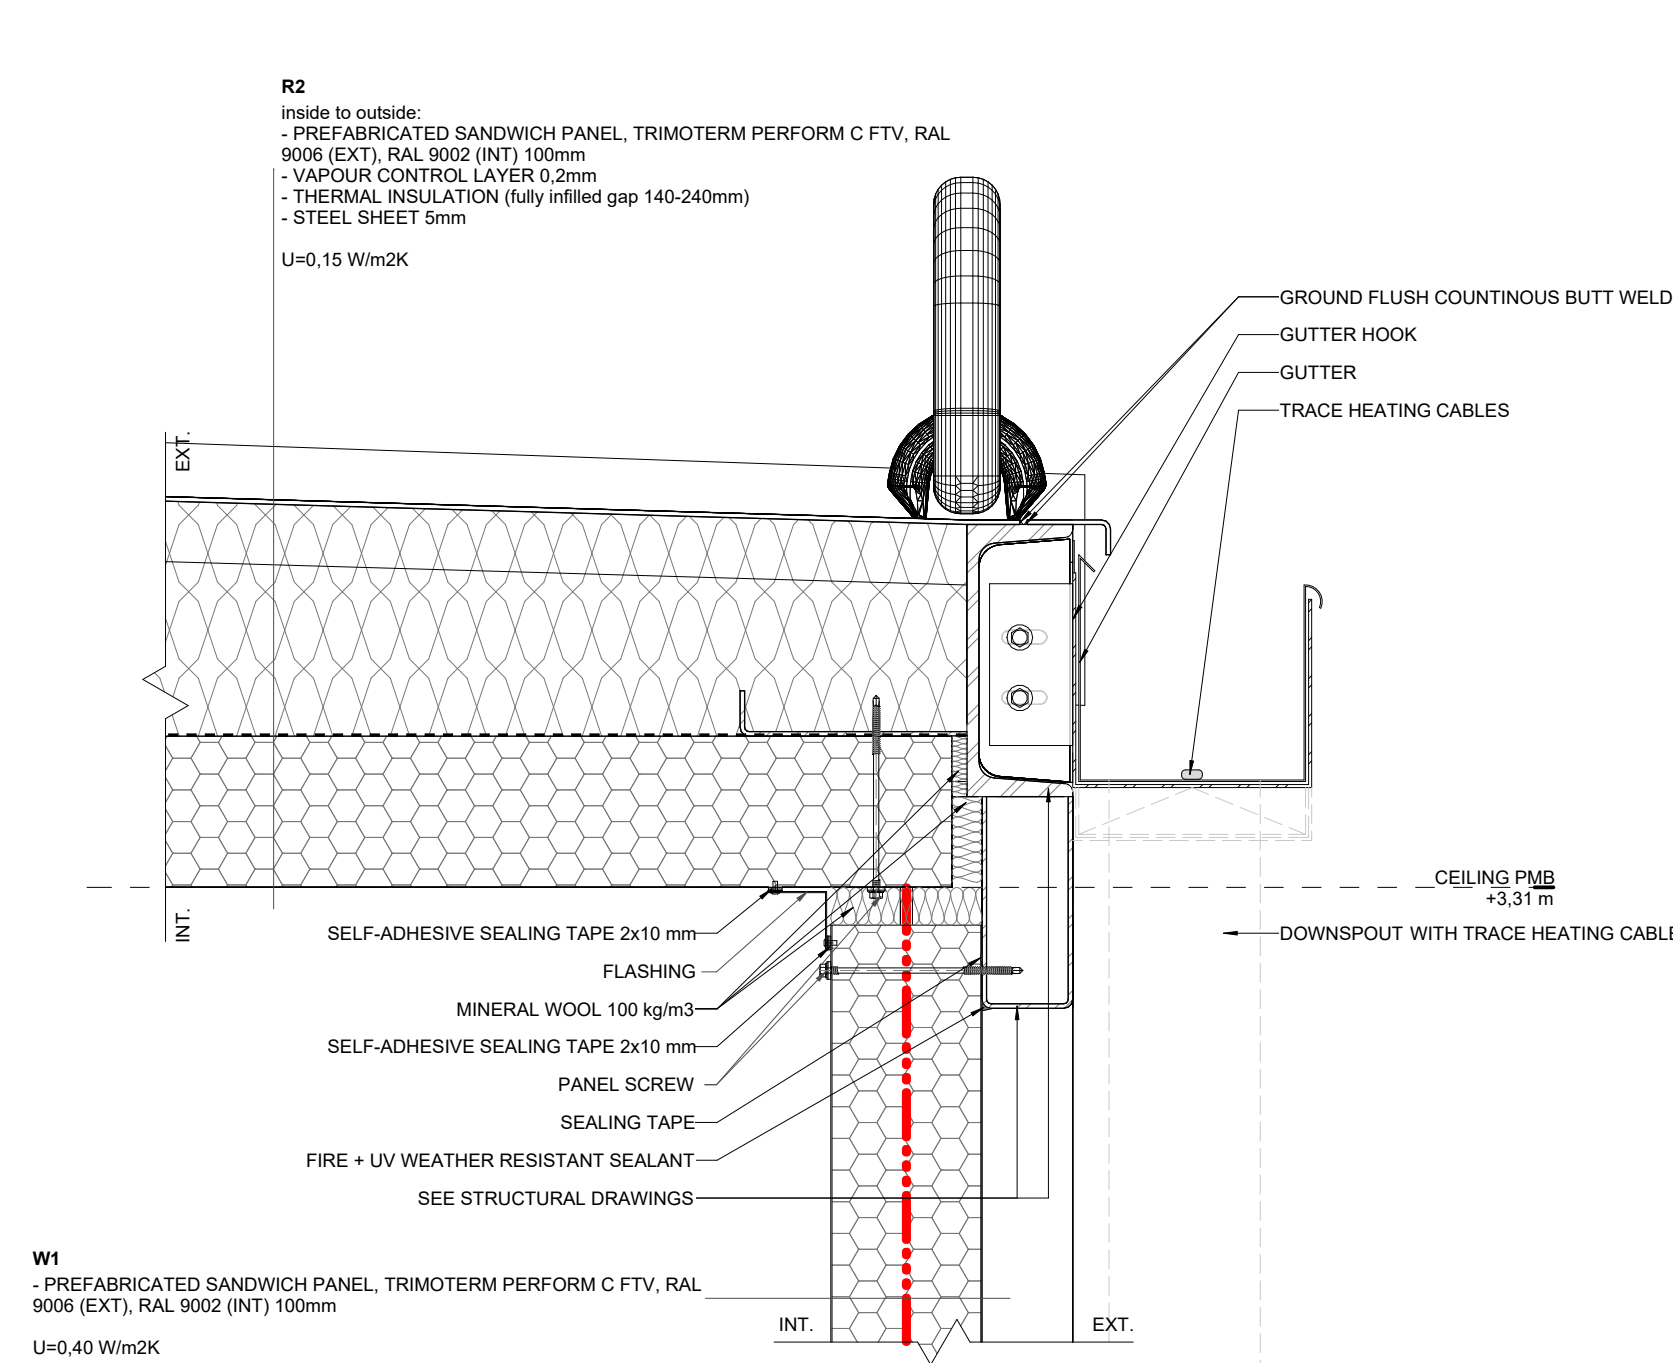


V09 PM/MV/MS - EXT. WALL/ROOF CONNECTION
1:5

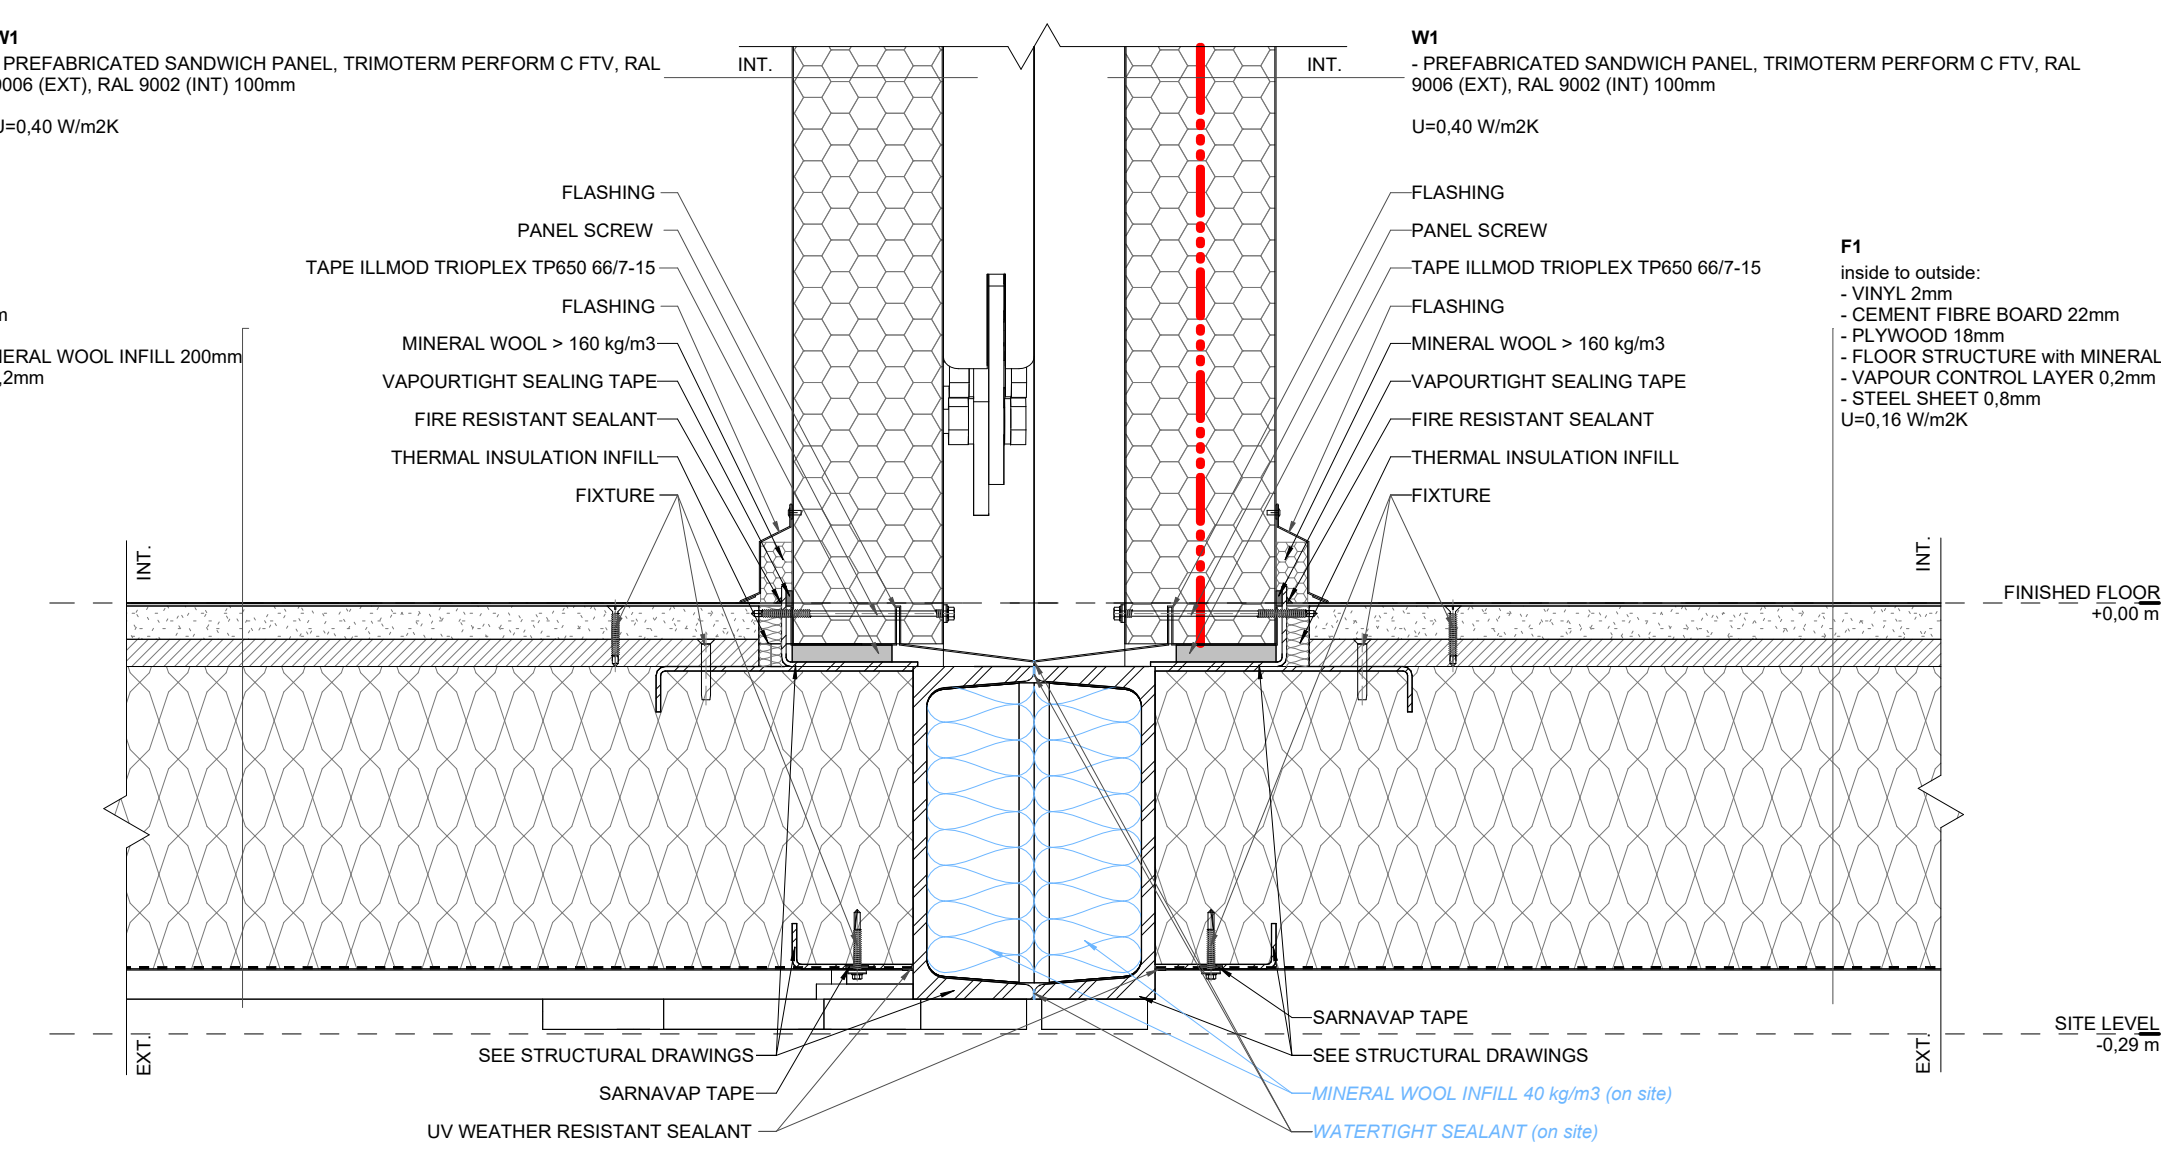


V08 PM/MV - MODULE CONNECTION-FLOOR
1:5

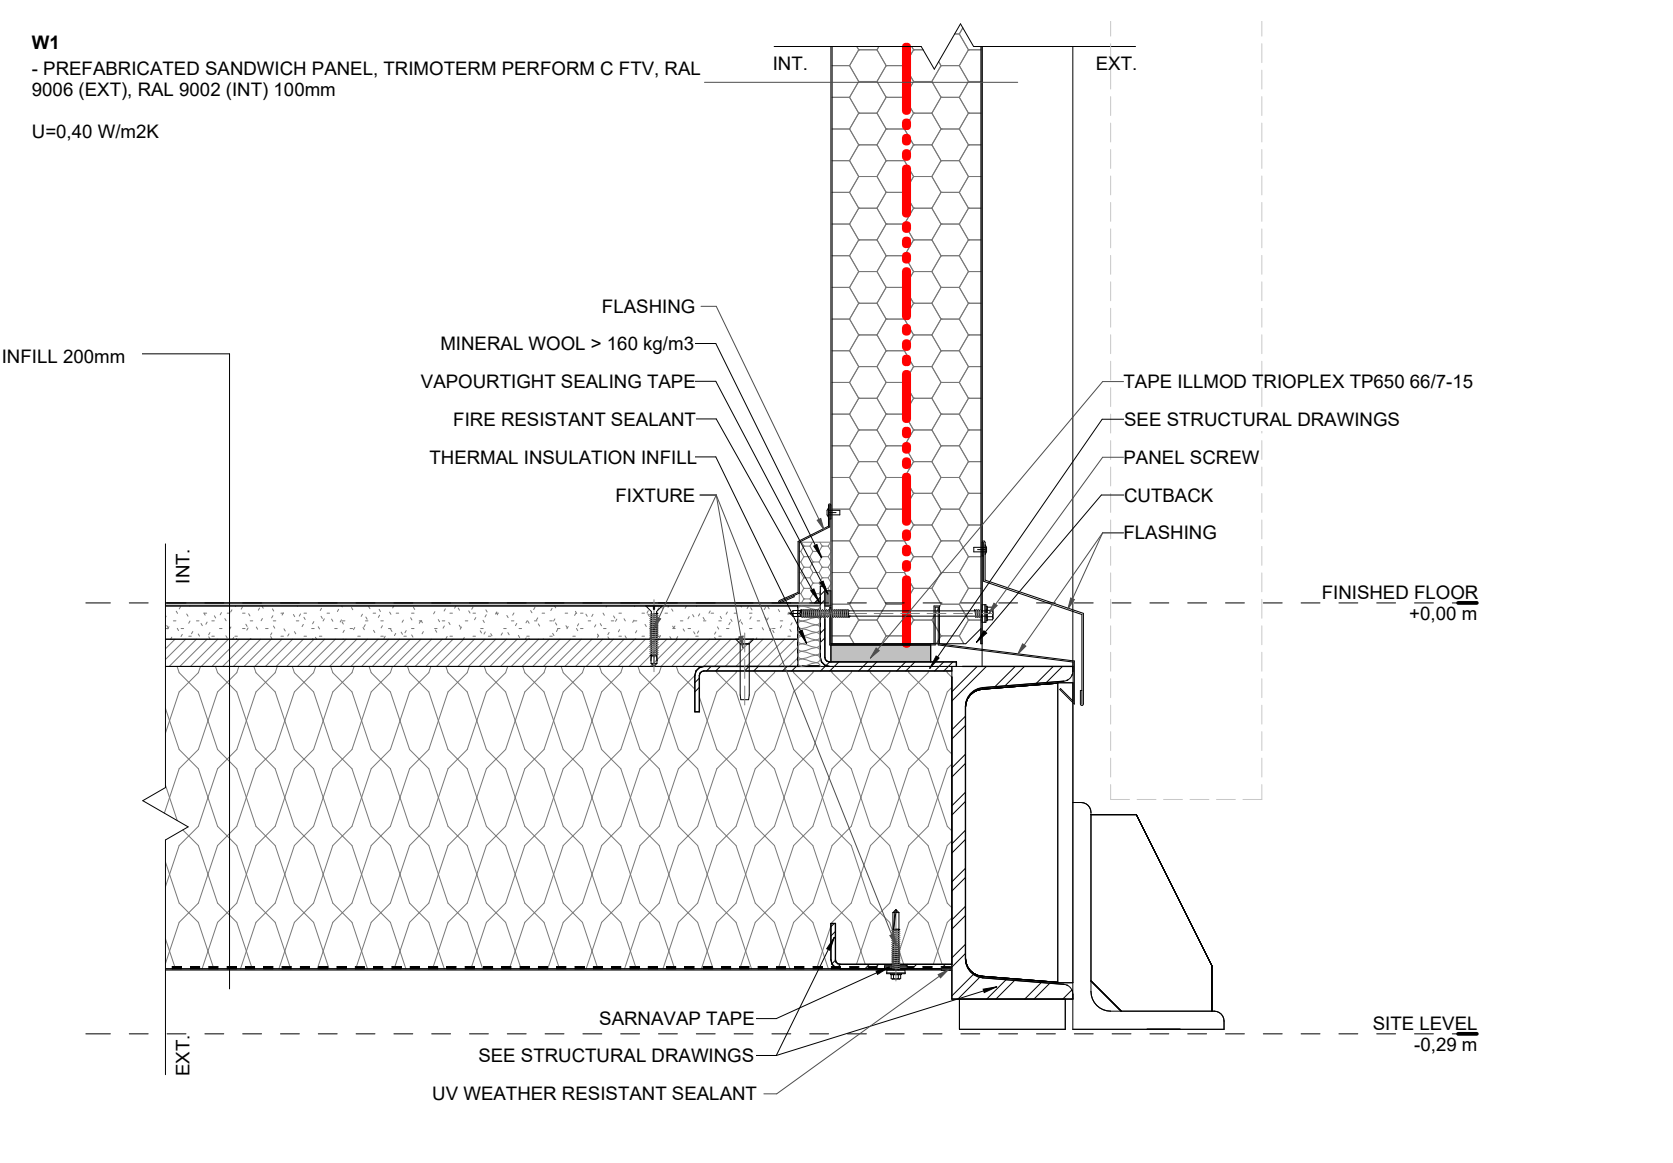

V10 PM/MV/MS - EXT. WALL/FLOOR CONNECTION
1:5

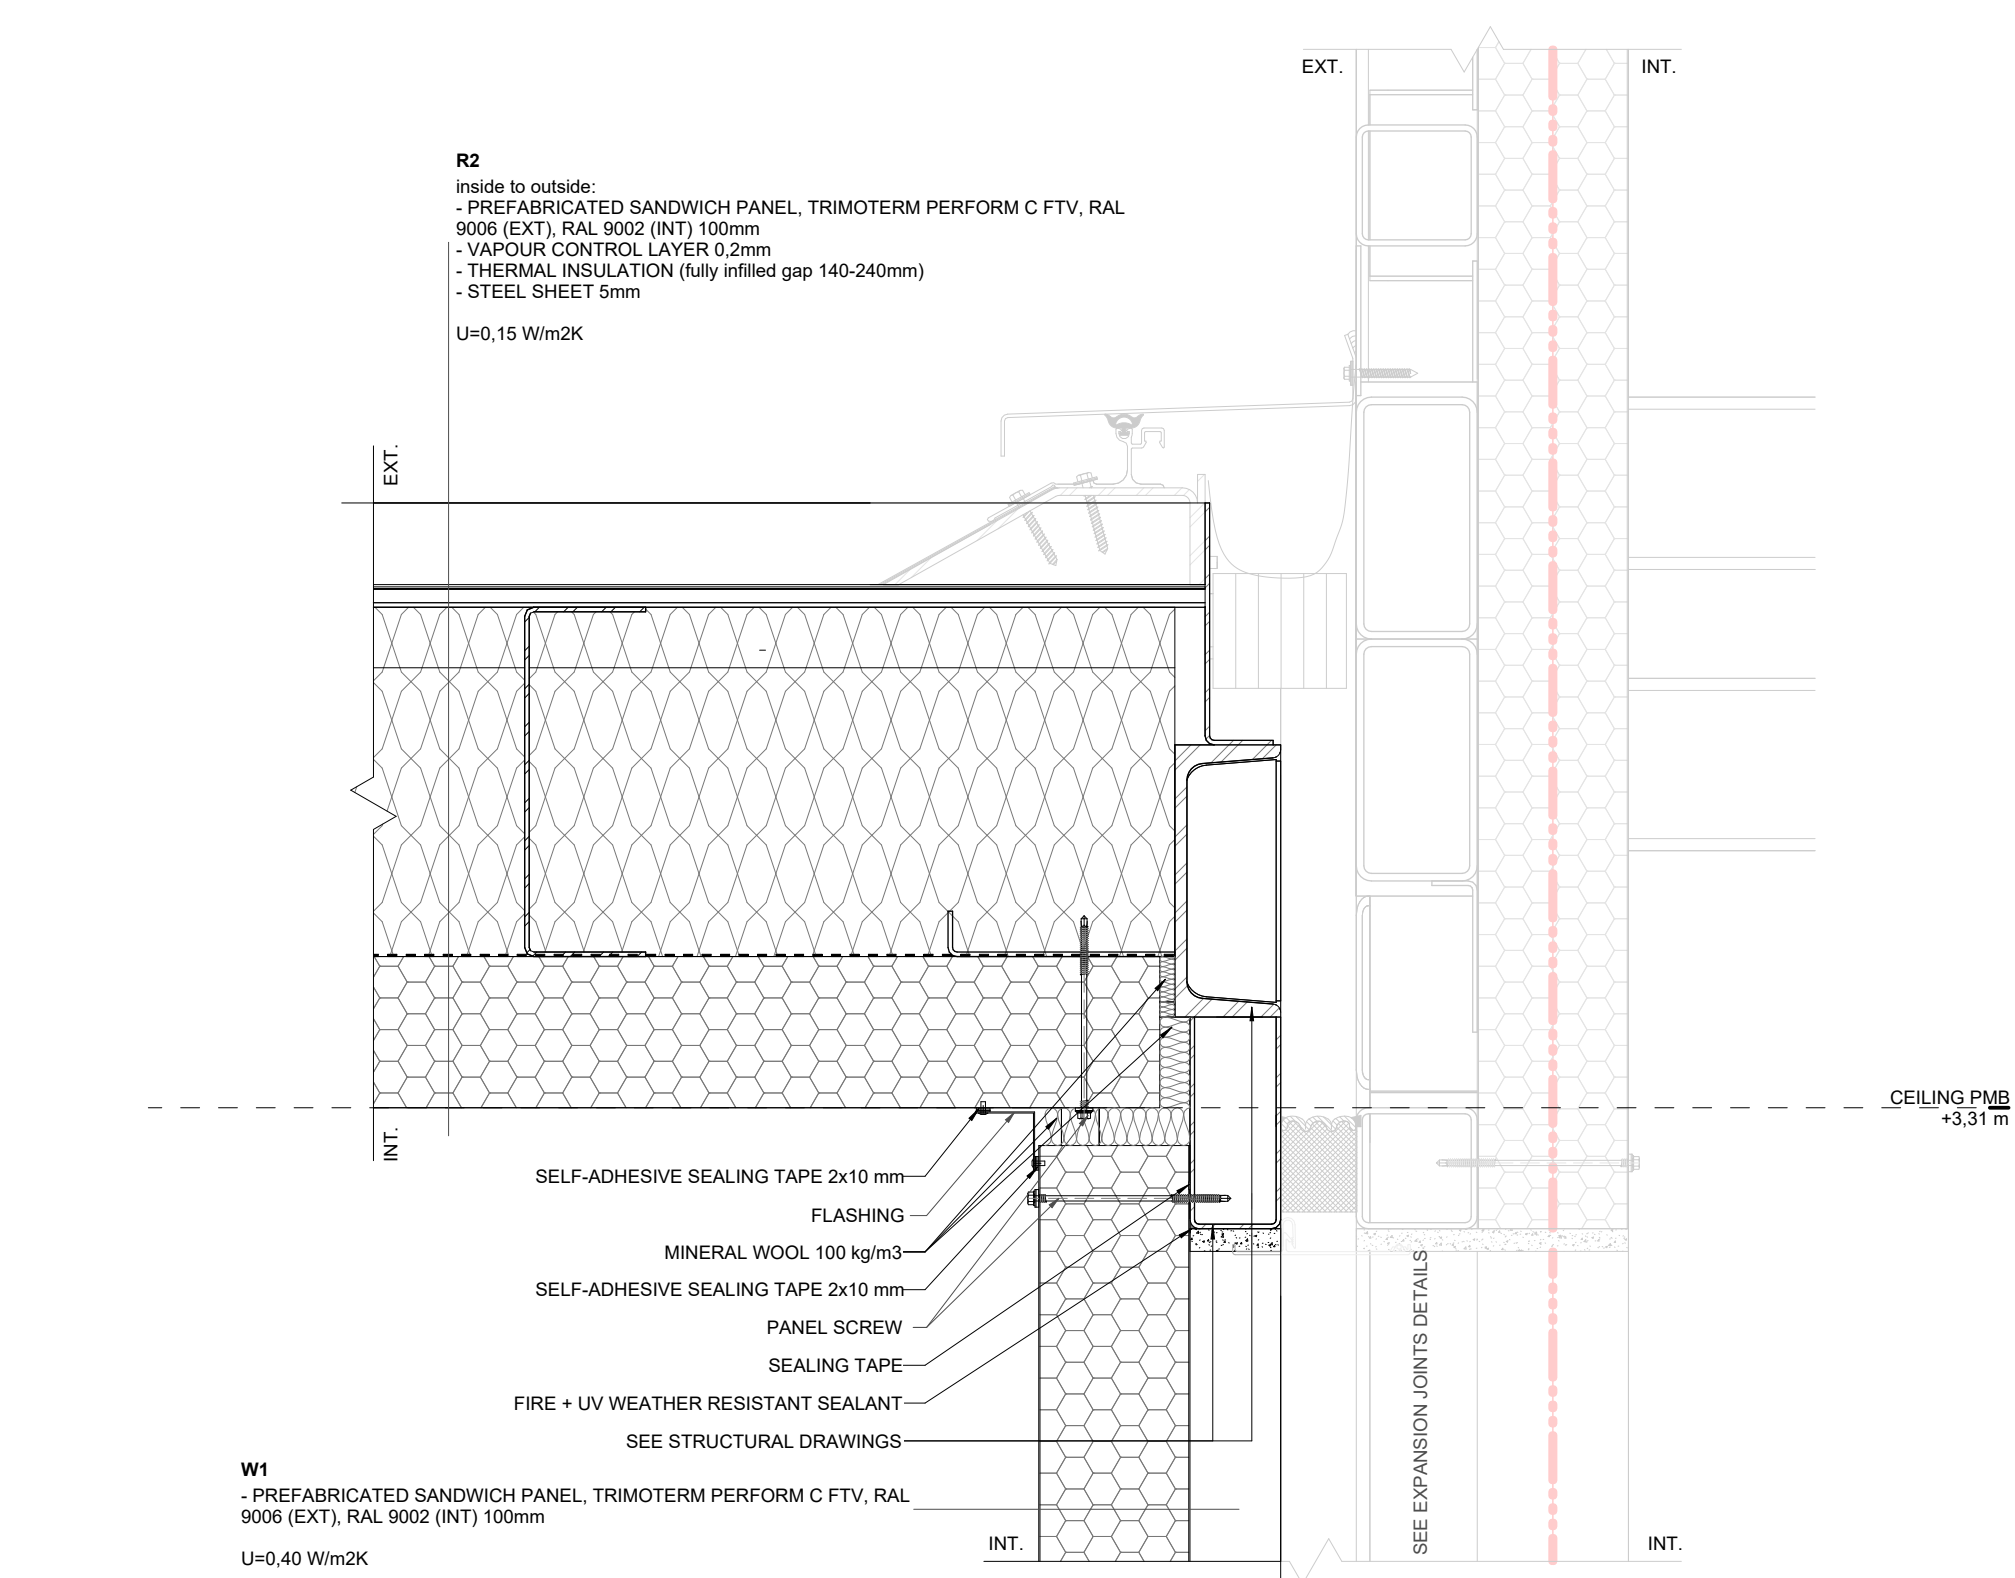

V11 PM - RPP MODULE CONNECTION-ROOF
1:5

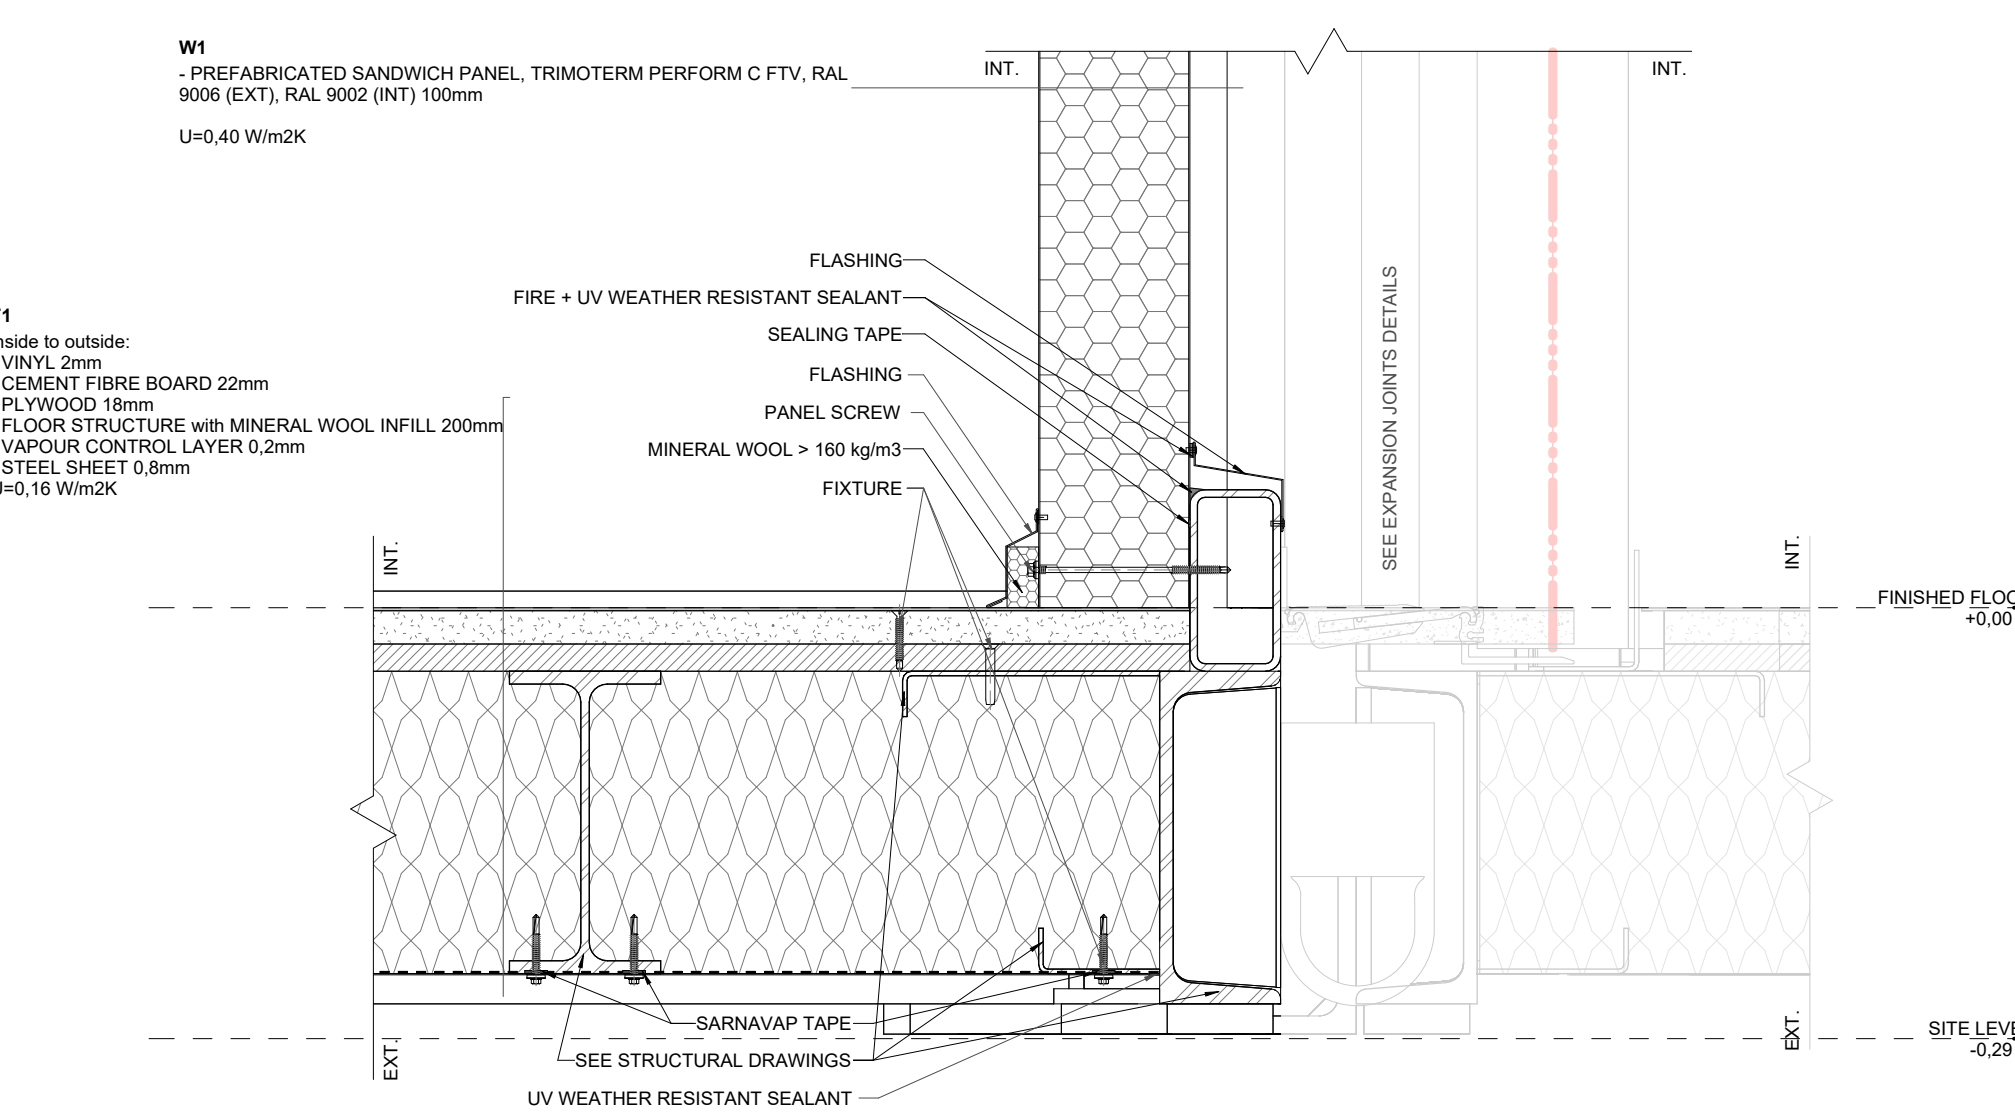


V12 PM - RPP MODULE CONNECTION-FLOOR
1:5

KEYNOTES

LEGEND:
- FIRE COMPARTMENT BORDER 60
- FIRE COMPARTMENT BORDER 30
- ELEMENTS INSTALLED ON SITE

KEY PLAN

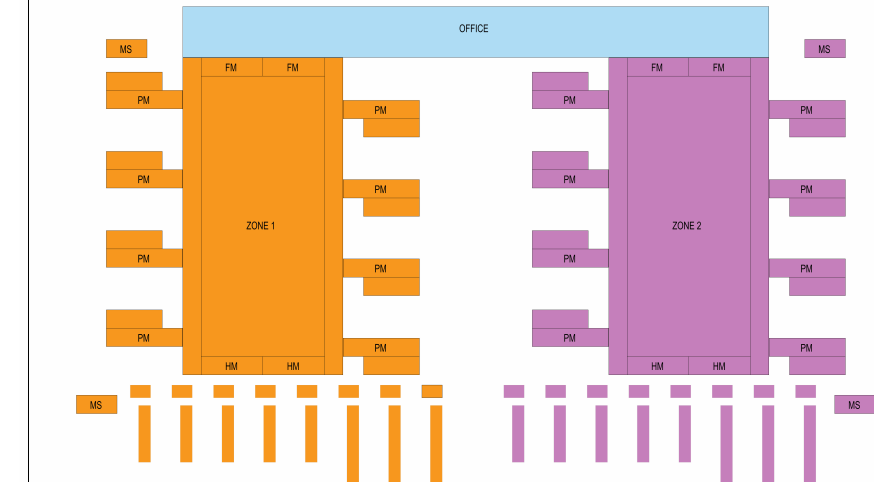

R01 CD SET - FOR INFORMATION 2026-07-24

REV. DESCRIPTION DATE



ECO DC MONALISA

ARCHITECTURAL DETAILS
- PREFABRICATED MODULES
- VERTICAL VIEWS - PM - MV - MS

PREPARED (ALSO SUBJECT RESPONSIBLE IF OTHER)

L. MAVREK / K. KOZINA

DOCUMENT RESPONSIBLE (APPROVED)

M. PACAK

DATE (YYYYMMDD)

2026-07-24

REVISION

R01