



LEGAL DISCLAIMER: THIS DOCUMENT AND THE CONTENTS HEREIN ARE CONFIDENTIAL AND THE SOLE PROPERTY OF VERTIV GROUP CORP. REPRODUCTION, DISTRIBUTION OR UNAUTHORIZED USE OF THIS DOCUMENT OR ANY PARTS WITHIN THIS DOCUMENT ARE FORBIDDEN WITHOUT THE WRITTEN CONSENT OF VERTIV GROUP CORP.

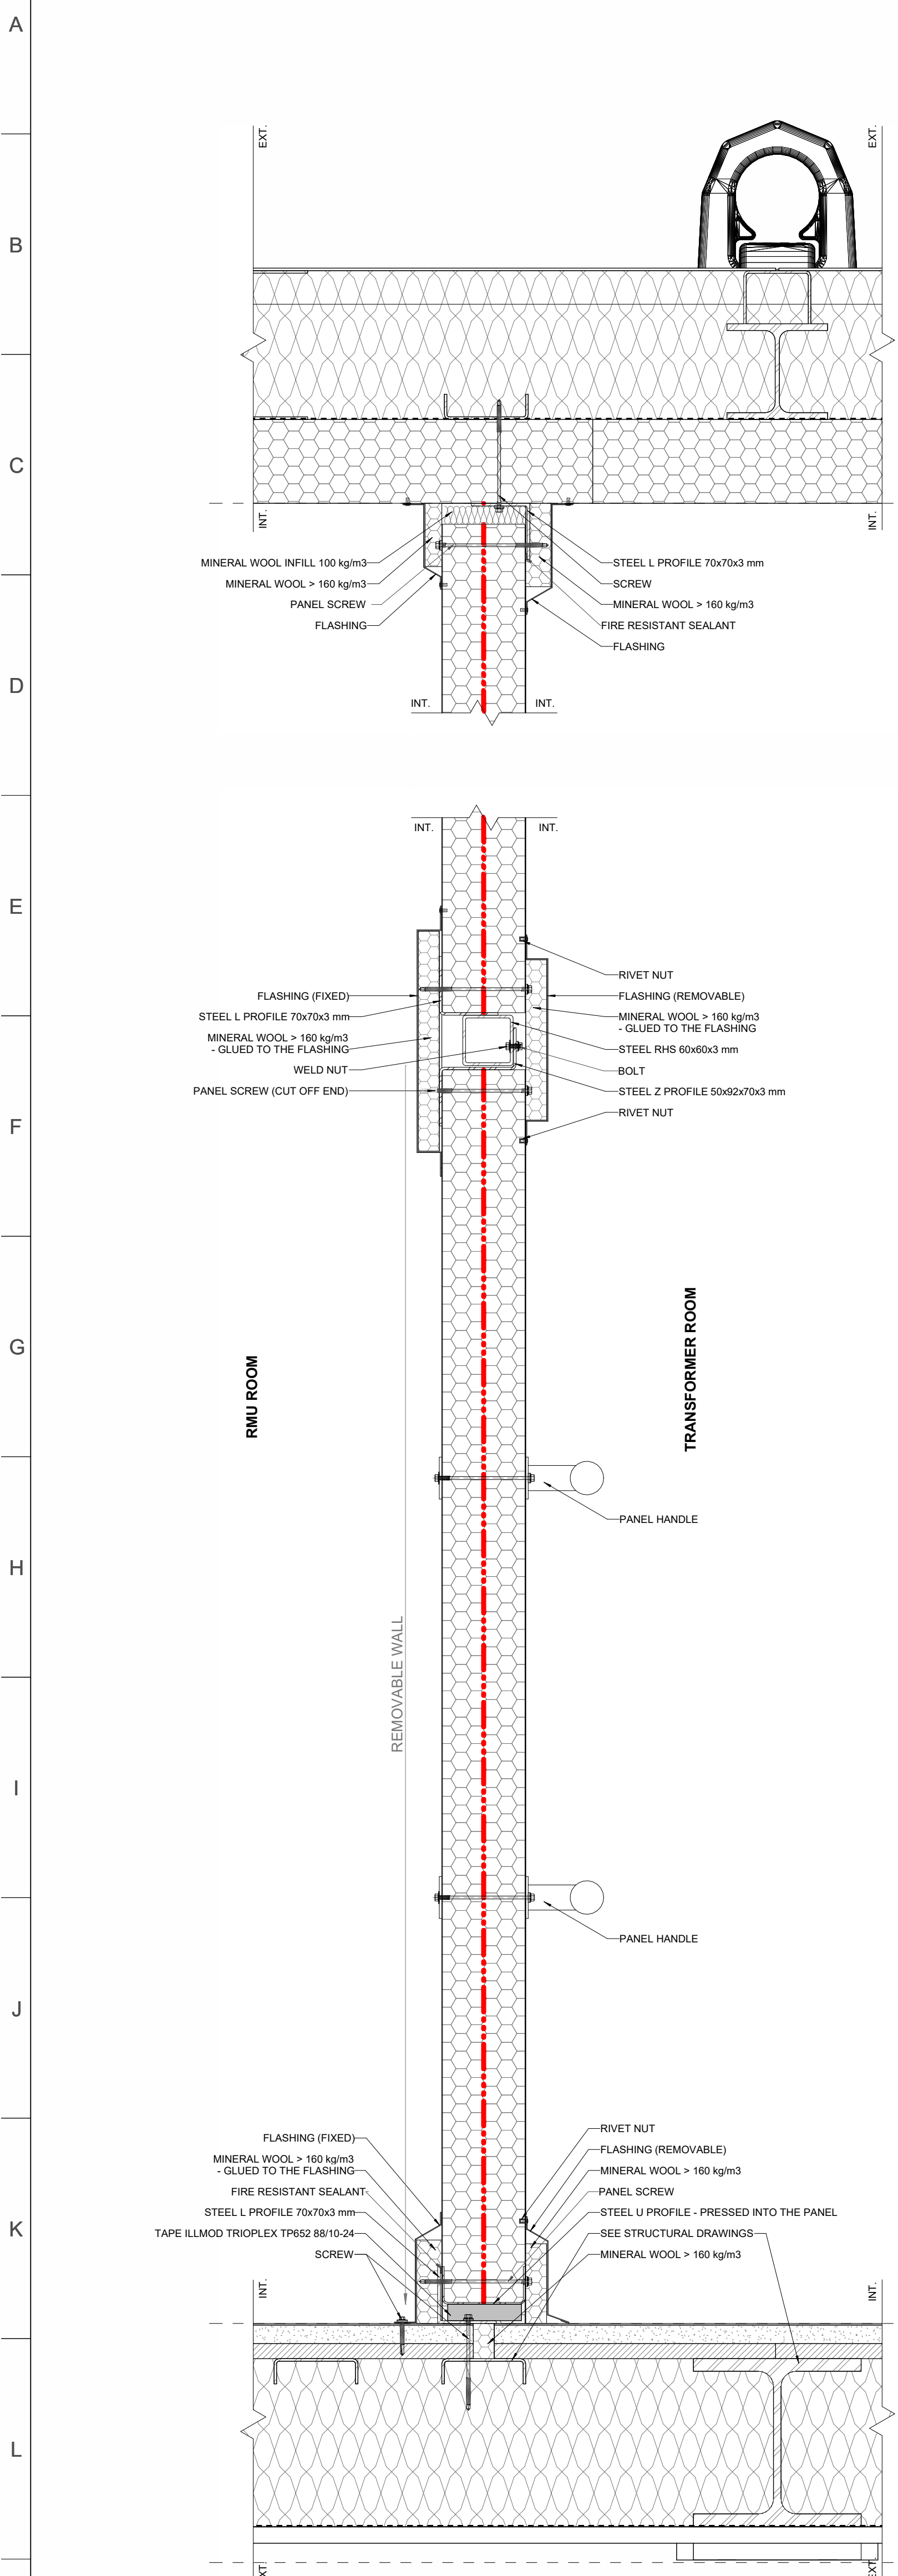


V13 MV-REMOVABLE WALL SECTION
1:5

PM - REMOVABLE WALLS SECTION


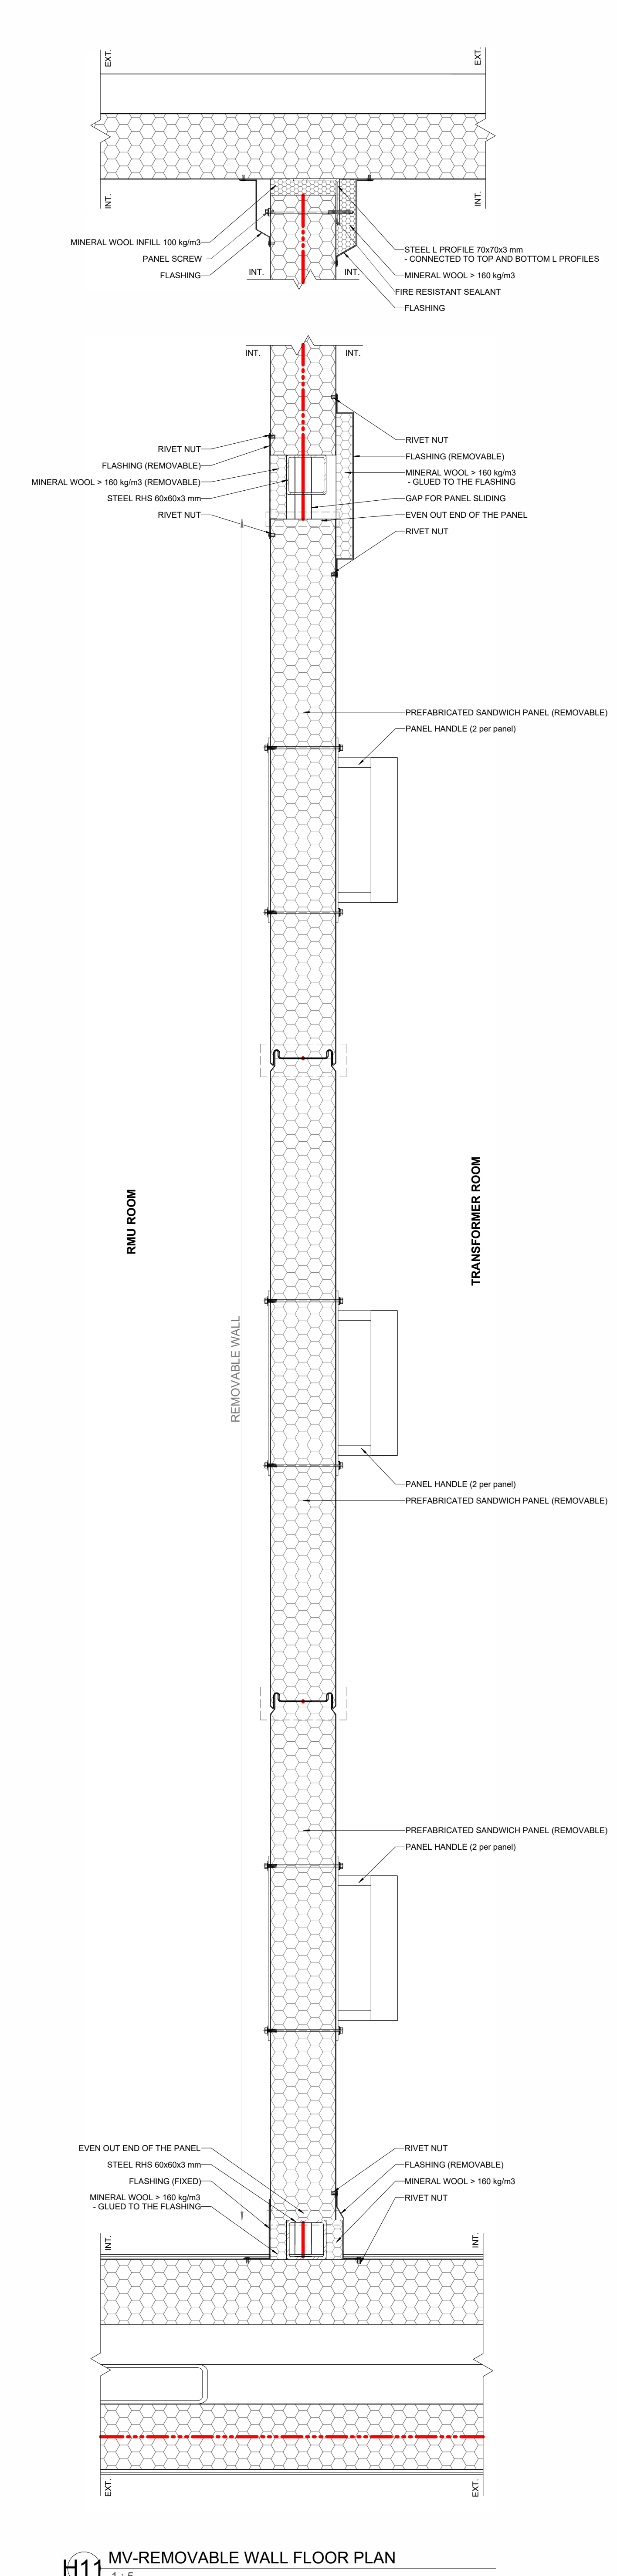


H11 MV-REMOVABLE WALL FLOOR PLAN
1:5

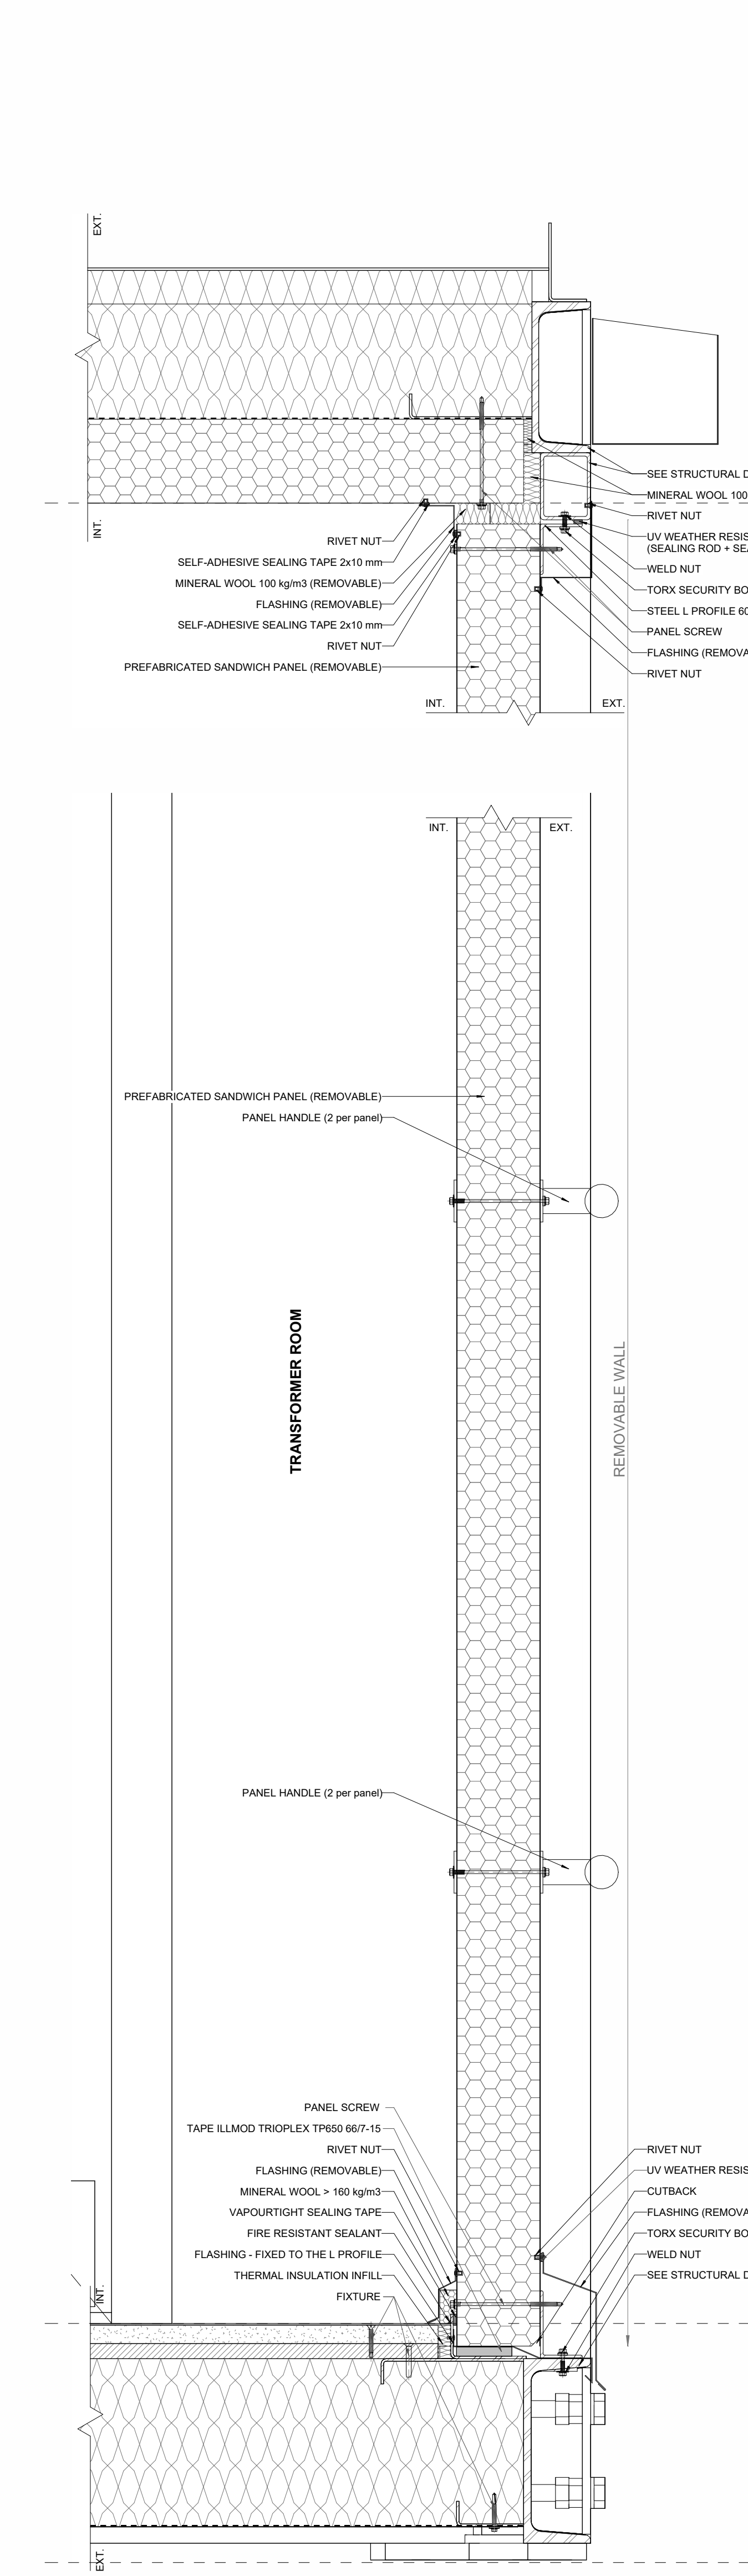


V14 TRANSFORMER REMOVABLE WALL SECTION
1:5

H12 TRANSFORMER REMOVABLE WALL FLOOR PLAN
1:5

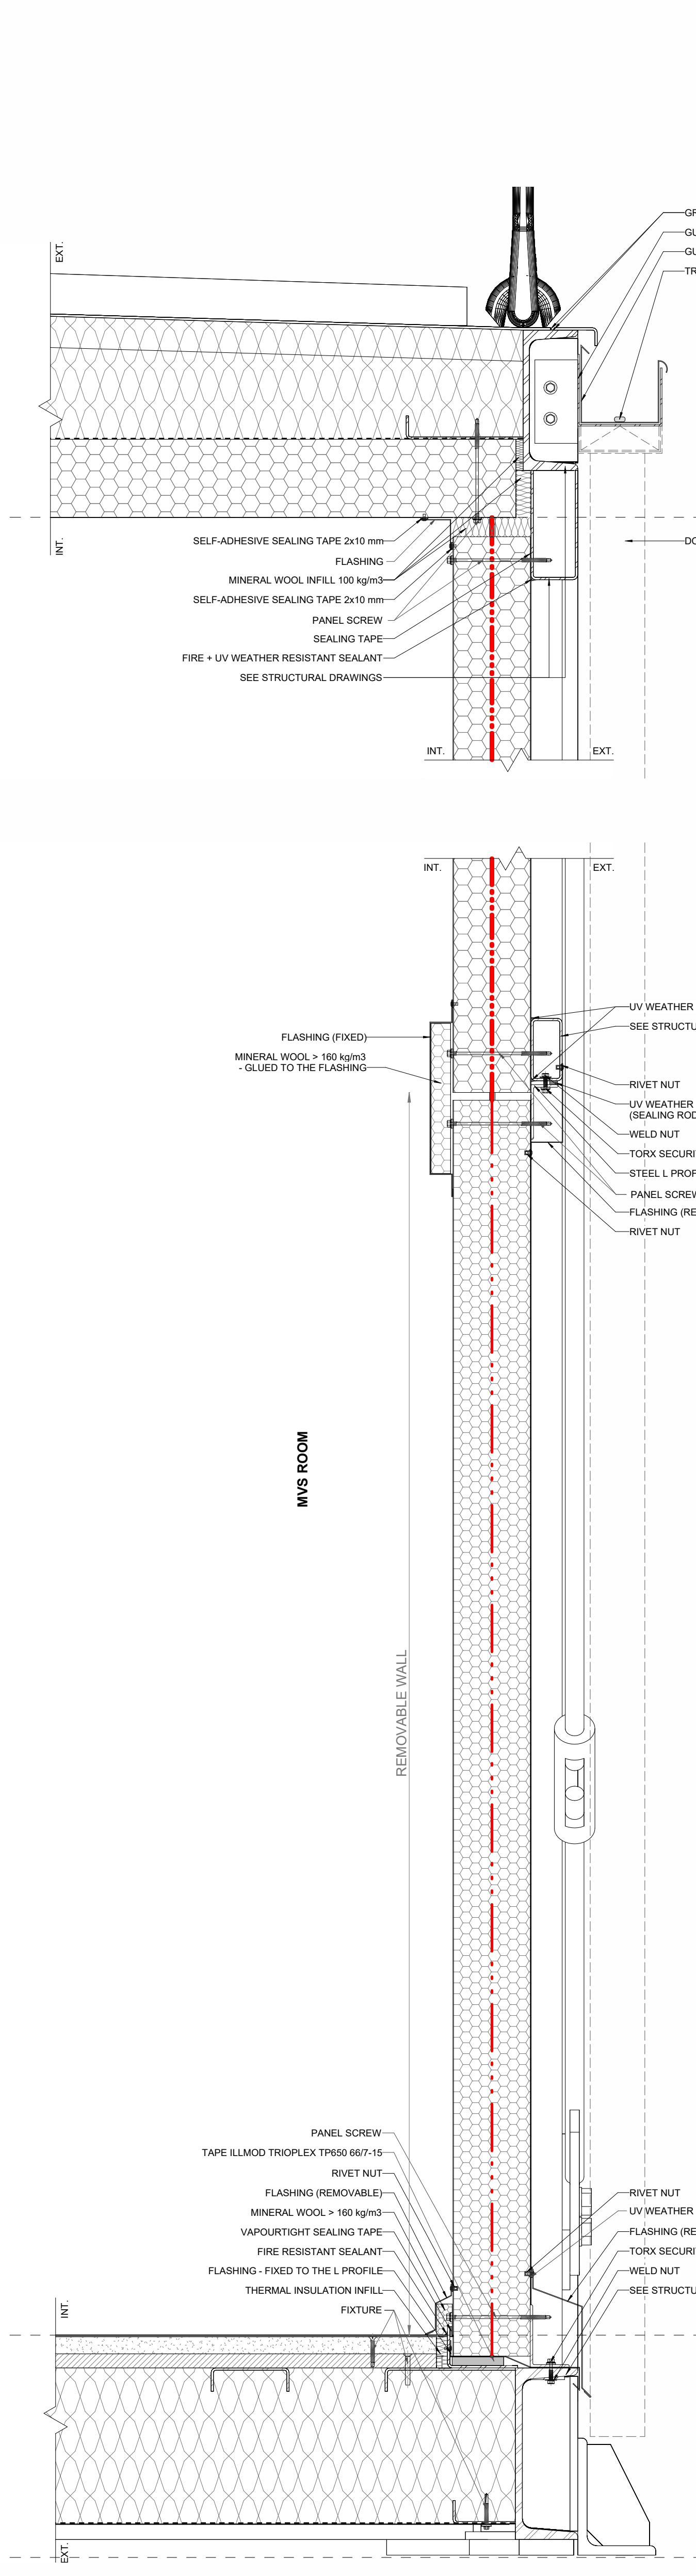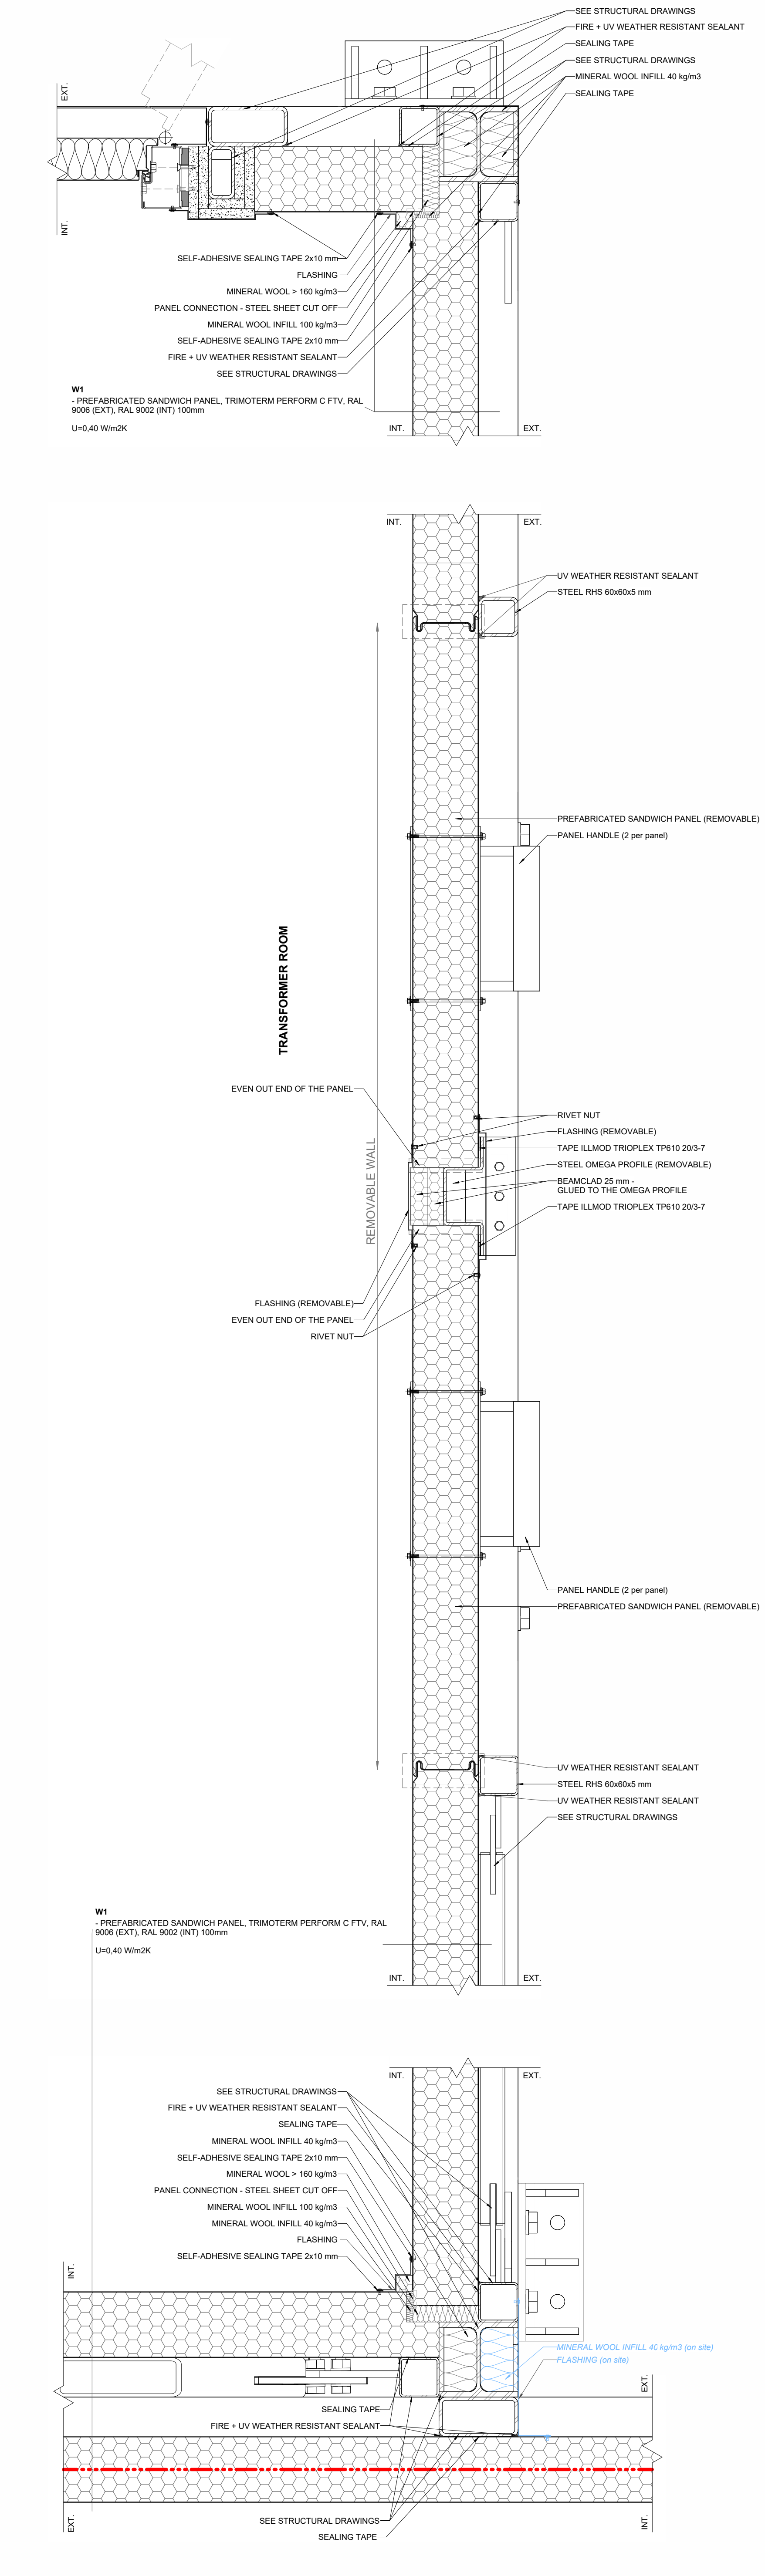

V15 MS REMOVABLE WALL SECTION
1:5

KEY PLAN - MS MODULE REMOVABLE WALL POSITION

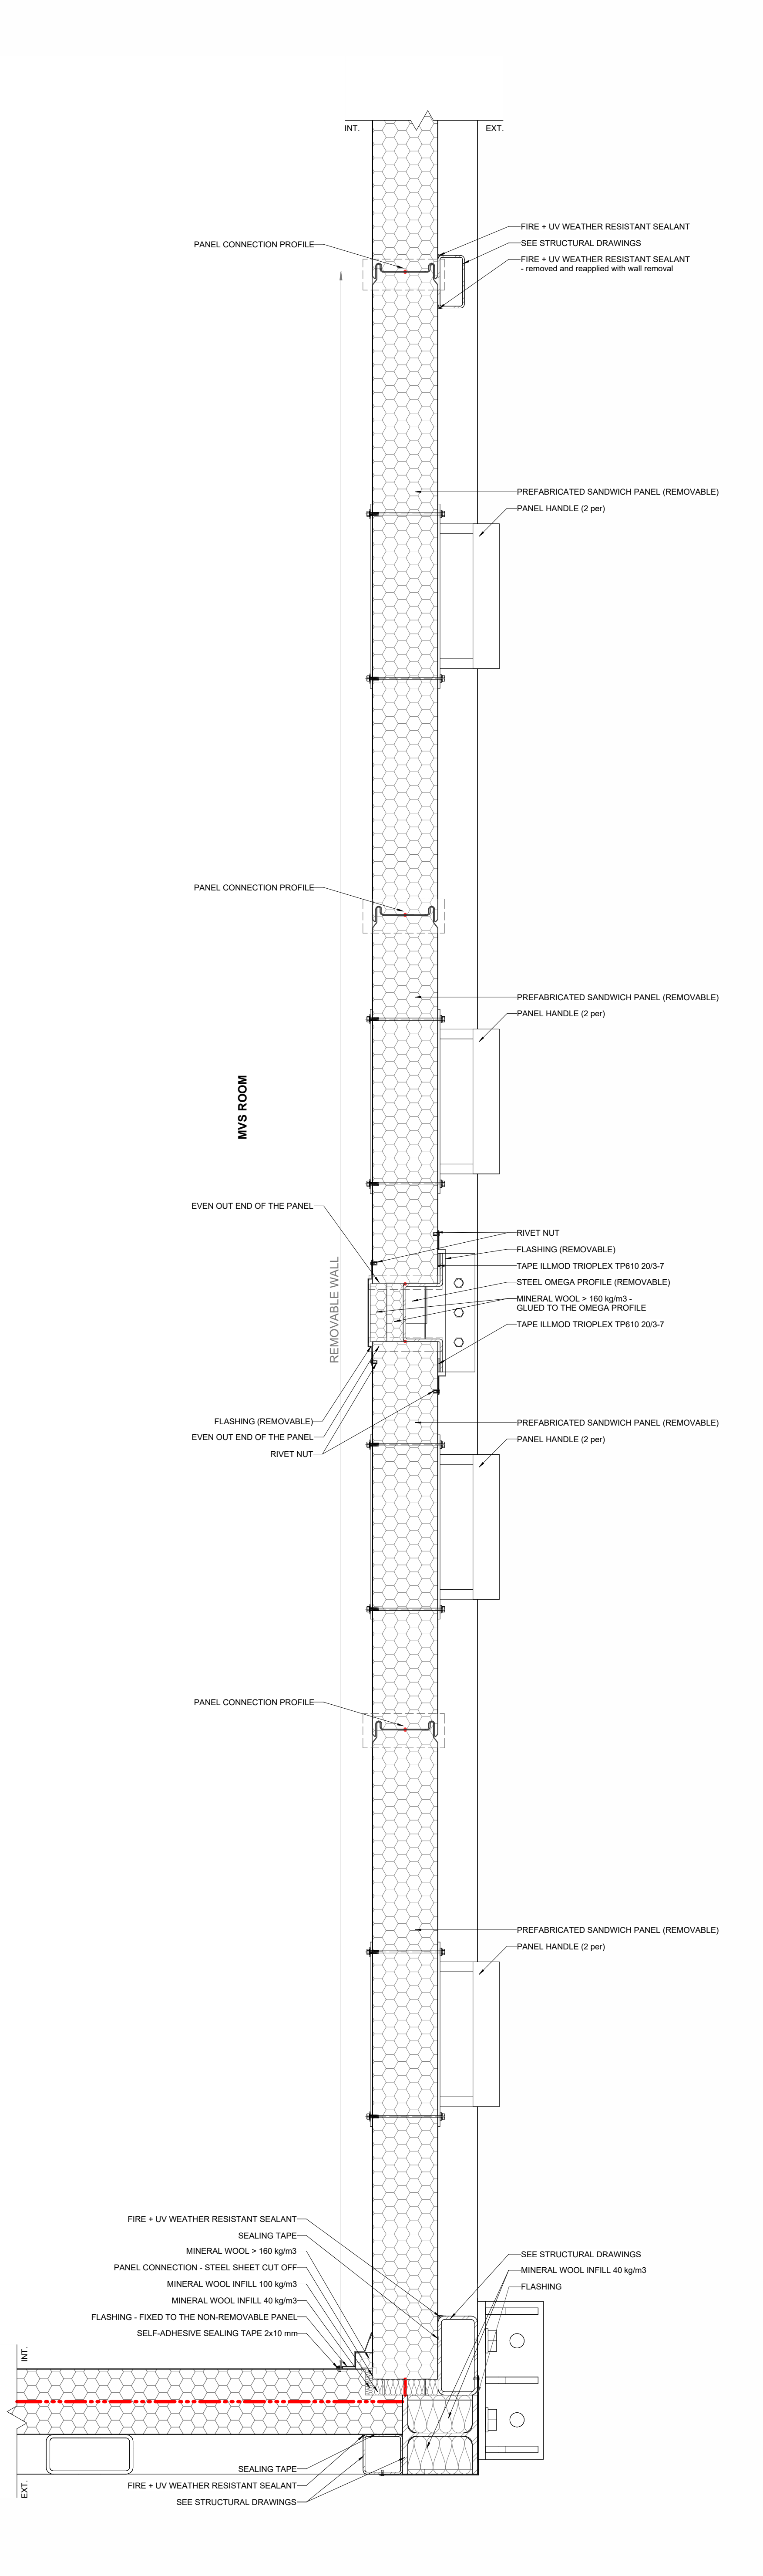

H13 MS REMOVABLE WALL FLOOR PLAN
1:5

KEYNOTES

- FIRE COMPARTMENT BORDER (E-60)
- FIRE COMPARTMENT BORDER (E-60)
- ELEMENTS INSTALLED ON SITE

KEY PLAN

REV. DESCRIPTION DATE

REV.	DESCRIPTION	DATE
R01	CD SET - FOR INFORMATION 2026-07-24	

PROJECT NAME
ECO DC MONALISA

DRAWING NAME
ARCHITECTURAL DETAILS
- PREFABRICATED MODULES
- REMOVABLE WALL - PM - MV - MS

PREPARED (AND SUBJECT TO APPROVAL IF OTHERS)
L. MAVREK / K. KOZINA

DOCUMENT RESPONSIBLE (APPROVED)
M. PACAK

DATE OF PREPARATION
2026-07-24

DATE OF APPROVAL
2026-07-24

ECO DC VRT-MDC19-00-DR-A-50103

SCALE
A0+ 1:5

SHEET 1 OF 1

R01