



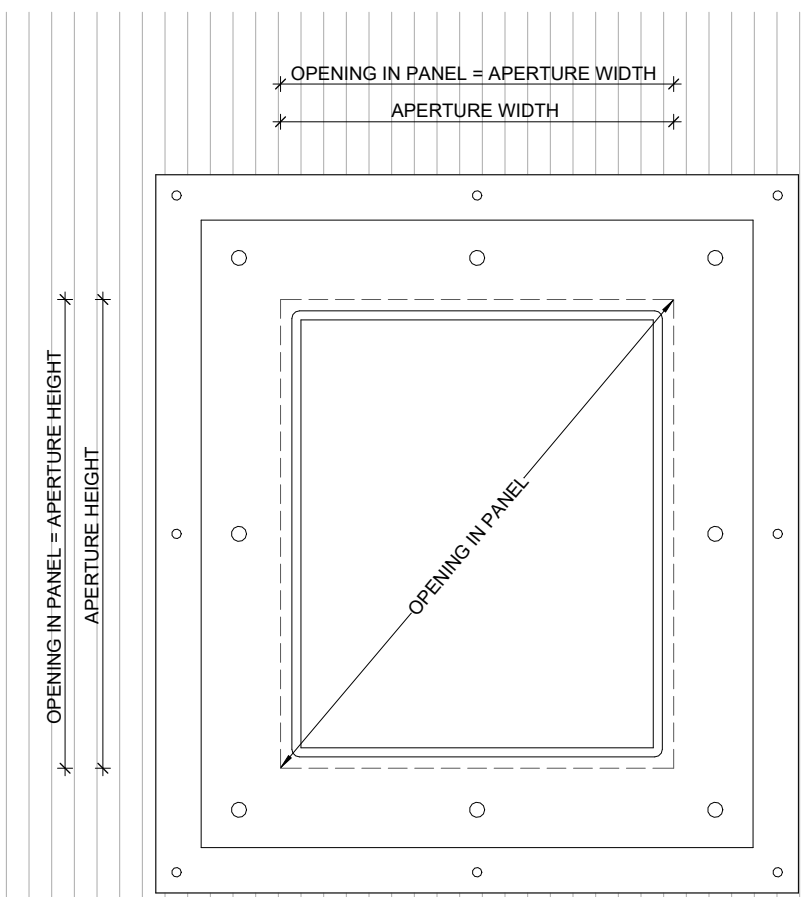


ELEVATION

P01 ROXTEC GH - EXTERIOR WALL 100 mm
1:5

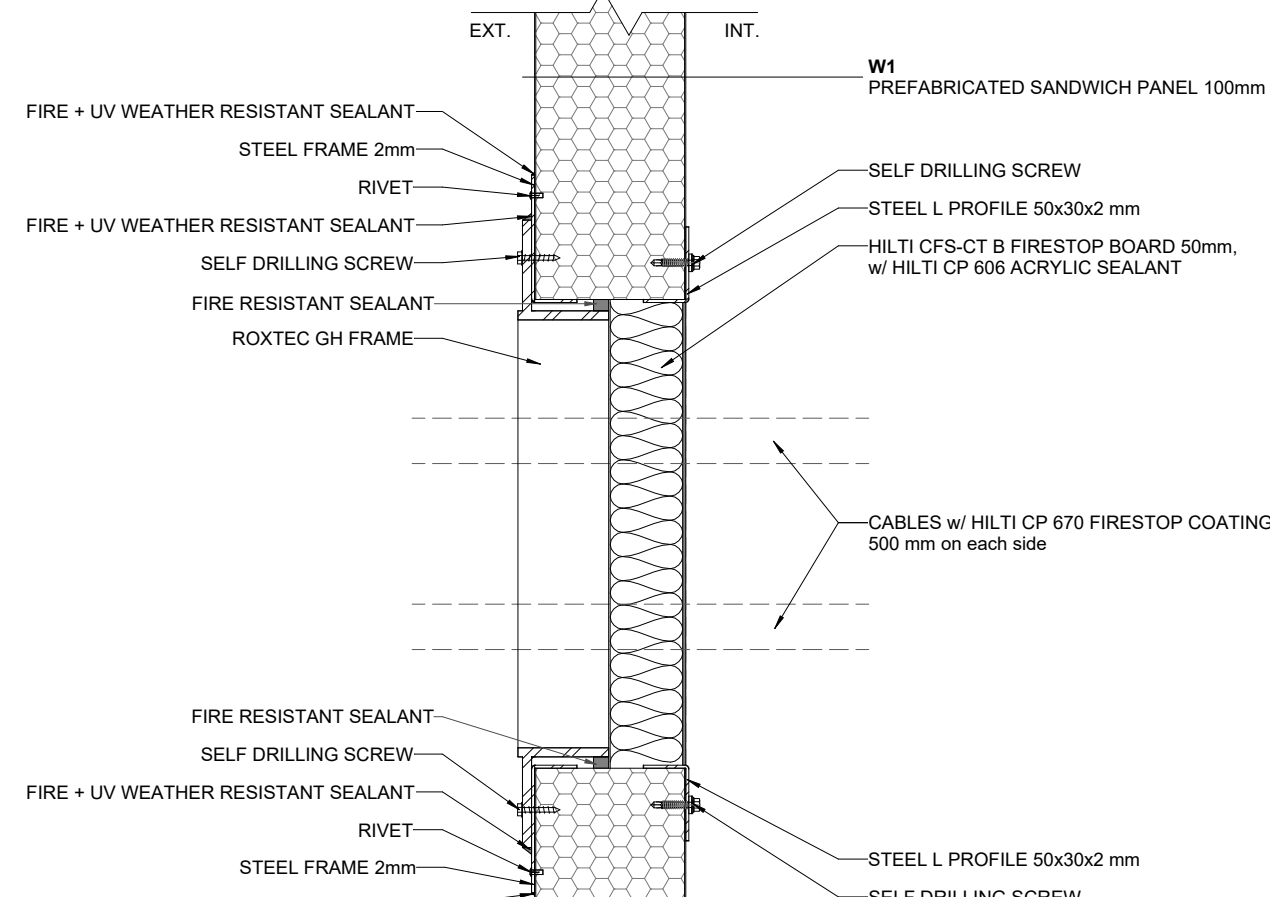


VERTICAL VIEW

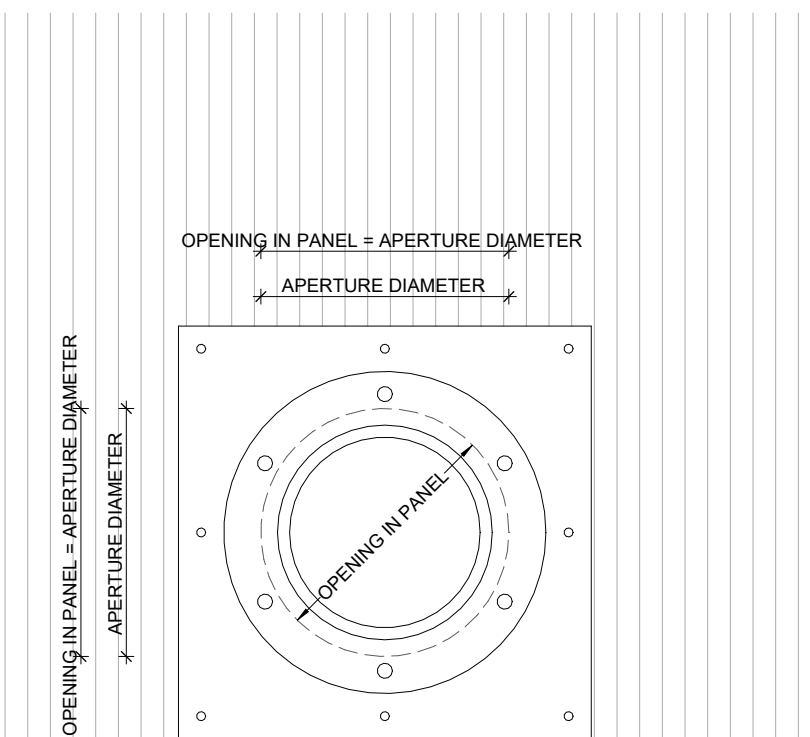


ELEVATION


P02 ROXTEC SLF RS - EXTERIOR WALL 100 mm
1:5

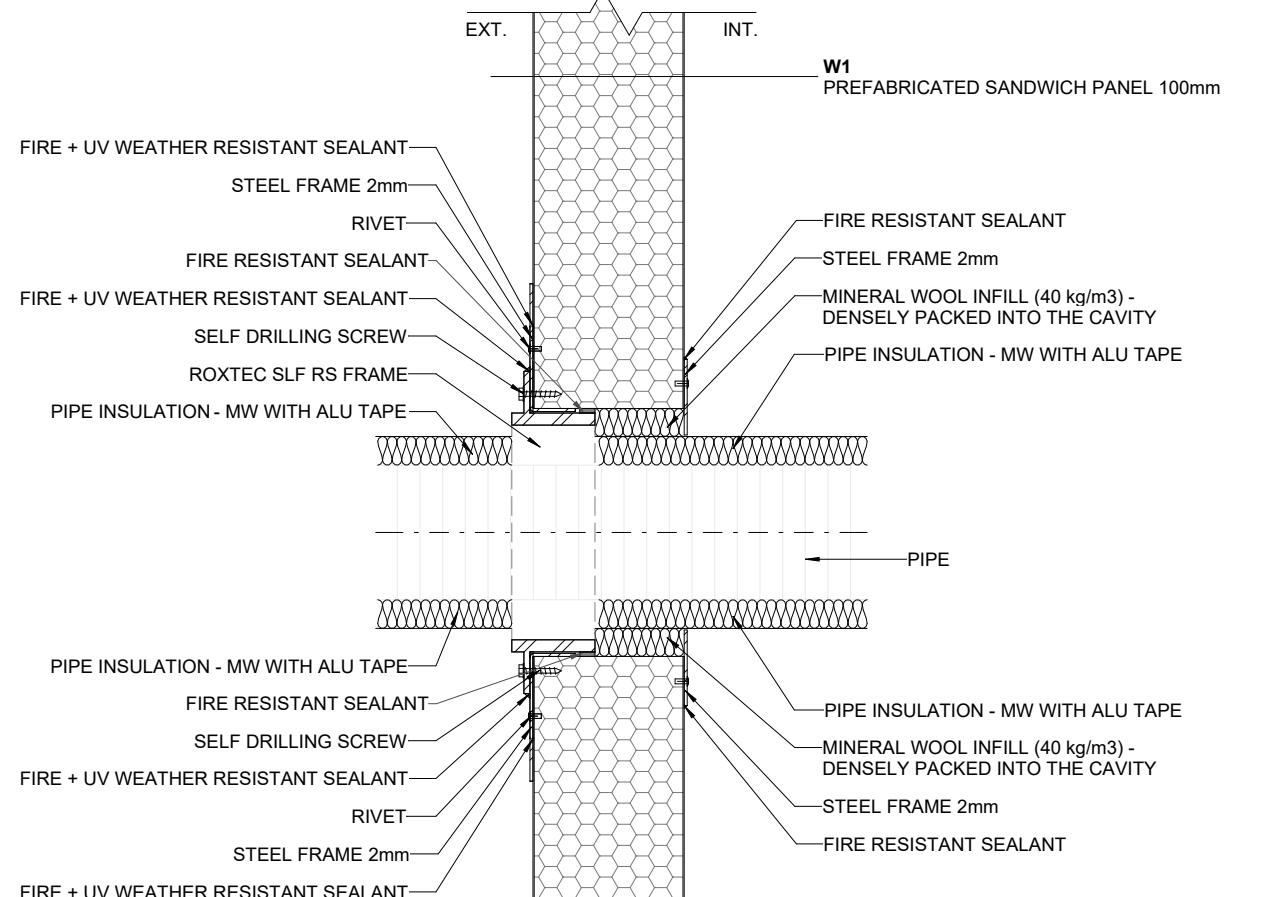


VERTICAL VIEW

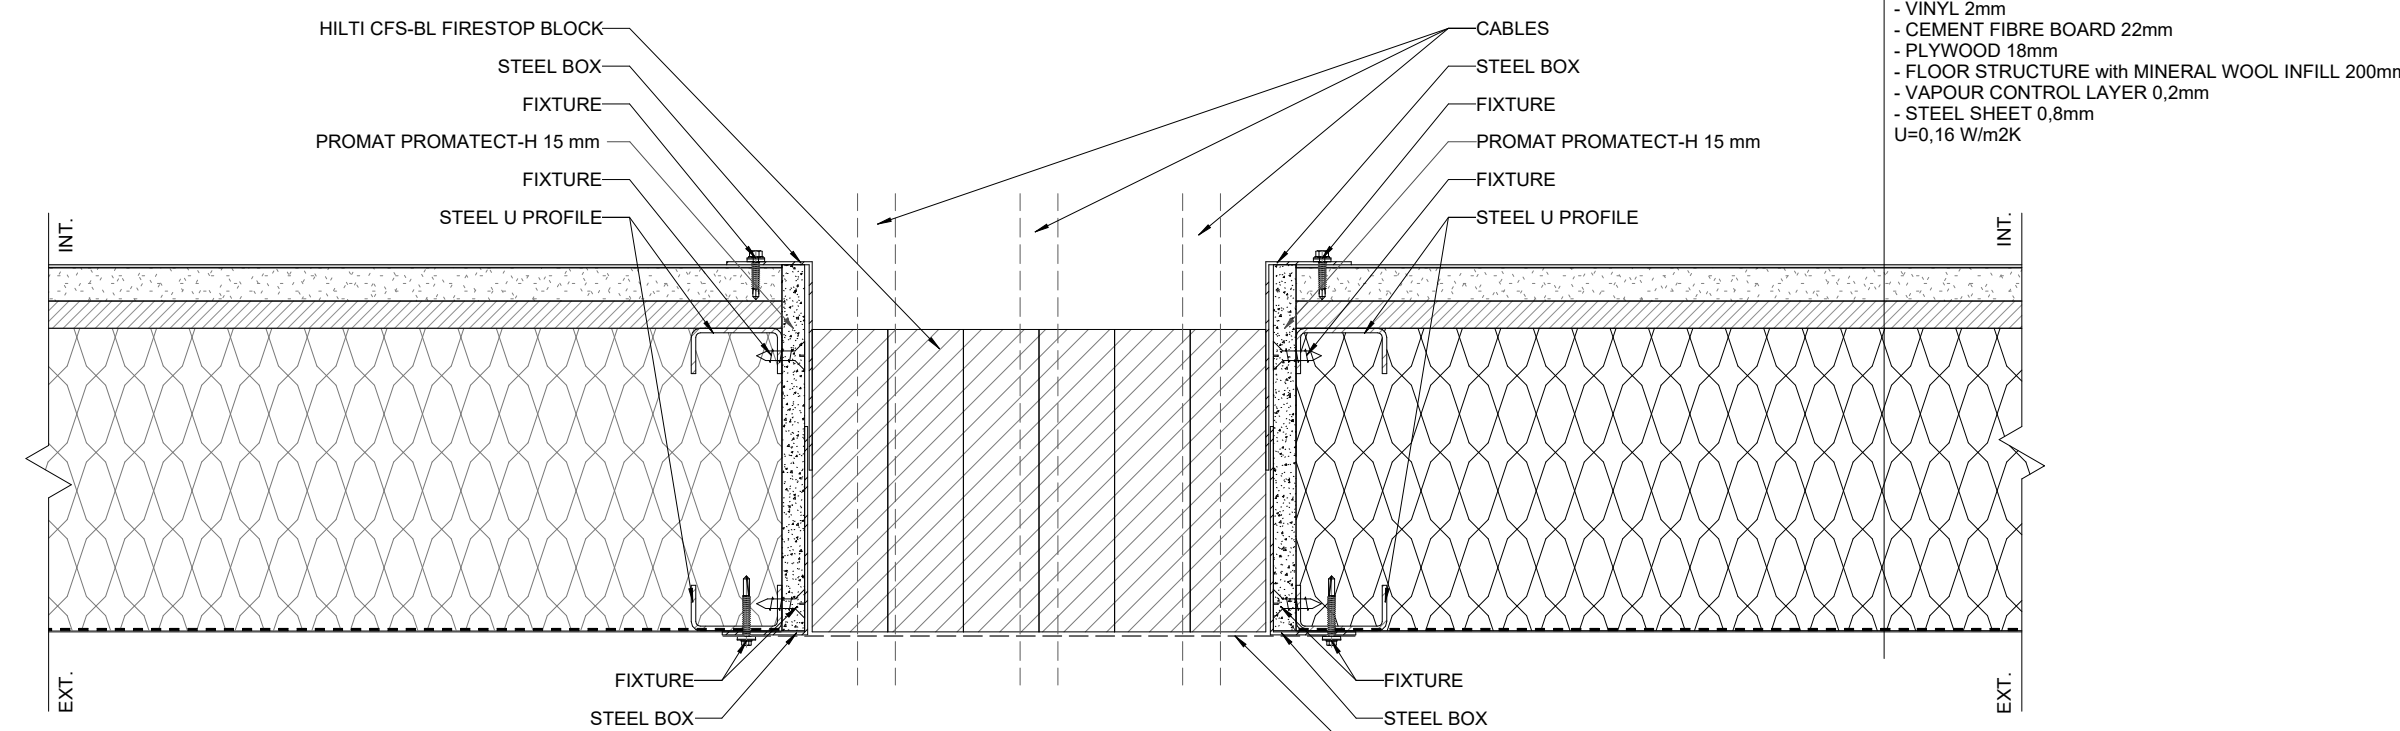

P15 HILTI CFS-BL FIRESTOP BLOCKS - FLOOR
1:5

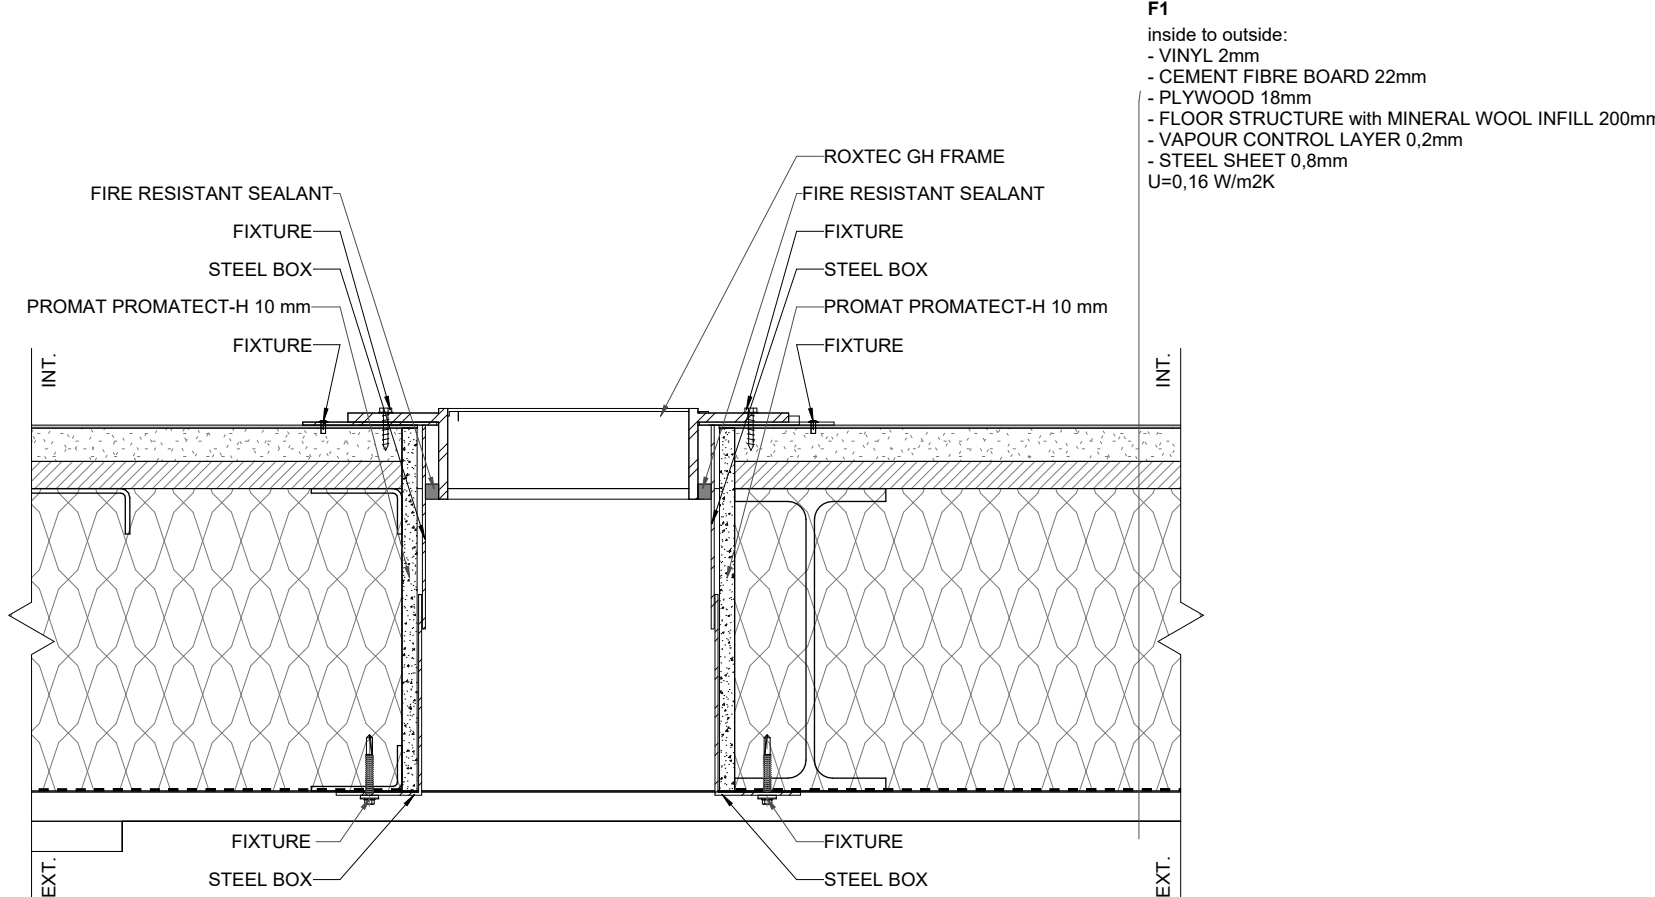


P03 ROXTEC GH - FLOOR
1:5

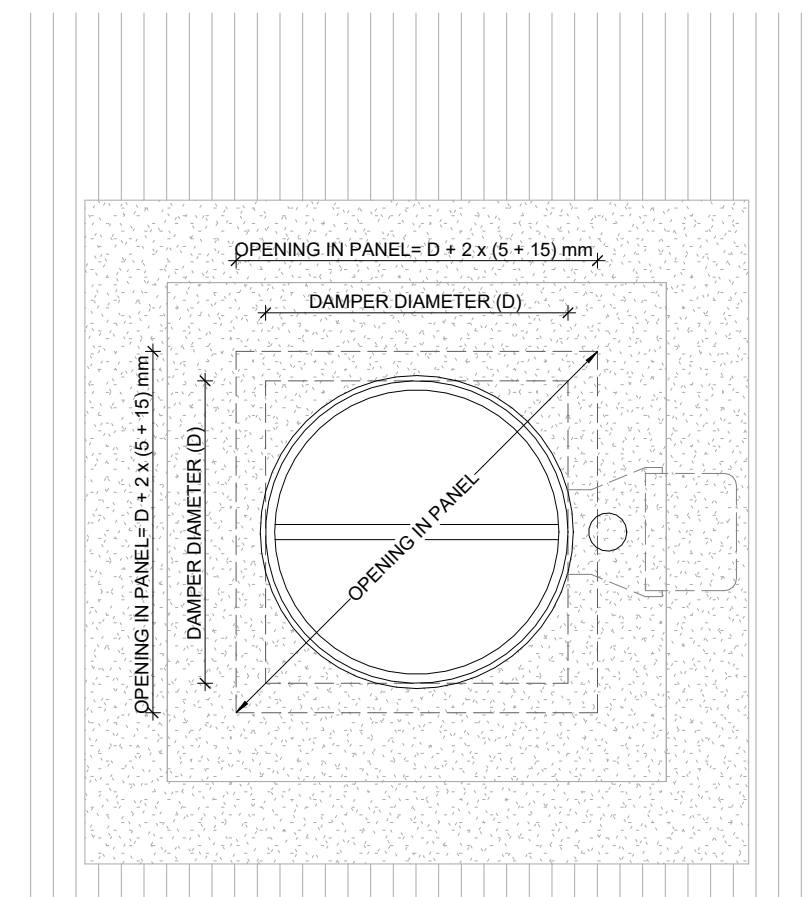


ELEVATION

P06 TROX FKRS-EU
1:5

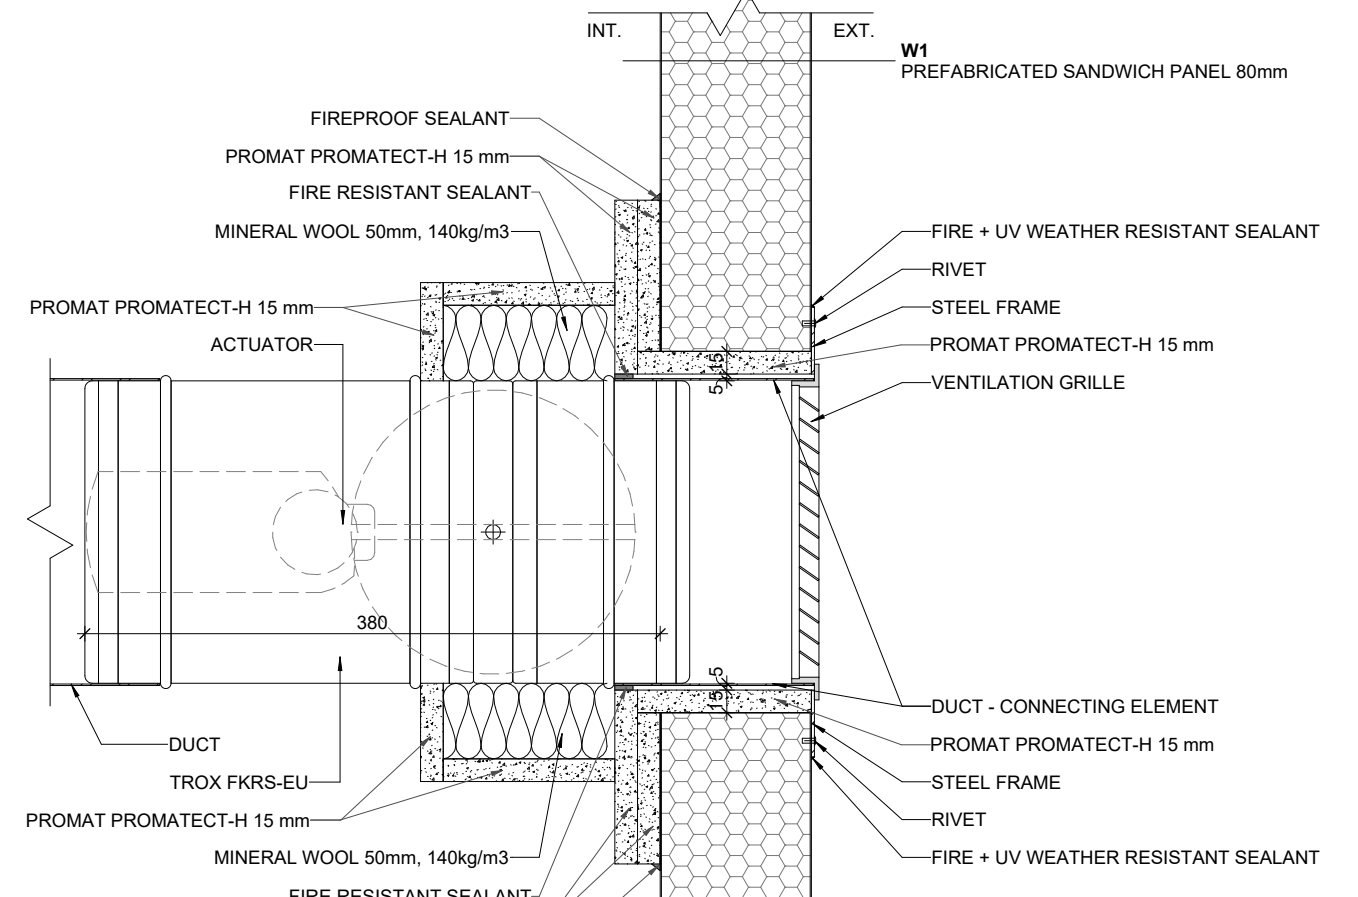


VERTICAL VIEW

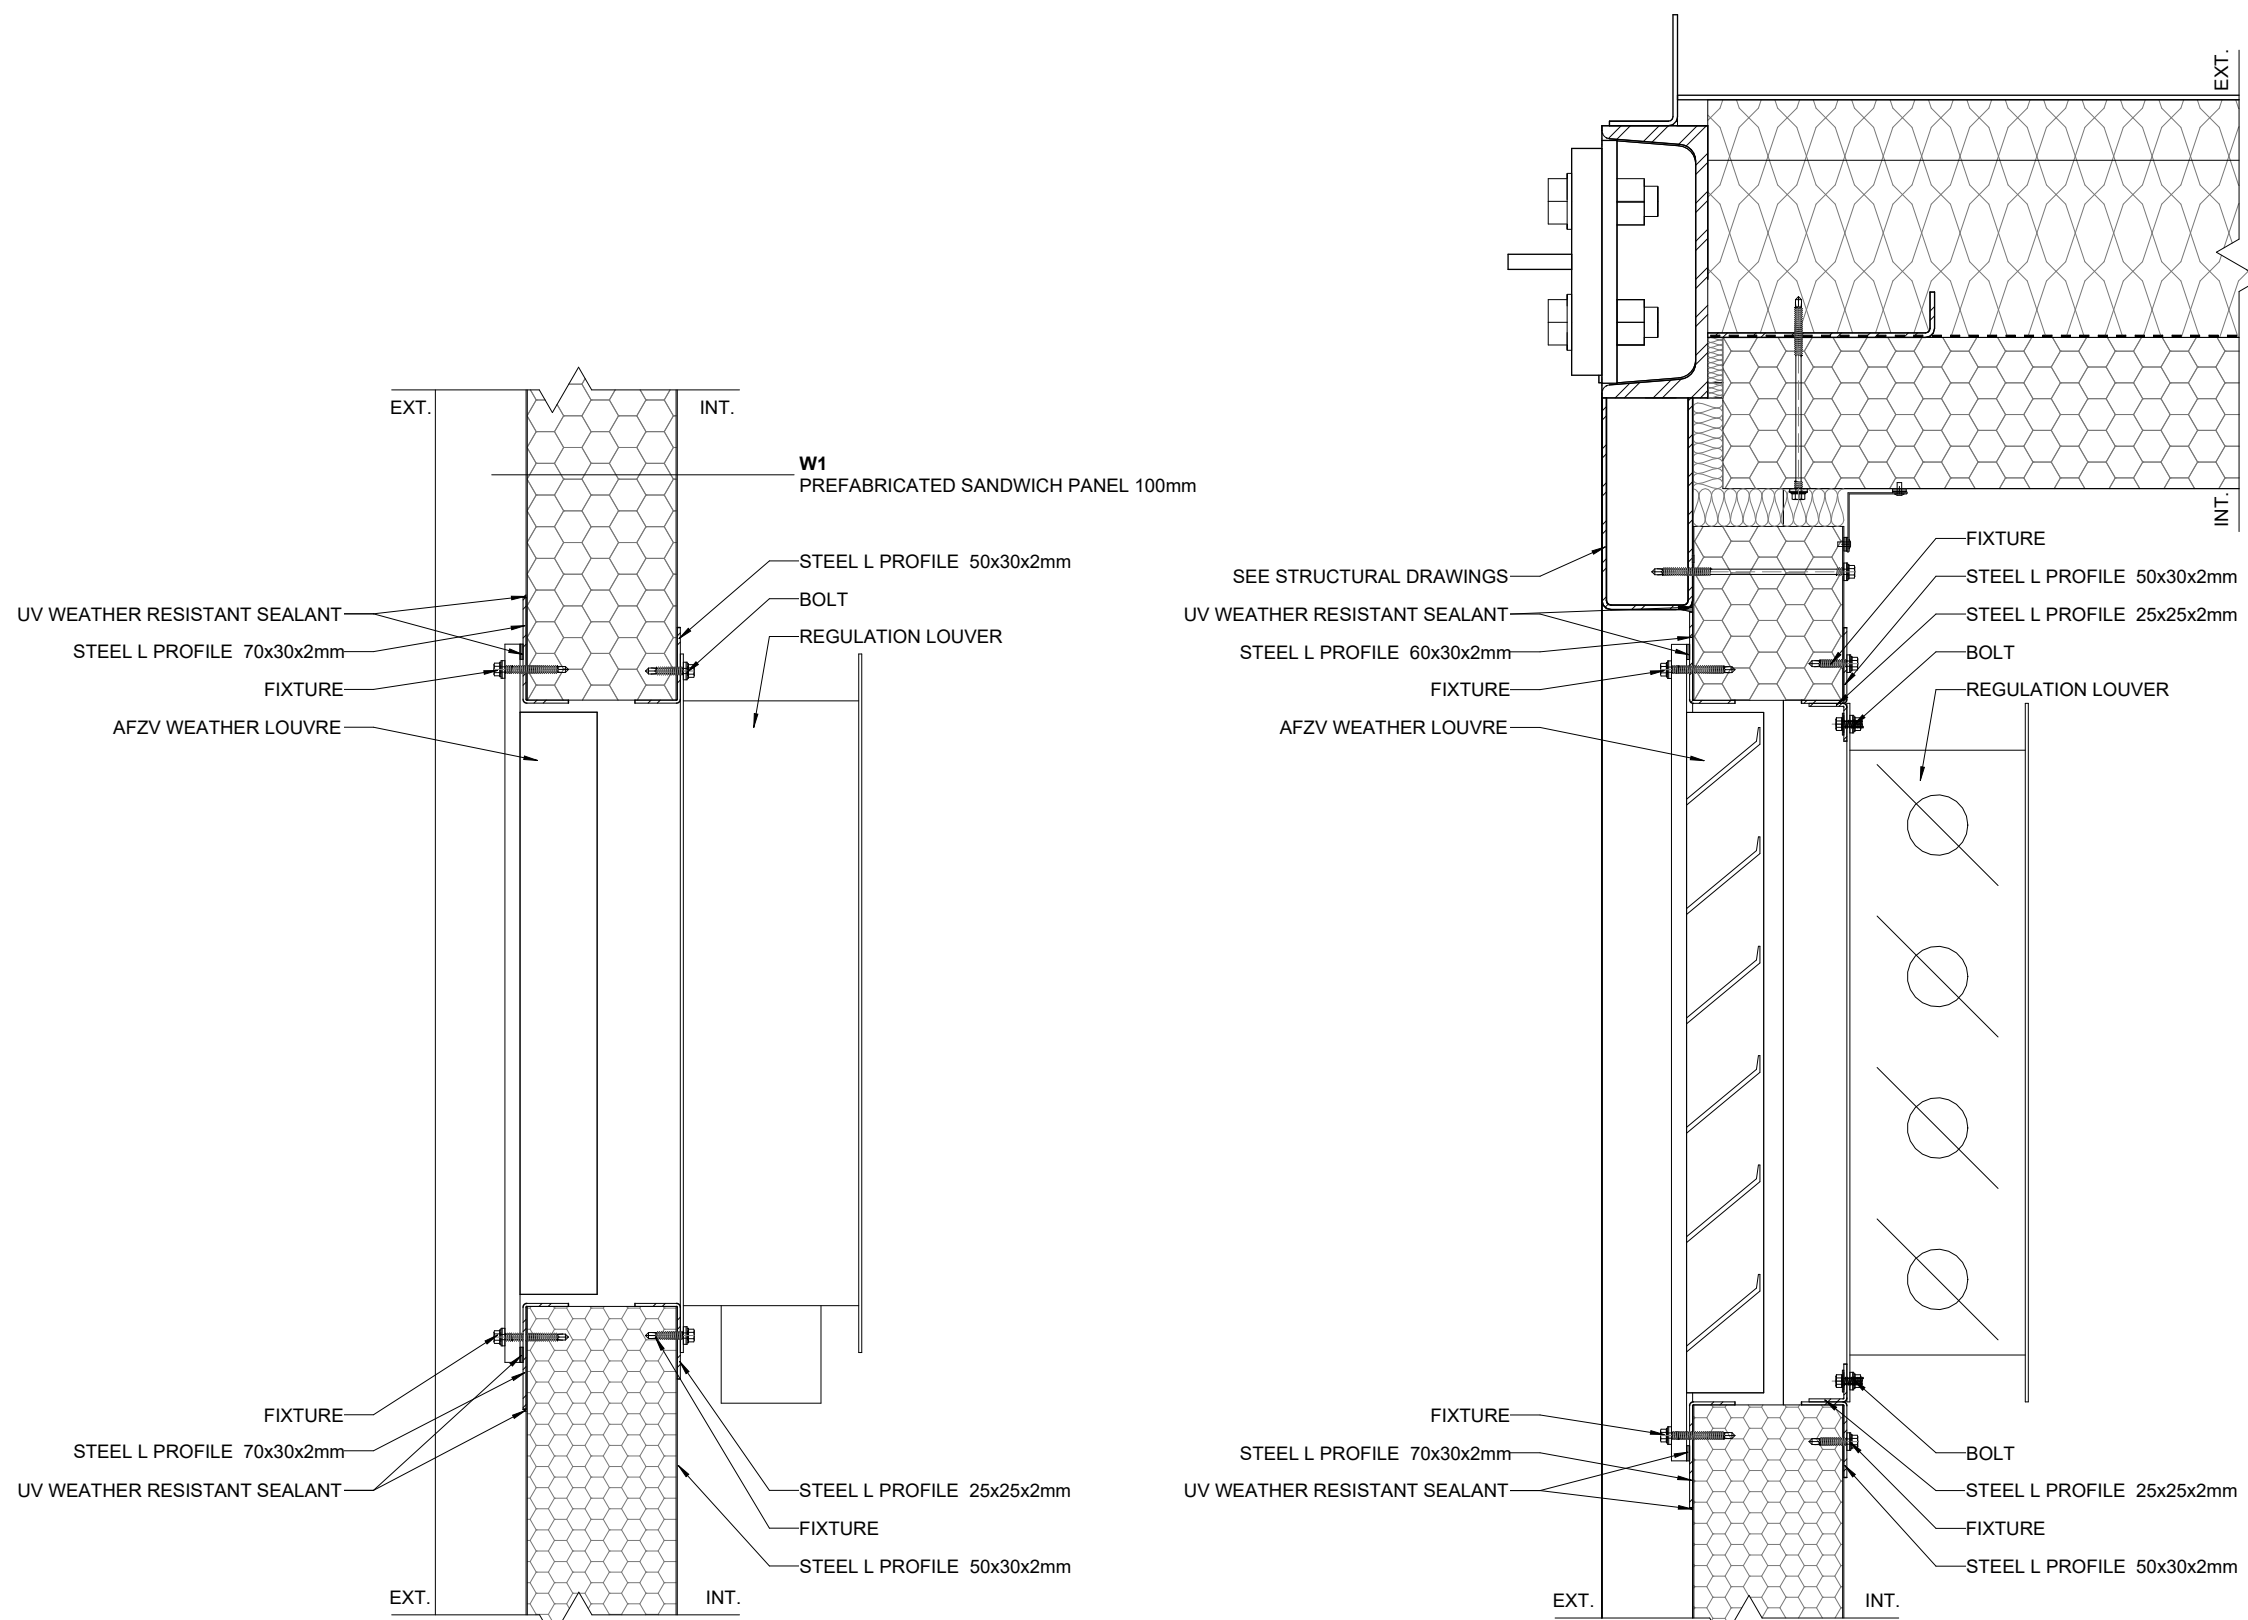


HORIZONTAL VIEW

VERTICAL VIEW


P11 AFZV WEATHER LOUVRE + REGULATION LOUVRE
1:5

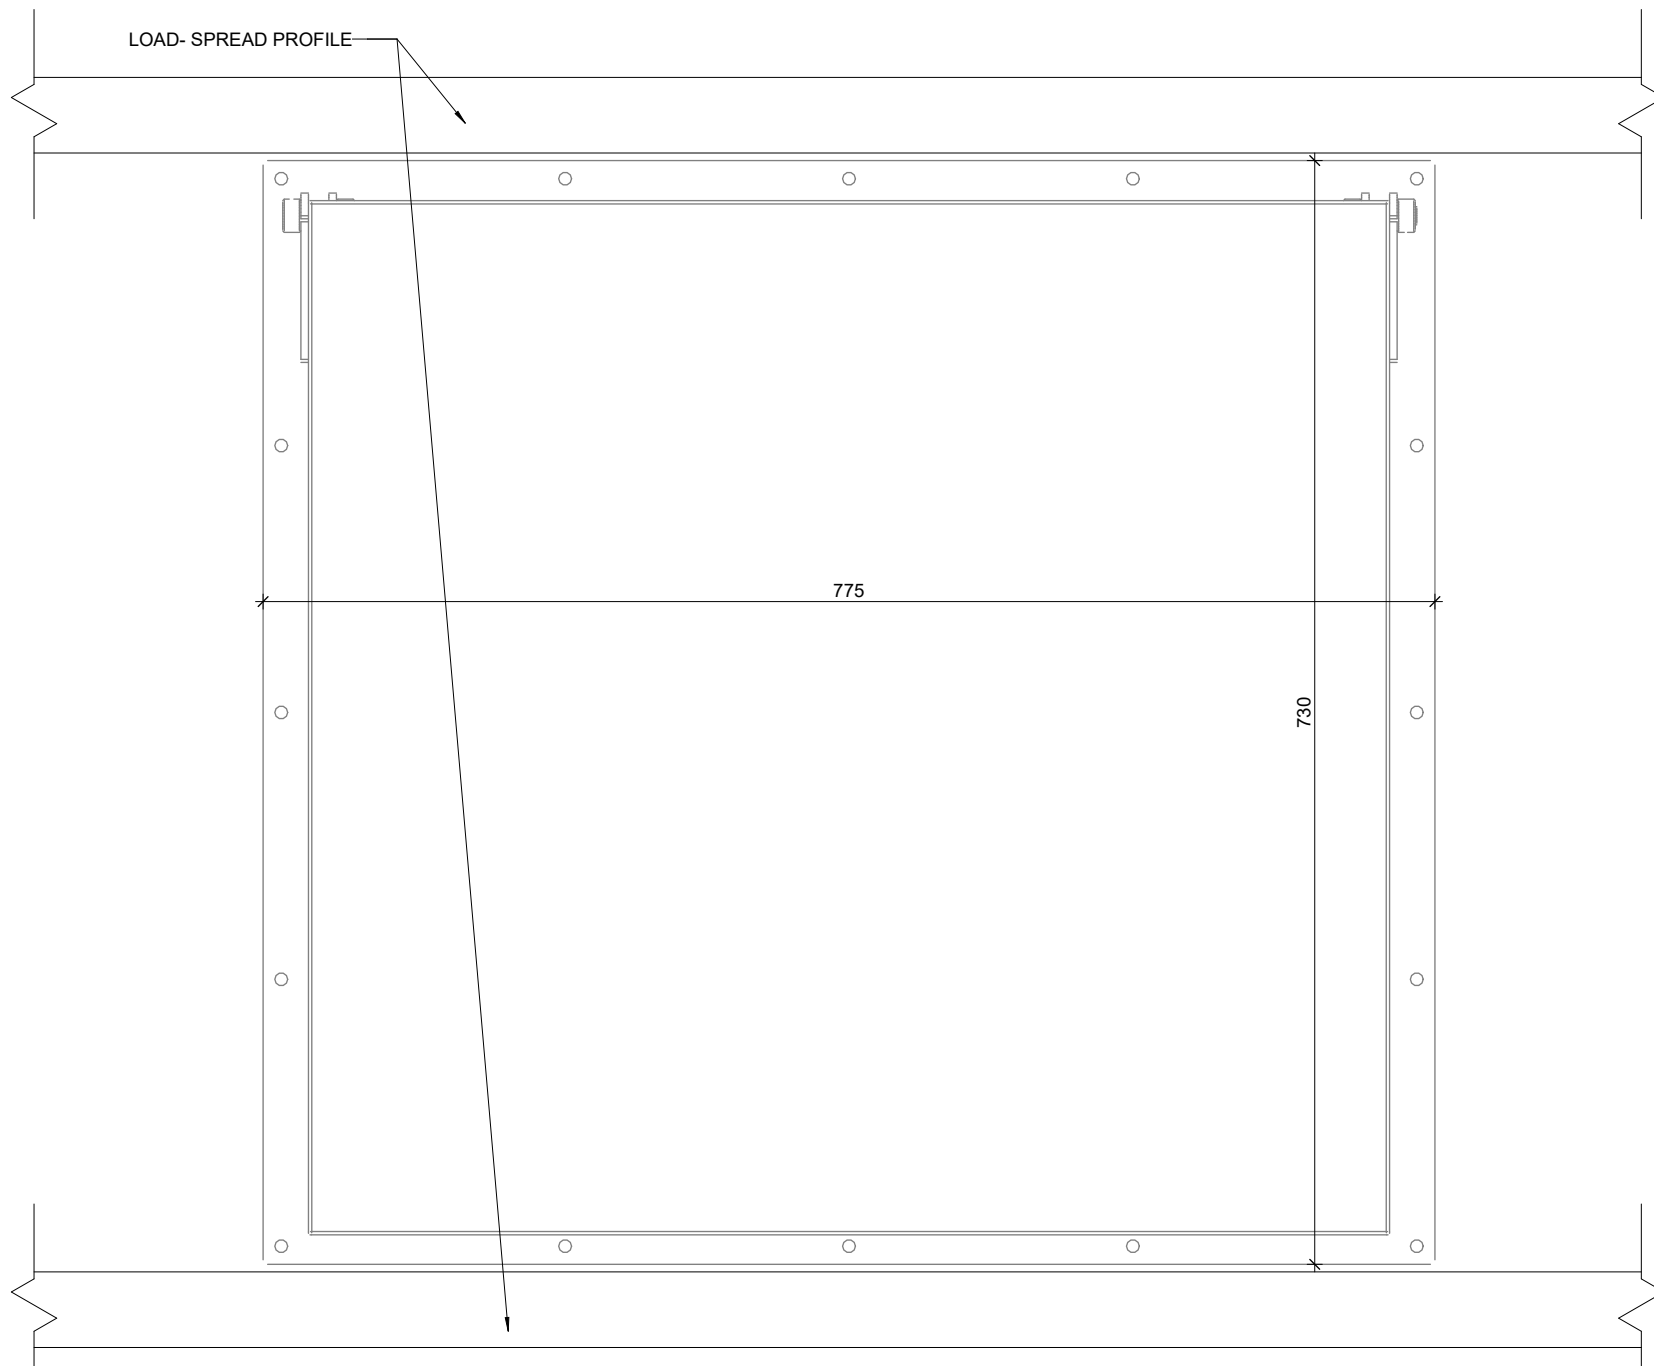


EXTERIOR ELEVATION

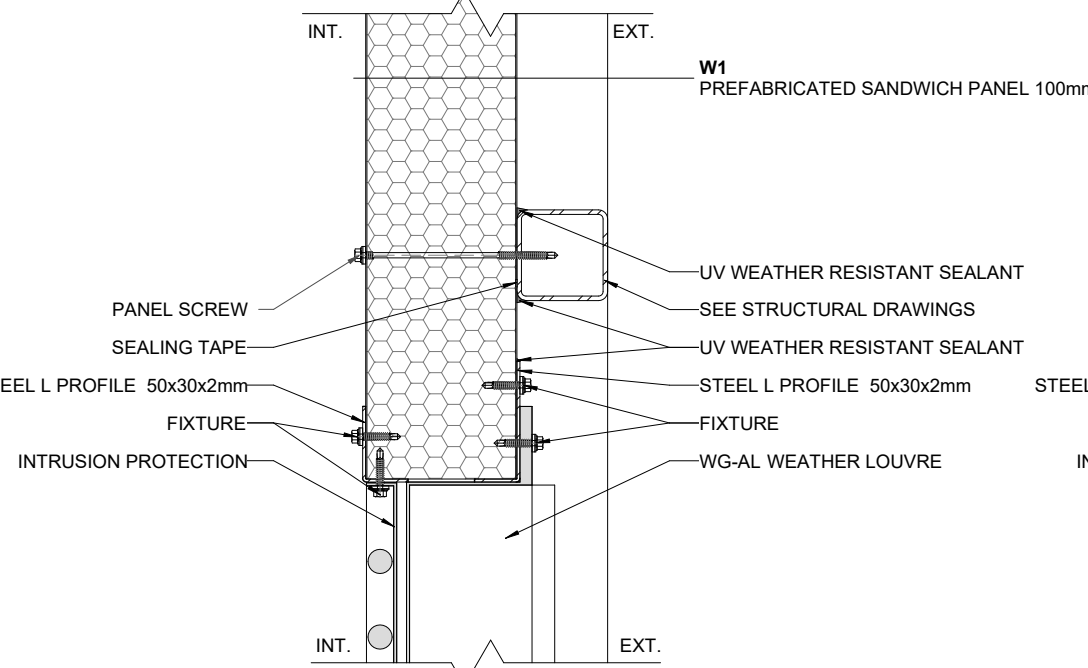


HORIZONTAL VIEW

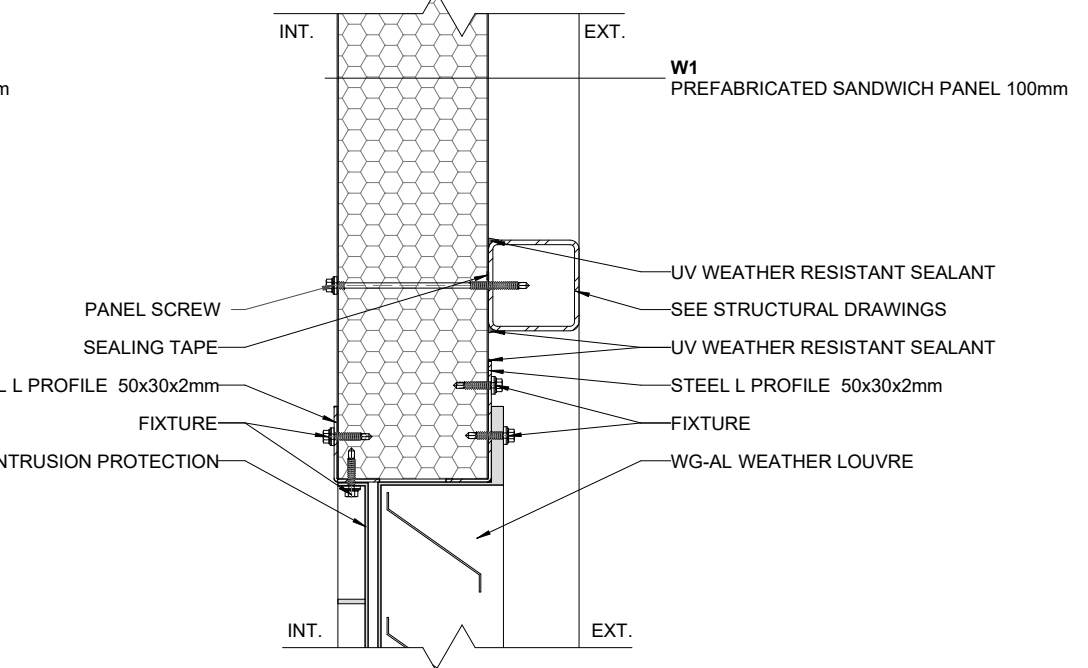

VERTICAL VIEW

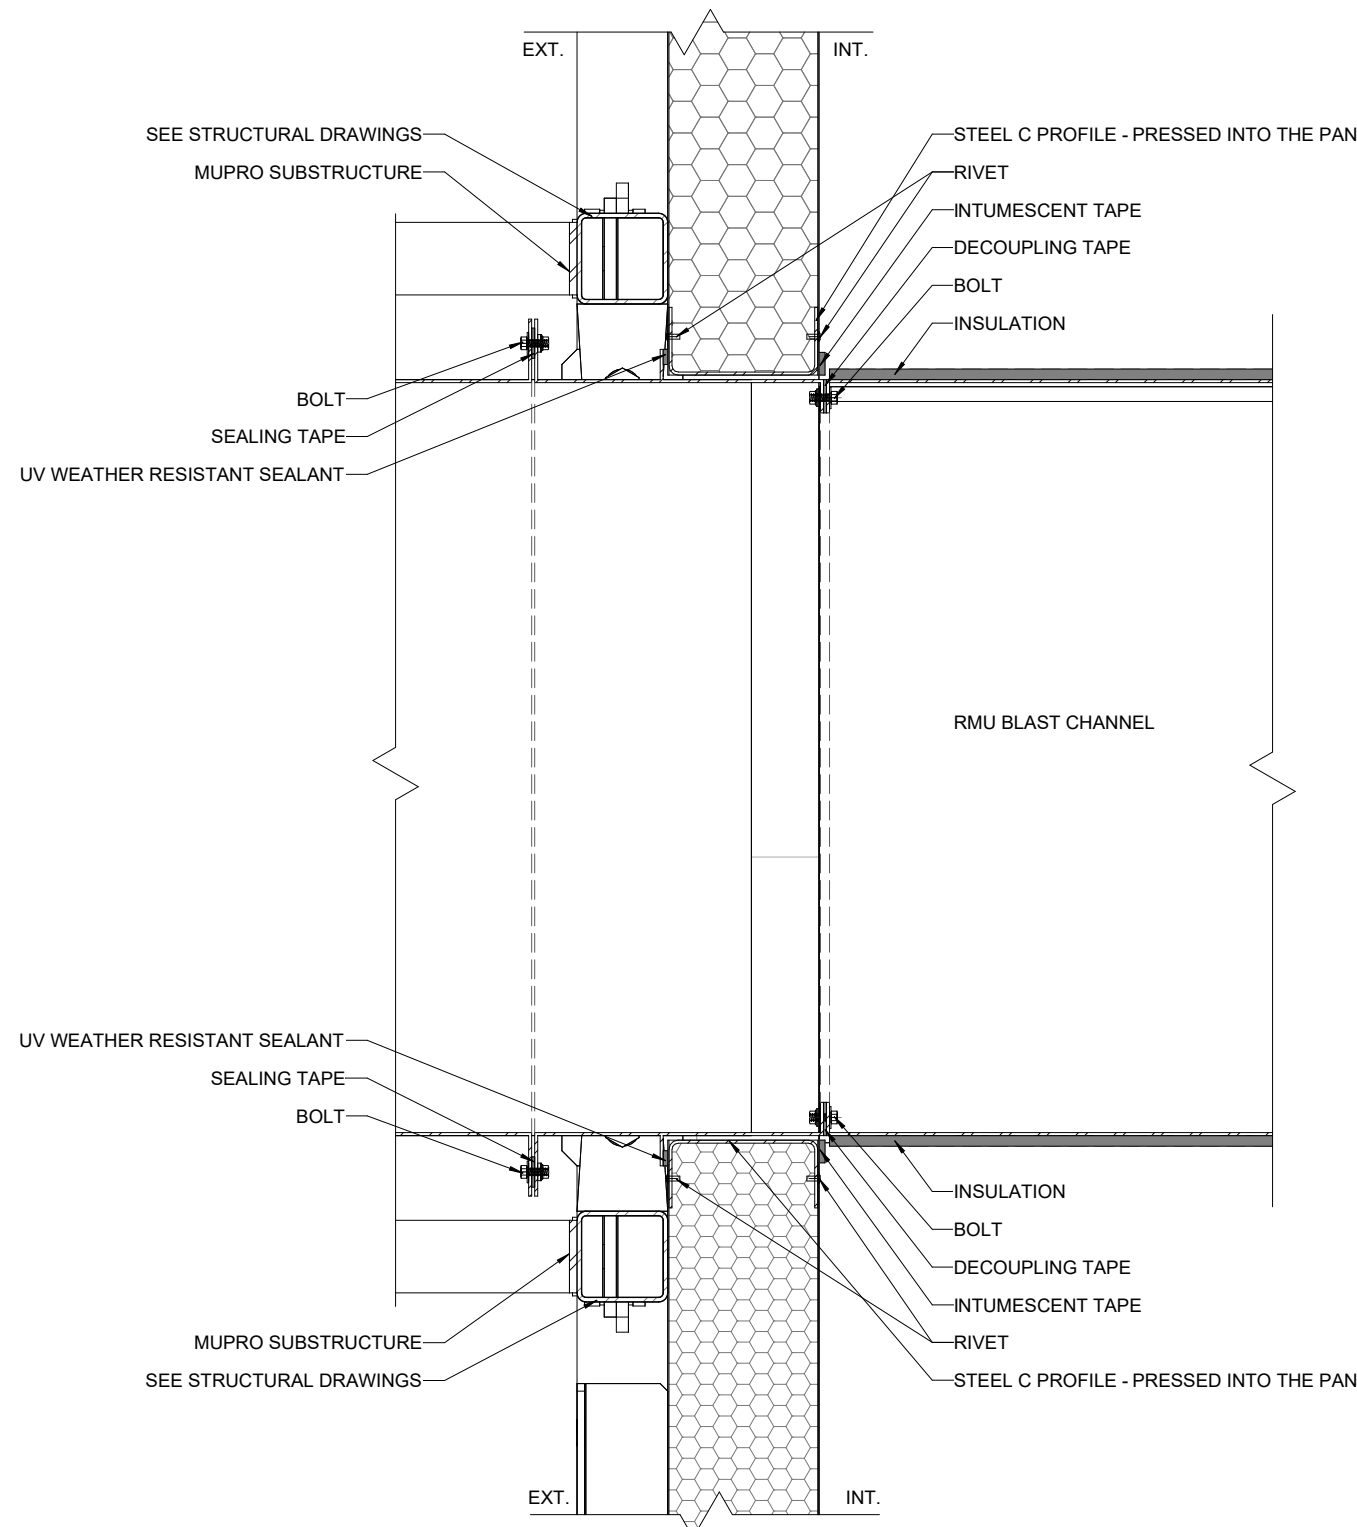


P13 RMU ARC BLAST
1:5

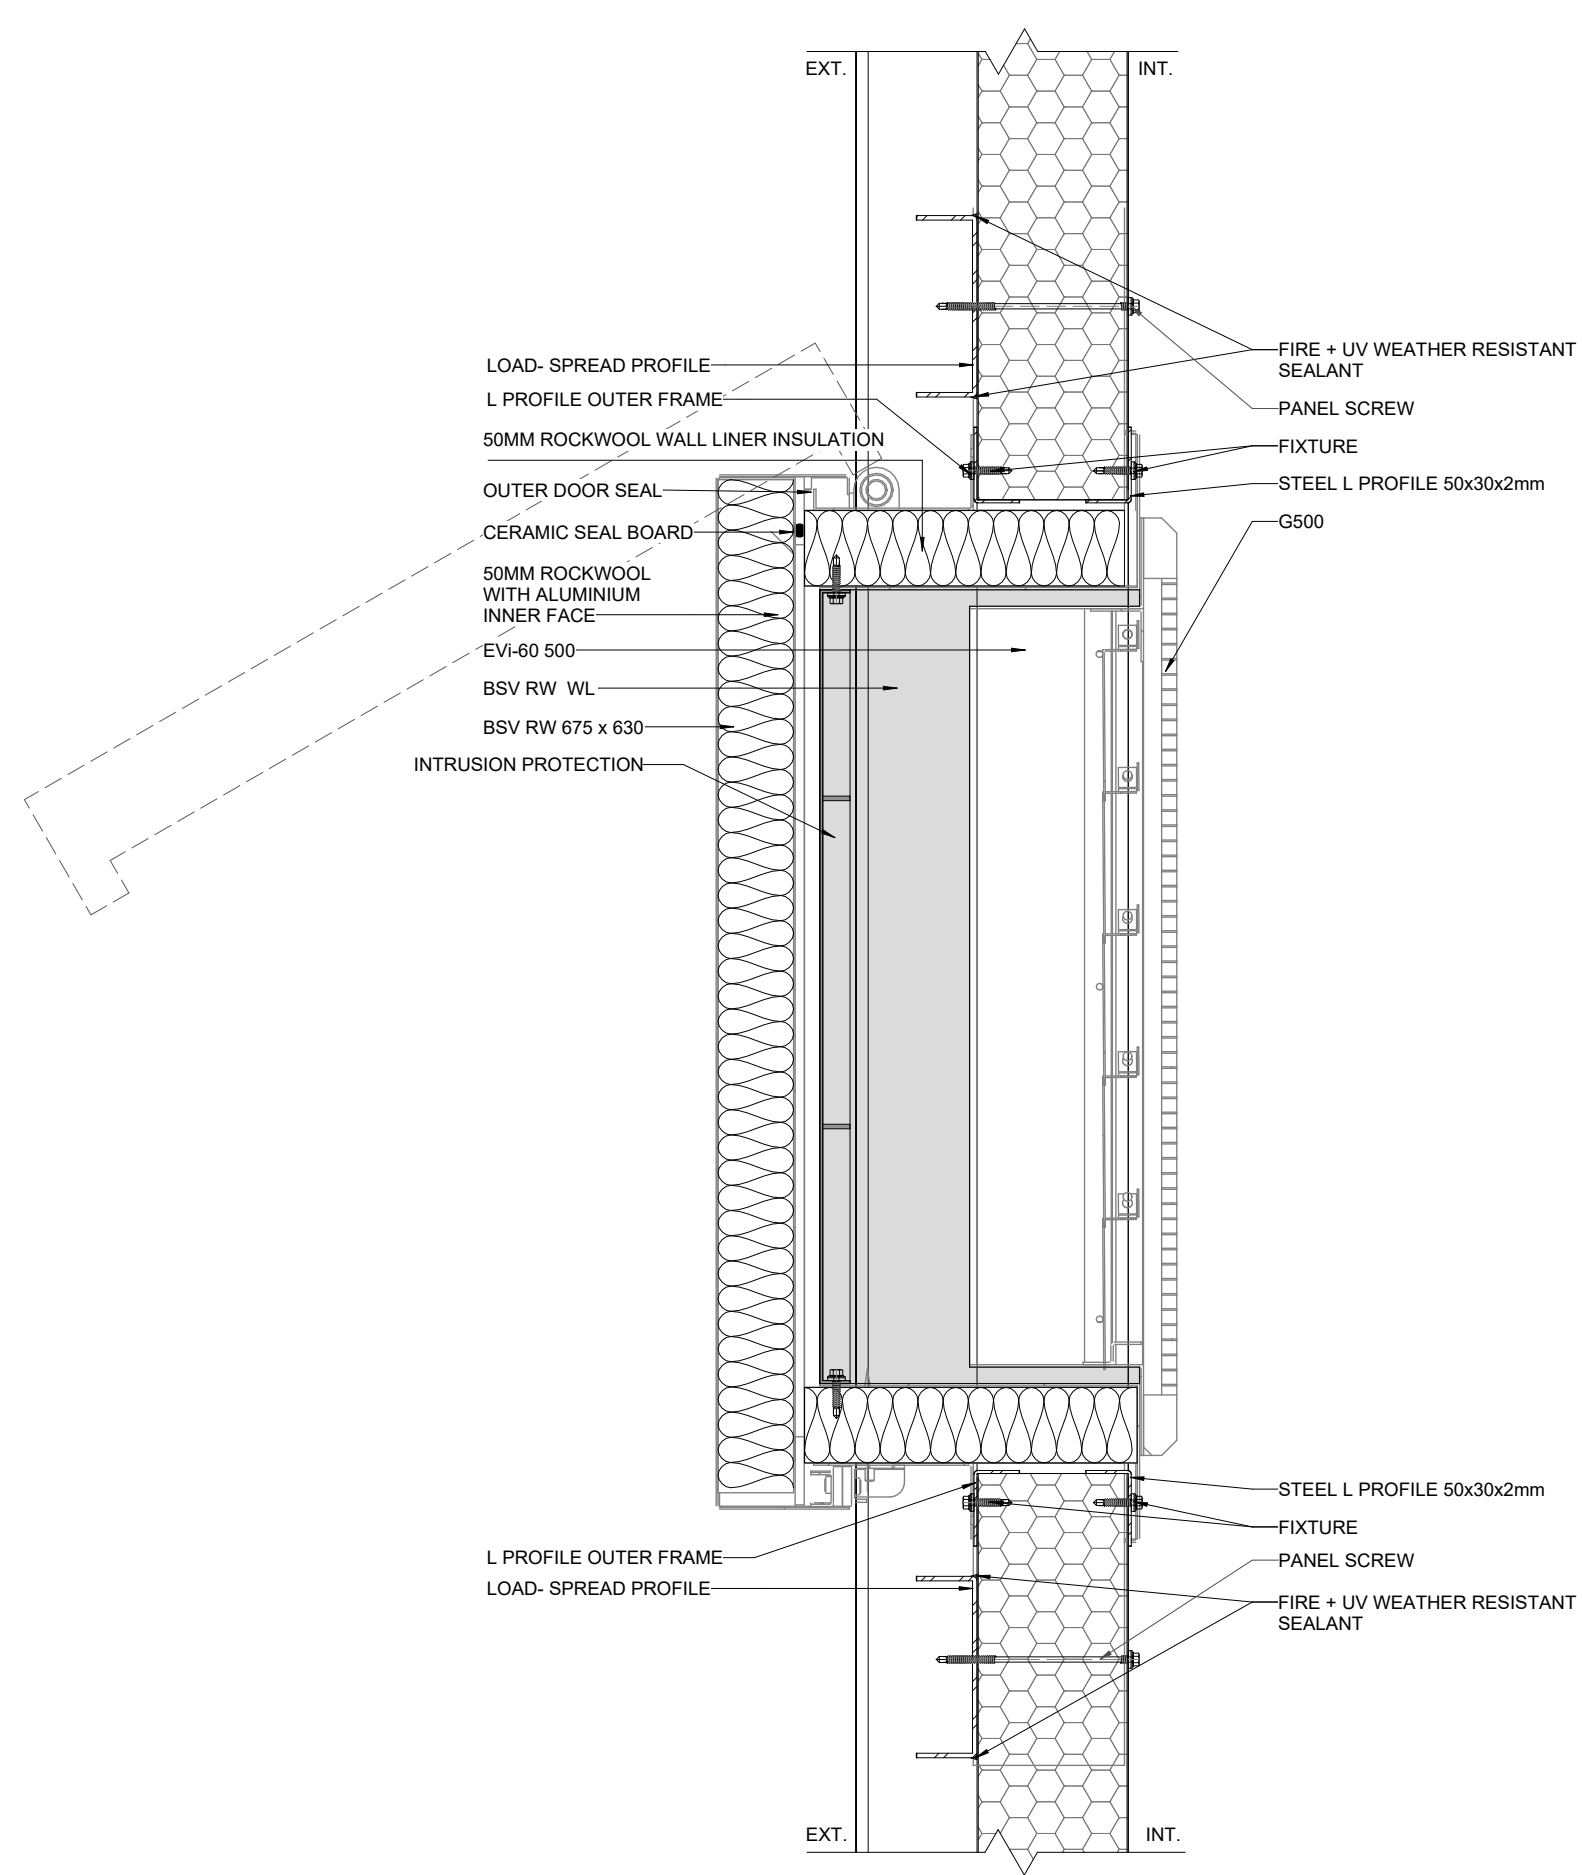


VERTICAL VIEW


P10b BSV + EVI500 + SGHD
1:5

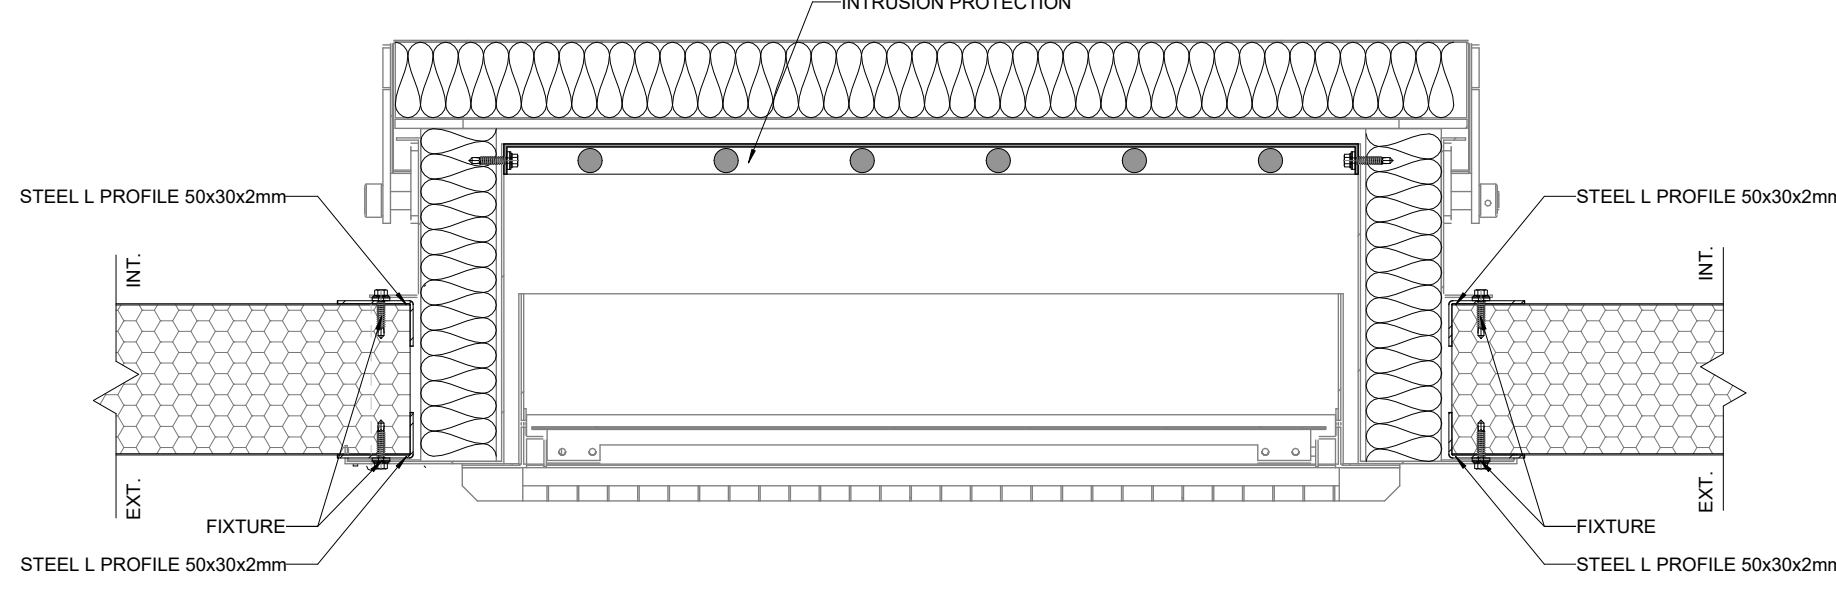

HORIZONTAL VIEW

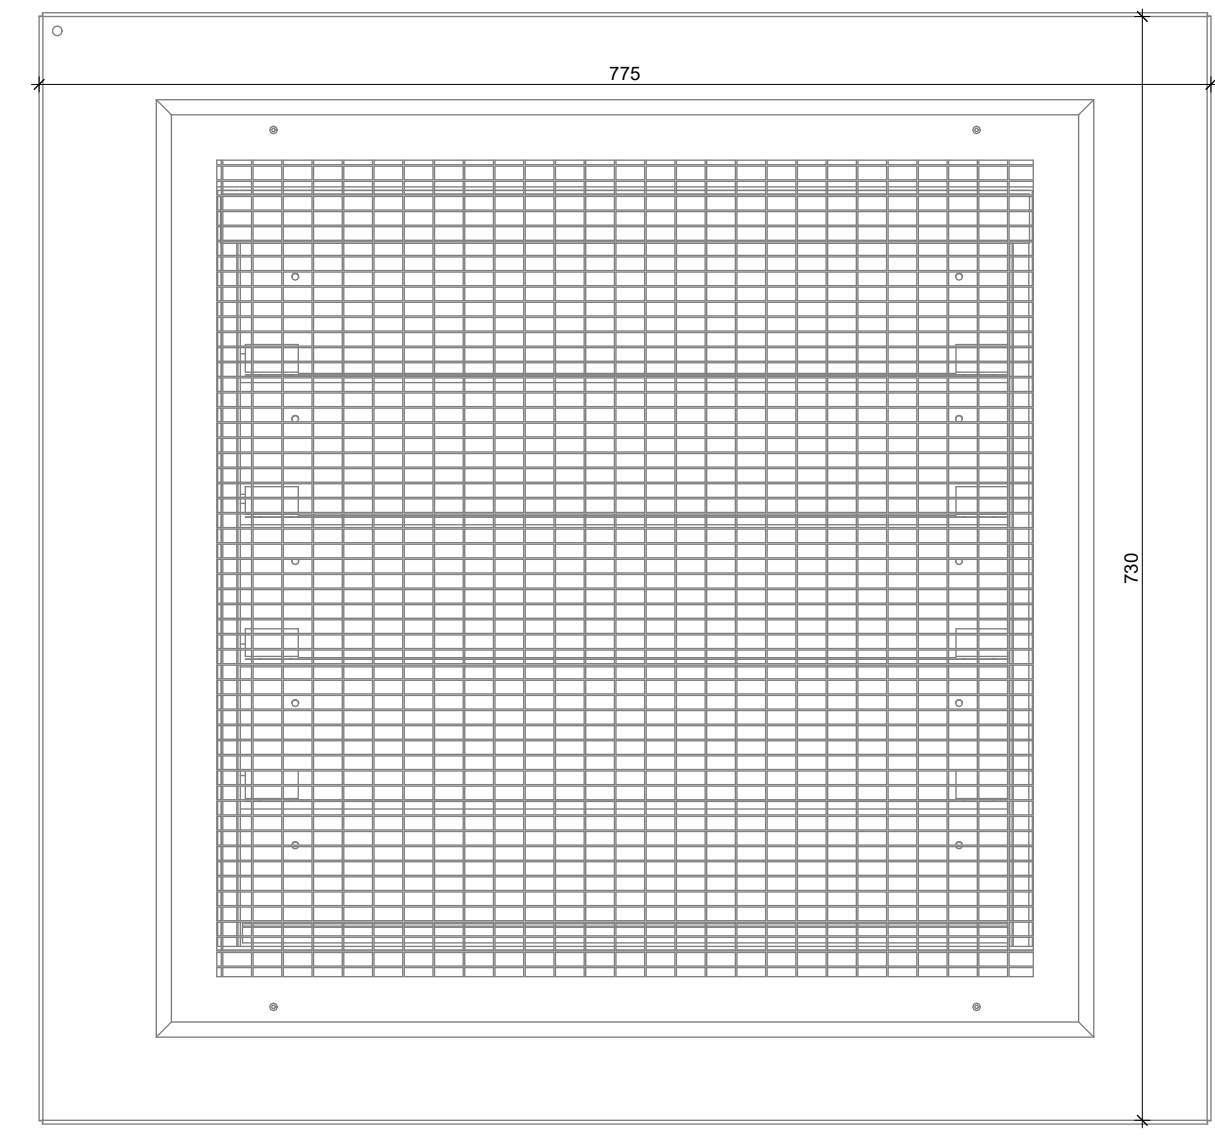

INTERIOR ELEVATION

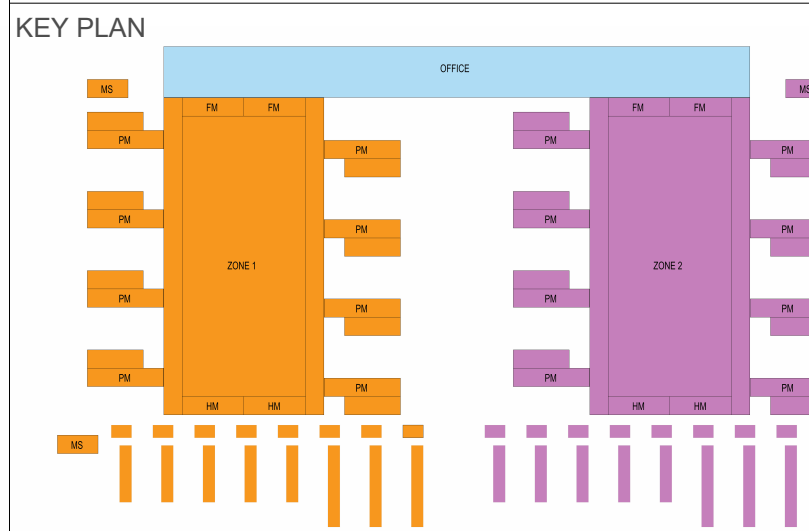

KEY PLAN

R01 CD SET - FOR INFORMATION 2026-07-24

REV. DESCRIPTION DATE



PROJECT NAME

ECO DC MONALISA

DRAWING NAME

ARCHITECTURAL DETAILS
- PREFABRICATED MODULES
- PENETRATIONS EXTERNAL - PM - MV - MS

PREPARED (ALSO SUBJECT RESPONSIBLE IF OTHER)

L. MAVREK / K. KOZINA

DOCUMENT RESPONSIBLE (APPROVED)

M. PACAK

LOAD (BIM SYSTEM) AUTODESK REVIT 2025

DOCUMENT NUMBER ECODC-VRT-MDC19-00-DR-A-50105

SHEET SIZE A0

DRAWING SCALE 1:5

DATE (YYYYMMDD) 2026-07-24

REVISION

R01

SHEET 1 OF 1