




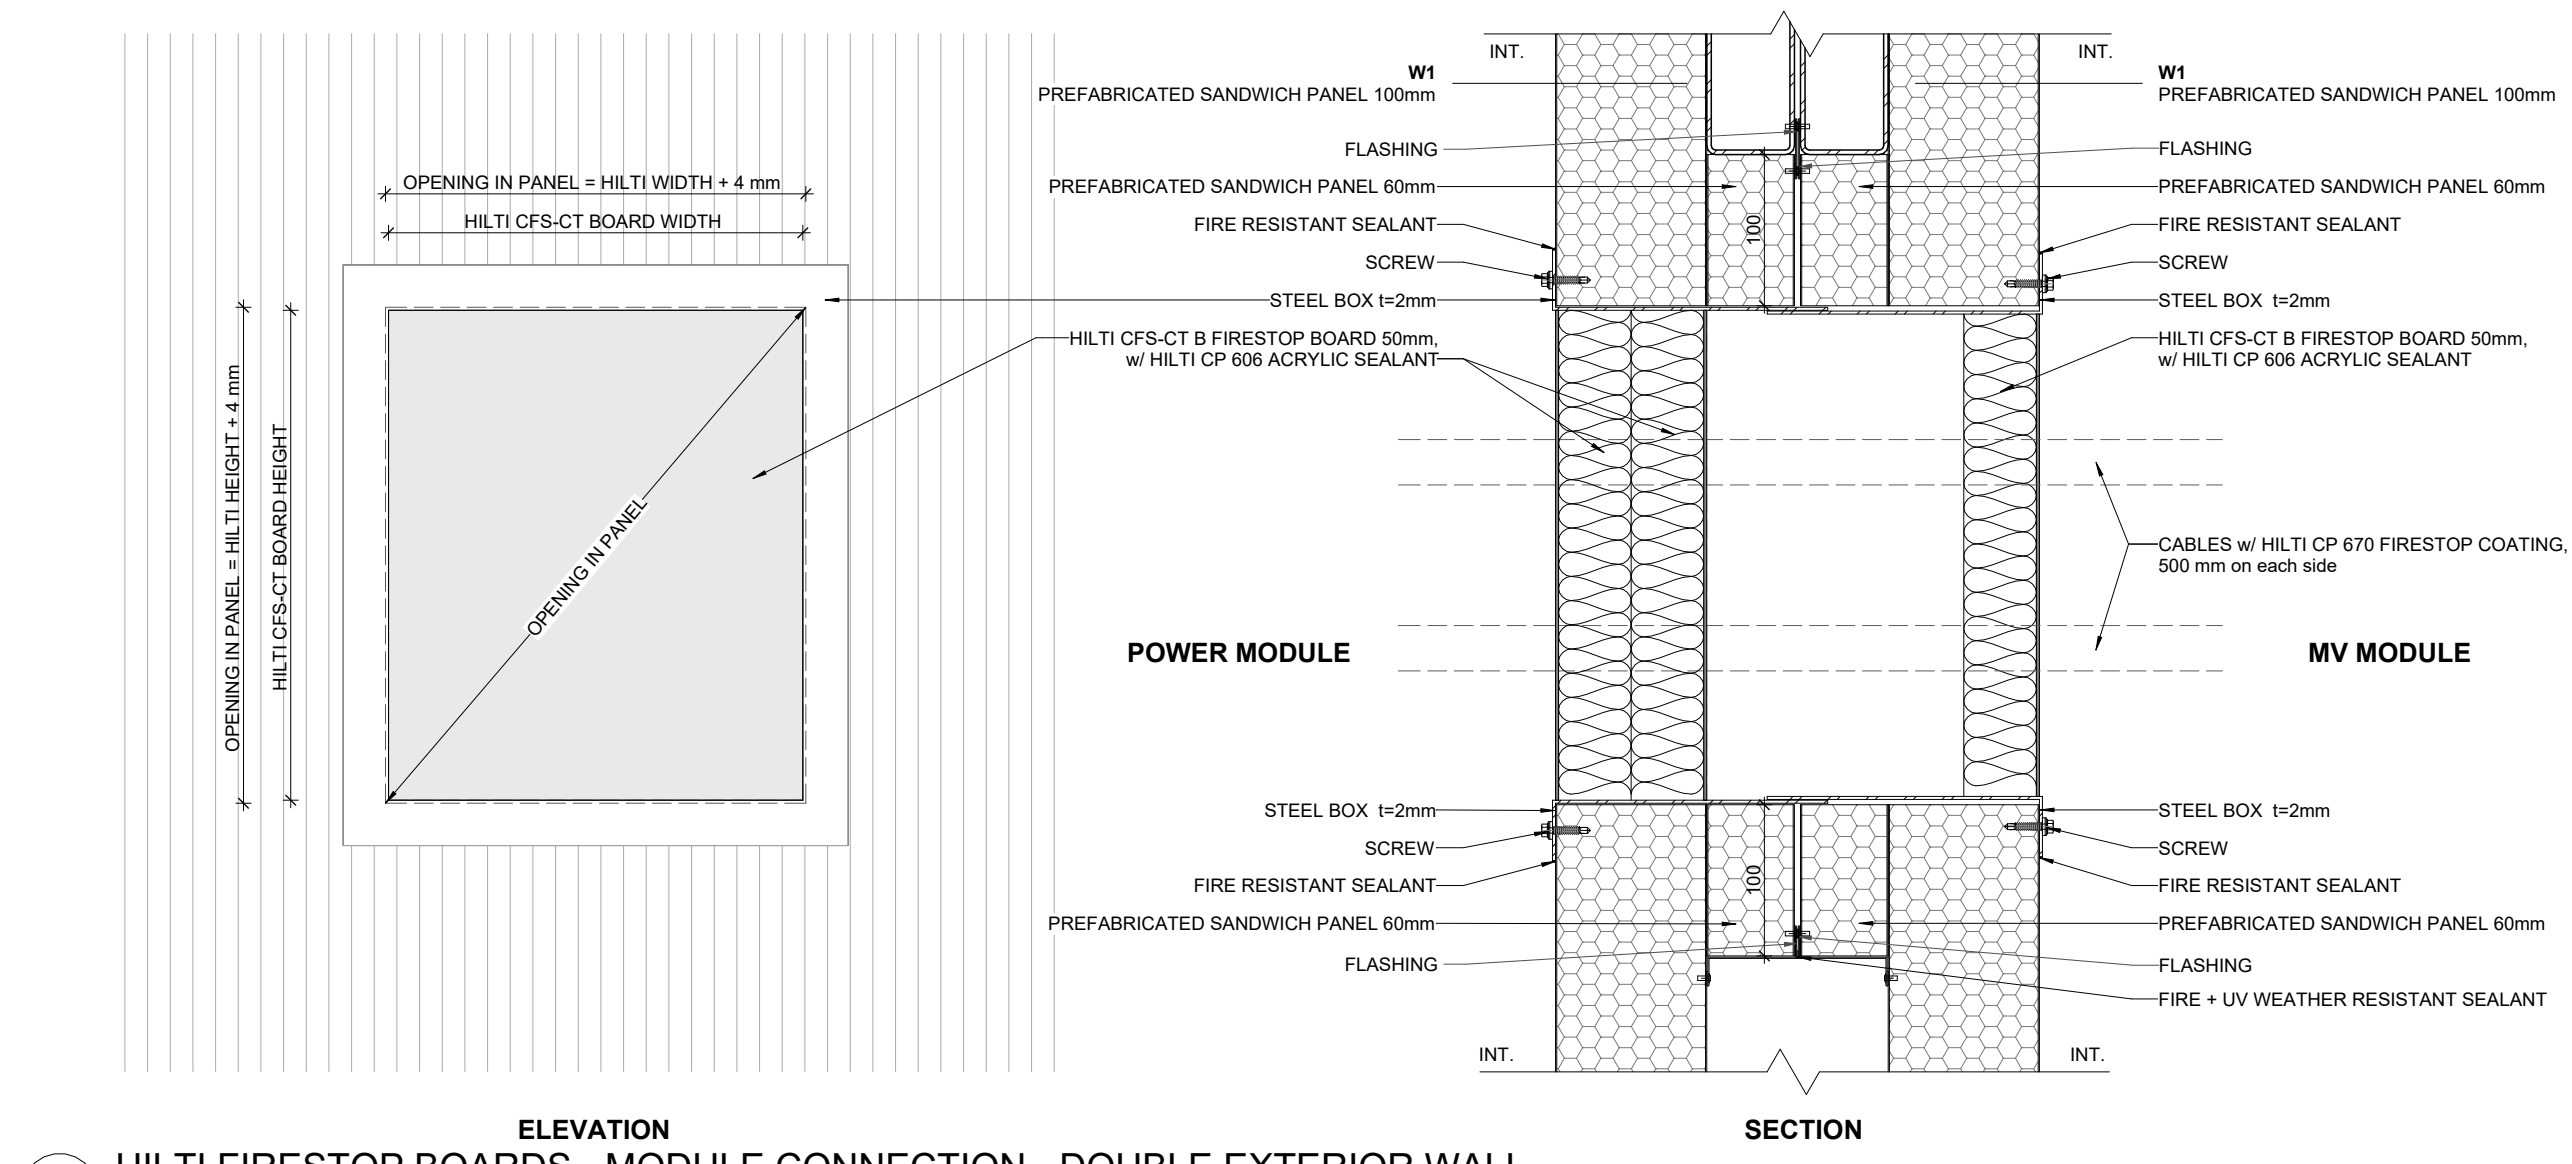


P04 HILTI FIRESTOP BOARDS - MODULE CONNECTION - DOUBLE EXTERIOR WALL
1:5

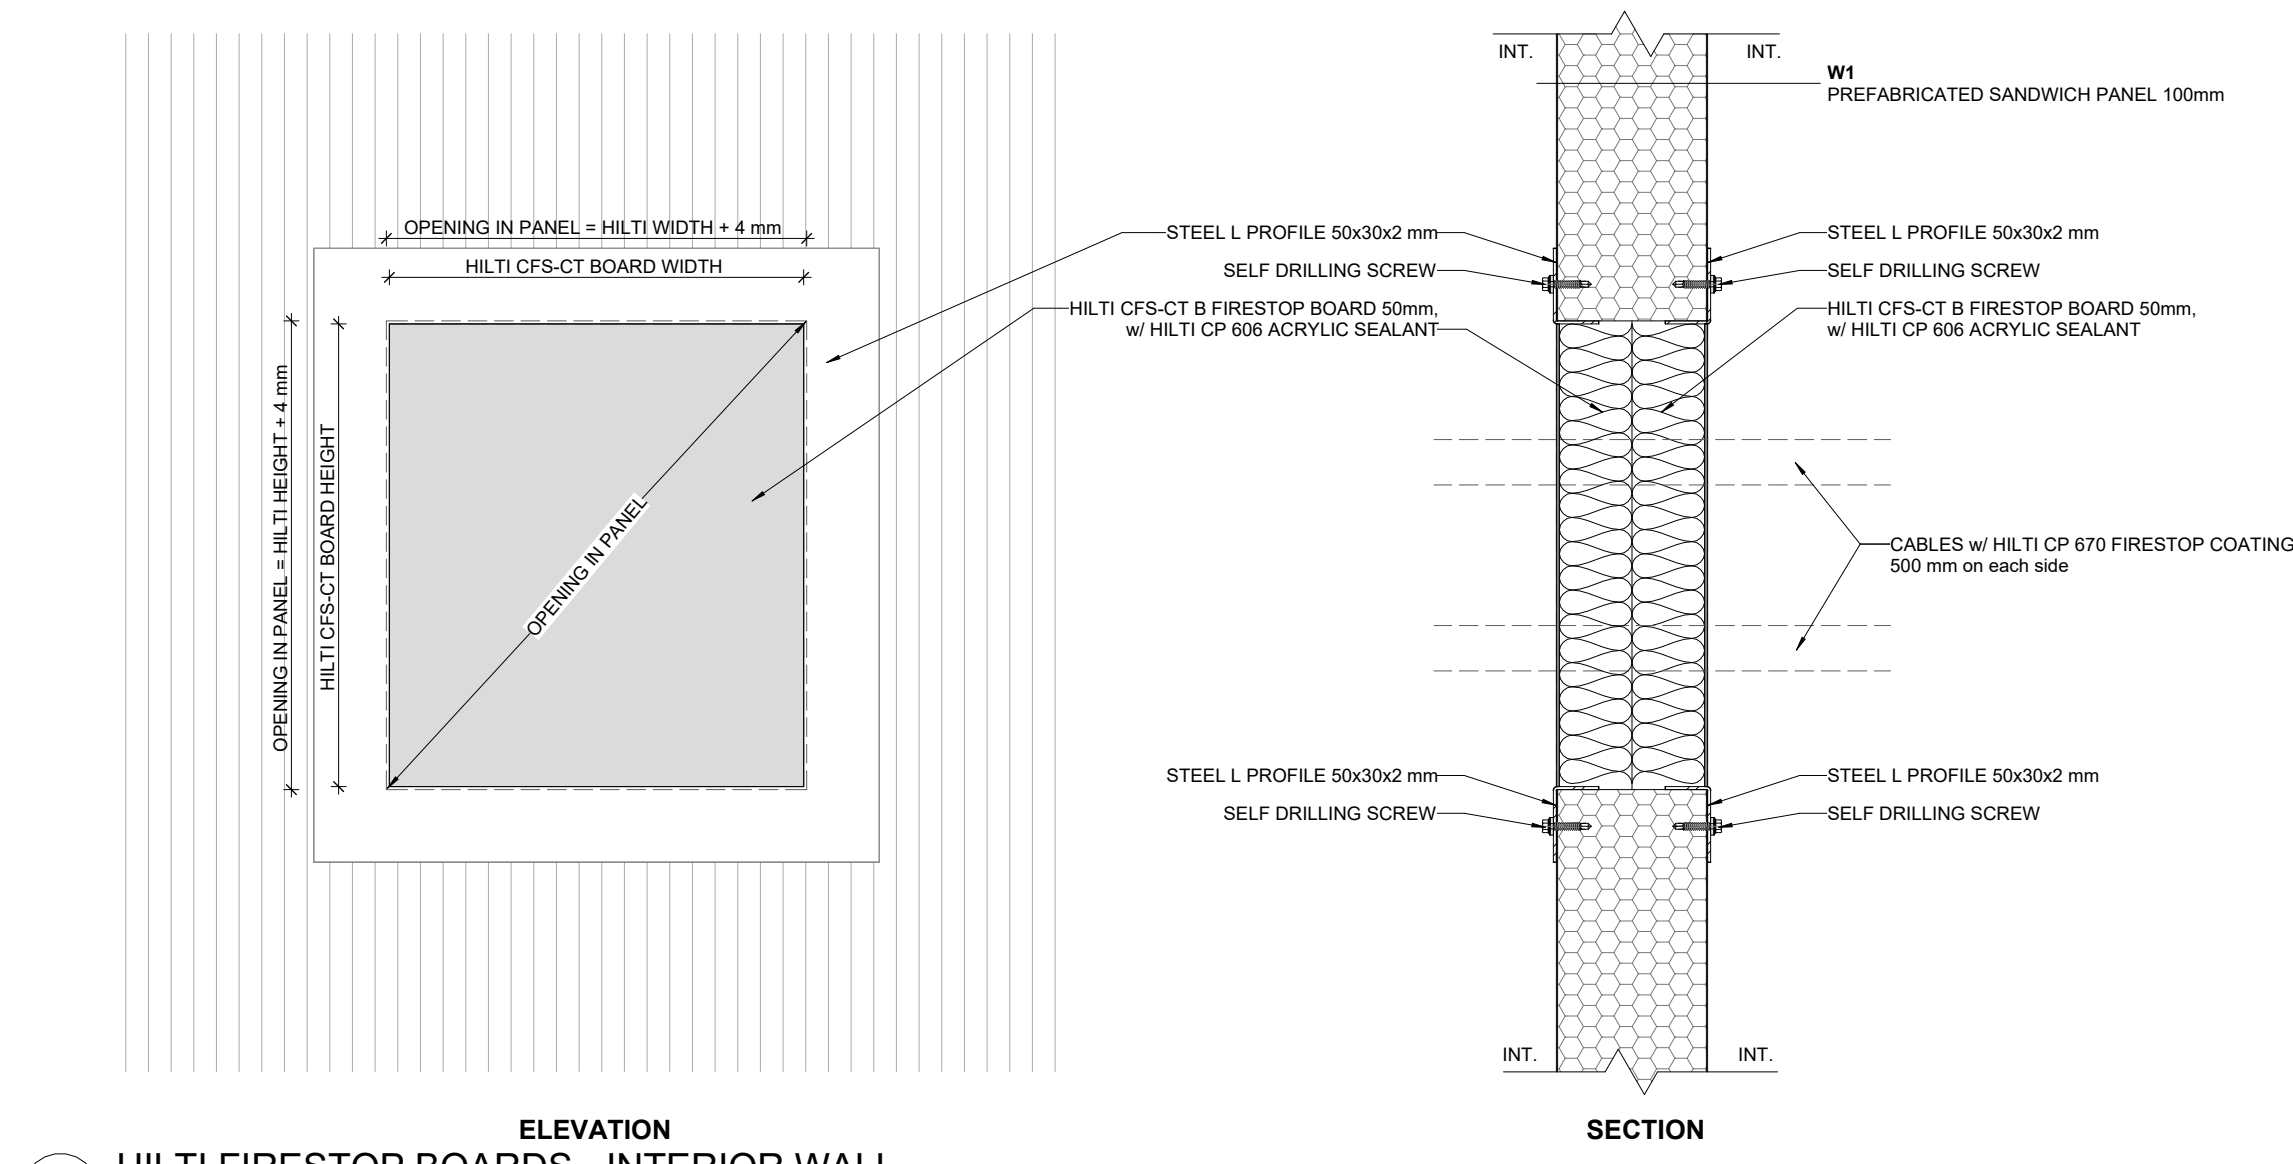


P05 HILTI FIRESTOP BOARDS - INTERIOR WALL
1:5

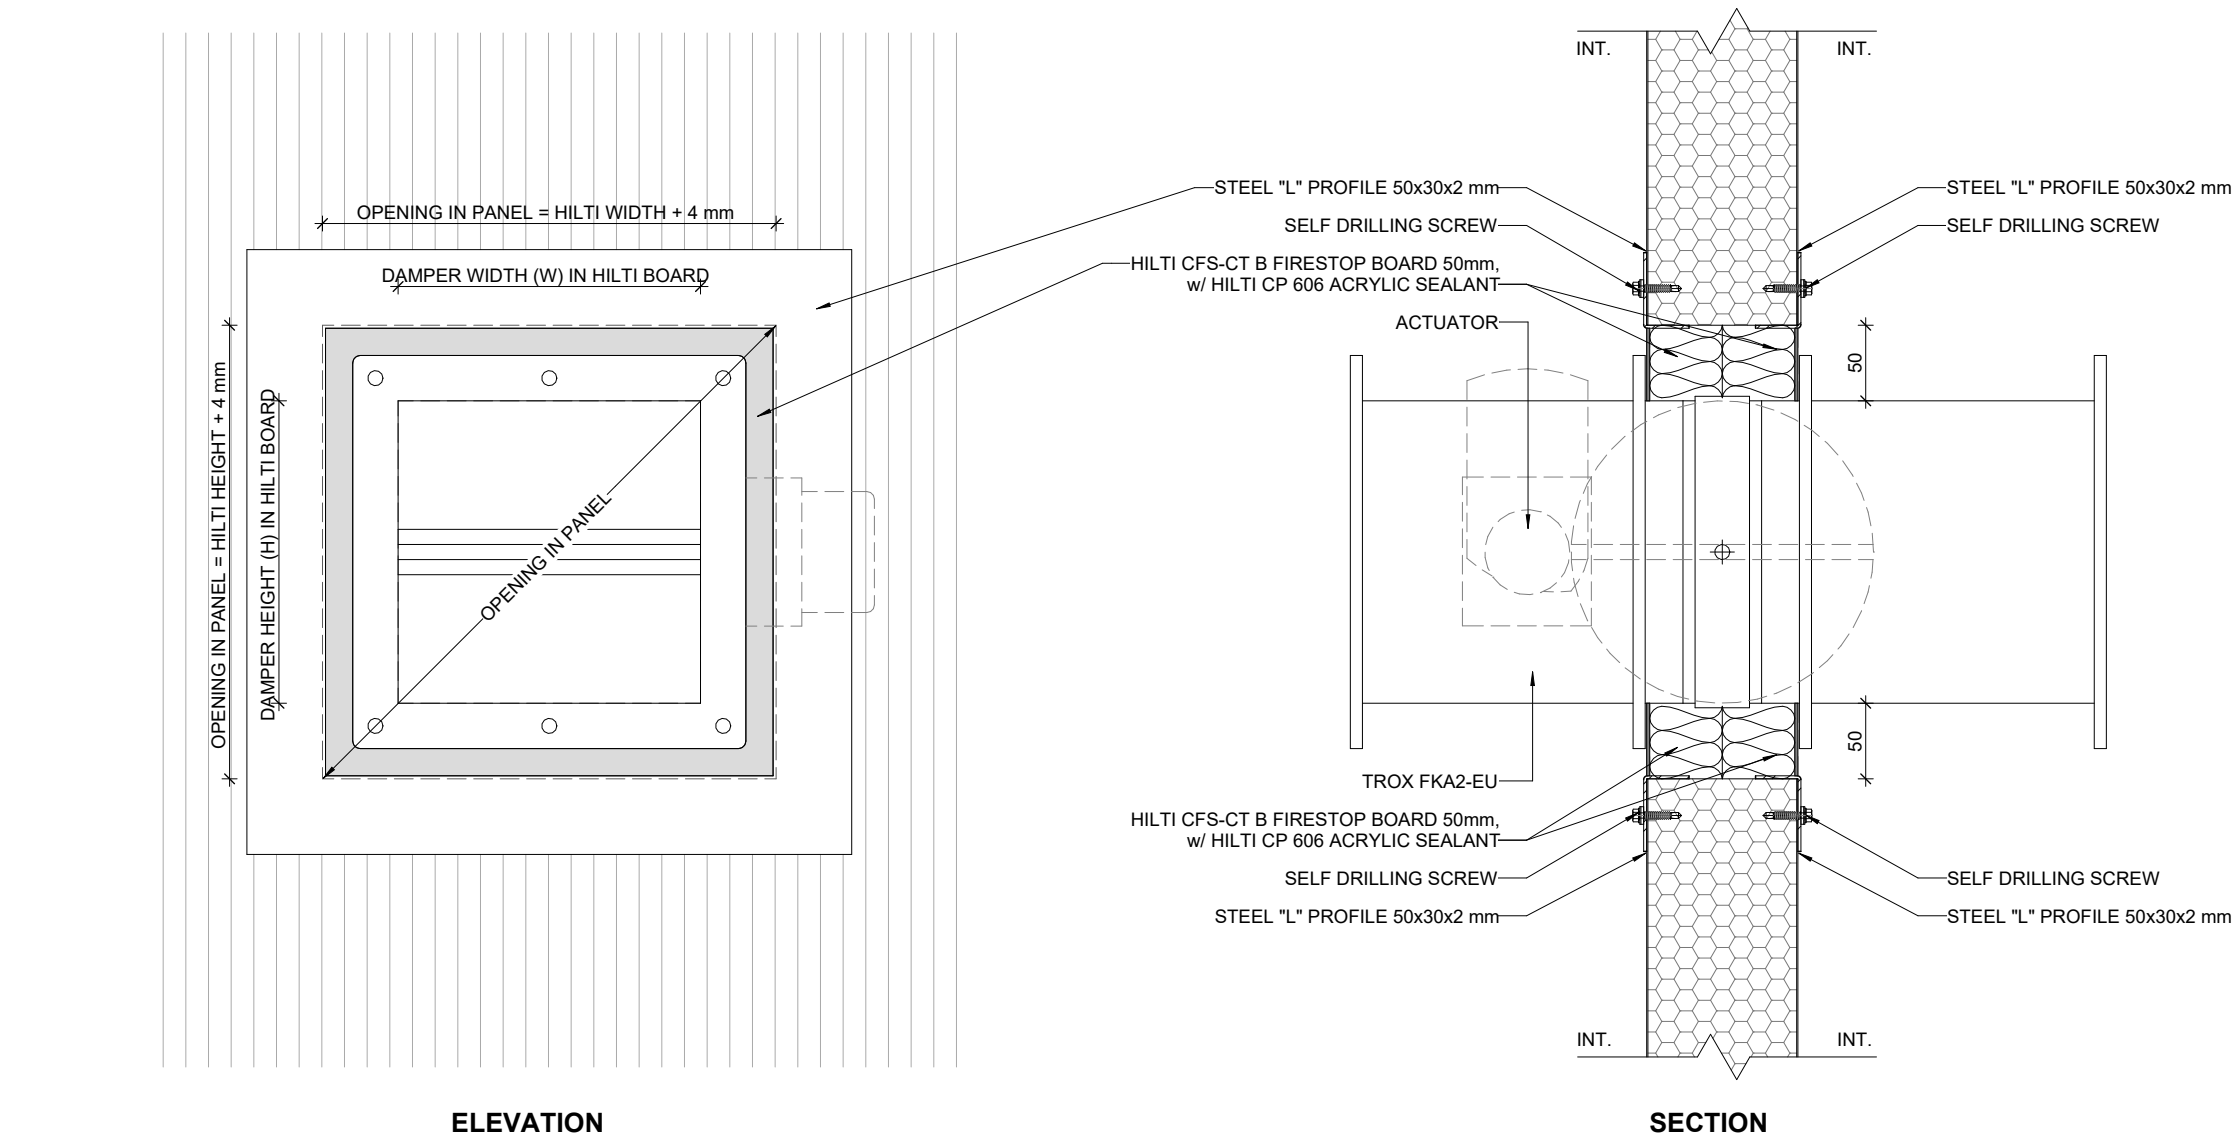


P07 TROX FKA2-EU
1:5

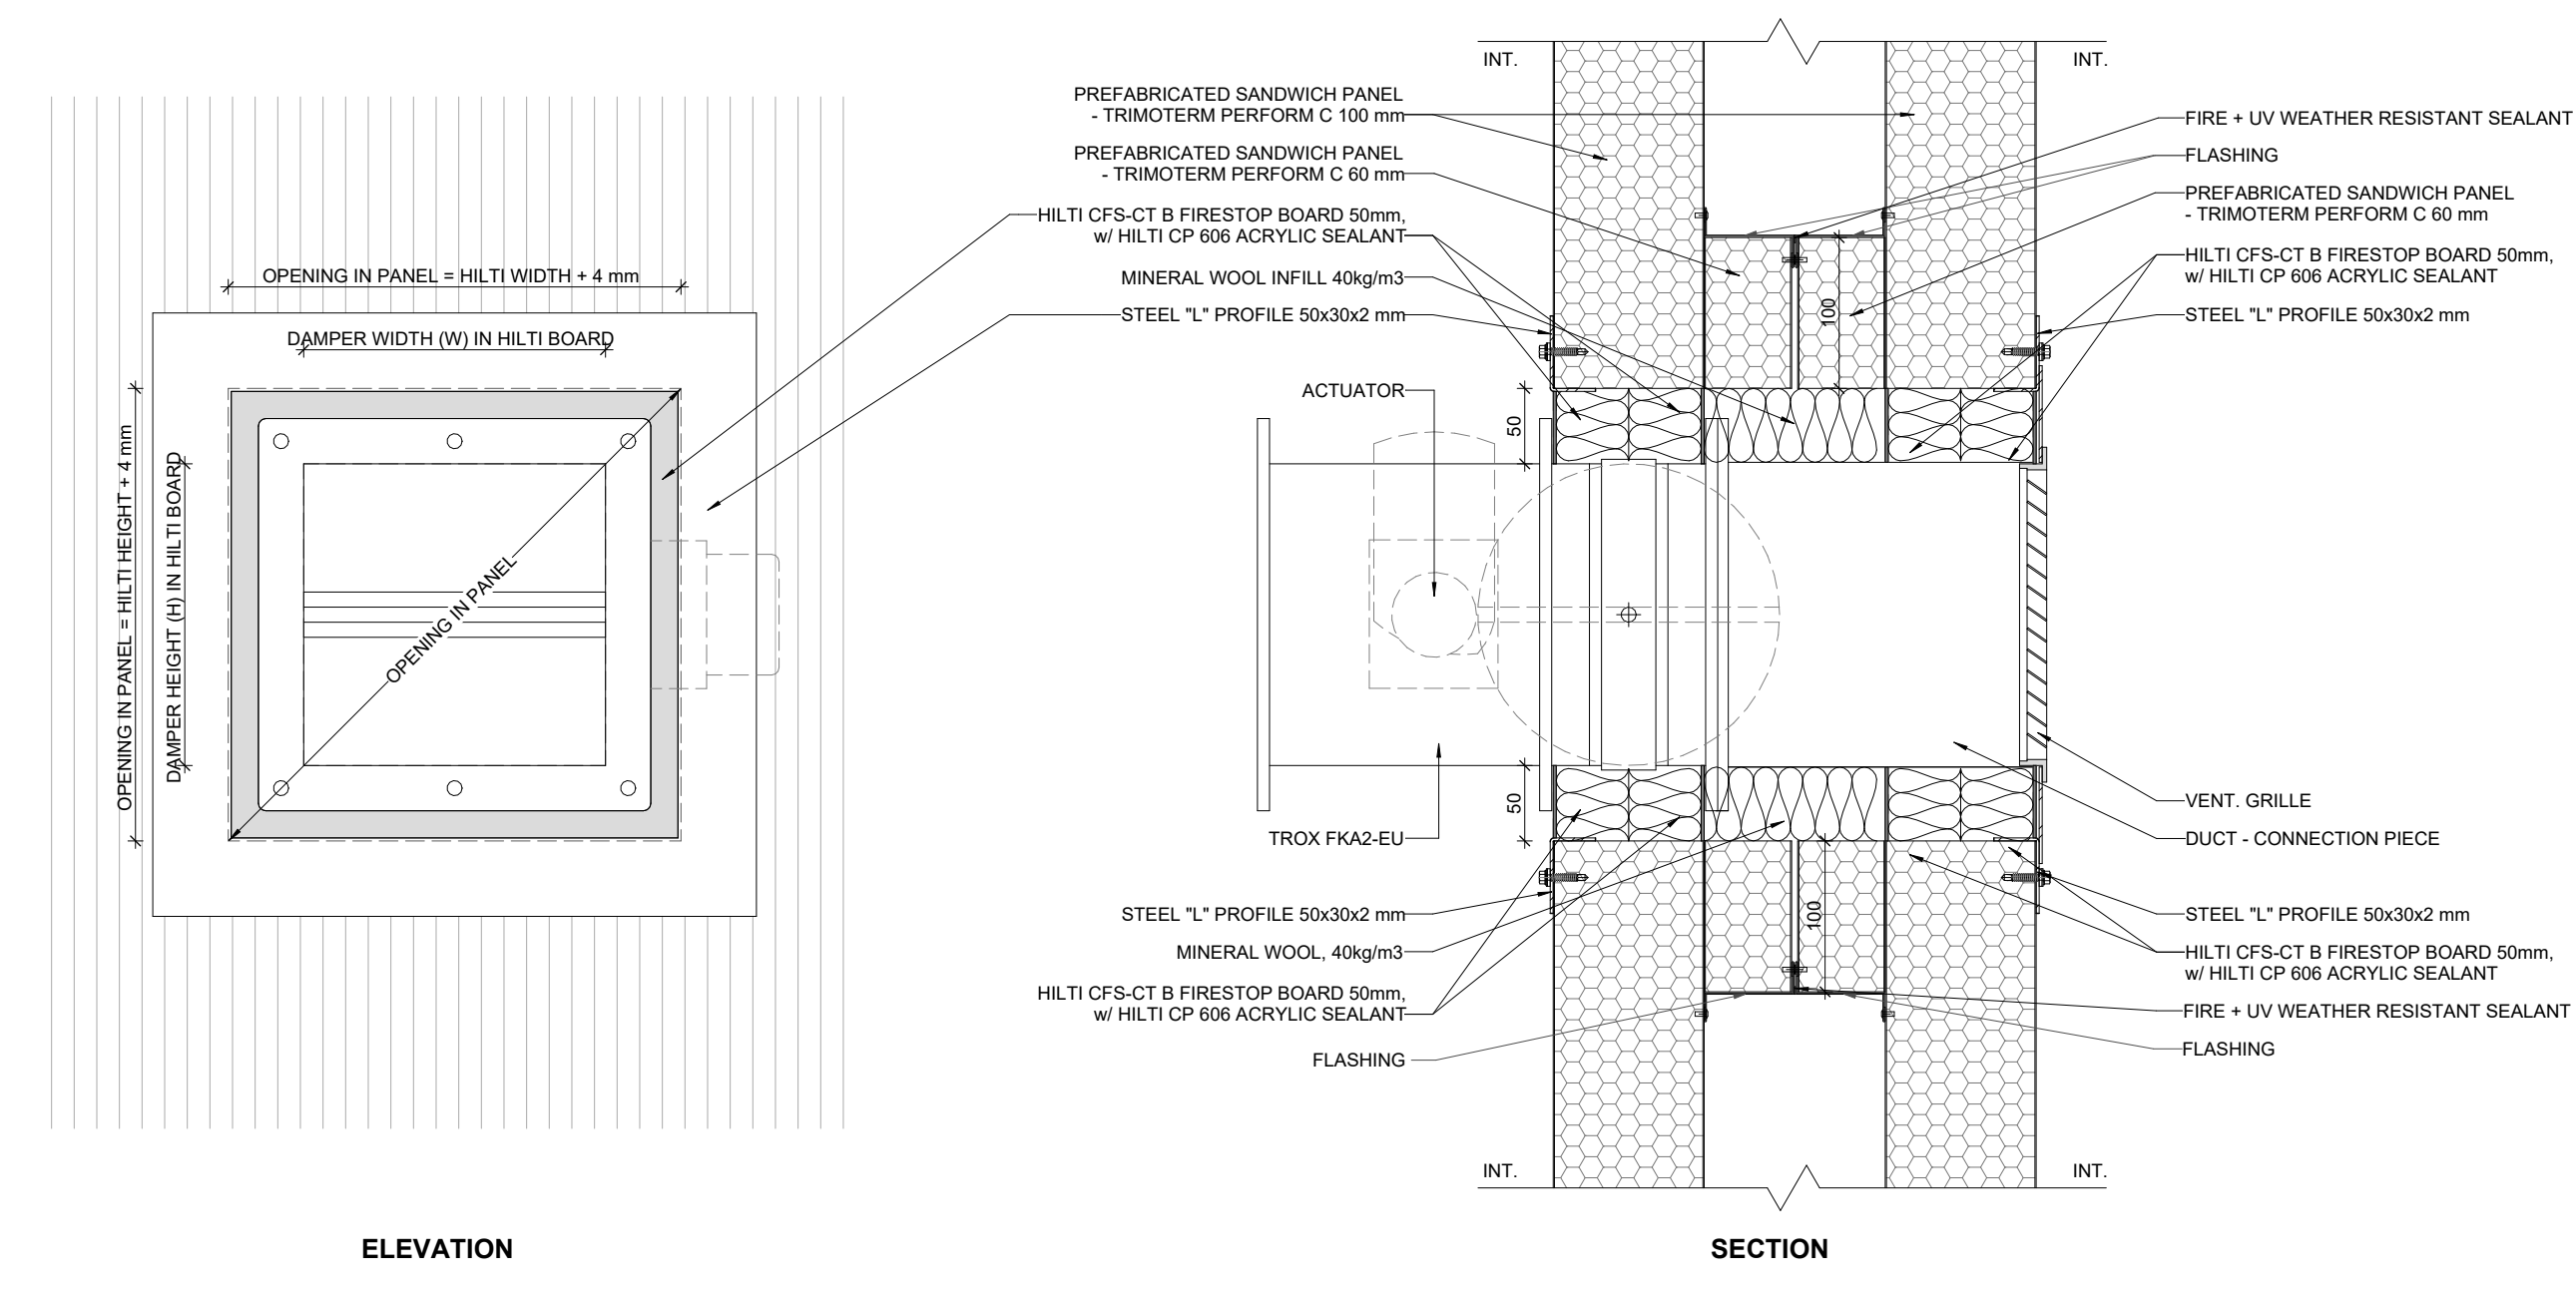

P08 TROX FKA2-EU
1:5

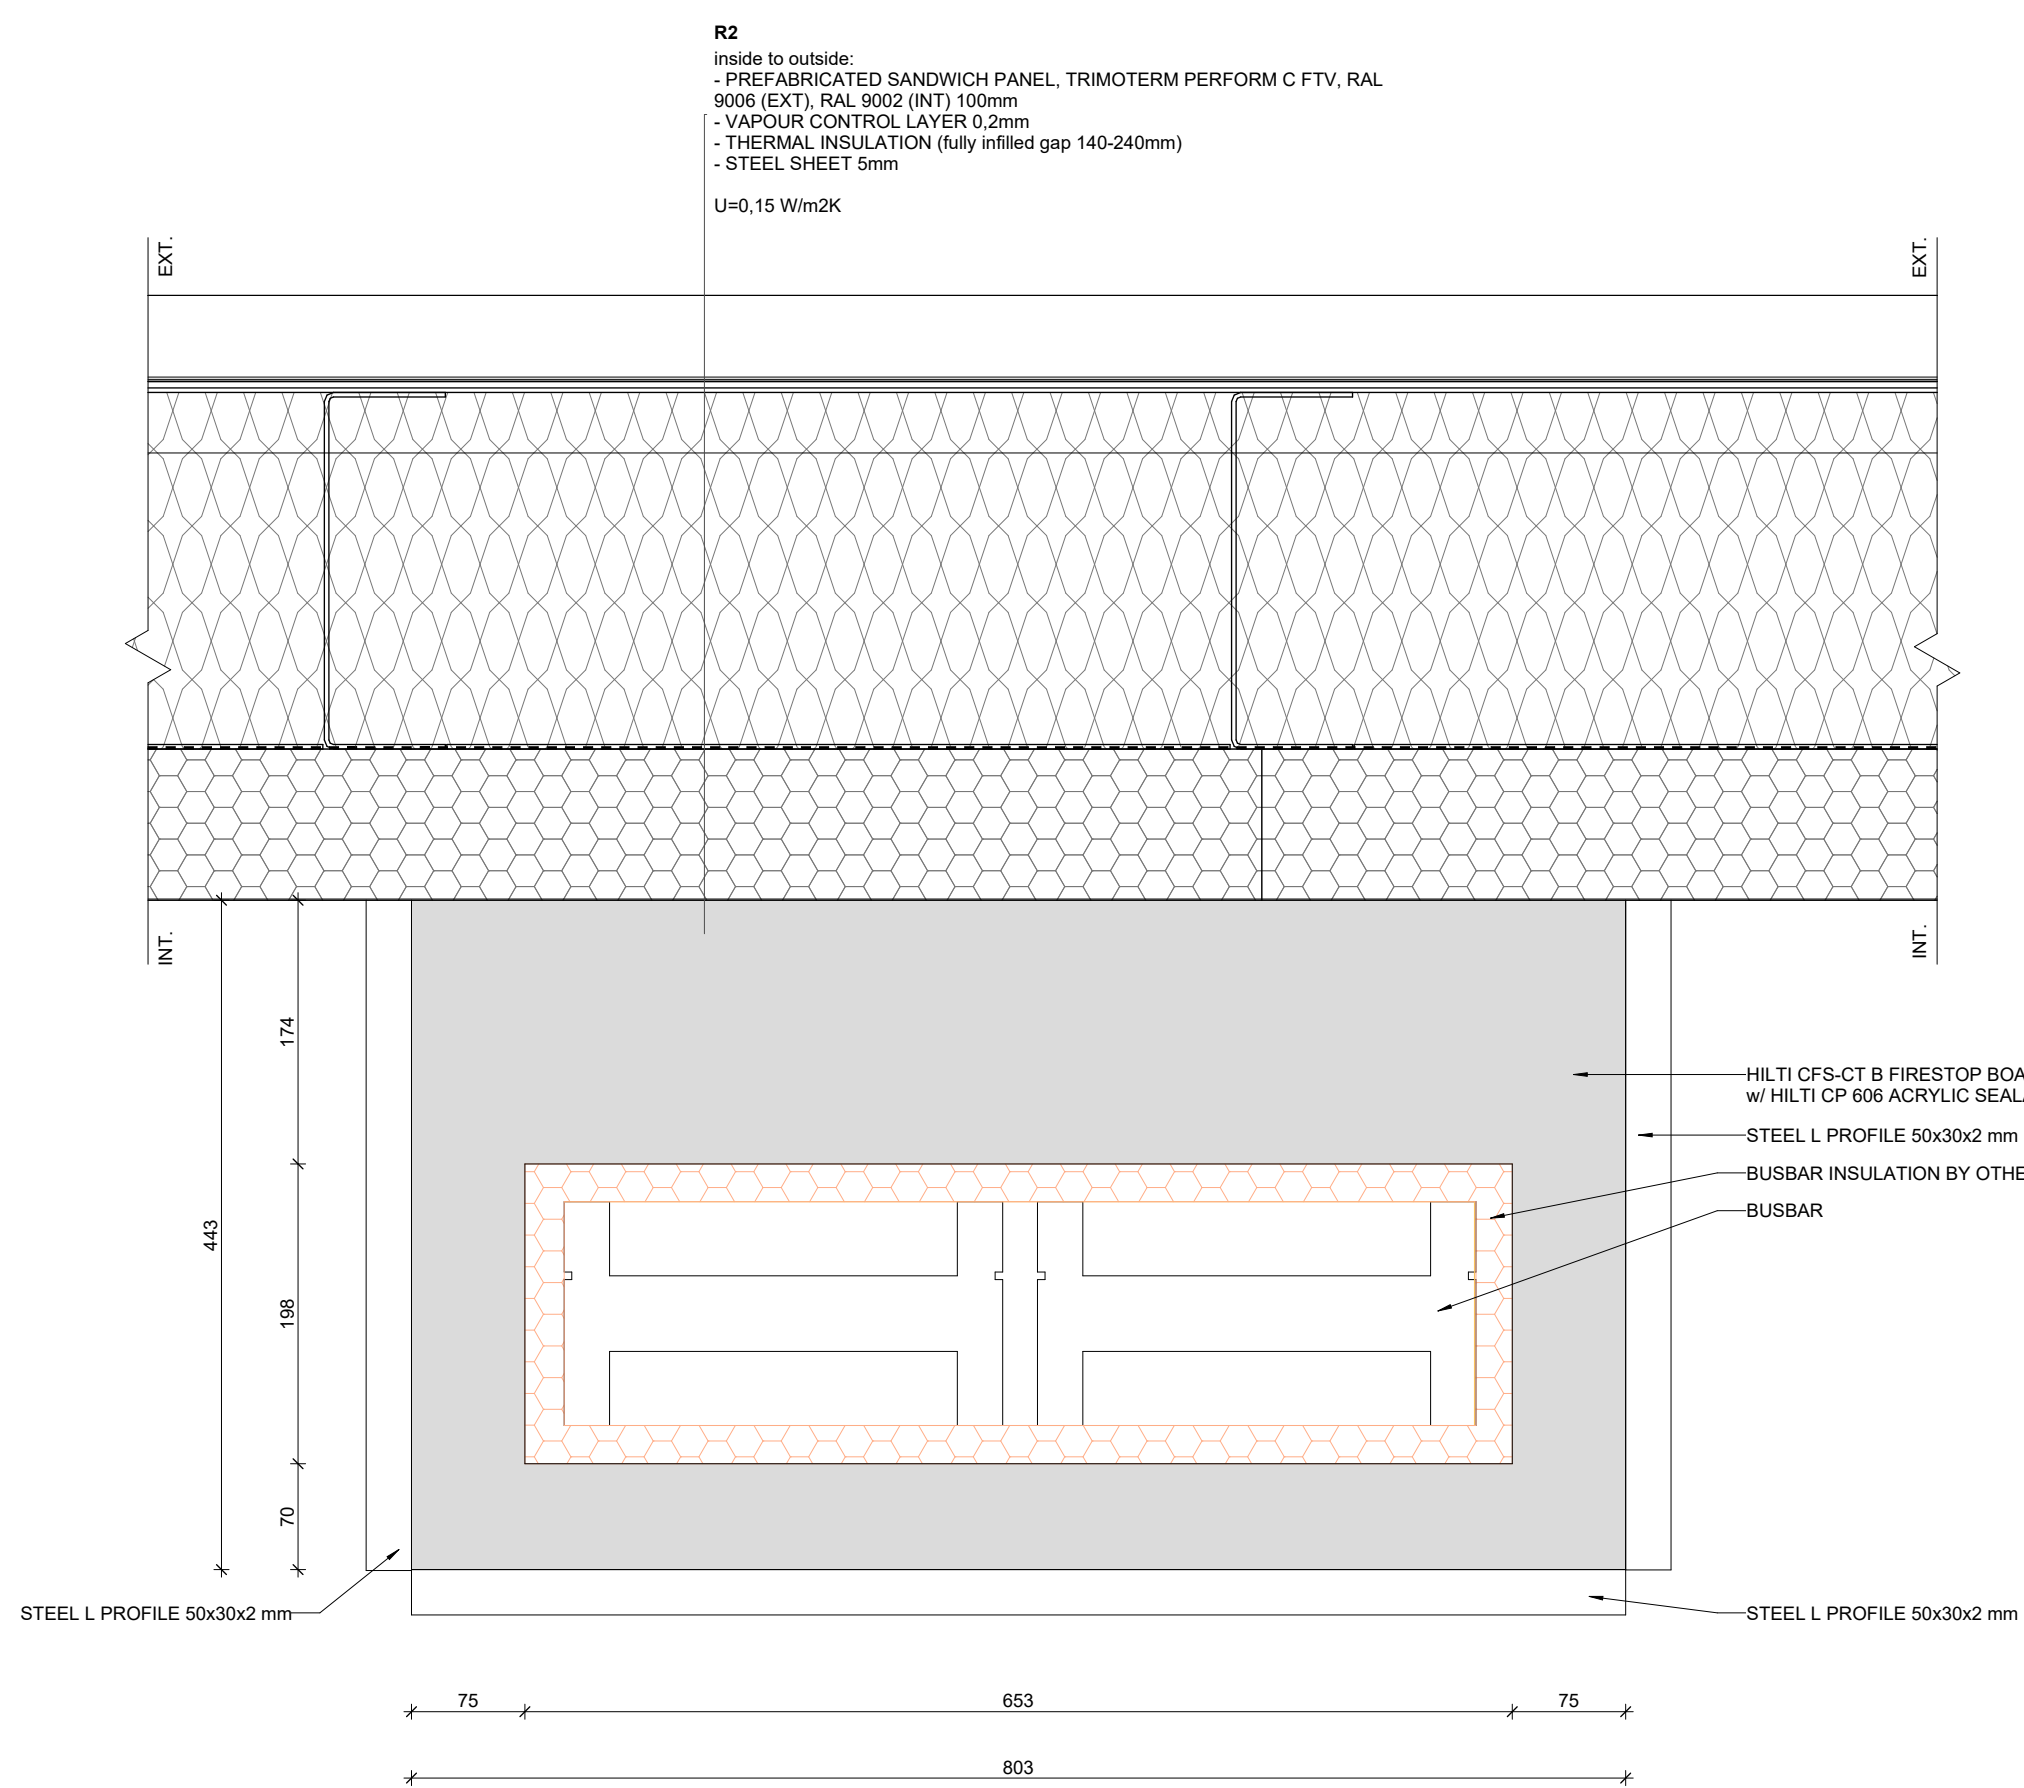


P09-PM BUSBAR-DOUBLE EXT. WALL
1:5

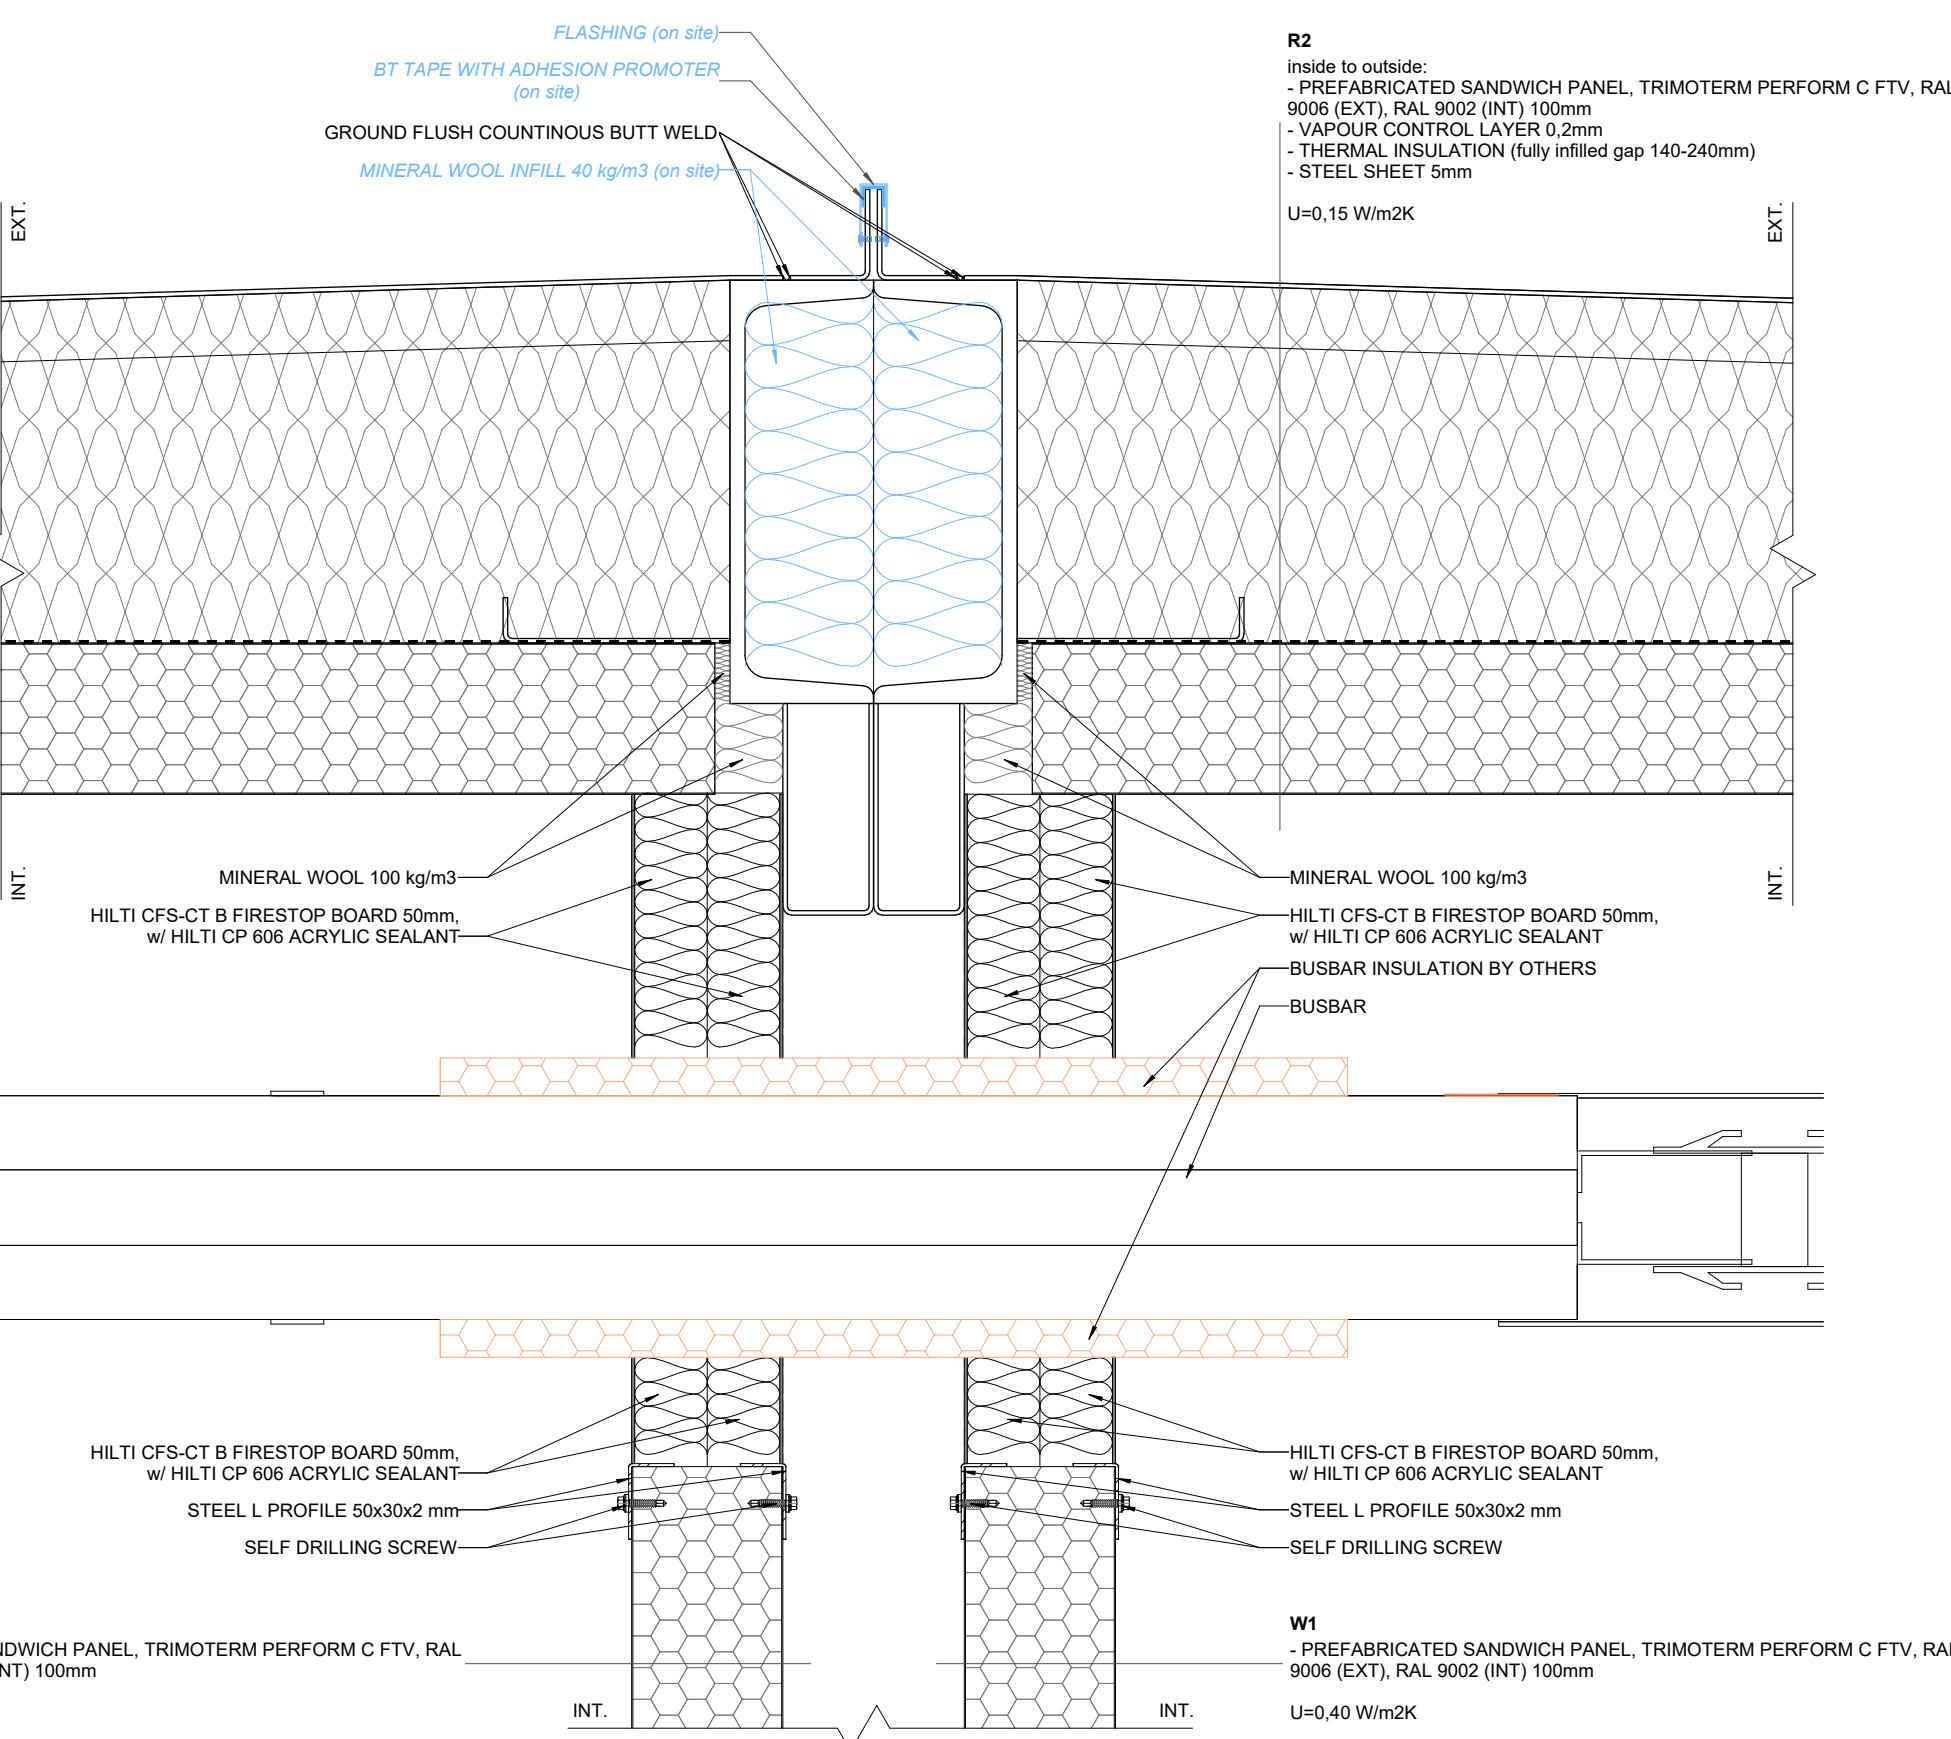

P10-PM BUSBAR-DOUBLE EXT. WALL
1:5

KEYNOTES

KEY PLAN

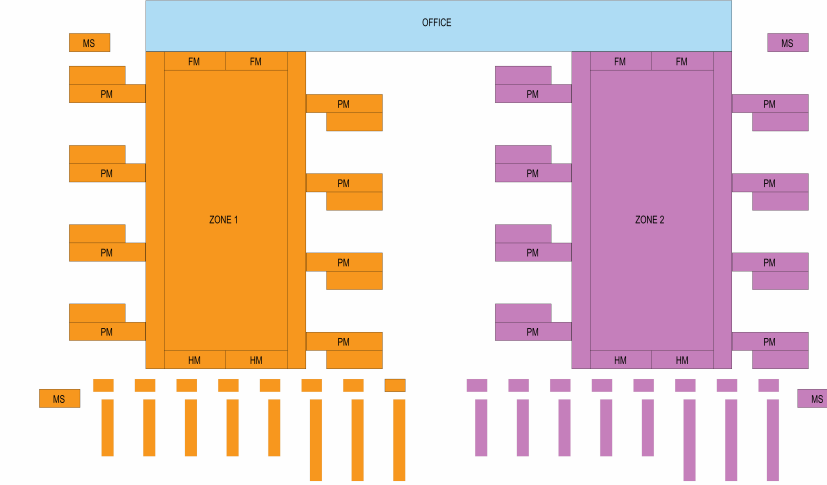

R01 CD SET - FOR INFORMATION 2026-07-24

REV. DESCRIPTION DATE



PROJECT NAME
ECO DC MONALISA

DRAWING NAME
ARCHITECTURAL DETAILS
- PREFABRICATED MODULES
- PENETRATIONS INTERNAL - PM - MV - MS

PREPARED (ALSO SUBJECT RESPONSIBLE IF OTHER)
L. MAVREK / K. KOZINA
DOCUMENT RESPONSIBLE (APPROVED)
M. PACAK
CAD: BIM SYSTEMS AUTODESK REVIT 2025

DOCUMENT NUMBER
ECODC-VRT-MDC19-00-DR-A-50106
SHEET SIZE
A0
DRAWING SCALE
1:5
DATE (YYYYMMDD)
2026-07-24
SHEET 1 OF 1
REVISION
R01