

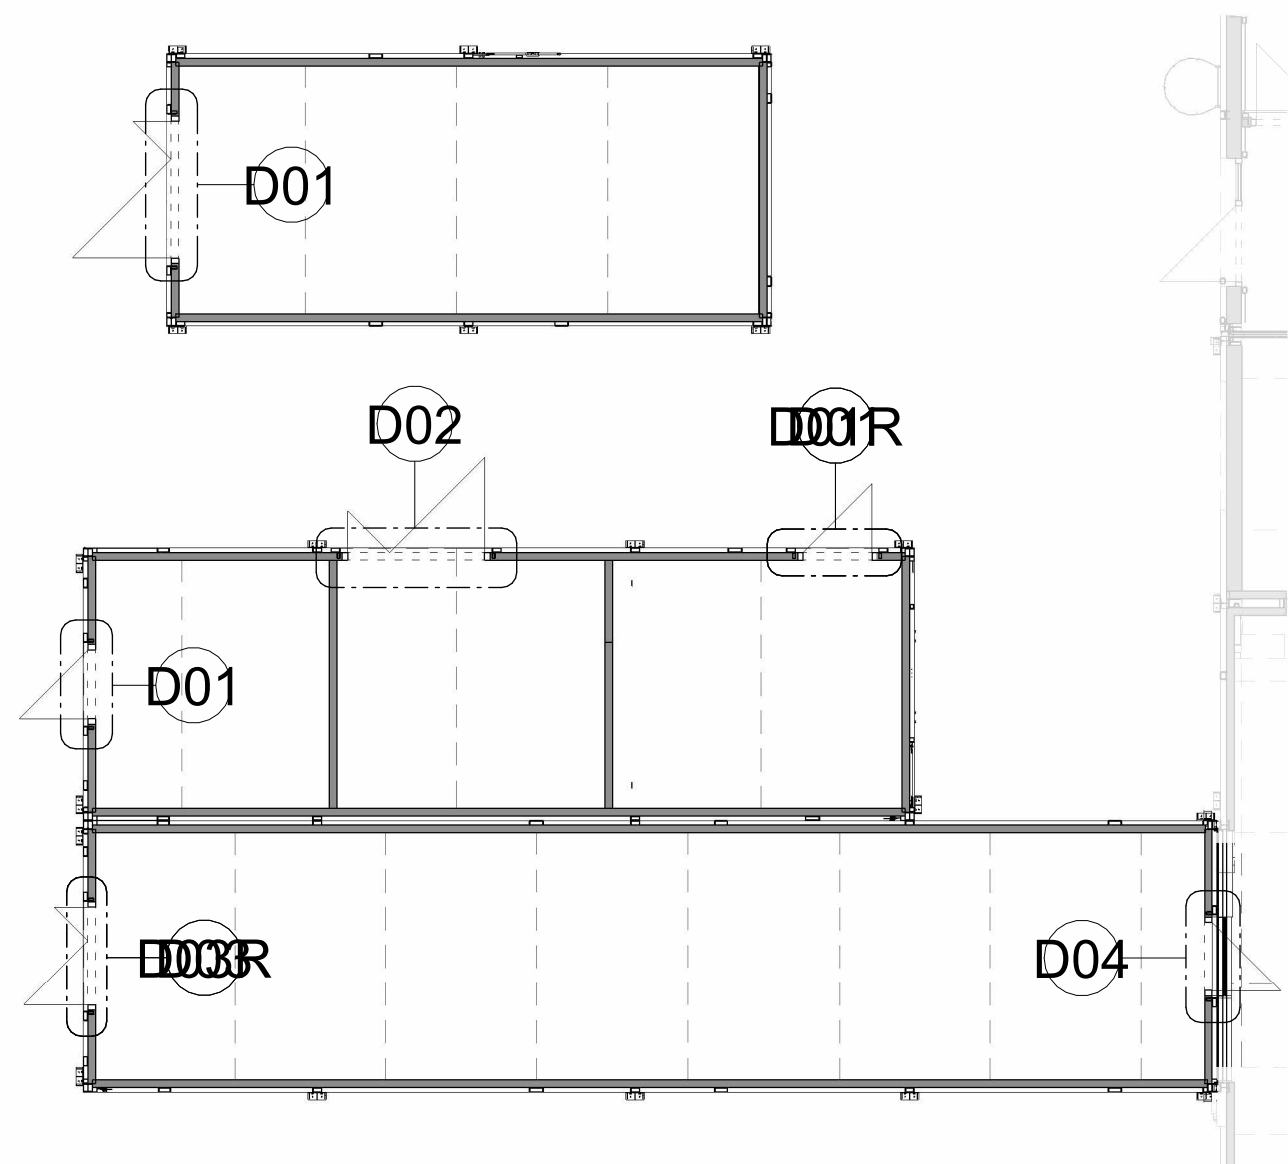


LEGAL DISCLAIMER: THIS DOCUMENT AND THE CONTENTS HEREIN ARE CONFIDENTIAL AND THE SOLE PROPERTY OF VERTIV GROUP CORP. REPRODUCTION, DISTRIBUTION OR UNAUTHORIZED USE OF THIS DOCUMENT OR ANY PARTS WITHIN THIS DOCUMENT ARE FORBIDDEN WITHOUT THE WRITTEN CONSENT OF VERTIV GROUP CORP.

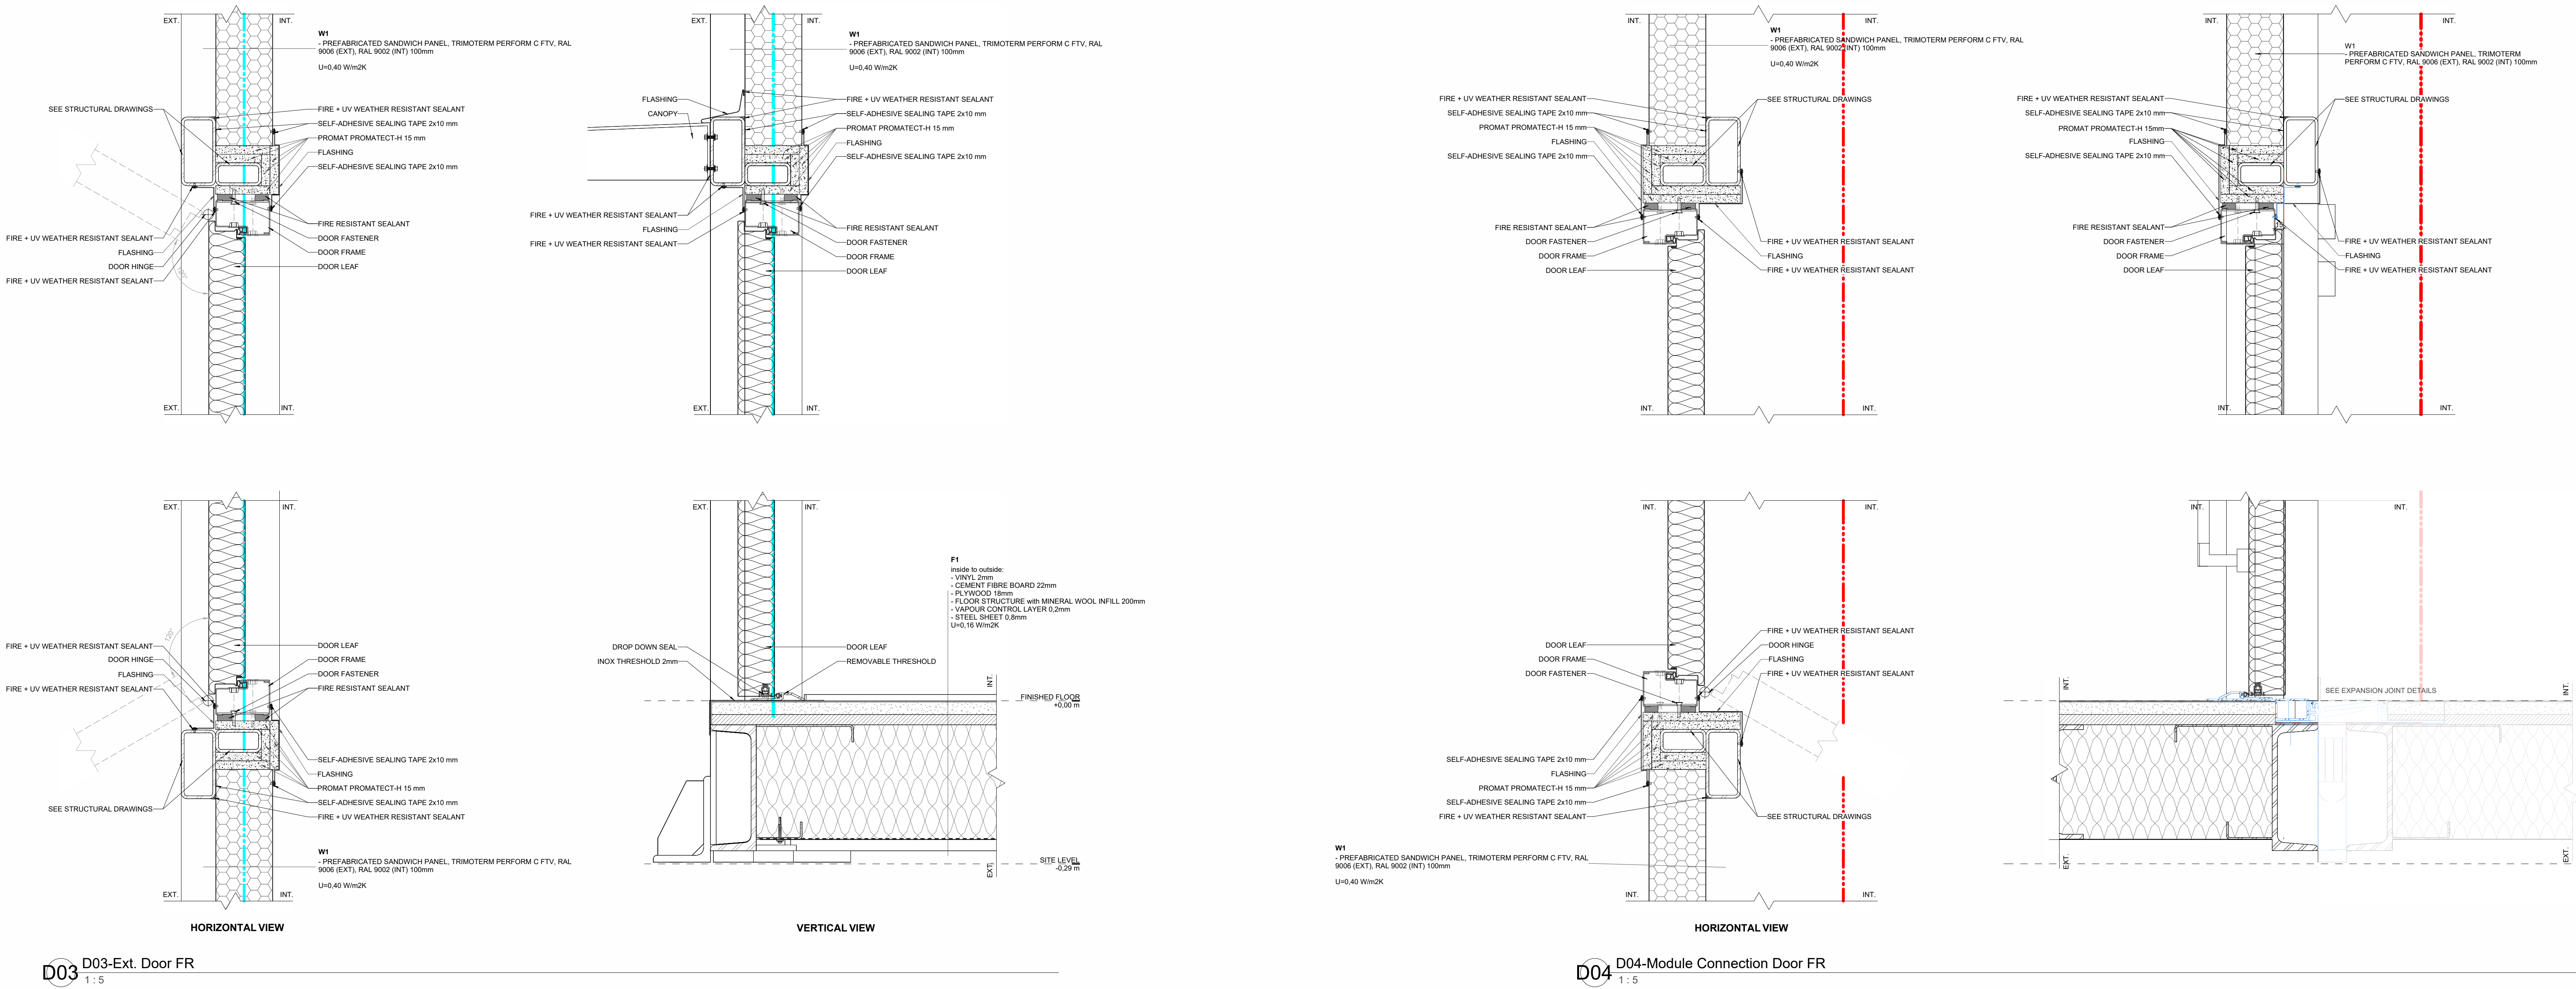


KEY PLAN - PM/MV/MS DOOR DETAIL POSITIONS

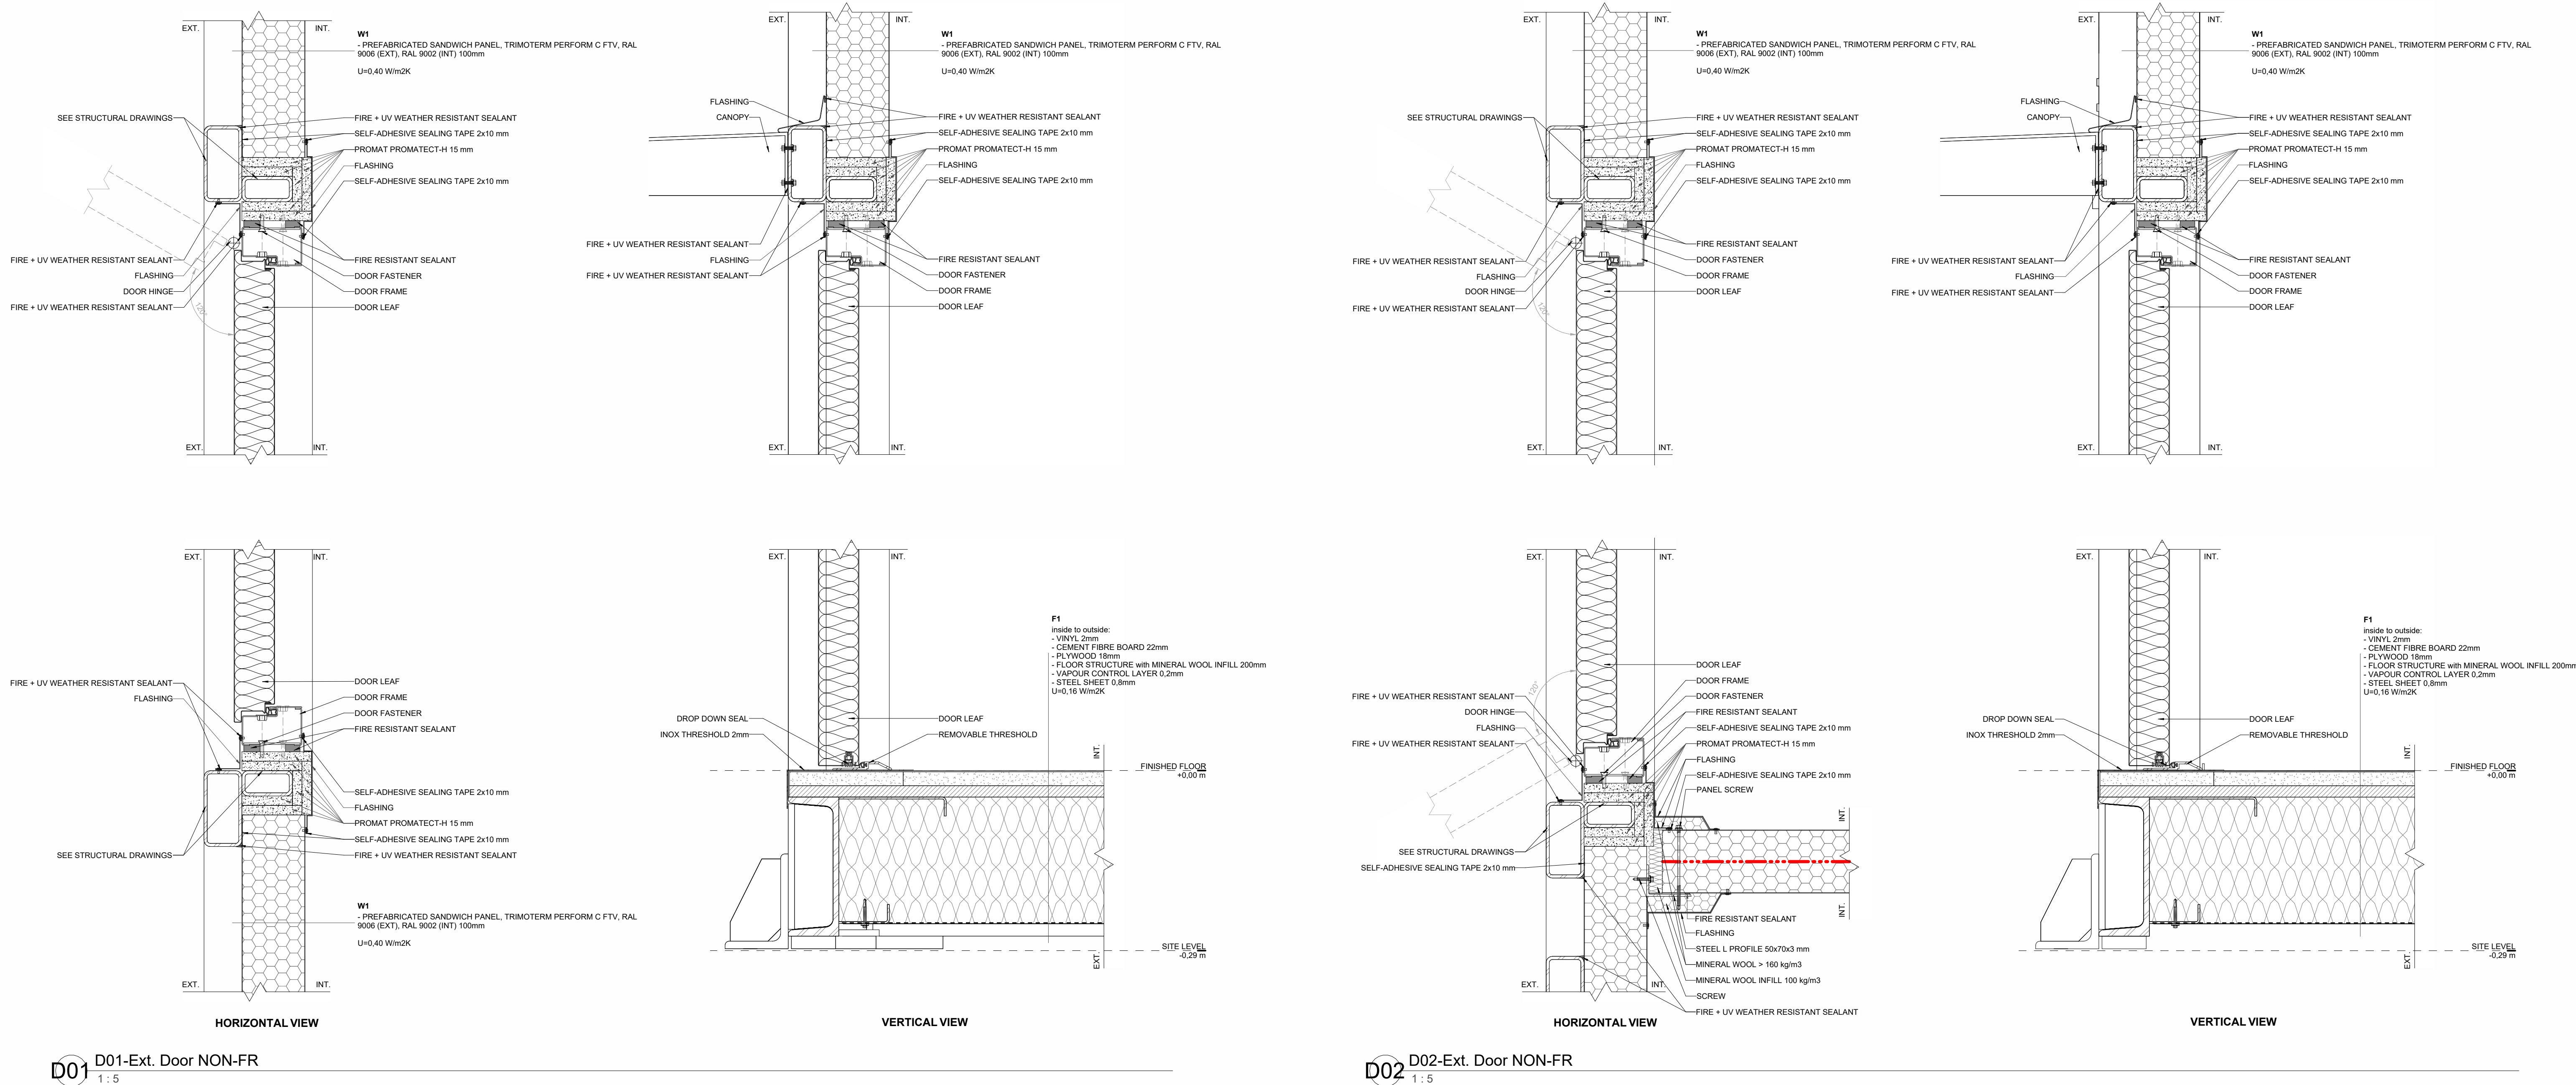

KEYNOTES

LEGEND:

- FIRE COMPARTMENT BORDER (31 80)
- FIRE COMPARTMENT BORDER (31 30)
- ELEMENTS INSTALLED ON SITE

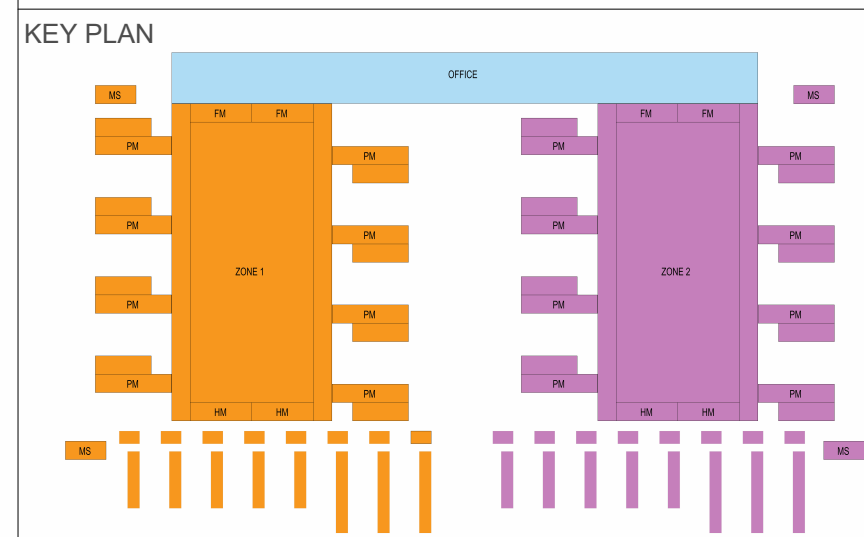

R01 CD SET - FOR INFORMATION 2026-07-24

REV. DESCRIPTION DATE



PROJECT NAME

ECO DC MONALISA

DRAWING NAME

ARCHITECTURAL DETAILS – PREFABRICATED
MODULES – DOORS – PM – MV – MS

PREPARED (ALSO SUBJECT RESPONSIBLE IF OTHER)

L. MAVREK / K. KOZINA

DOCUMENT RESPONSIBLE / APPROVED

M. PACAK

DATE (YYYYMMDD)

2026-07-24

DOCUMENT NUMBER

ECODC-VRT-MDC19-00-DR-A-50130

SHEET SIZE

A0

DRAWING SCALE

1:5

SHEET 1 OF 1

REVISION

R01