






LEGAL DISCLAIMER: THIS DOCUMENT AND THE CONTENTS HEREIN ARE CONFIDENTIAL AND THE SOLE PROPERTY OF VERTIV GROUP CORP. REPRODUCTION, DISTRIBUTION OR UNAUTHORIZED USE OF THIS DOCUMENT OR ANY PARTS WITHIN THIS DOCUMENT ARE FORBIDDEN WITHOUT THE WRITTEN CONSENT OF VERTIV GROUP CORP.

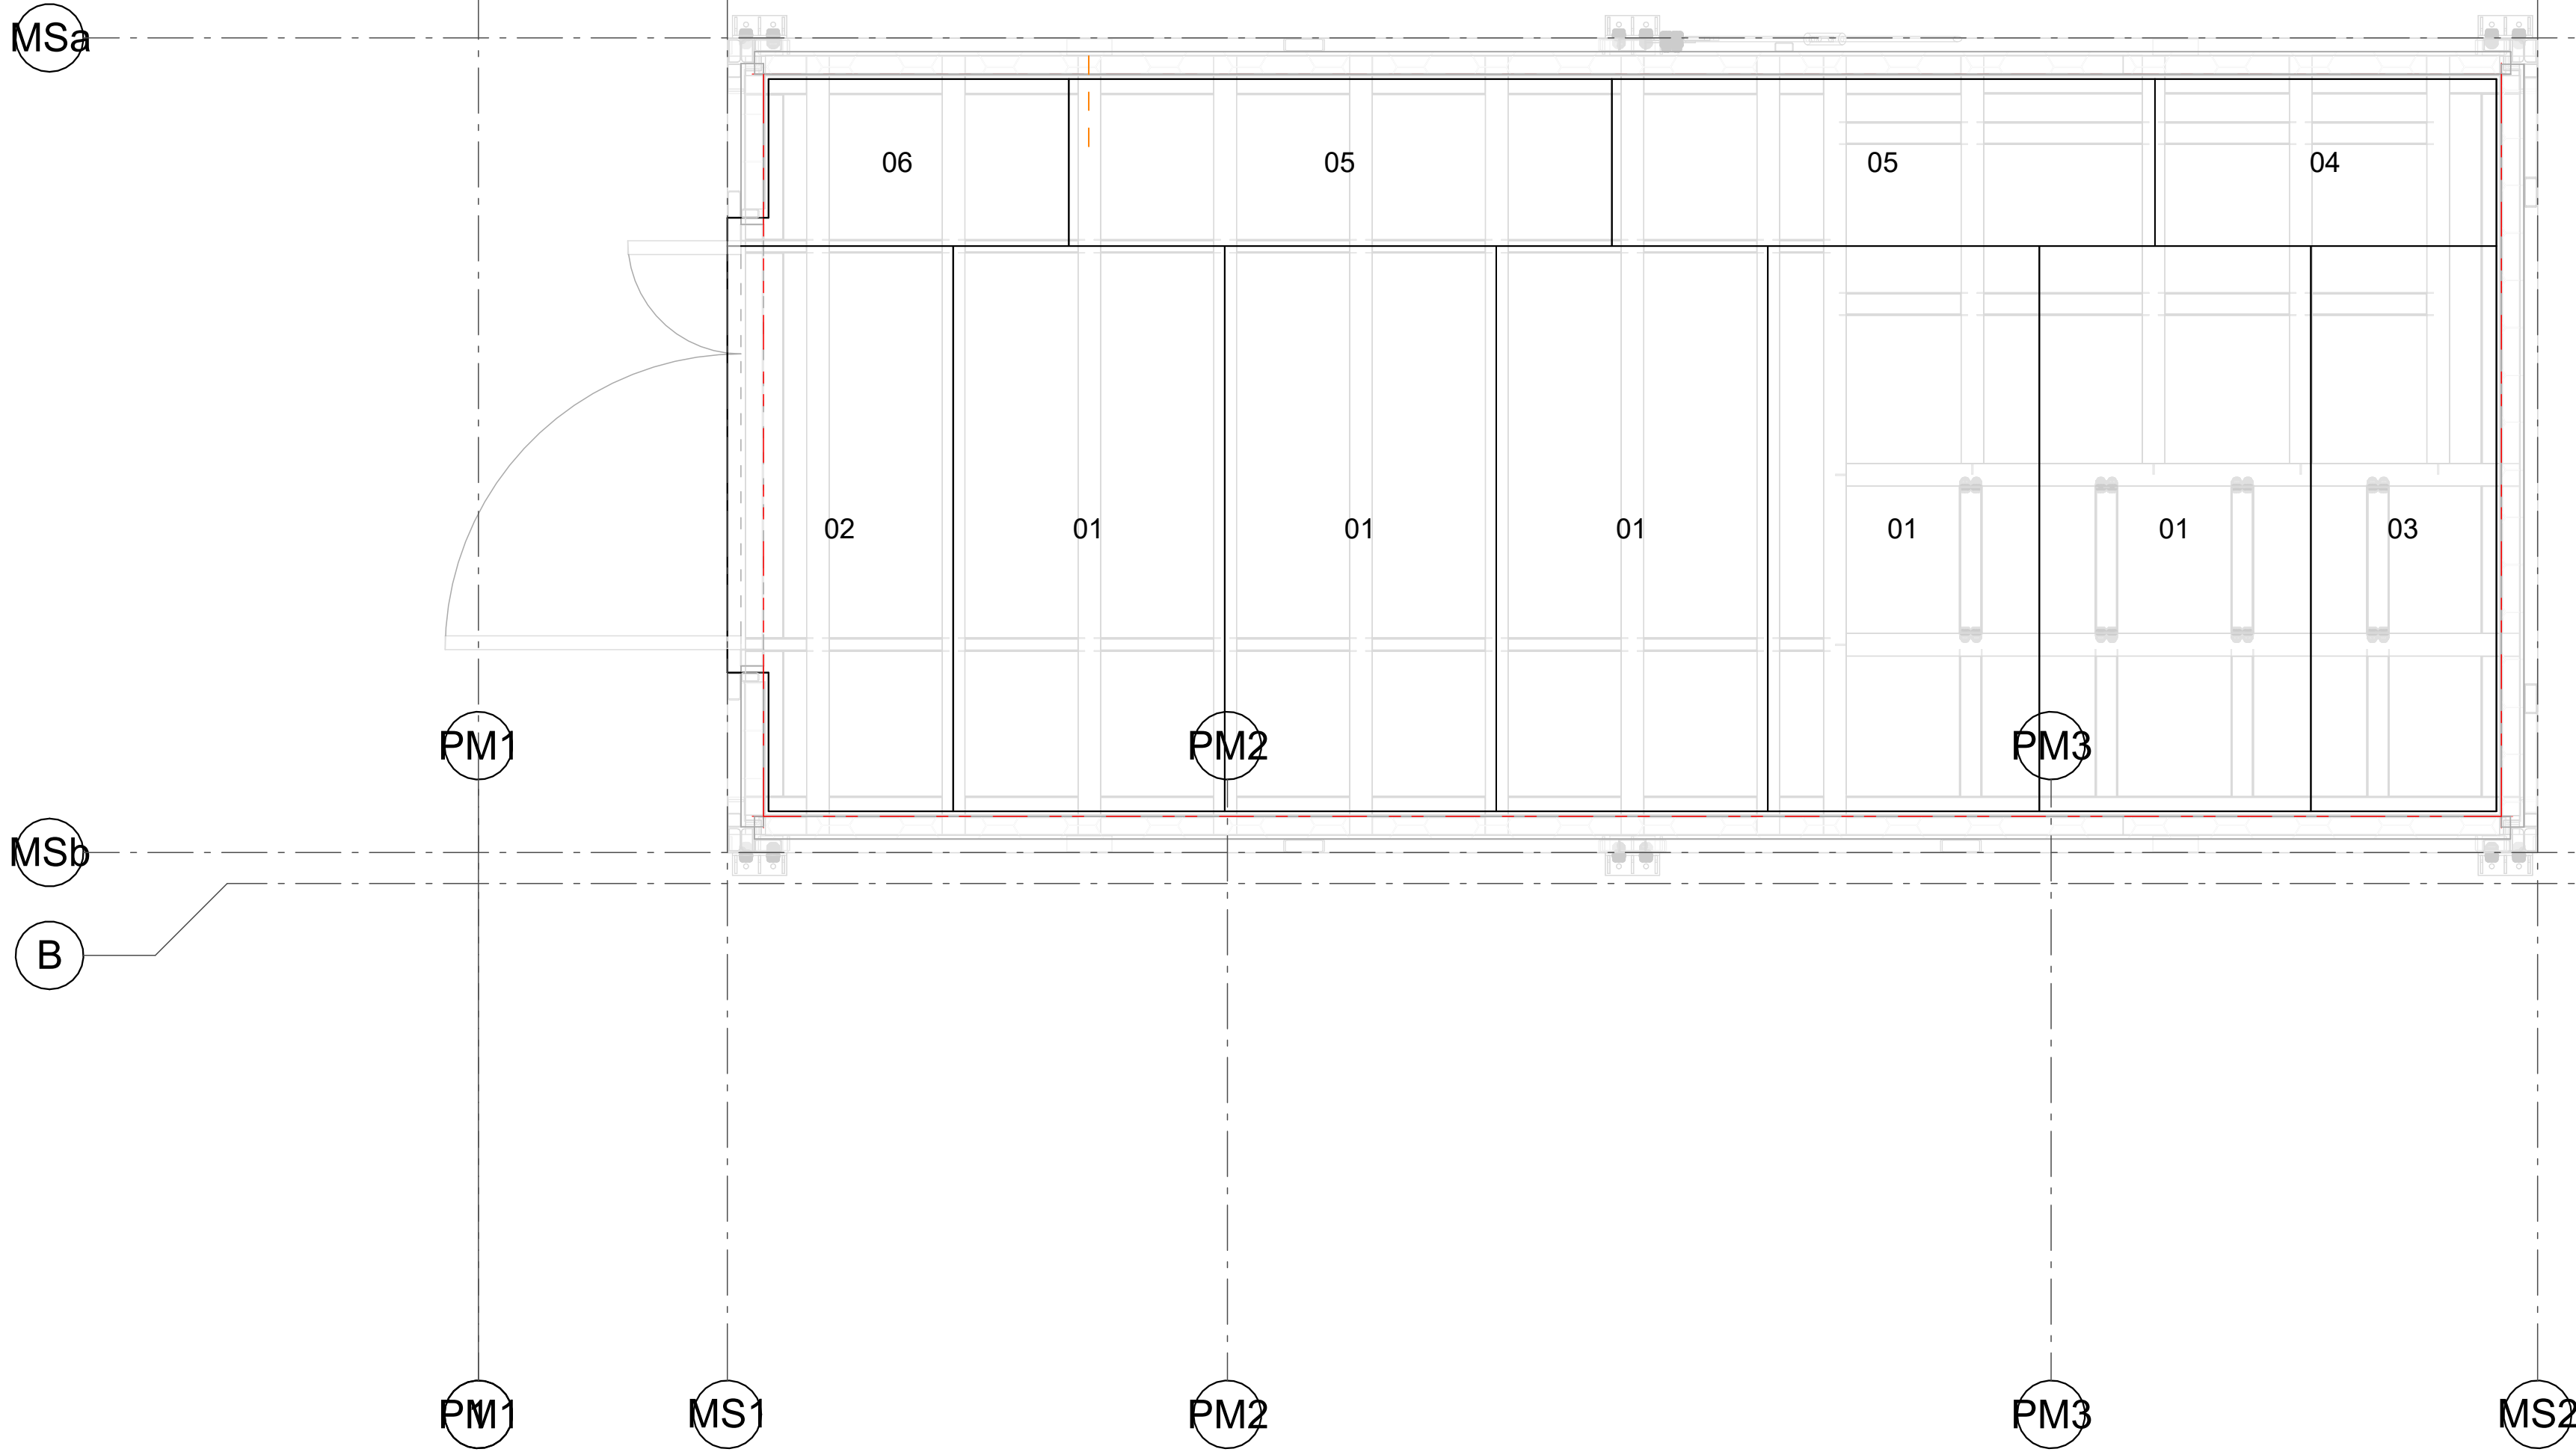

PM - FIRST FLOOR LAYER LAYOUT - PLYWOOD

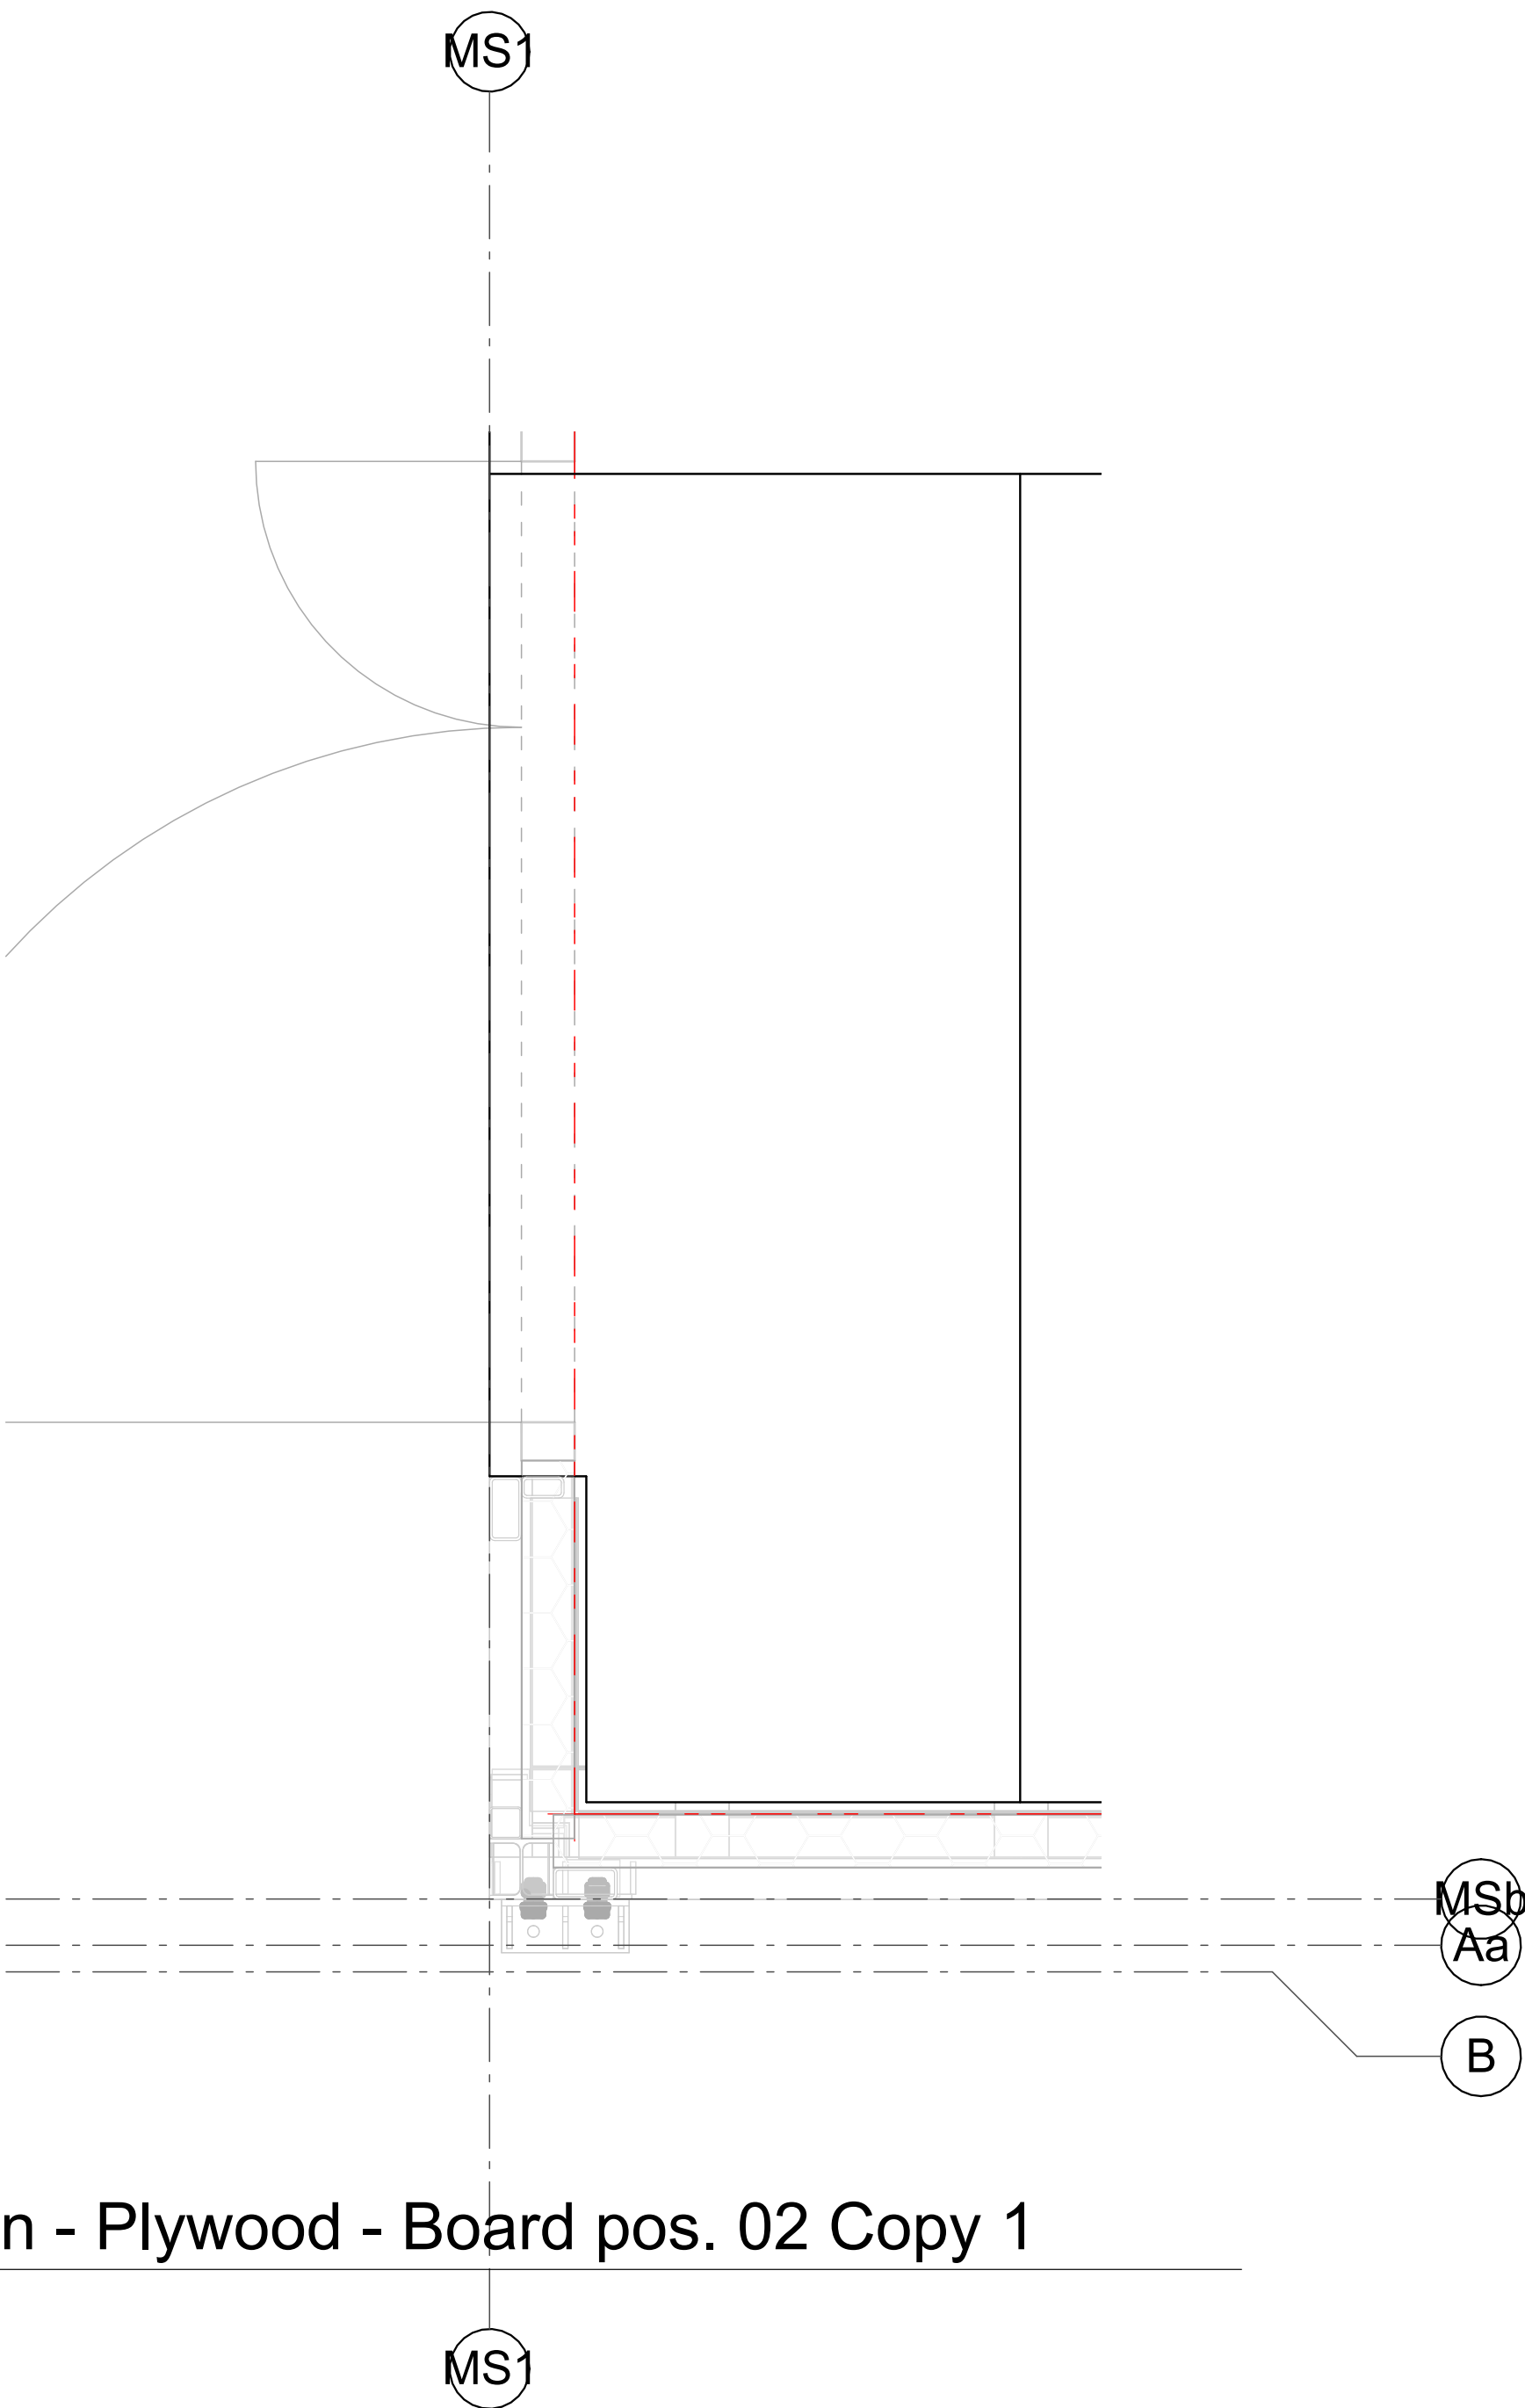

2 MS - Floor Plan - Plywood - Board pos. 02 Copy 1
1 : 25

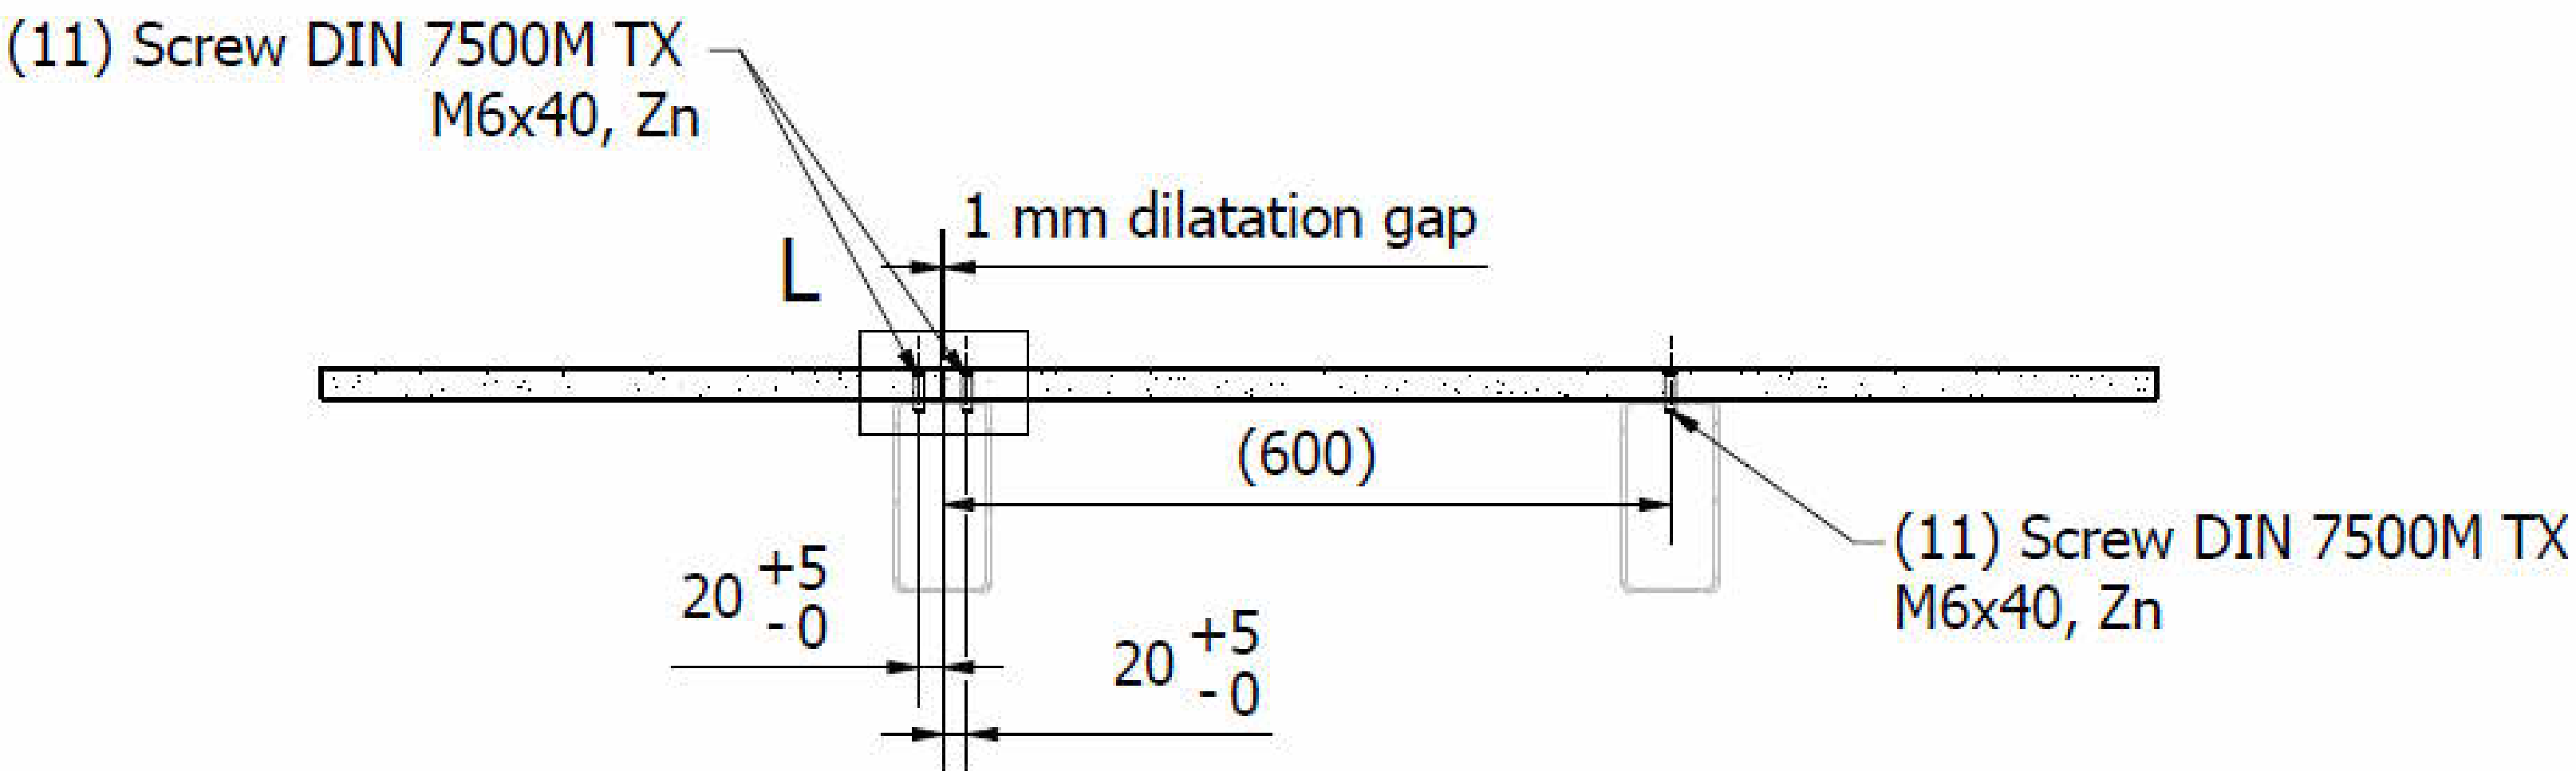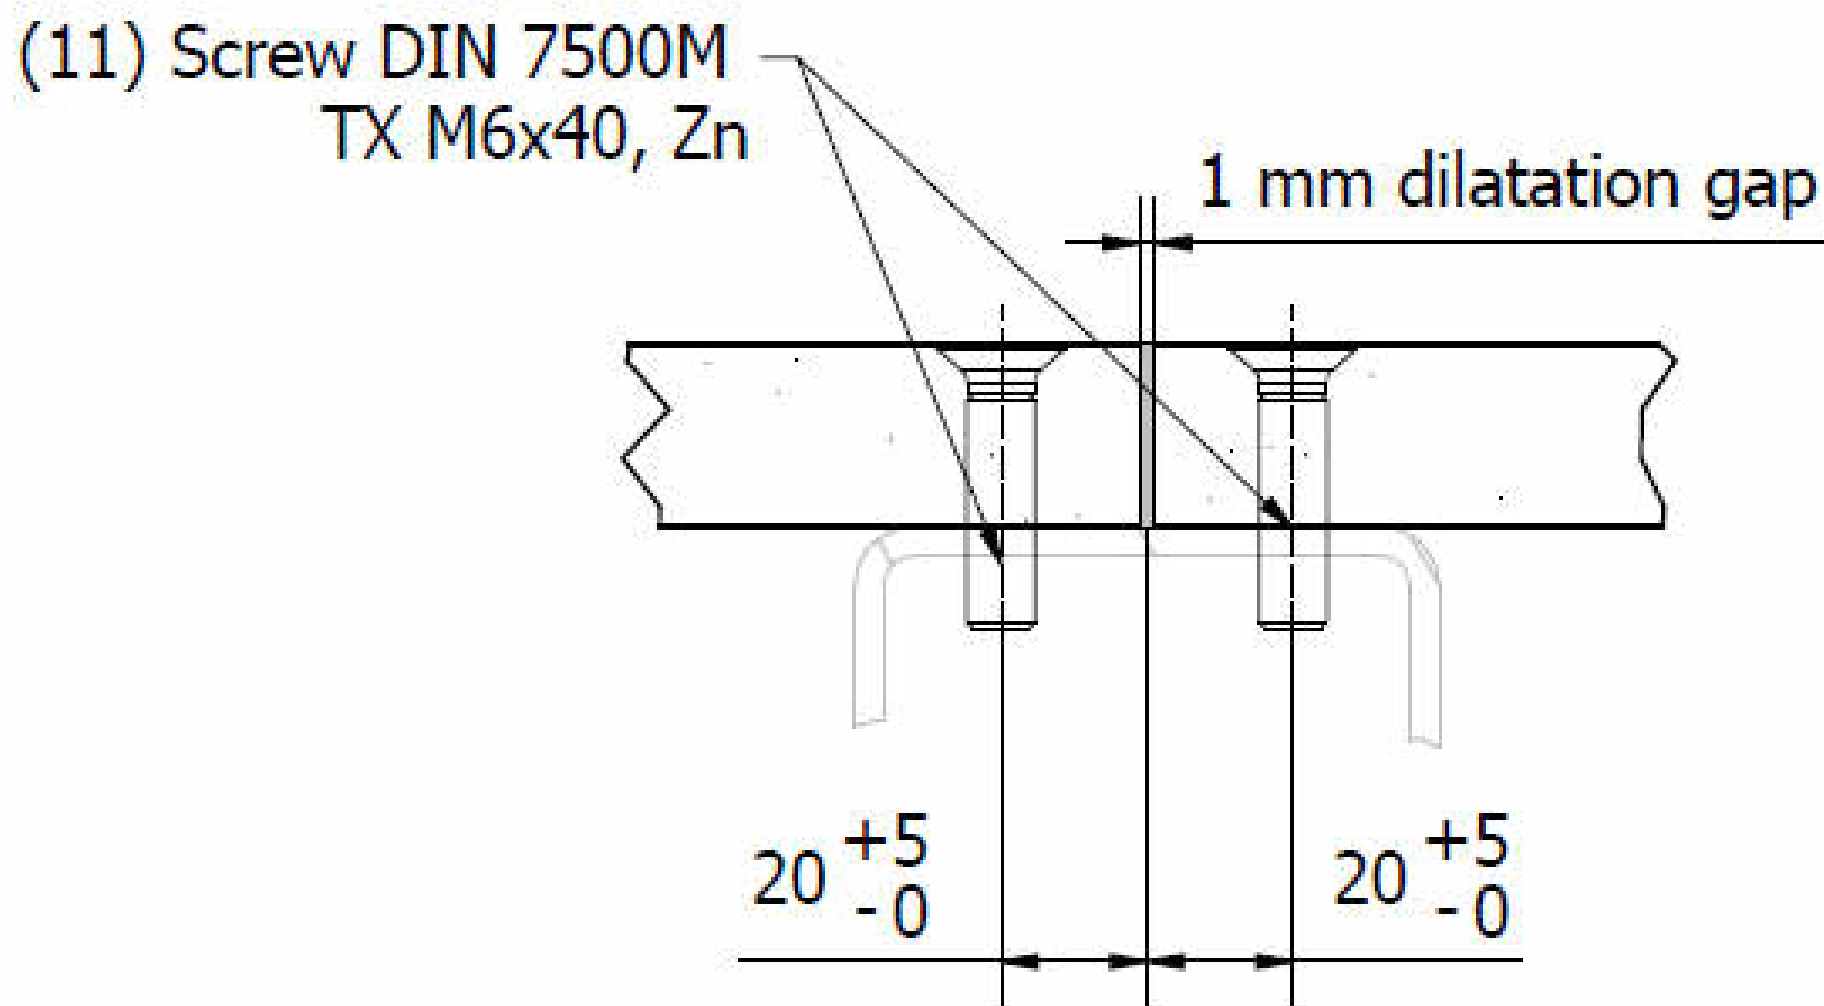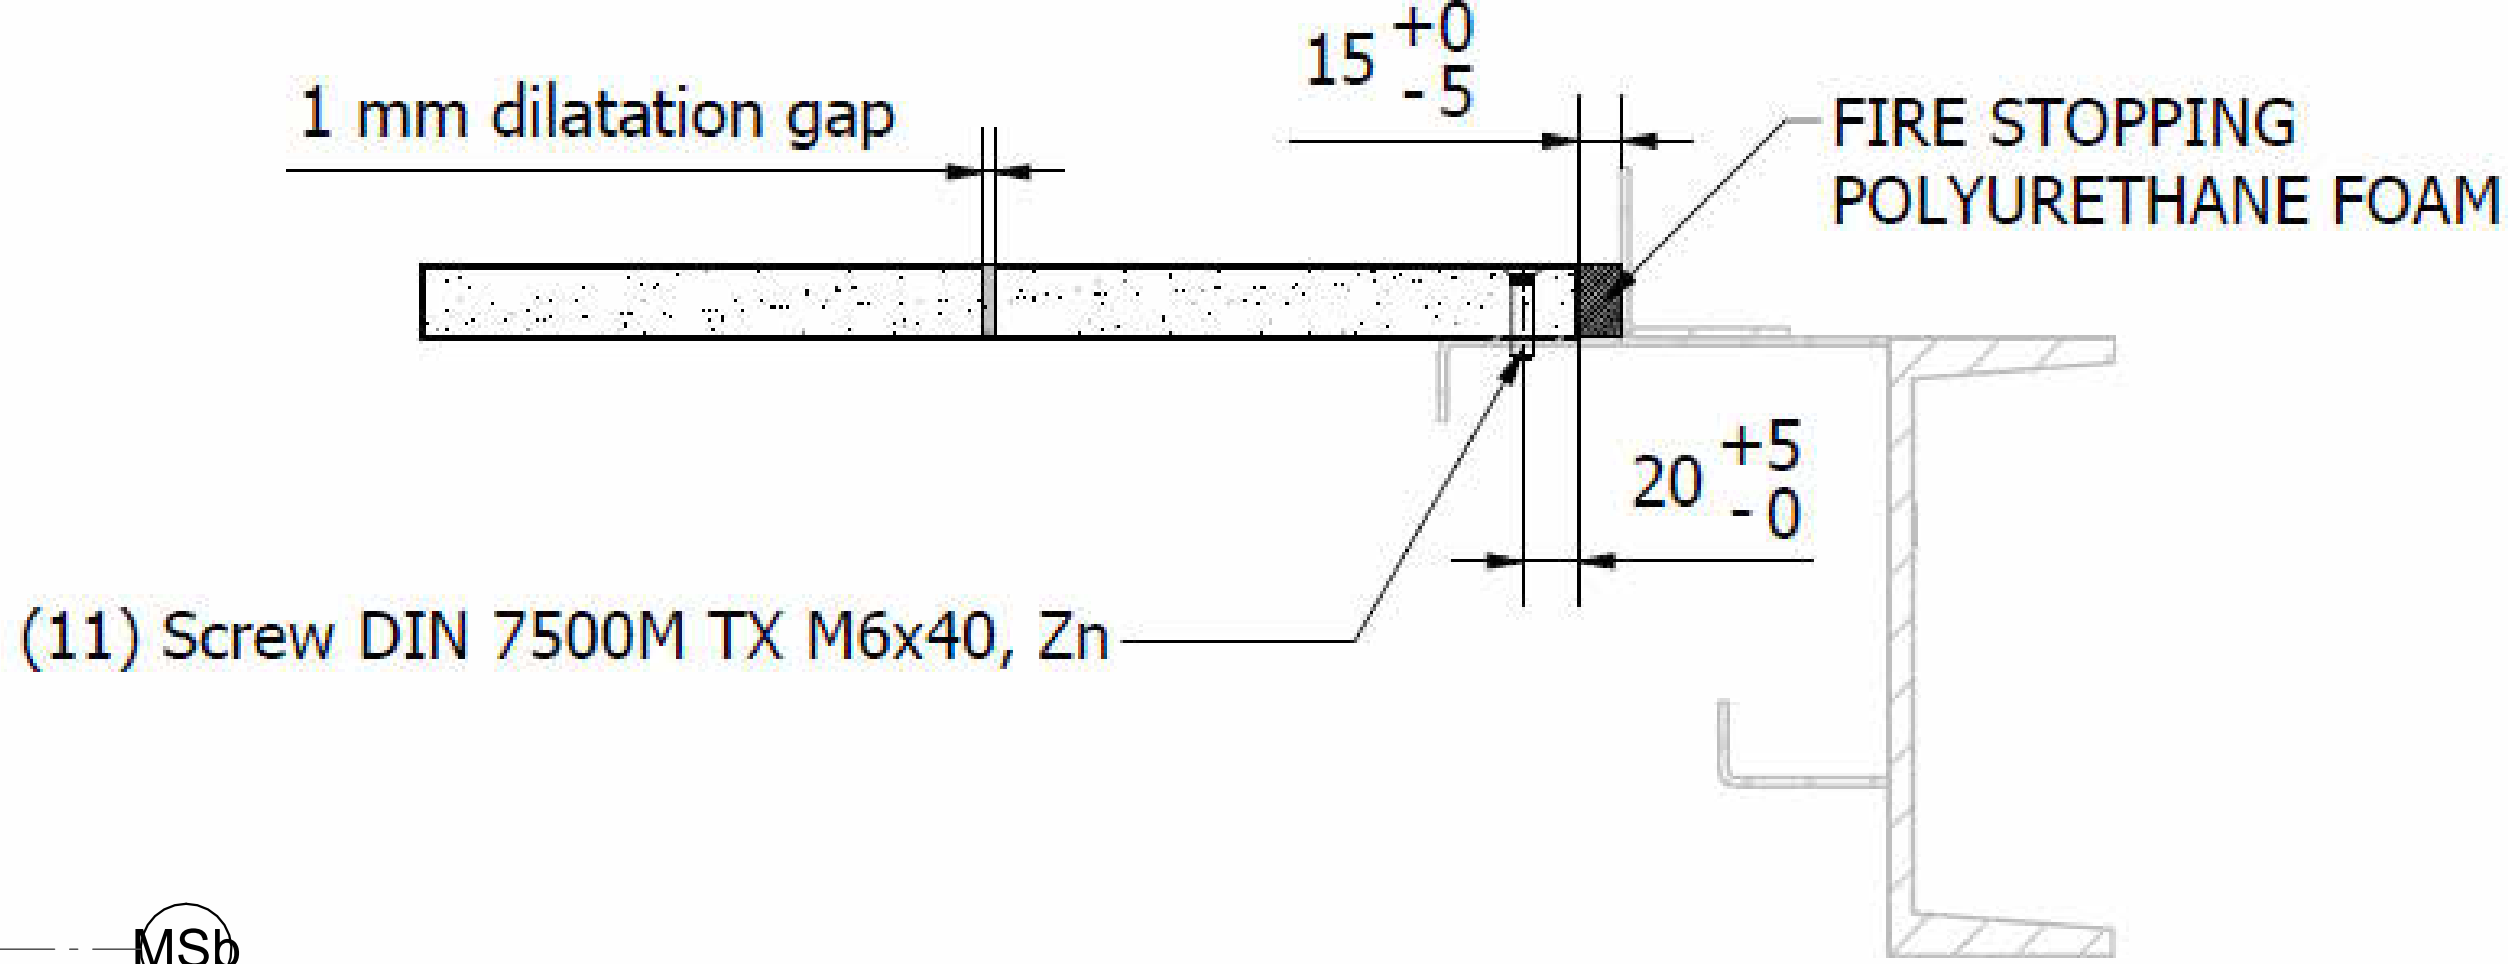


- GENERAL NOTES:**
- Every board needs to be supported on the steel floor understructure on at least three sides
 - All detailed cutting should be done during installation.
 - Orient the smooth or stamped side facing up (to the ceiling)

- Installation notes:**
- Fix OSB board to steel frame using Self-taping screw DIN 7500M M6x40, Zn
 - If board dimensions are smaller then 600mm, min. 4 screws needs to be used

ASI - MS PLYWOOD			
Mark	Height Manual [mm]	Width Manual [mm]	Count [pcs]
01	2500	1200	5
02	2500	998	1
03	2500	820	1
04	738	1509	1
05	738	2400	2
06	738	1509	1
Grand total: 11			

REFERENCE NOTES

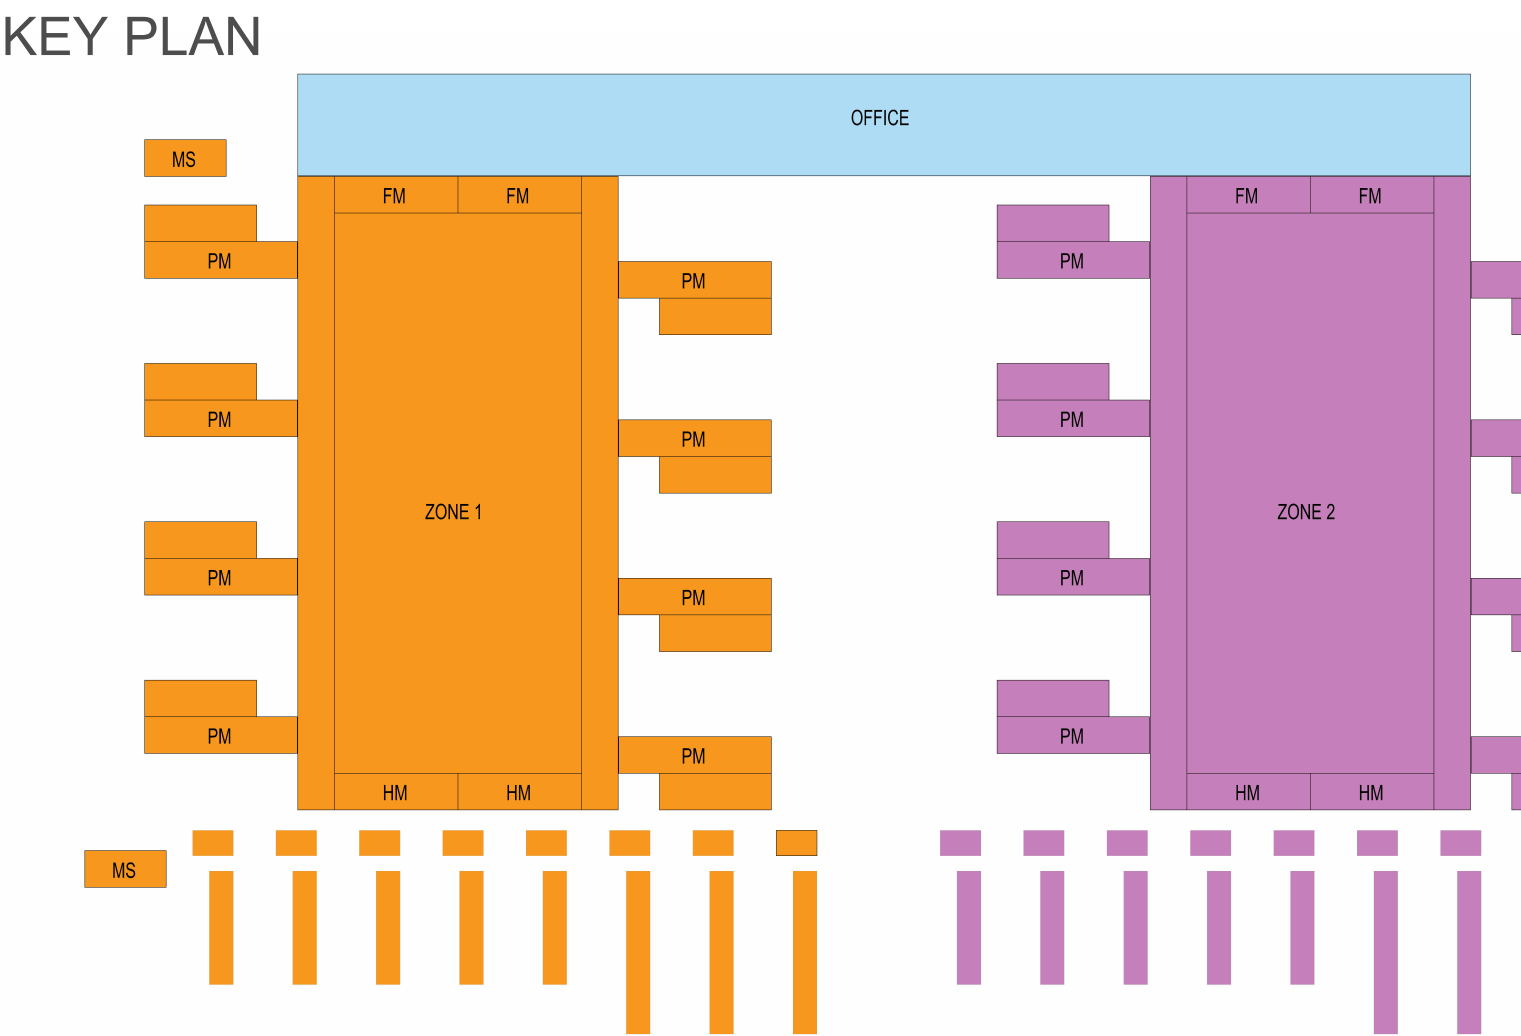

R01	FOR MANUFACTURING	2026-05-26
REV.	DESCRIPTION	DATE



PROJECT NAME		
ECO DC MONALISA		
DRAWING NAME		
MS – FIRST FLOOR LAYER LAYOUT – PLYWOOD		
PREPARED (ALSO SUBJECT RESPONSIBLE IF OTHER)		
I. PUTICA / K. KOZINA / V. SPANIC		
DOCUMENT RESPONSIBLE / APPROVED		
M. PACAK / J. CICVARIC		
CAD / BIM SYSTEM		
AUTODESK REVIT 2025		
DOCUMENT NUMBER		SHEET 1 OF 1
ASI-102-MS		REVISION
SHEET SIZE	DRAWING SCALE	DATE (YYYYMM-DD)
A2	As indicated	2026-05-26
		R01