


LEGAL DISCLAIMER: THIS DOCUMENT AND THE CONTENTS HEREIN ARE CONFIDENTIAL AND THE SOLE PROPERTY OF VERTIV GROUP CORP. REPRODUCTION, DISTRIBUTION OR UNAUTHORIZED USE OF THIS DOCUMENT OR ANY PARTS WITHIN THIS DOCUMENT ARE FORBIDDEN WITHOUT THE WRITTEN CONSENT OF VERTIV GROUP CORP.

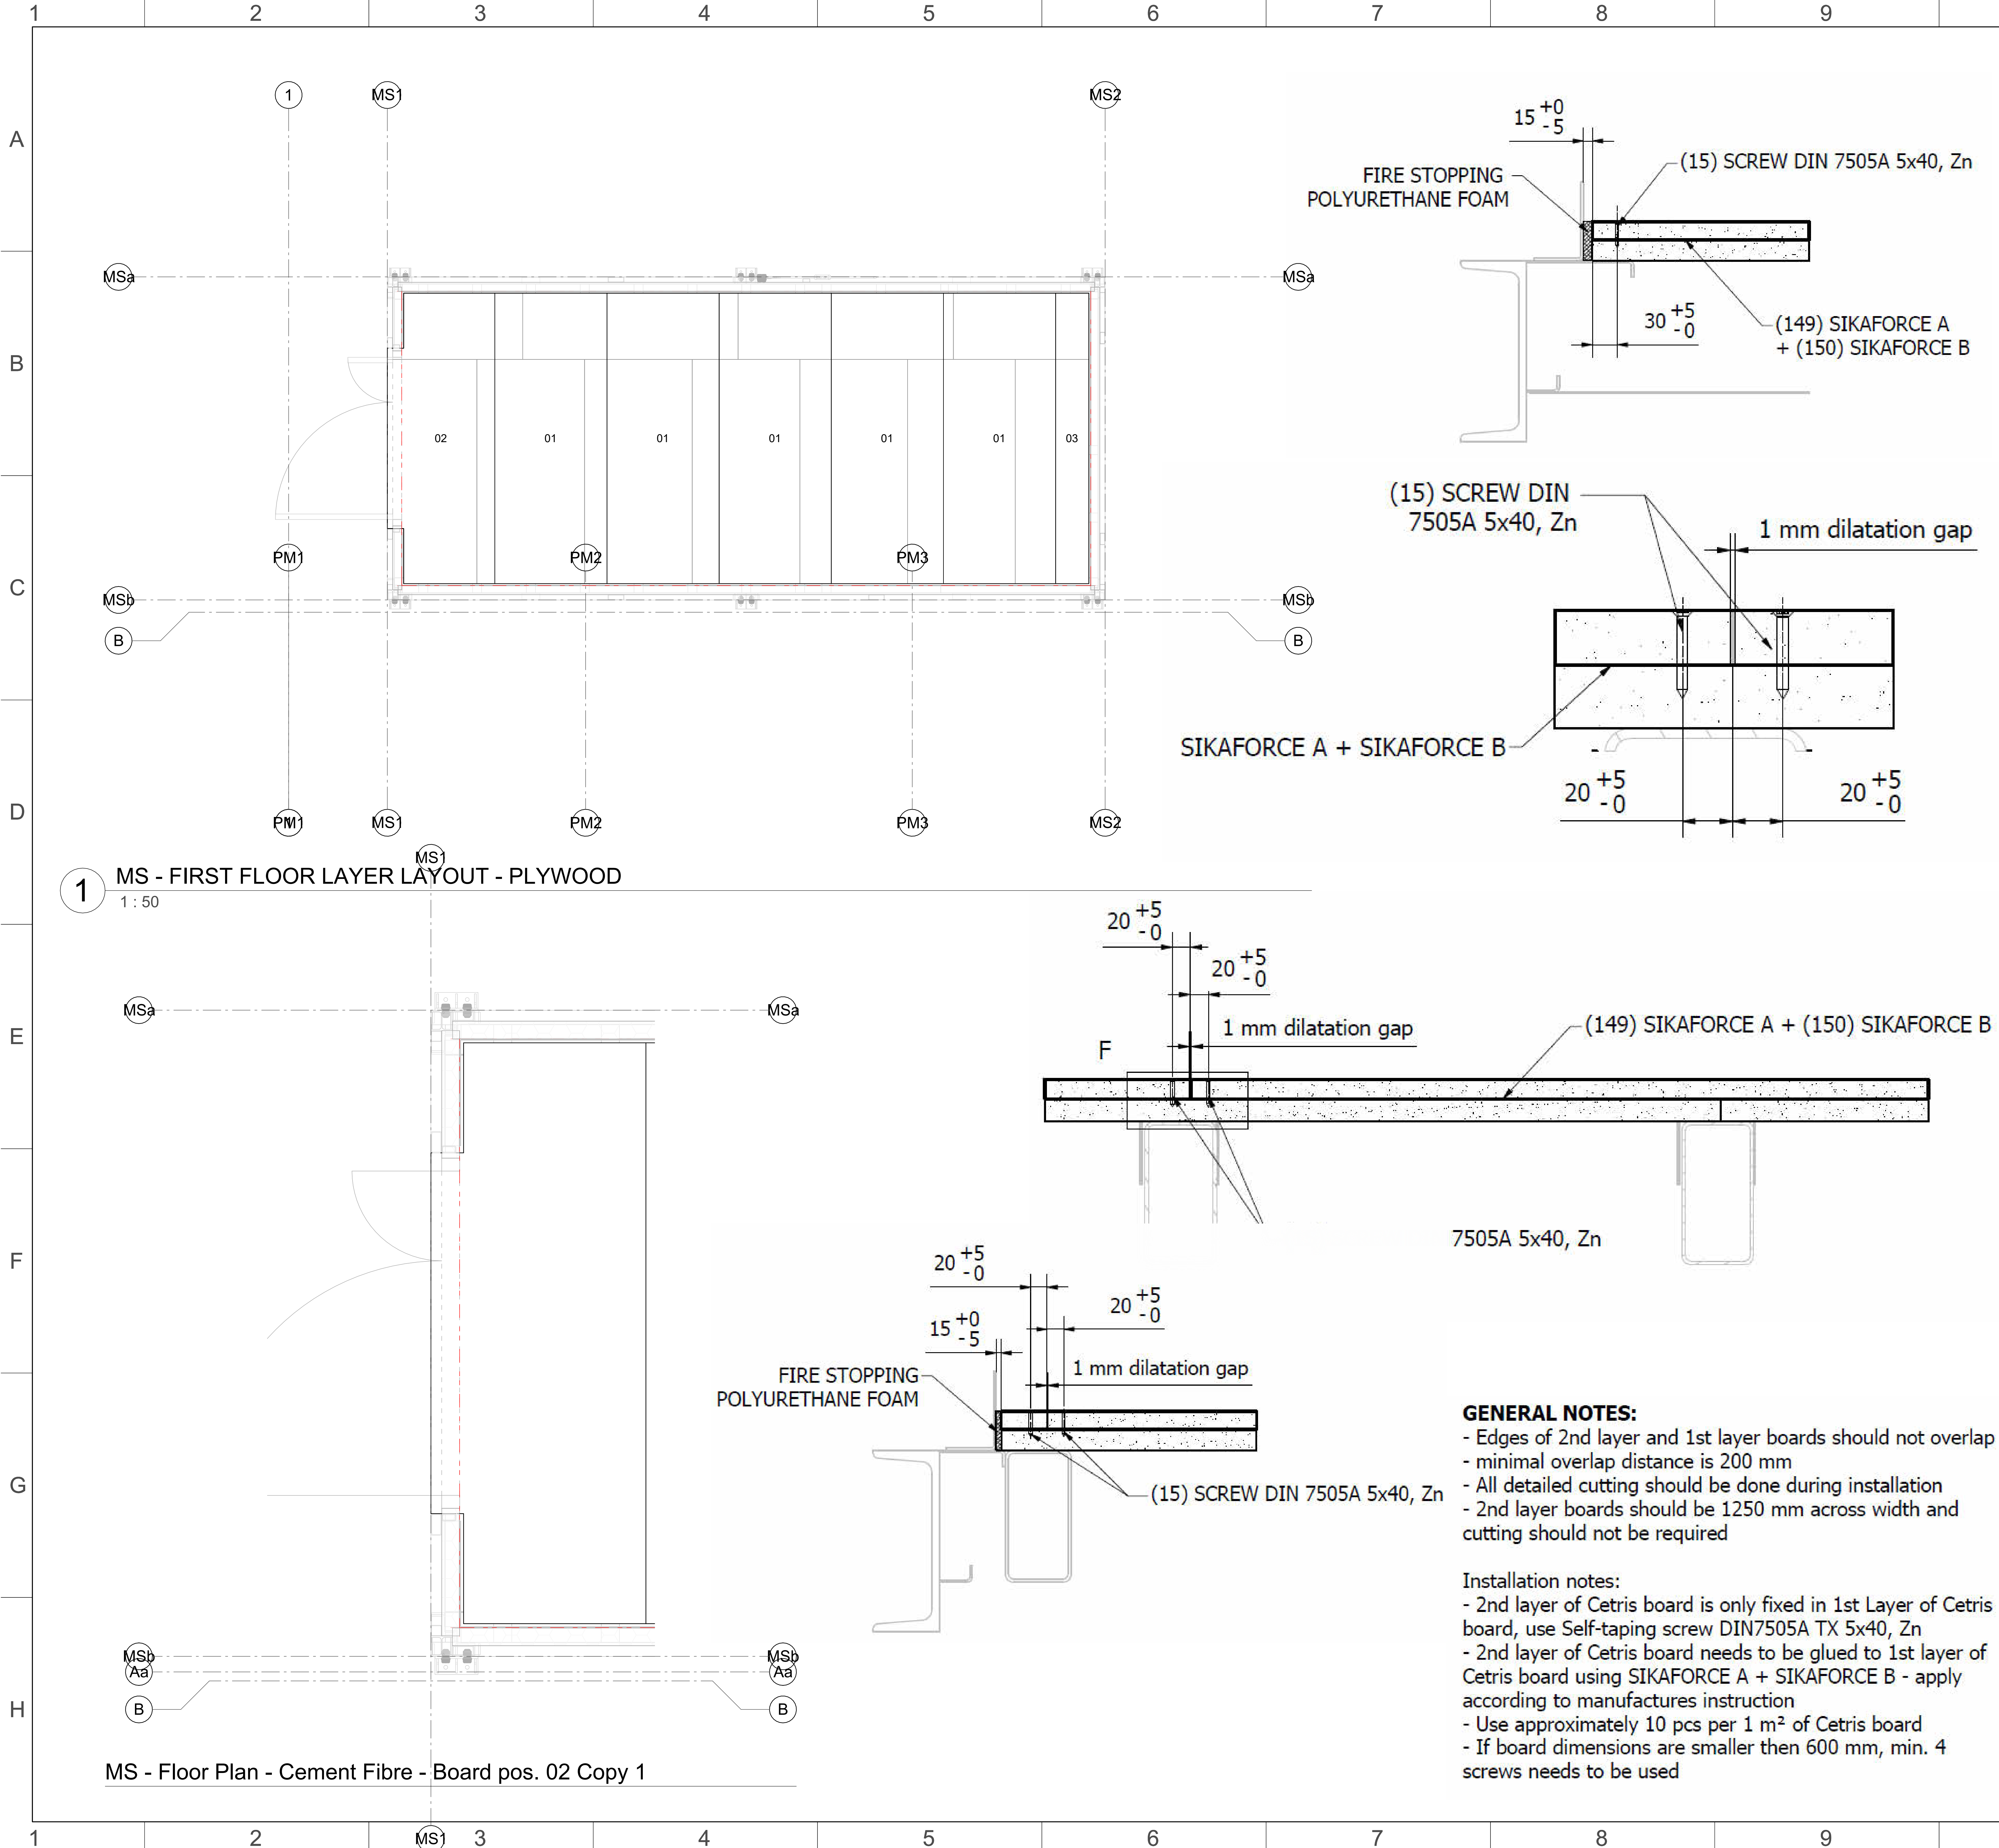

KEYNOTES

ASI - MS CEMENT FIBRE BOARD			
Mark	Height Manual [mm]	Width Manual [mm]	Count [pcs]
01	3236	1250	5
02	3236	1198	1
03	3236	370	1
Grand total: 7			

REFERENCE NOTES

KEY PLAN

R01	FOR MANUFACTURING	2026-05-26
REV.	DESCRIPTION	DATE

PROJECT NAME

ECO DC MONALISA

DRAWING NAME

MS – SECOND FLOOR LAYER LAYOUT – CEMENT FIBRE

PREPARED (ALSO SUBJECT RESPONSIBLE IF OTHER)

I. PUTICA / K. KOZINA / V. SPANIC

DOCUMENT RESPONSIBLE / APPROVED

M. PACAK / J. CICVARIC

CAD / BIM SYSTEM

AUTODESK REVIT 2025

DOCUMENT NUMBER

ASI-103-MS

SHEET 1 OF 1

REVISION

R01