


LEGAL DISCLAIMER: THIS DOCUMENT AND THE CONTENTS HEREIN ARE CONFIDENTIAL AND THE SOLE PROPERTY OF VERTIV GROUP CORP. REPRODUCTION, DISTRIBUTION OR UNAUTHORIZED USE OF THIS DOCUMENT OR ANY PARTS WITHIN THIS DOCUMENT ARE FORBIDDEN WITHOUT THE WRITTEN CONSENT OF VERTIV GROUP CORP.

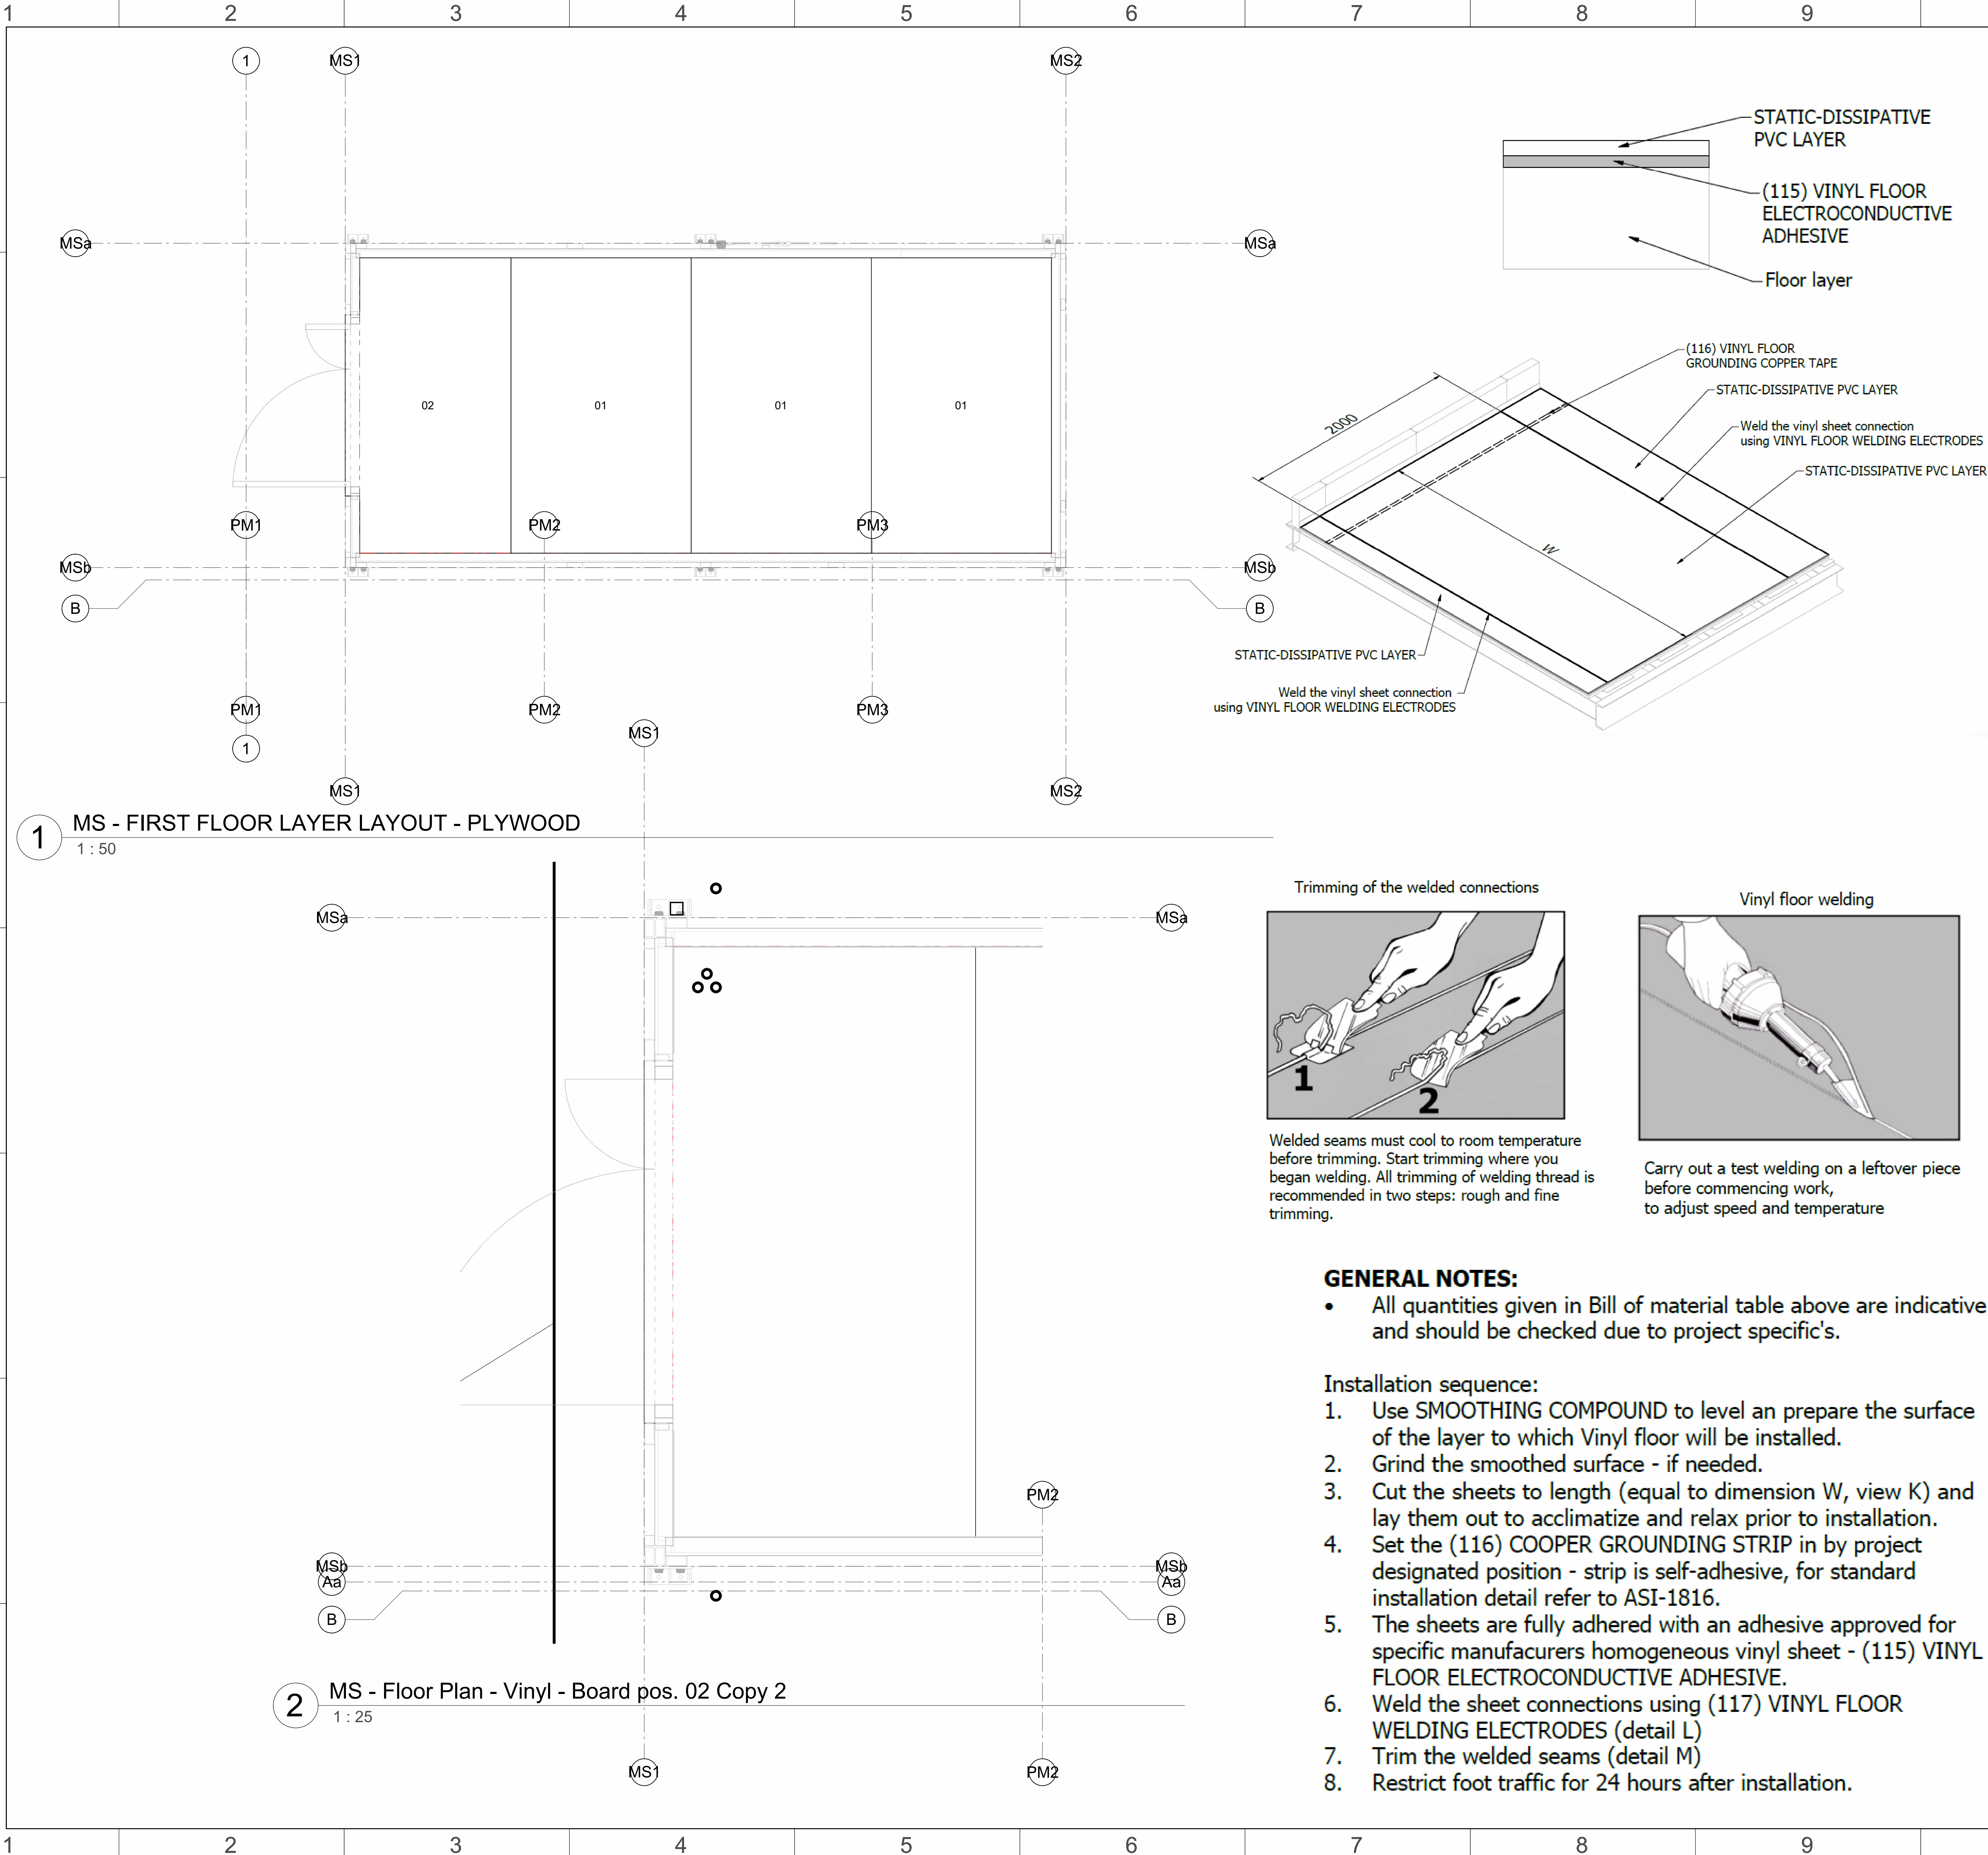

VERTIV

PROJECT NAME
ECO DC MONALISA

DRAWING NAME
MS – THIRD FLOOR LAYER LAYOUT – VINYL

PREPARED (ALSO SUBJECT RESPONSIBLE IF OTHER)
I. PUTICA / K. KOZINA / V. SPANIC

DOCUMENT RESPONSIBLE / APPROVED
M. PACAK / J. CICVARIC

CAD / BIM SYSTEM
AUTODESK REVIT 2025

DOCUMENT NUMBER
ASI-107-MS

SHEET 1 OF 1

REVISION
R01

SHEET SIZE
A2

DRAWING SCALE
As indicated

DATE (YYYYMM-DD)
2026-05-26

REV. DESCRIPTION DATE

R01 FOR MANUFACTURING 2026-05-26