




LEGAL DISCLAIMER: THIS DOCUMENT AND THE CONTENTS HEREIN ARE CONFIDENTIAL AND THE SOLE PROPERTY OF VERTIV GROUP CORP. REPRODUCTION, DISTRIBUTION OR UNAUTHORIZED USE OF THIS DOCUMENT OR ANY PARTS WITHIN THIS DOCUMENT ARE FORBIDDEN WITHOUT THE WRITTEN CONSENT OF VERTIV GROUP CORP.

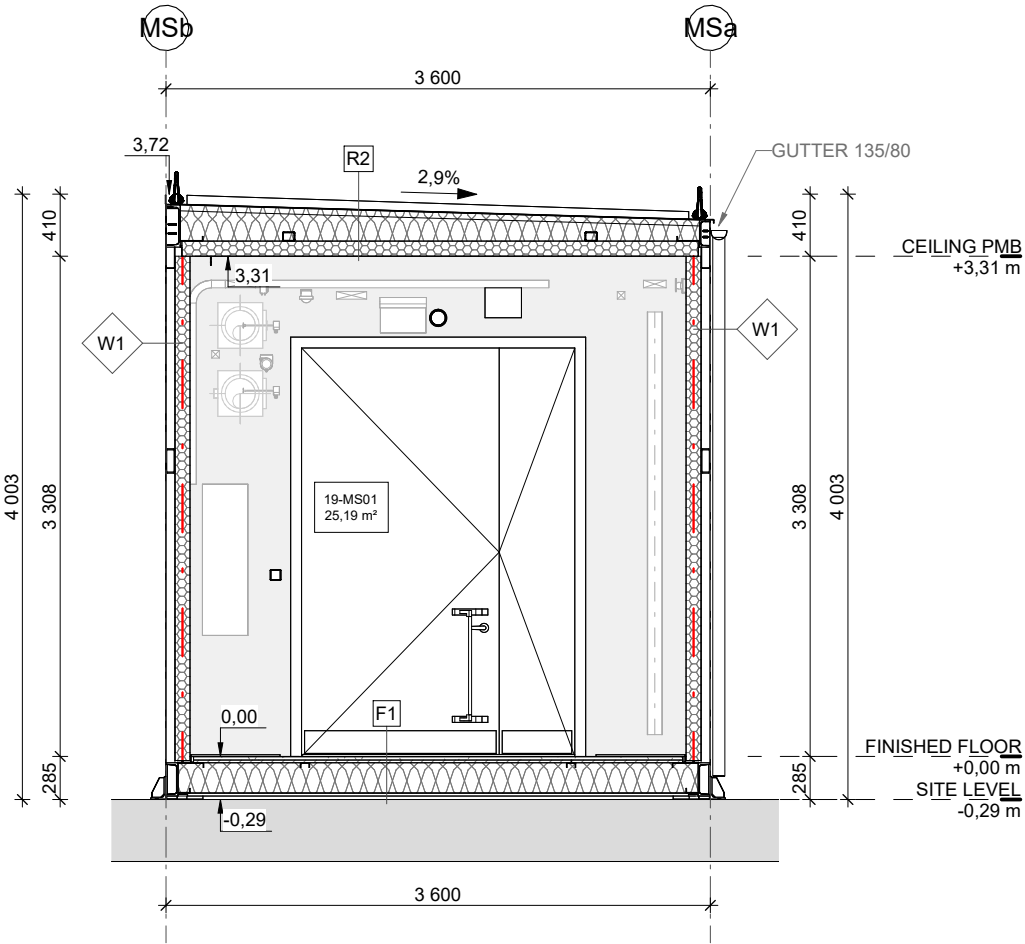


1 MS MODULE - SECTION 1-1
1 : 50

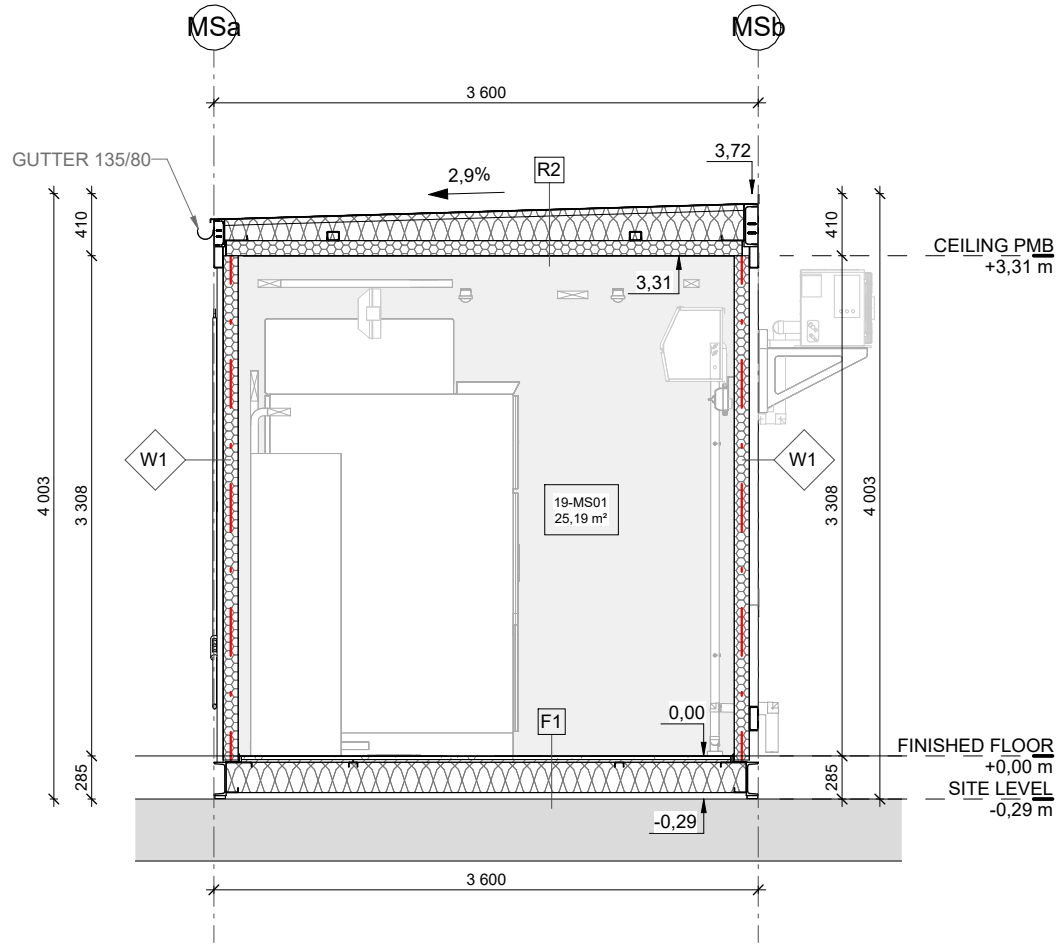


2 MS MODULE - SECTION 2-2
1 : 50

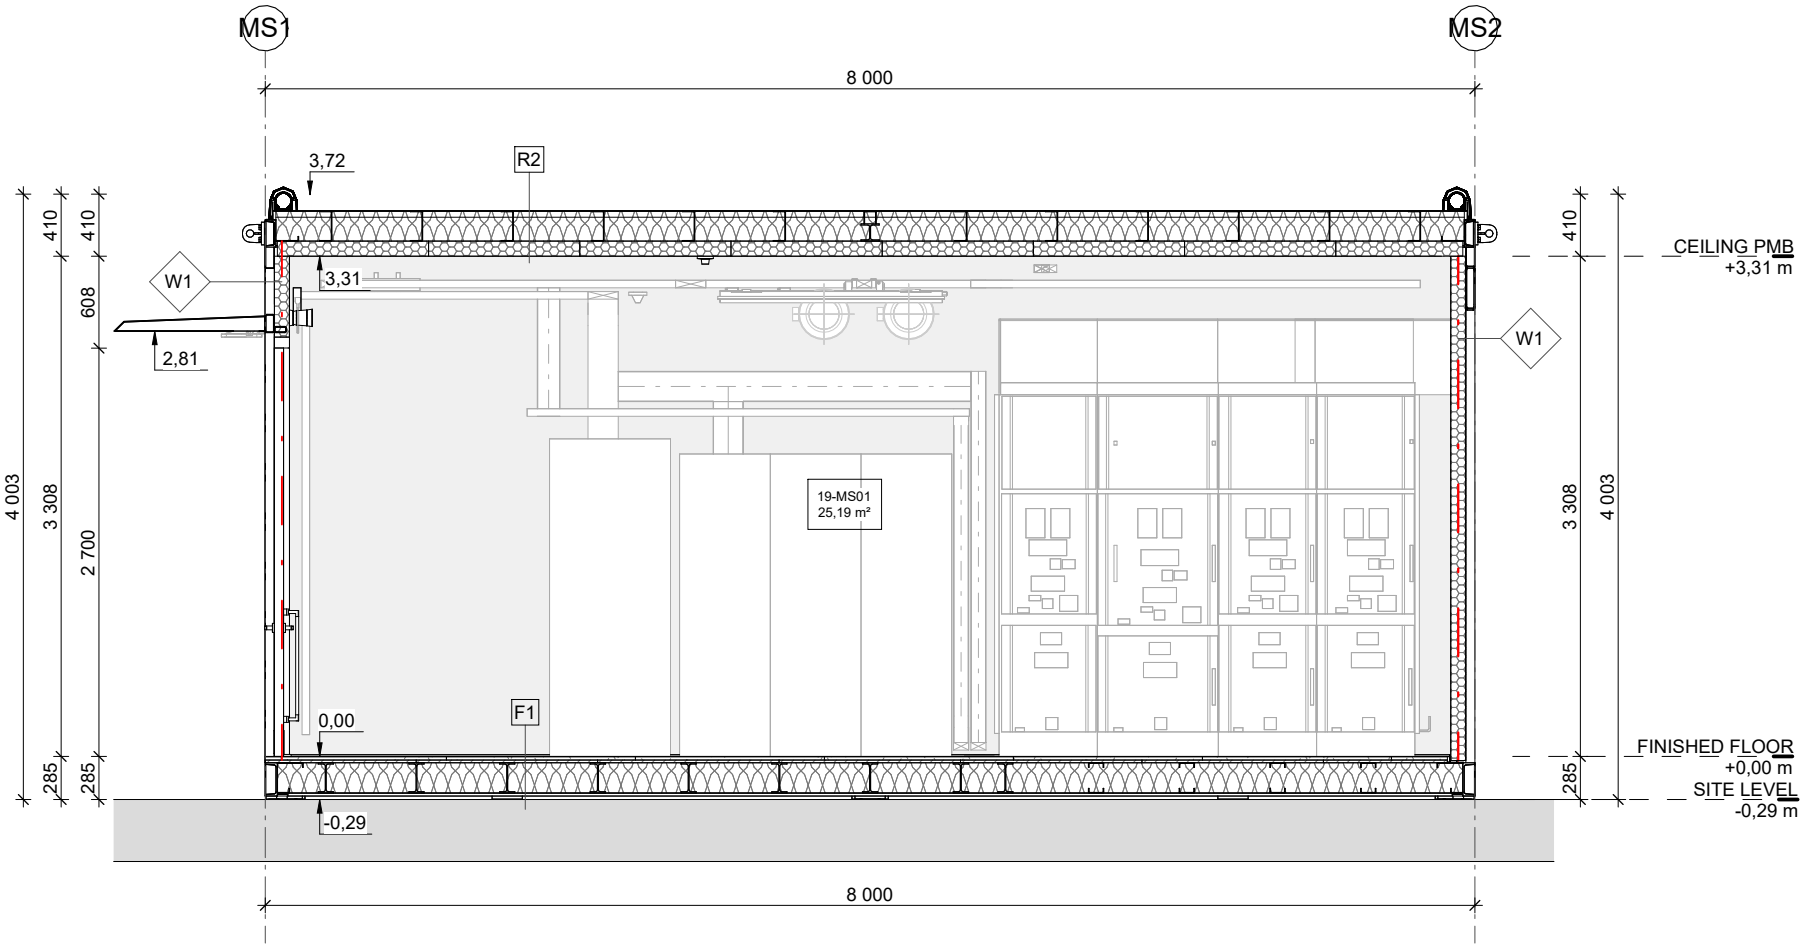

A MS MODULE - SECTION A-A
1 : 50

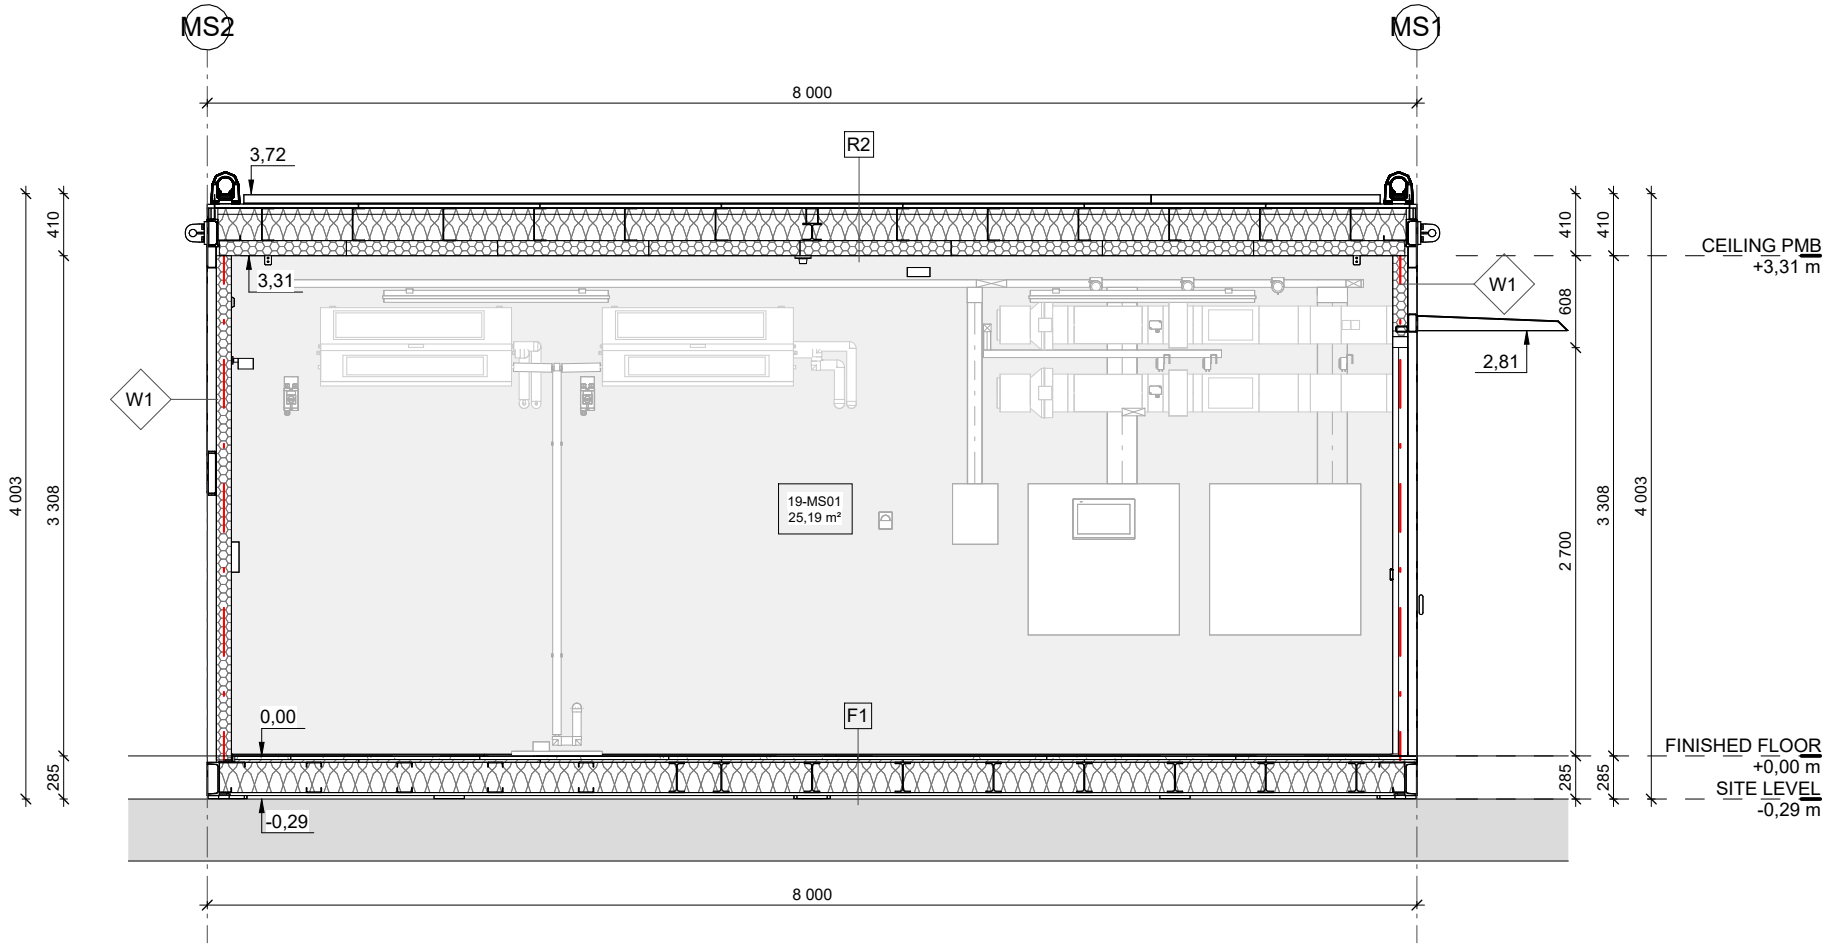

B MS MODULE - SECTION B-B
1 : 50

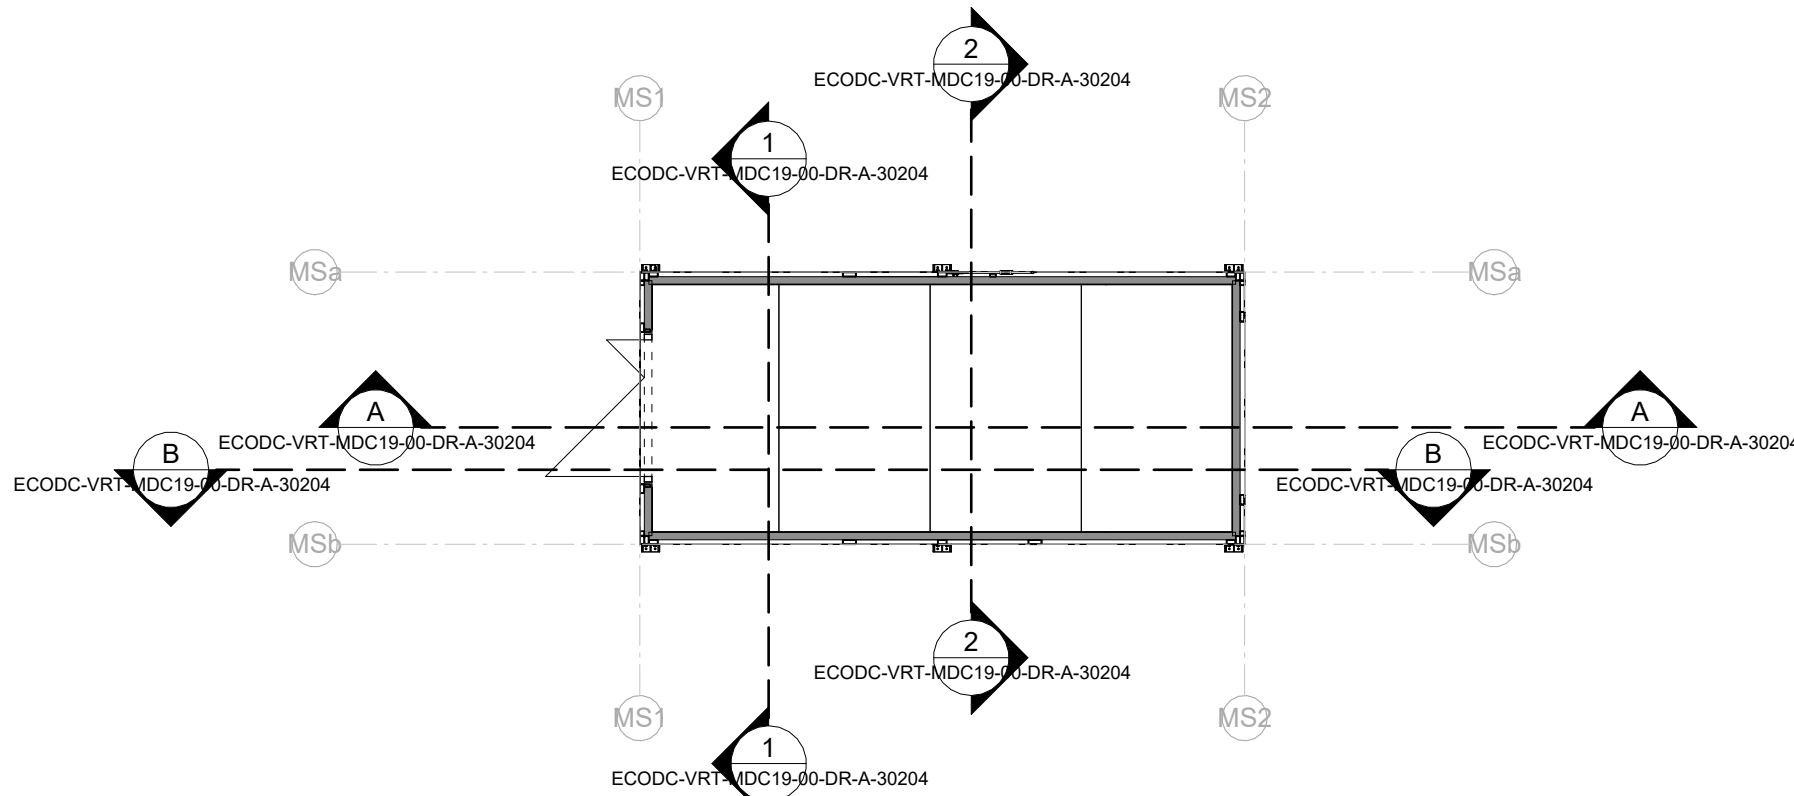

KEY PLAN - MS MODULE SECTION POSITIONS
1 : 100

KEYNOTES

FLOOR SCHEDULE - MS MODULE

Type Mark	Description	Fire Rating
F1	inside to outside: - VINYL 2mm - CEMENT FIBRE BOARD 22mm - PLYWOOD 18mm - FLOOR STRUCTURE with MINERAL WOOL INFILL 200mm - VAPOUR CONTROL LAYER 0.2mm - STEEL SHEET 0.8mm - U=0,16 W/m2K	N/A

ROOF SCHEDULE - MS MODULE

Type Mark	Description	Fire Rating
R2	inside to outside: - PREFABRICATED SANDWICH PANEL, TRIMOTERM PERFORM C.F.T.V. RAL 9006 (EXT), RAL 9002 (INT) 100mm - VAPOUR CONTROL LAYER 0.2mm - THERMAL INSULATION (fully infilled gap 140-240mm) - GALVANIZED STEEL SHEET, CONTINUOUSLY WELDED, C4M, 3mm - U=0,15 W/m2K	N/A

WALL SCHEDULE - MS MODULE

Type Mark	Keynote Description	Fire Rating
W1	- PREFABRICATED SANDWICH PANEL, TRIMOTERM PERFORM C.F.T.V. RAL 9006 (EXT), RAL 9002 (INT) 100mm	EI 60 (where indicated)
U=0,40 W/m2K		

GENERAL NOTE

- ARCHITECTURAL LAYERS ARE LISTED FROM INSIDE TO OUTSIDE

- VERTIV RESERVES THE RIGHT TO INSTALL ANY OTHER BRAND OF SANDWICH PANEL, MINERAL WOOL OF EQUAL CHARACTERISTICS AND QUALITY, INSTEAD OF THE PRODUCT SPECIFIED IN THE KEYNOTES, DEPENDING ON THE AVAILABILITY OF THE PRODUCT IN THE MOMENT OF ORDERING

- WHERE WALL IS REQUIRED TO PROVIDE FIRE RESISTANCE FROM BOTH SIDES, AND WHERE STRUCTURE LACKS ALTERNATIVE FIRE PROTECTION, IN INTUMESCENT COATING SHALL BE APPLIED TO THE STRUCTURAL ELEMENTS

- ALL FACADE PANELS ARE INSTALLED VERTICALLY UNLESS OTHERWISE SPECIFIED

- THIS DRAWING SHOWS A SINGLE MS MODULE AND IS TYPICAL FOR ALL MS MODULES IN THE PROJECT. EACH MODULE, ALONG WITH ITS CORRESPONDING EQUIPMENT, PENETRATIONS, AND MEP SERVICES, IS IDENTIFIED BY A UNIQUE TAG.

- BUILDING LAYERS AND STRUCTURE SURFACE COLOUR:
RAL 9006 EXTERIOR
RAL 9002 INTERIOR

- ANTICORROSION LEVEL:
C4M EXTERIOR
C2M INTERIOR

LEGEND

 FIRE COMPARTMENT BORDER REIM 60

 FIRE COMPARTMENT BORDER EI 60

 FIRE COMPARTMENT BORDER EI 30

 TRANSPORT COLUMNS

 OUT OF VERTIV SCOPE

 SELF-SUPPORTING CEILING

 PUSH BUTTON FOR ELECTROMECHANICALLY OPERATED DOORS (BOTH SIDES OF WALL) FOR EXACT POSITION, REFER TO DOOR SCHEME.

KEY PLAN

R03	CD SET - FOR INFORMATION	2026-09-11
R02	CD SET - FOR INFORMATION	2026-07-24
R01	DD SET - FOR INFORMATION	2026-05-20
REV.	DESCRIPTION	DATE

VERTIV™

PROJECT NAME

ECO DC MONALISA

DRAWING NAME

ARCHITECTURAL SECTION VIEWS
- MS MODULE

PREPARED (ALSO SUBJECT RESPONSIBLE IF OTHER)

L. MAVREK / K. KOZINA

DOCUMENT RESPONSIBLE / APPROVED

M. PACAK

DOCUMENT NUMBER

ECODC-VRT-MDC19-00-DR-A-30204

CAD / BIM SYSTEM

AUTODESK REVIT 2025

DOCUMENT NUMBER

ECODC-VRT-MDC19-00-DR-A-30204

SHEET SIZE

A1

DRAWING SCALE

1 : 50

DATE (YYYYMM-DD)

2026-09-11

SHEET 1 OF 1

REVISION

R03