



LEGAL DISCLAIMER: THIS DOCUMENT AND THE CONTENTS HEREIN ARE CONFIDENTIAL AND THE SOLE PROPERTY OF VERTIV GROUP CORP. REPRODUCTION, DISTRIBUTION OR UNAUTHORIZED USE OF THIS DOCUMENT OR ANY PARTS WITHIN THIS DOCUMENT ARE FORBIDDEN WITHOUT THE WRITTEN CONSENT OF VERTIV GROUP CORP.

PENETRATION SCHEDULE - MS MODULE FLOOR PLAN									
BUILDING NUMBER	ROOM NUMBER	GRID	PENETRATION MARK	PENETRATION TYPE	PENETRATION DESCRIPTION	PENETRATION DETAIL TYPE	FINAL OPENING DIAMETER	FINAL OPENING HEIGHT	FINAL OPENING WIDTH
19	MS01	FFL	E01	Roxtec GH 5x1 GALV.	MVS GPL	P03		285	128
19	MS01	FFL	E02	Hilti	MV Incomer	P15		340	590
19	MS01	FFL	E03	Hilti	MV Outgoing Cables	P15		340	440
19	MS01	FFL	E04	Hilti	MV Outgoing Cables	P15		340	440

1 ARCHITECTURAL BUILDING PENETRATIONS – MS MODULE – FLOOR PLAN
1 : 50

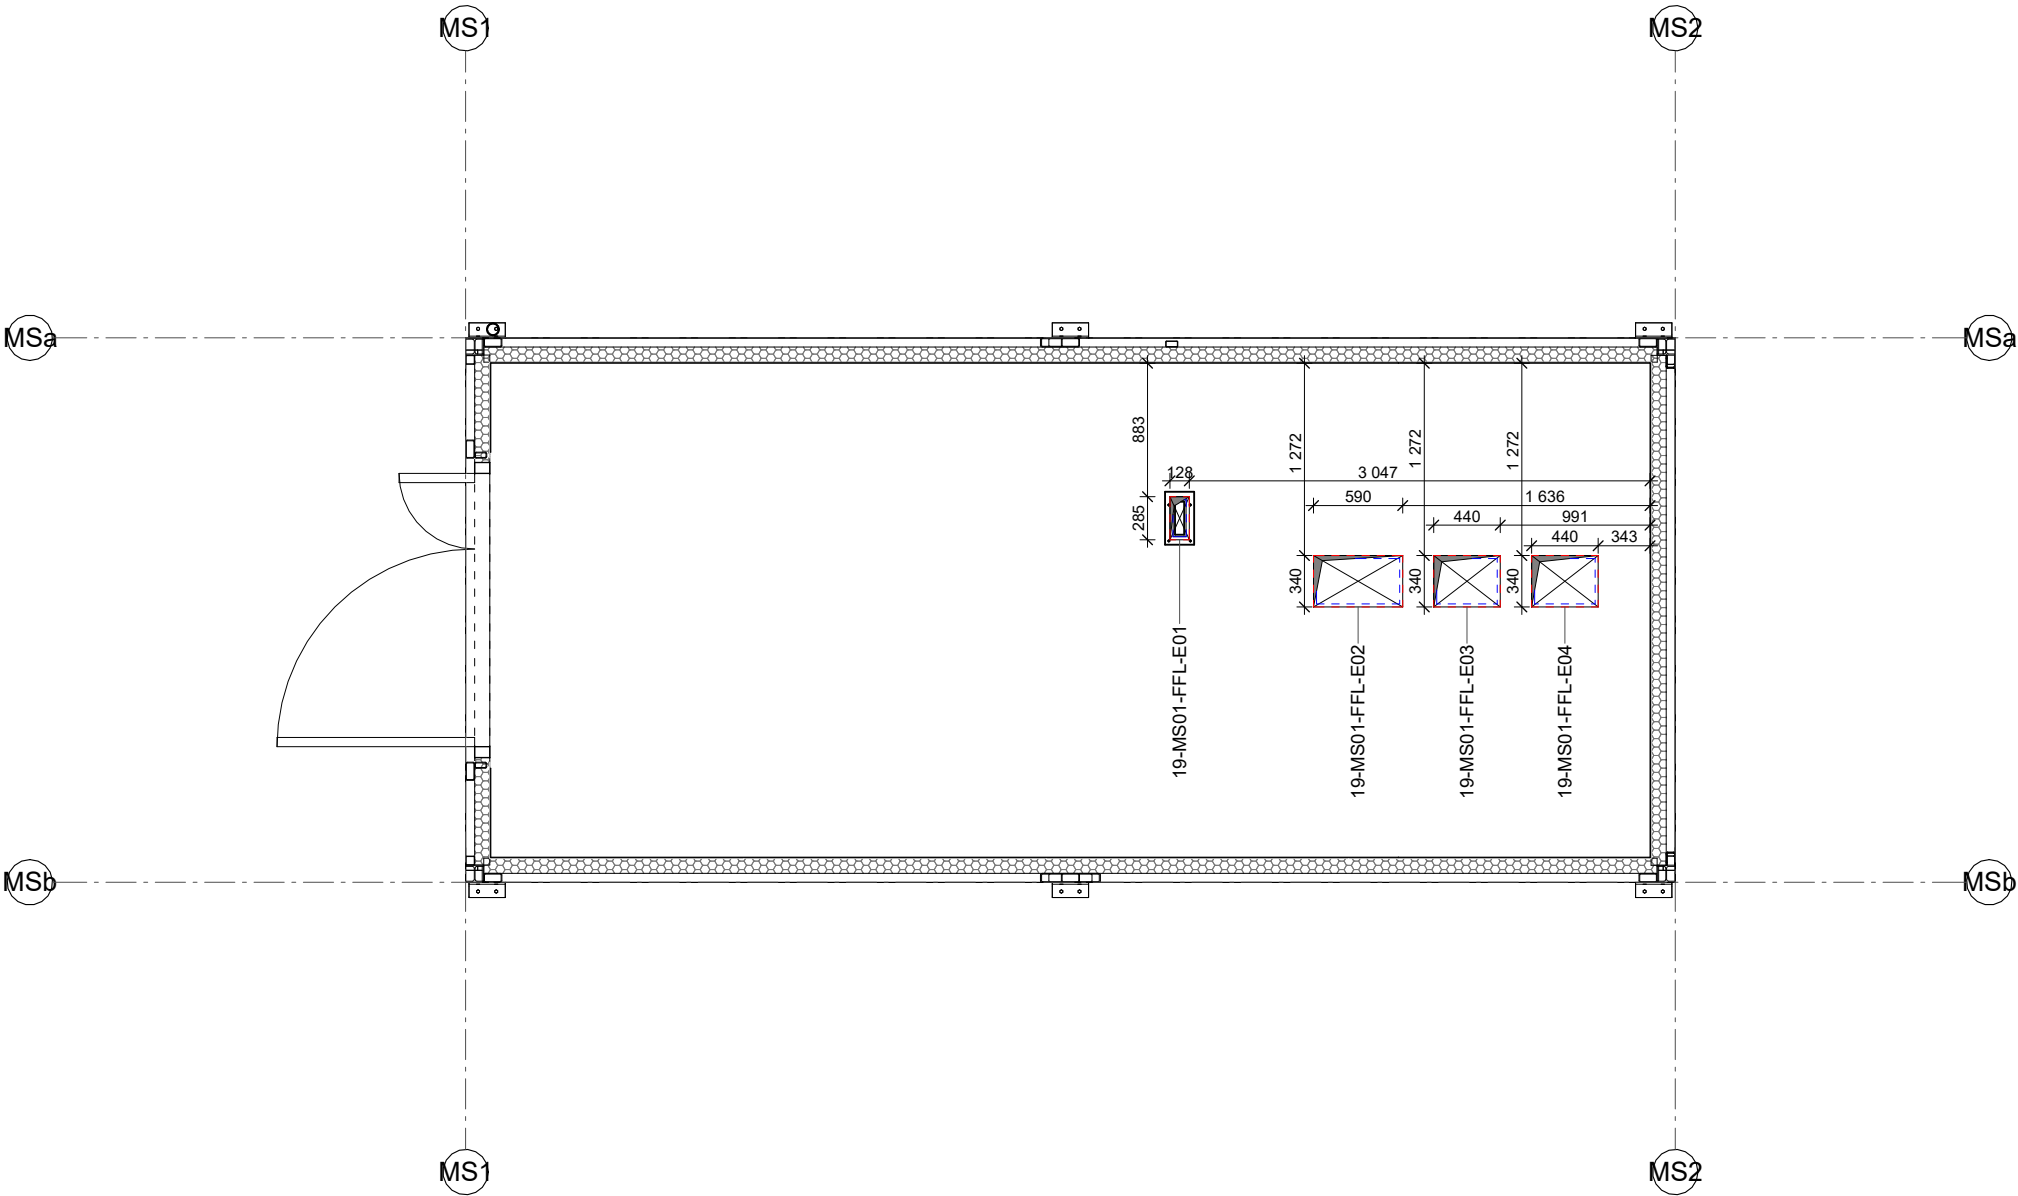

KEYNOTES

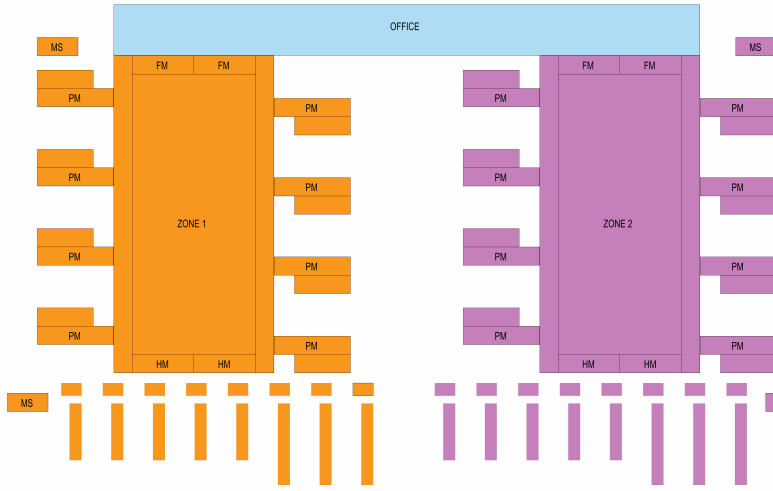

R02	CD SET - FOR INFORMATION	2026-09-11
R01	CD SET - FOR INFORMATION	2026-07-24
REV.	DESCRIPTION	DATE



PROJECT NAME

ECO DC MONALISA

DRAWING NAME

ARCHITECTURAL BUILDING PENETRATIONS – MS MODULE – FLOOR PLAN

PREPARED (ALSO SUBJECT RESPONSIBLE IF OTHER)

L. MAVREK / K. KOZINA

DOCUMENT RESPONSIBLE / APPROVED

M. PACAK

CAD / BIM SYSTEM AUTODESK REVIT 2025

DOCUMENT NUMBER
ECODC-VRT-MDC19-00-DR-A-40209

SHEET 1 OF 1

REVISION

SHEET SIZE
A2

DRAWING SCALE
1:50

DATE (YYYY-MM-DD)
2026-09-11

R02