




LEGAL DISCLAIMER: THIS DOCUMENT AND THE CONTENTS HEREIN ARE CONFIDENTIAL AND THE SOLE PROPERTY OF VERTIV GROUP CORP. REPRODUCTION, DISTRIBUTION OR UNAUTHORIZED USE OF THIS DOCUMENT OR ANY PARTS WITHIN THIS DOCUMENT ARE FORBIDDEN WITHOUT THE WRITTEN CONSENT OF VERTIV GROUP CORP.

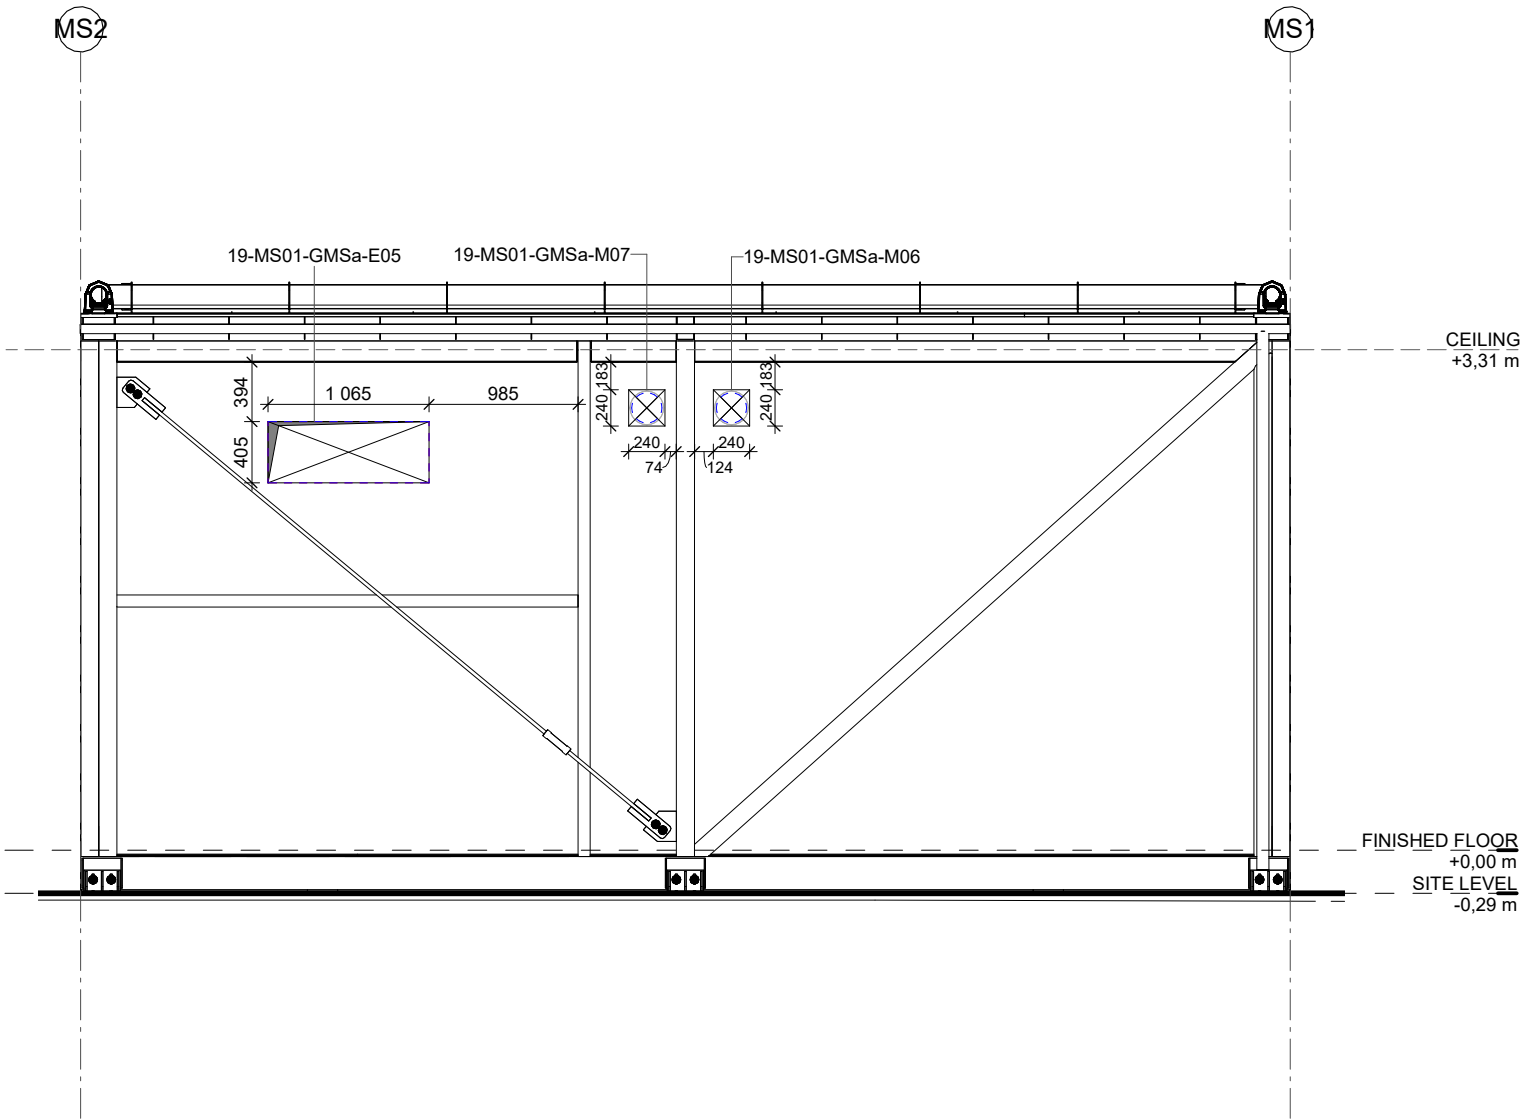


1 MS-PEN ELEVATION NORTH
1 : 50

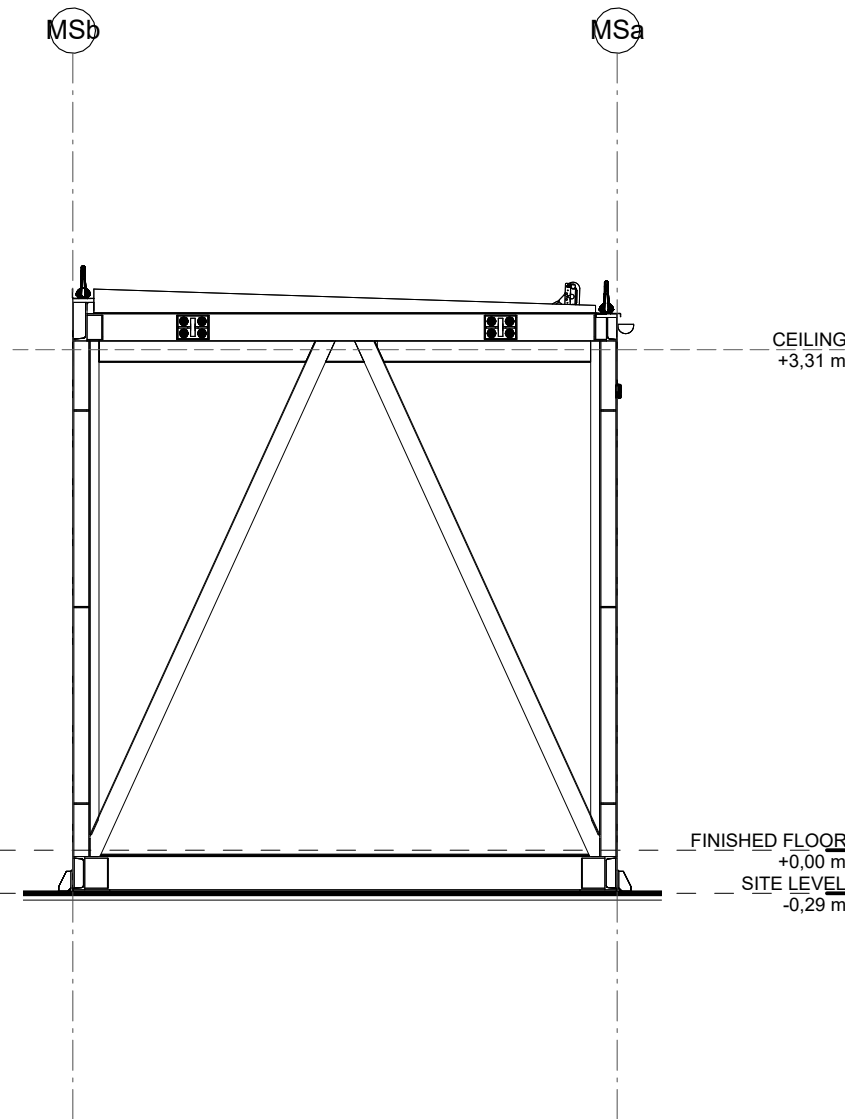

3 MS-PEN ELEVATION EAST
1 : 50

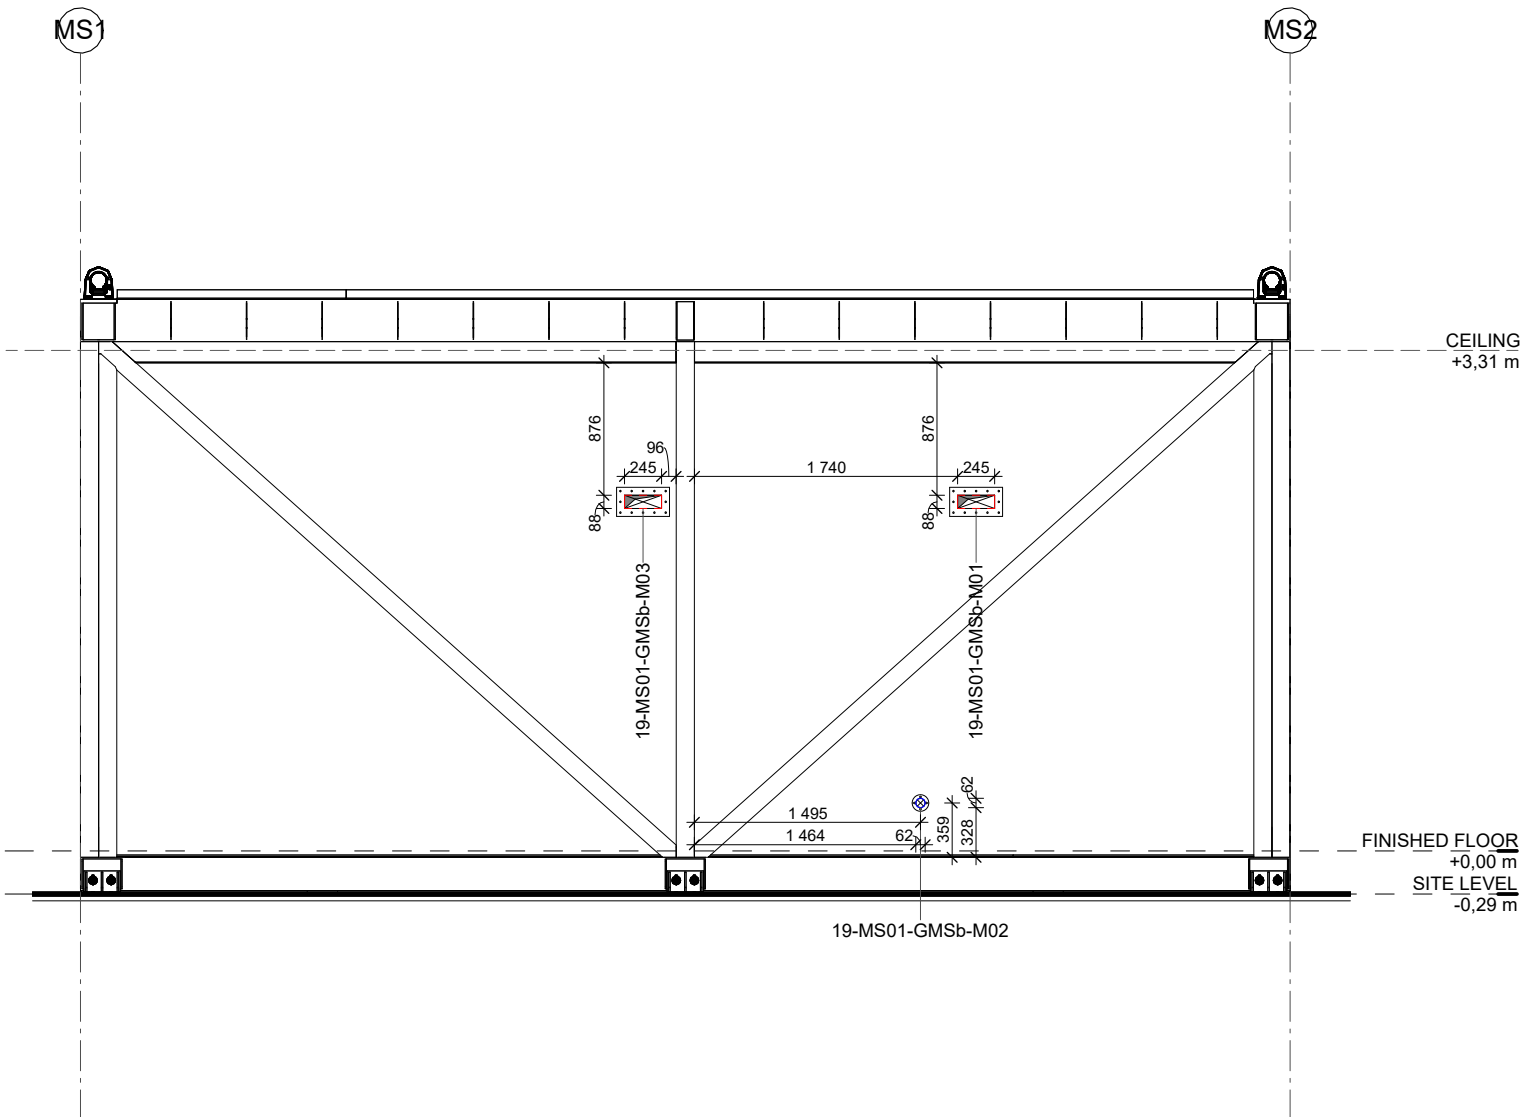


2 MS-PEN ELEVATION SOUTH
1 : 50

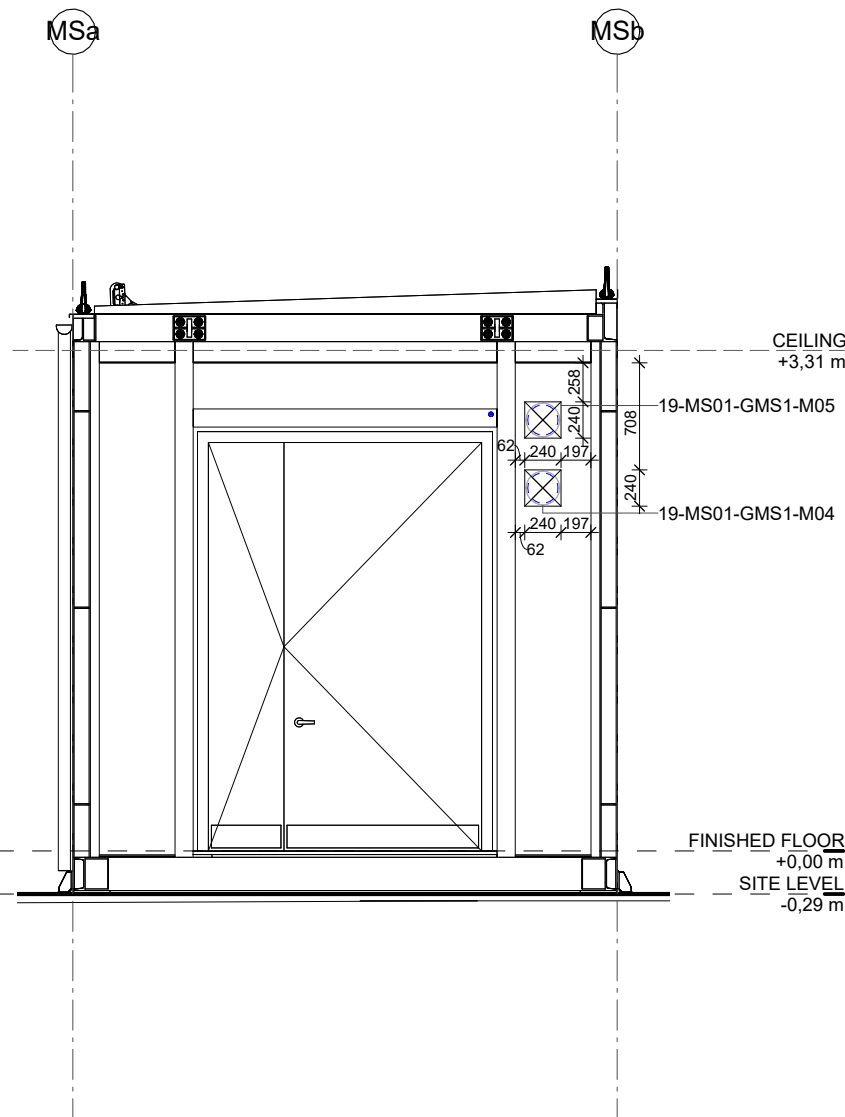

4 MS-PEN ELEVATION WEST
1 : 50


PENETRATION SCHEDULE - MS MODULE

BUILDING NUMBER	ROOM NUMBER	GRID	PENETRATION MARK	PENETRATION TYPE	PENETRATION DESCRIPTION	PENETRATION DETAIL TYPE	FINAL OPENING DIAMETER	FINAL OPENING HEIGHT	FINAL OPENING WIDTH
19	MS01	GMSa	E05	Opening	Arc Blast Channel	P13		405	1065
19	MS01	GMSb	M01	Roxtec GHM 5x1 AISI	Roxtec	P01		88	245
19	MS01	GMSb	M02	Roxtec RS + SLFRS 43	Roxtec	P02	62		
19	MS01	GMSb	M03	Roxtec GHM 5x1 AISI	Roxtec	P01		88	245
19	MS01	GMS1	M04	Trox FKRS-EU	Fire damper	P06	200	240	240
19	MS01	GMS1	M05	Trox FKRS-EU	Fire damper	P06	200	240	240
19	MS01	GMSa	M06	Trox FKRS-EU	Fire damper	P06	200	240	240
19	MS01	GMSa	M07	Trox FKRS-EU	Fire damper	P06	200	240	240

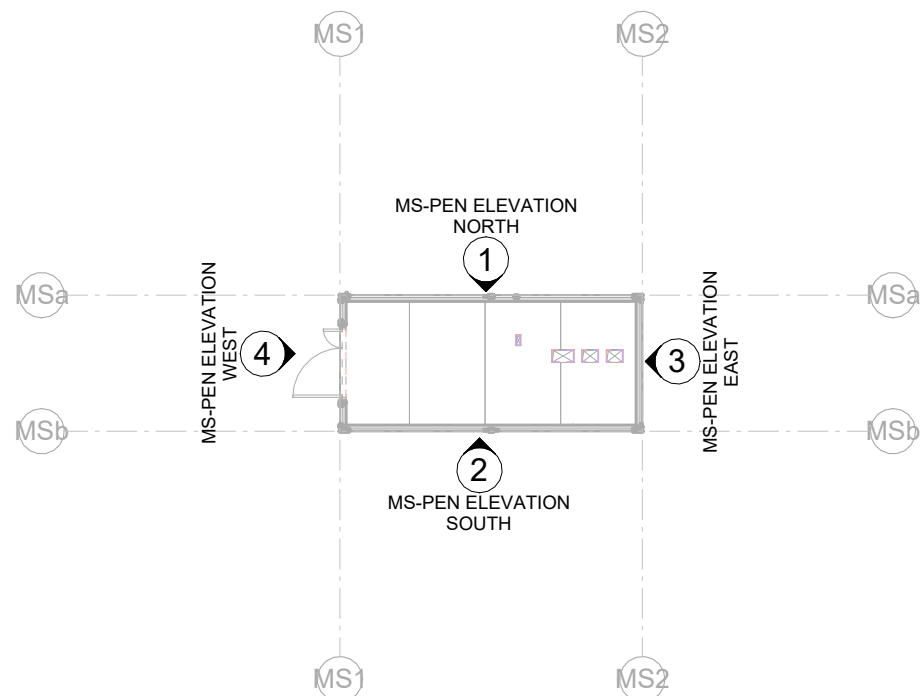

KEYPLAN - MS MODULE - PEN ELEVATION POSITIONS

KEYNOTES

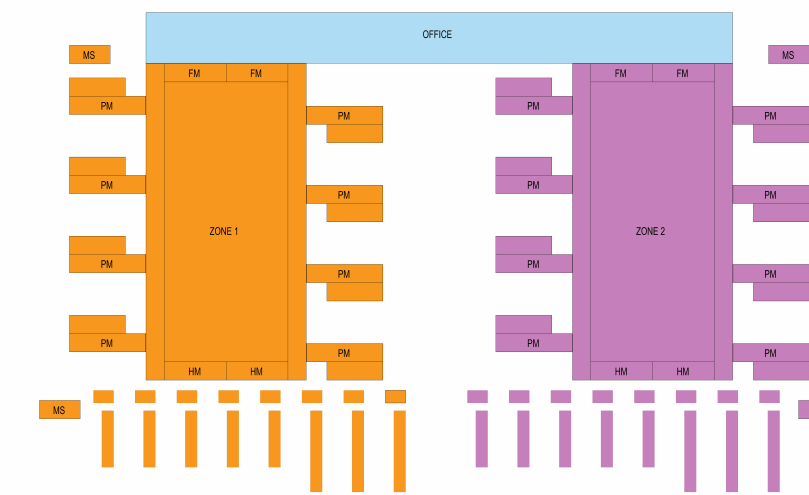

R02	CD SET - FOR INFORMATION	2026-09-11
R01	CD SET - FOR INFORMATION	2026-07-24
REV.	DESCRIPTION	DATE



PROJECT NAME

ECO DC MONALISA

DRAWING NAME

ARCHITECTURAL BUILDING PENETRATIONS – MS MODULE – ELEVATIONS

PREPARED (ALSO SUBJECT RESPONSIBLE IF OTHER)

L. MAVREK / K. KOZINA

DOCUMENT RESPONSIBLE / APPROVED

M. PACAK

CAD / BIM SYSTEM AUTODESK REVIT 2025

DOCUMENT NUMBER	DRAWING SCALE	DATE (YYYYMM-DD)	REVISION
ECODC-VRT-MDC19-00-DR-A-40210	1:50	2026-09-11	R02
SHEET SIZE	DRAWING SCALE	DATE (YYYYMM-DD)	REVISION
A1	1:50	2026-09-11	R02