




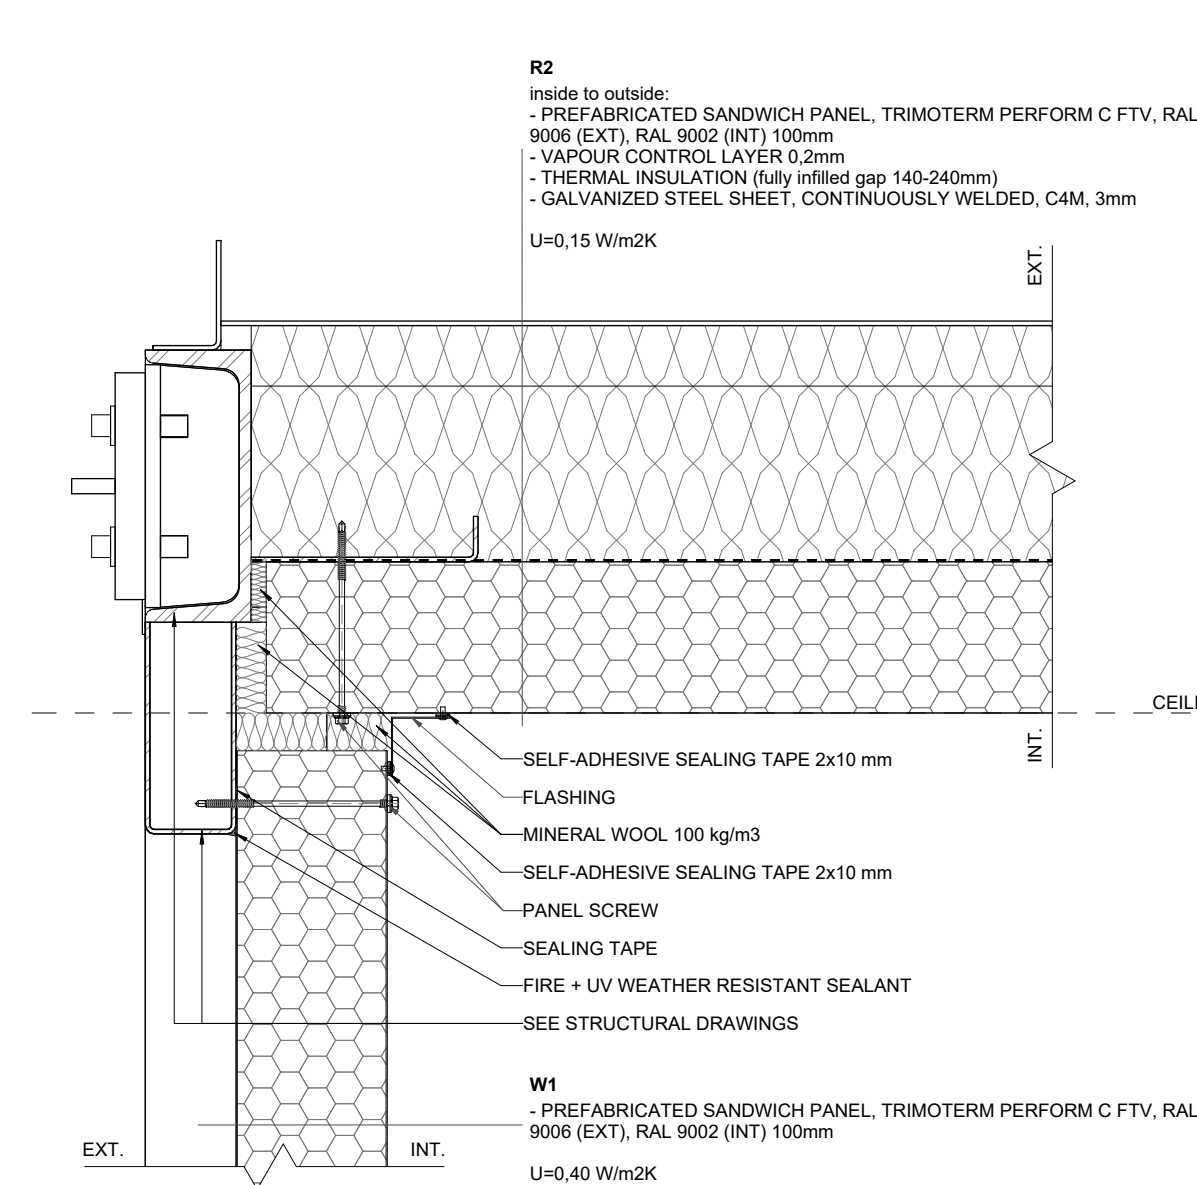


V01 PM/MV/MS - EXT. WALL/ROOF CONNECTION
1:5

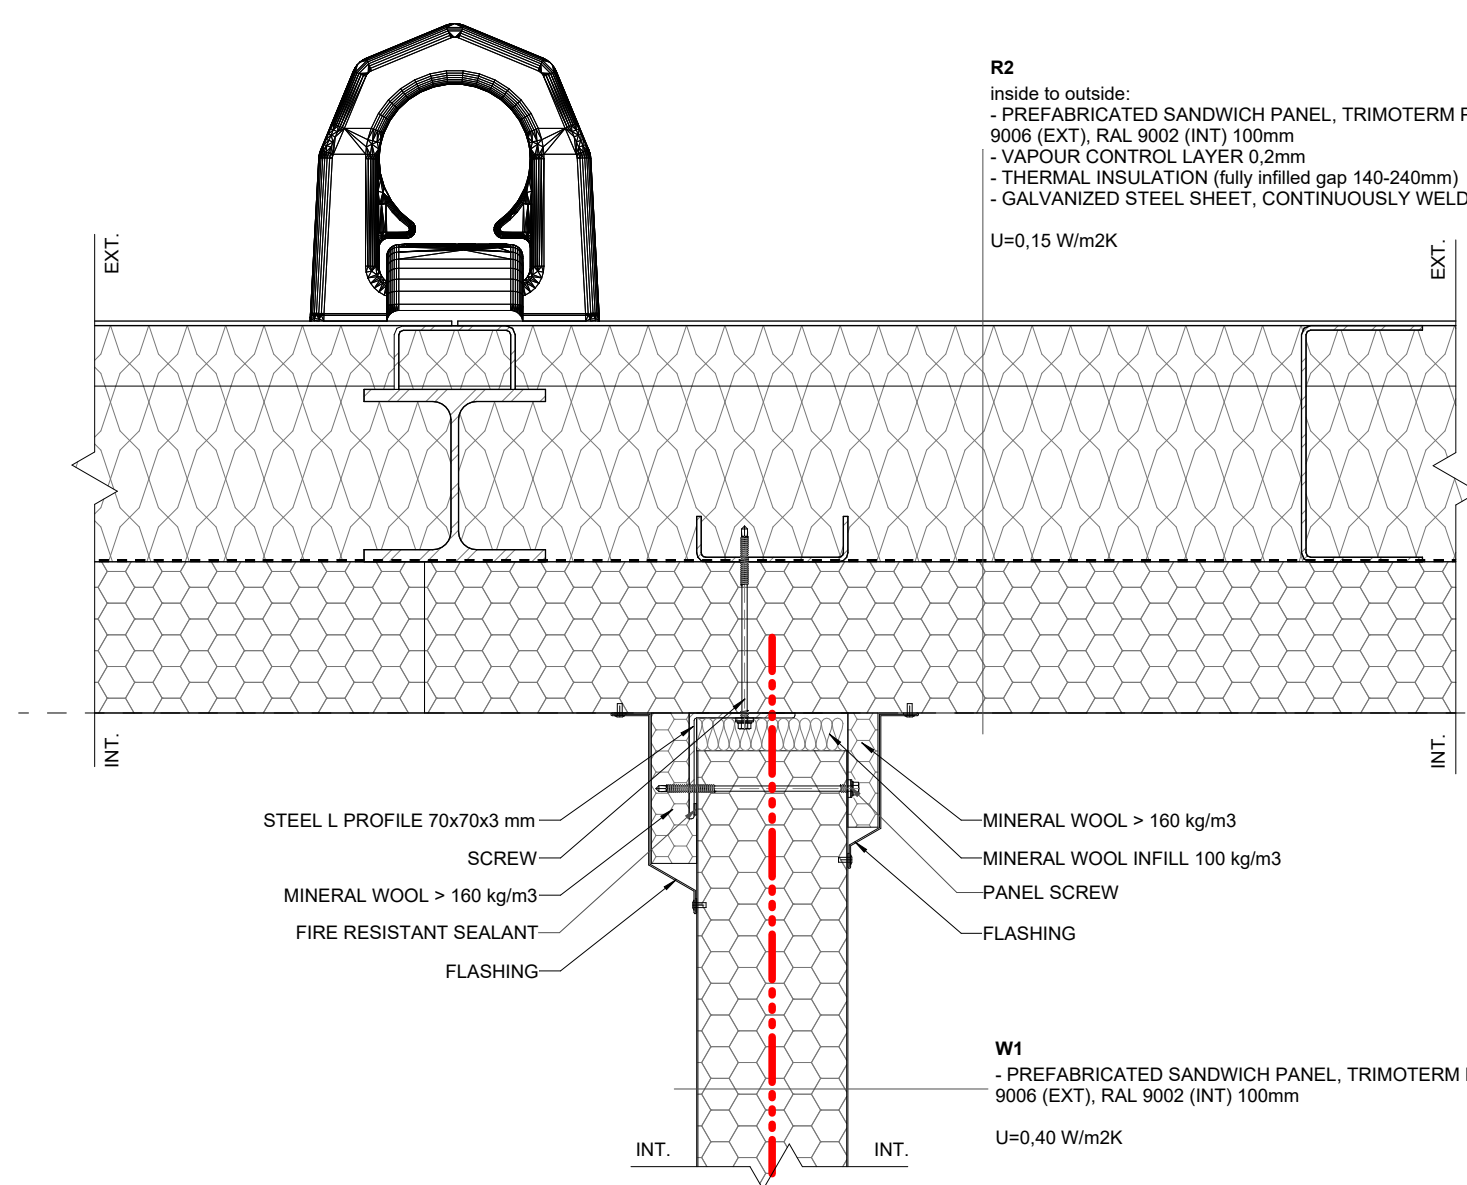


V03 MV - INT. WALL/ROOF CONNECTION
1:5

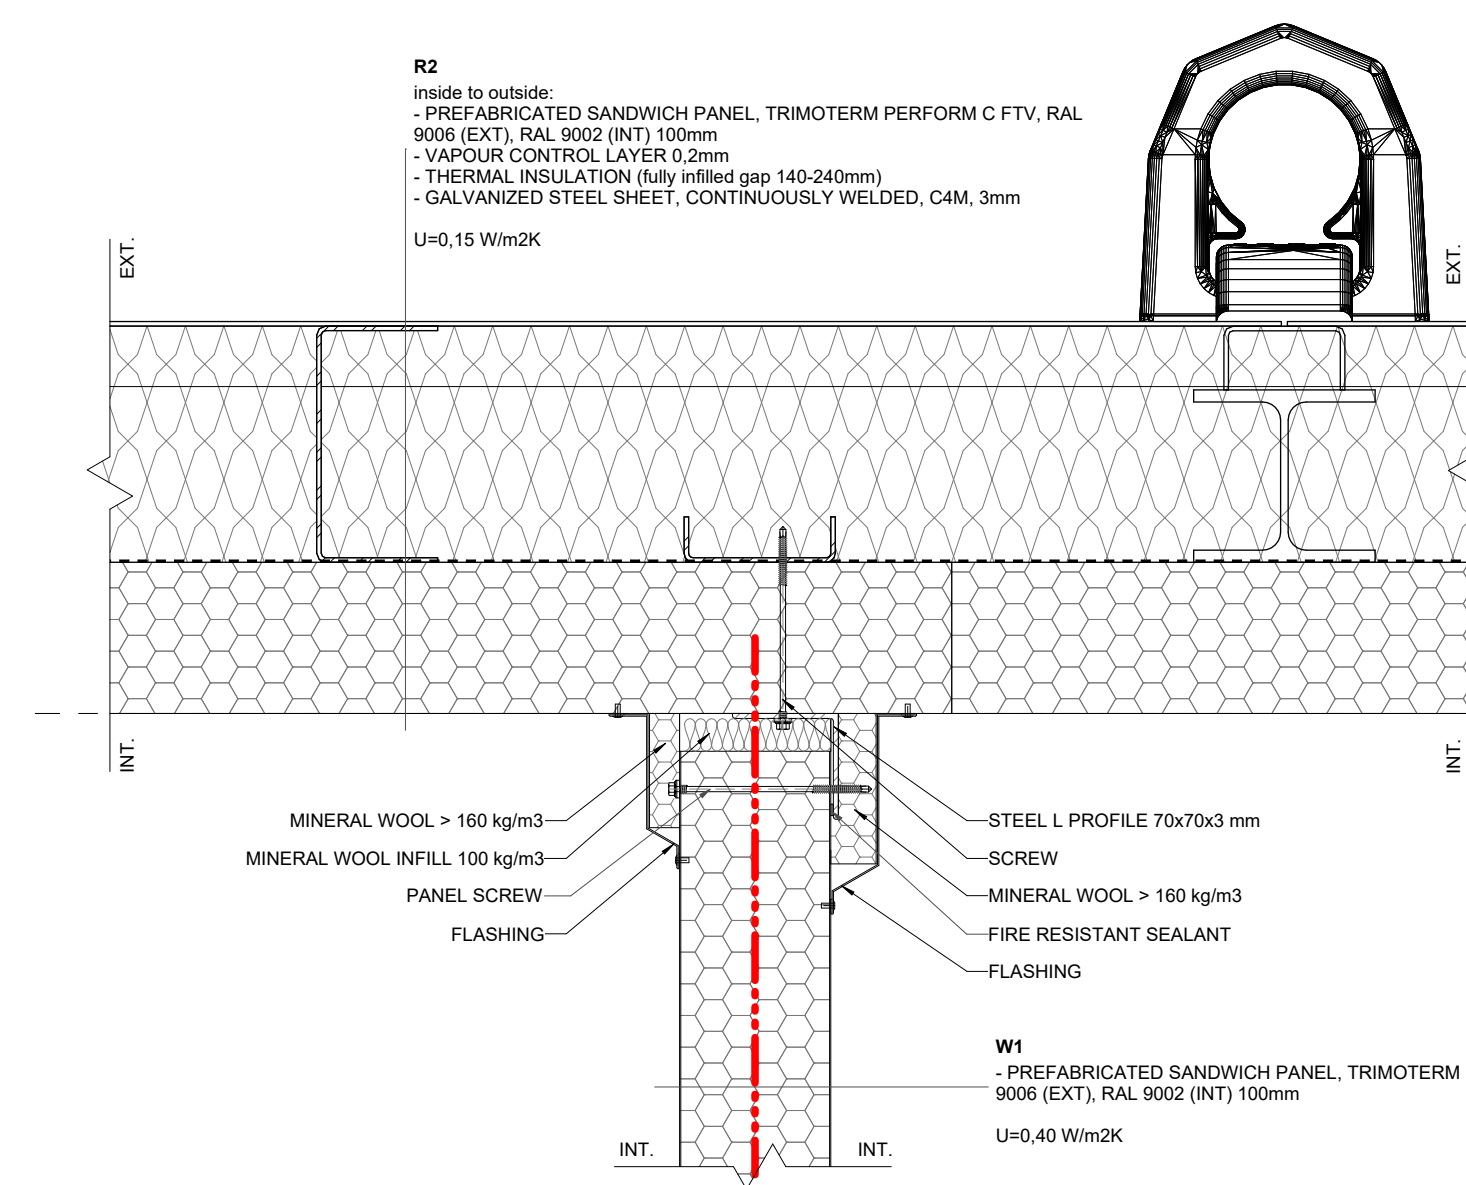


V05 MV - INT. WALL/ROOF CONNECTION
1:5

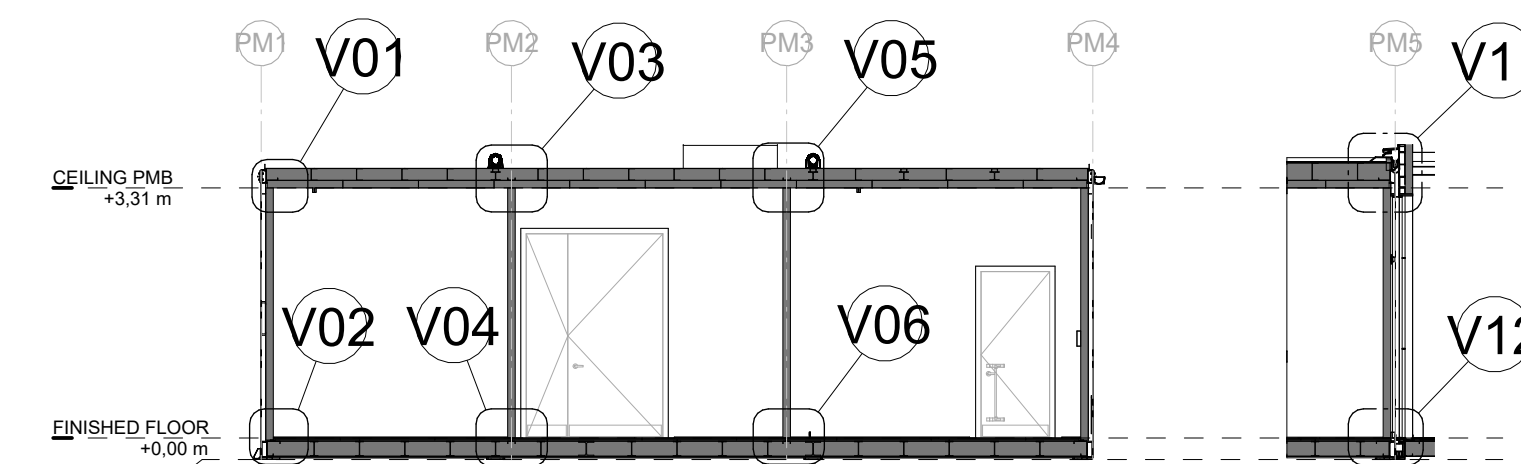


LONGITUDINAL SECTION
KEY PLAN - PM/MV/MS MODULE DETAIL POSITIONS - VERTICAL VIEWS

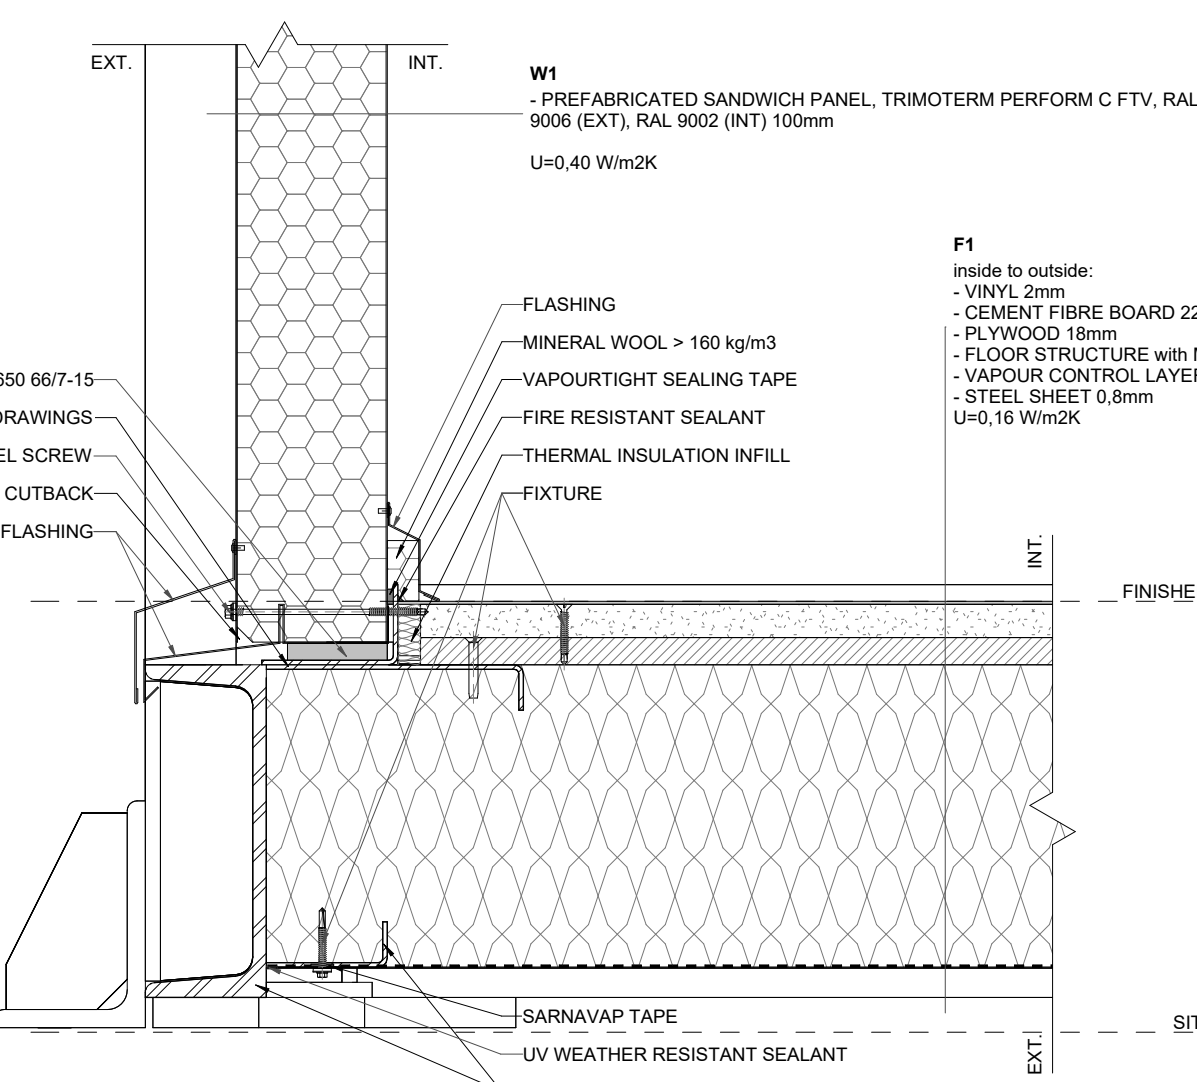


V02 PM/MV/MS - EXT. WALL/FLOOR CONNECTION
1:5

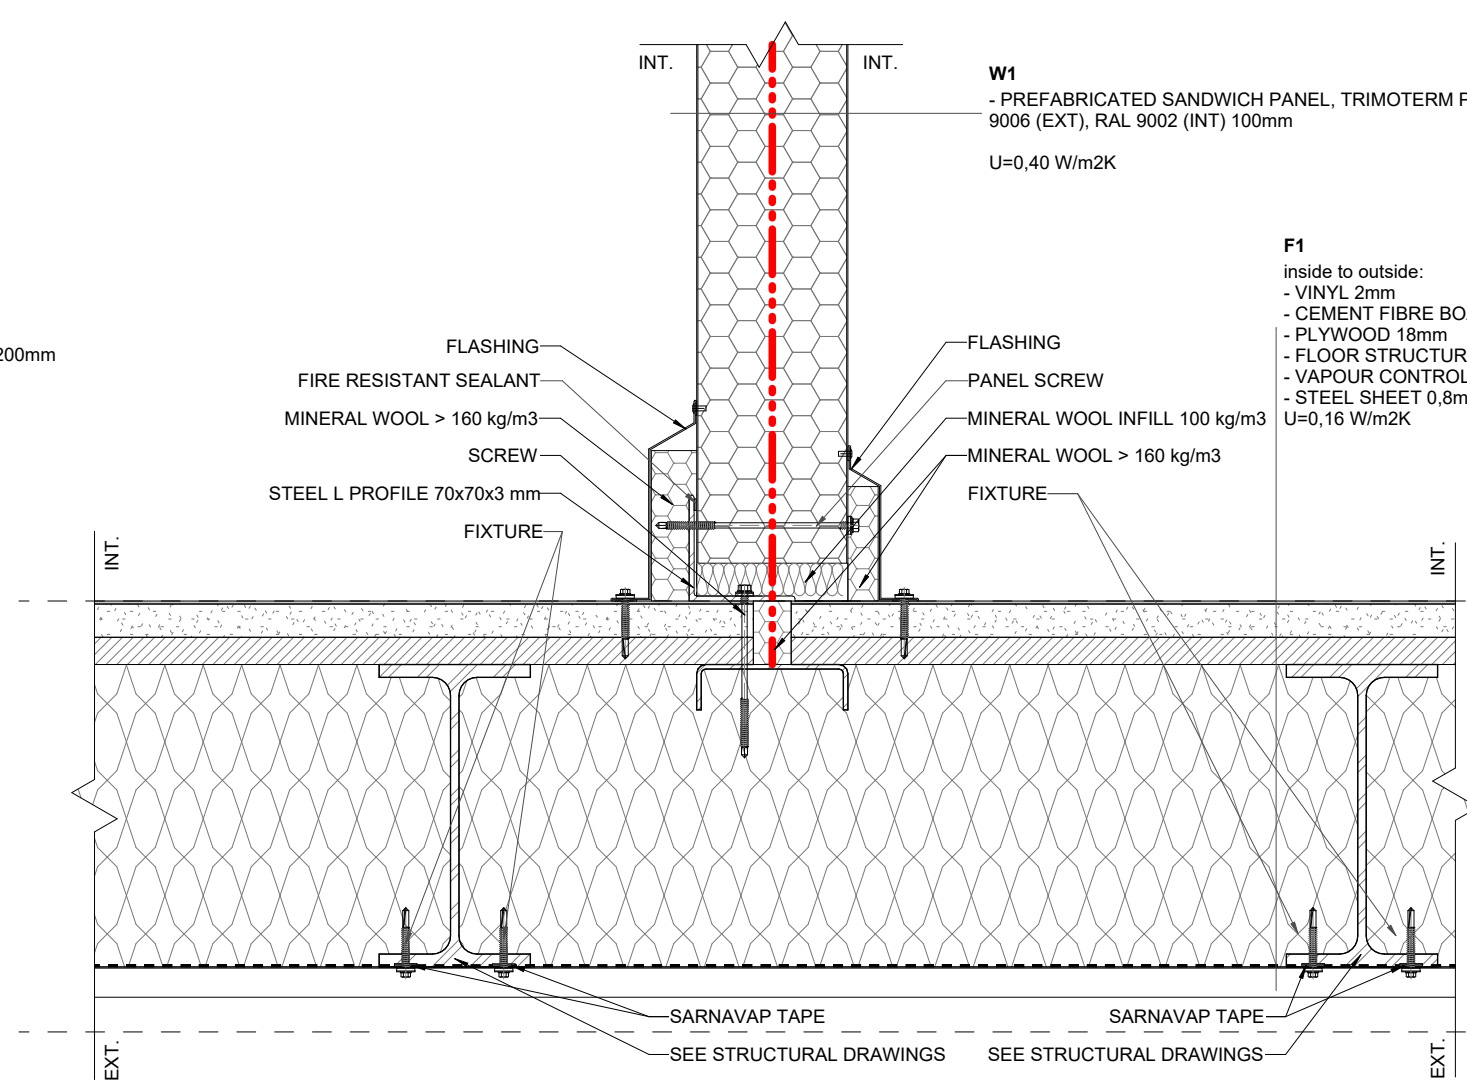


V04 MV - INT. WALL/FLOOR CONNECTION
1:5

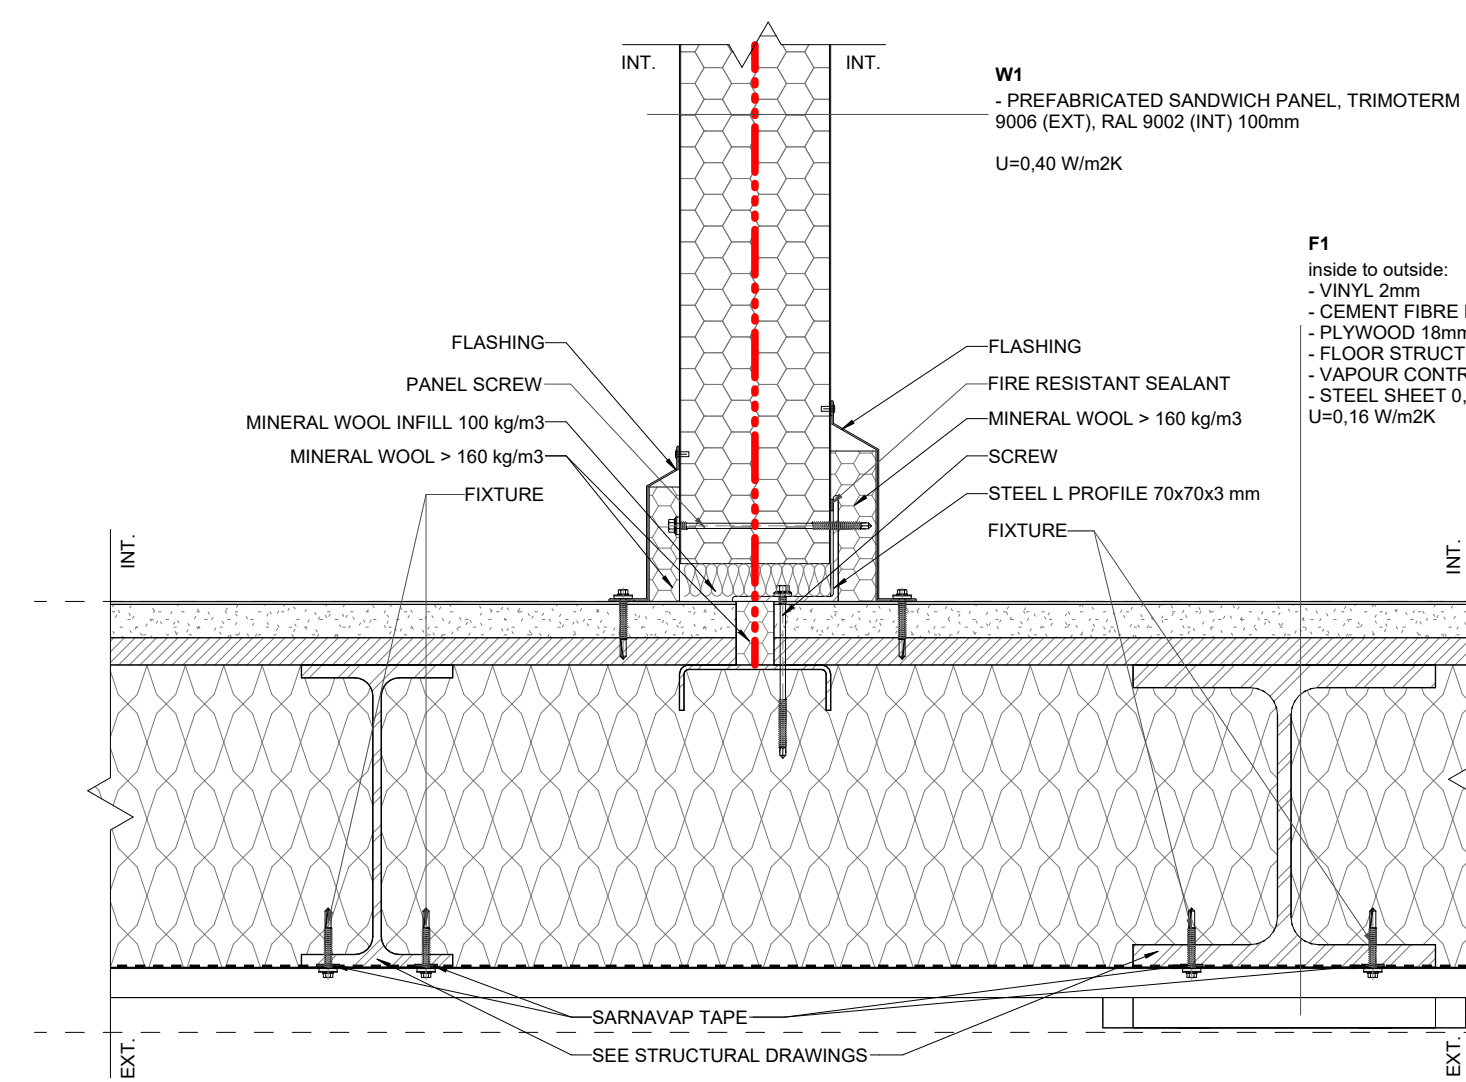


V06 MV - INT. WALL/FLOOR CONNECTION
1:5

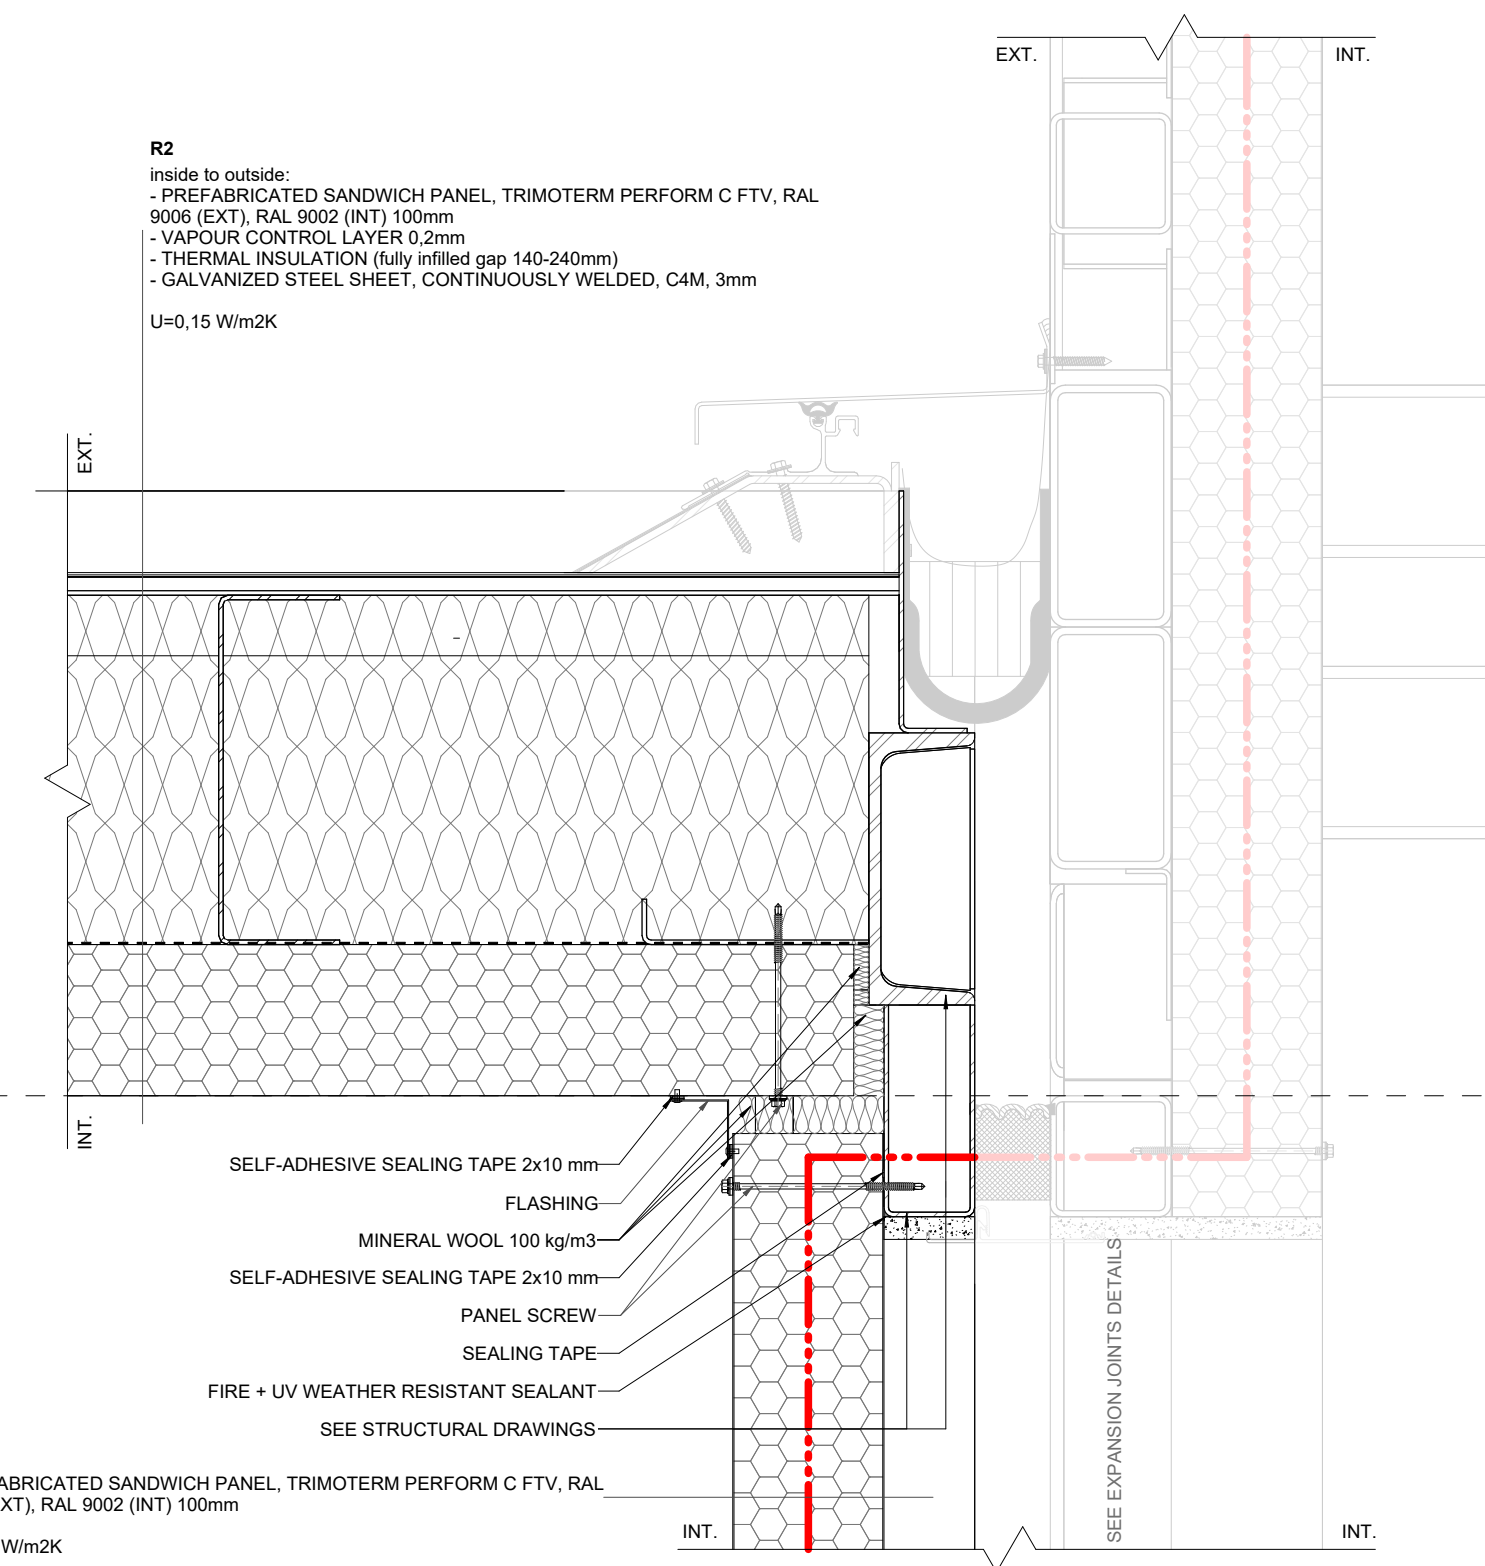


V11 PM - RPP MODULE CONNECTION-ROOF
1:5

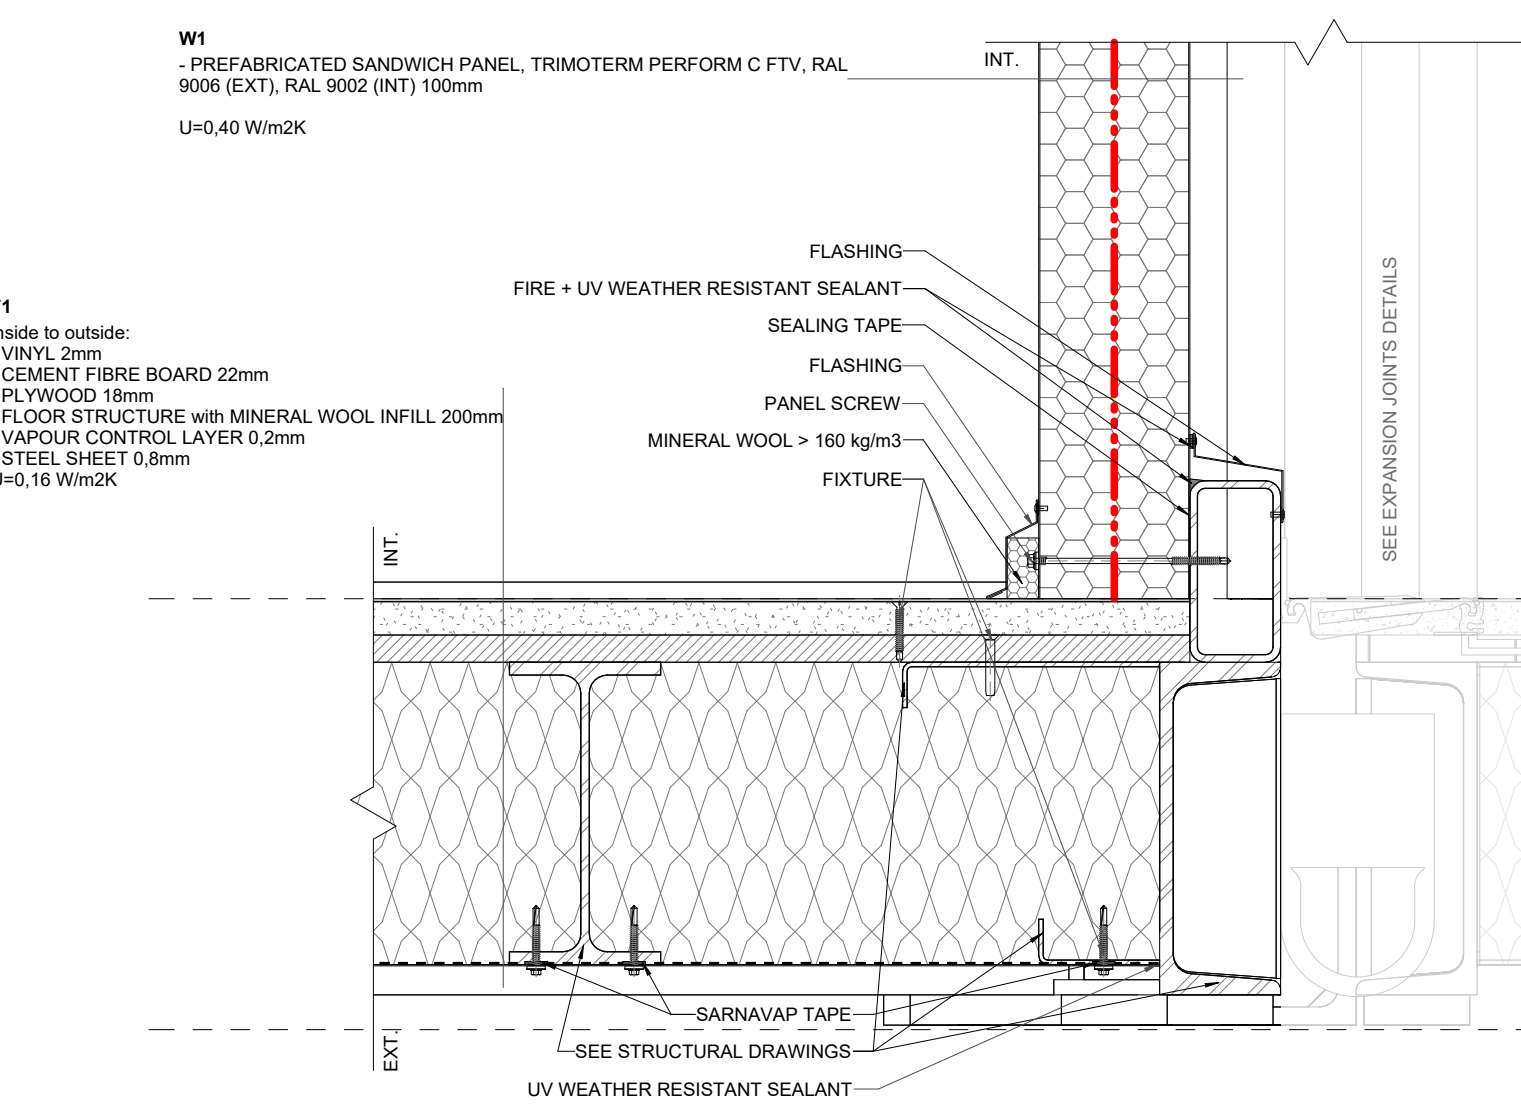


V12 PM - RPP MODULE CONNECTION-FLOOR
1:5

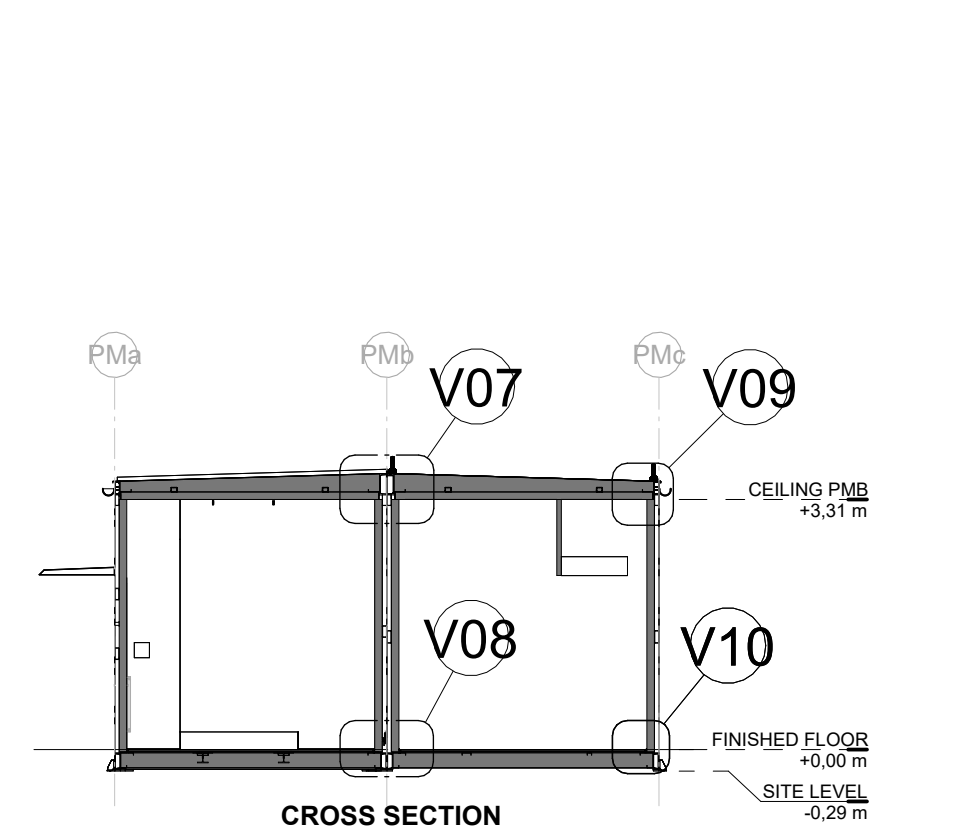


CROSS SECTION
KEY PLAN - PM/MV/MS MODULE DETAIL POSITIONS

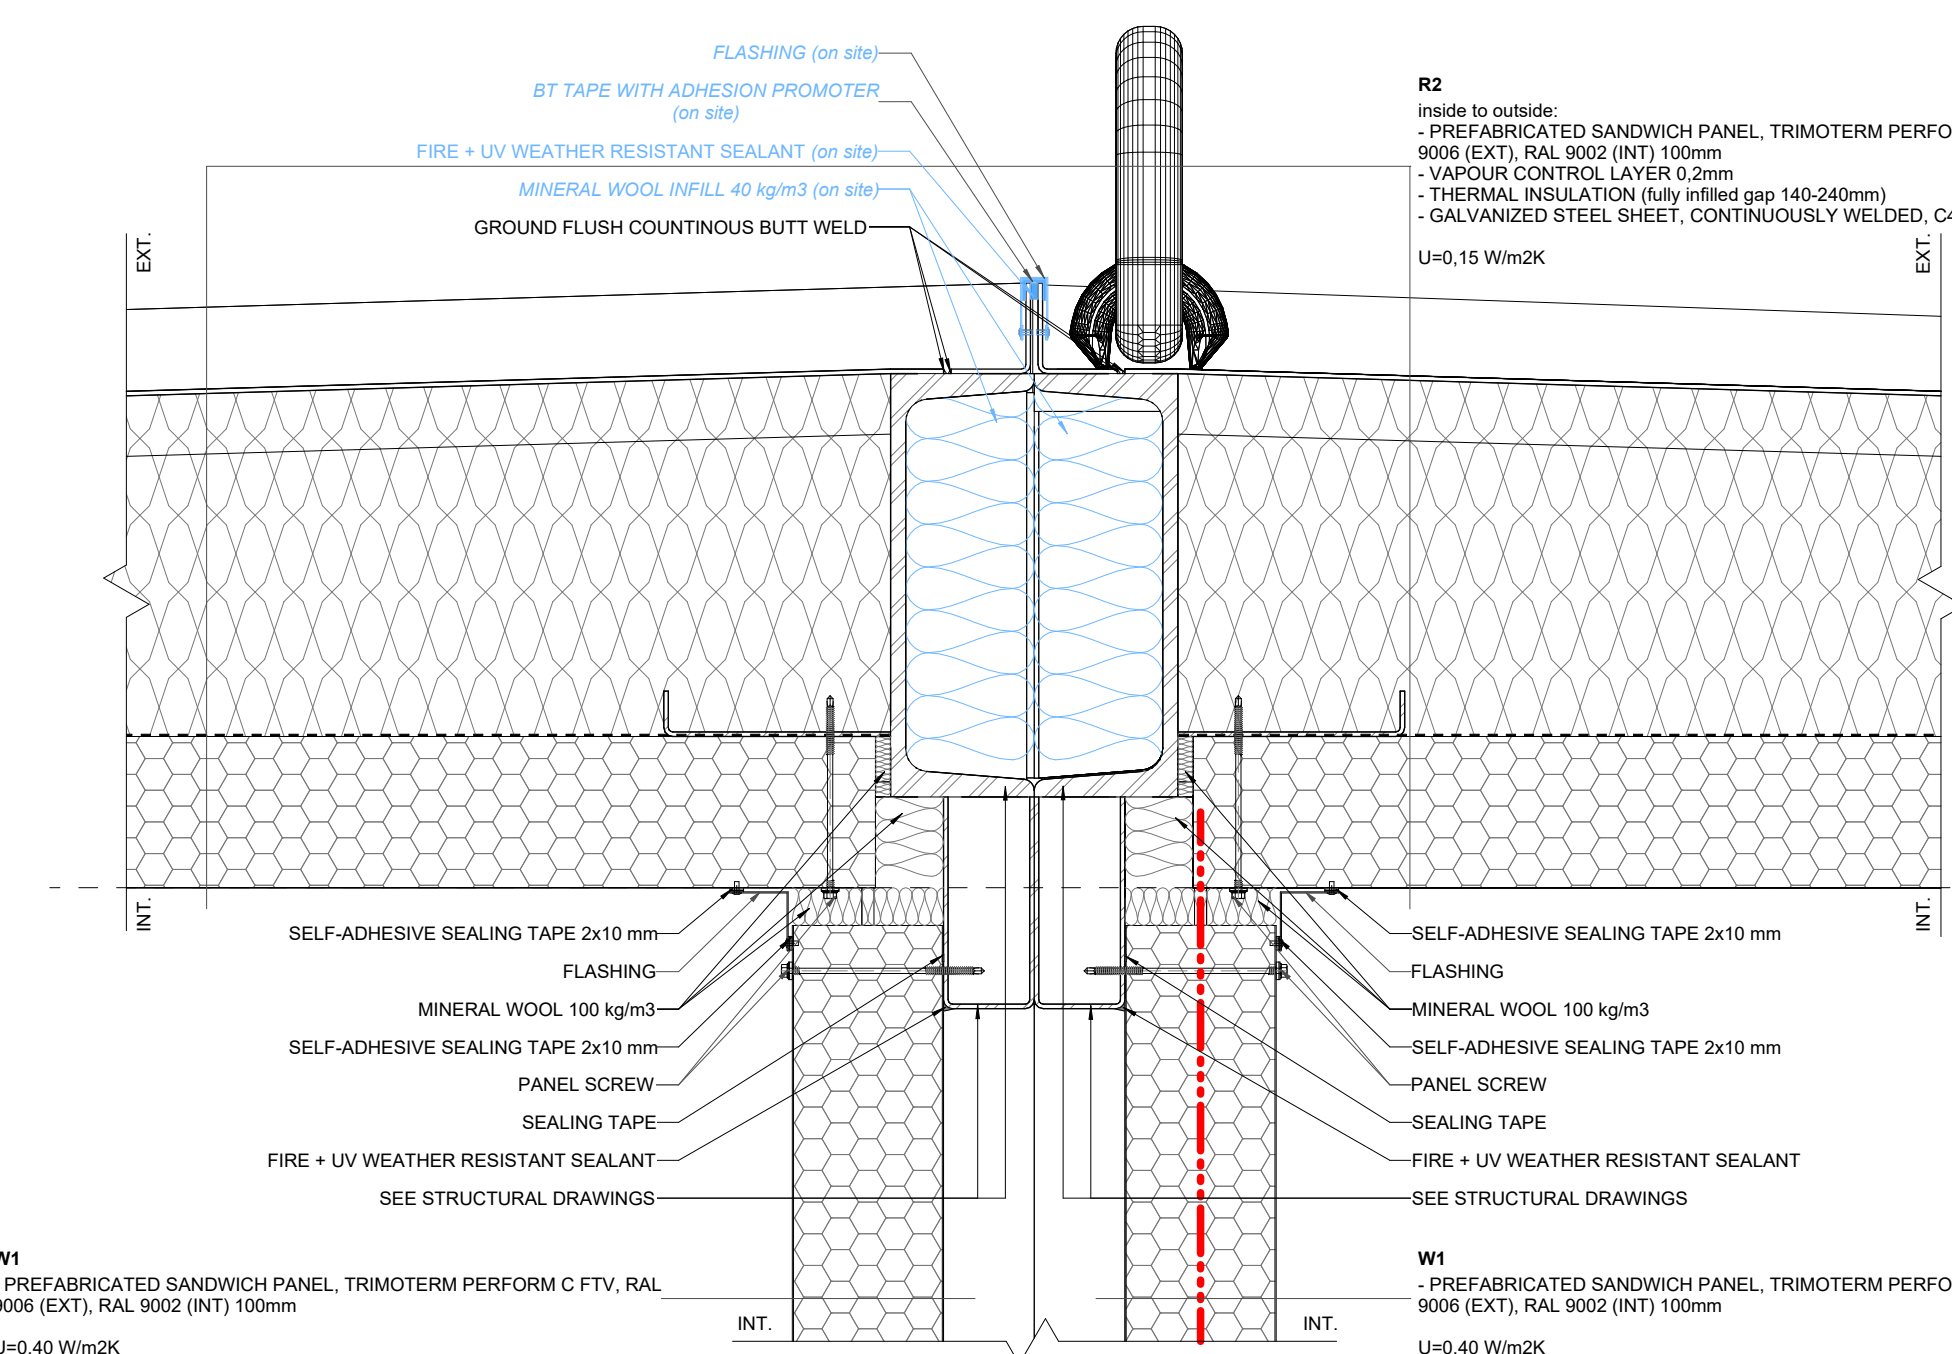


V07 PM/MV - MODULE CONNECTION-ROOF
1:5

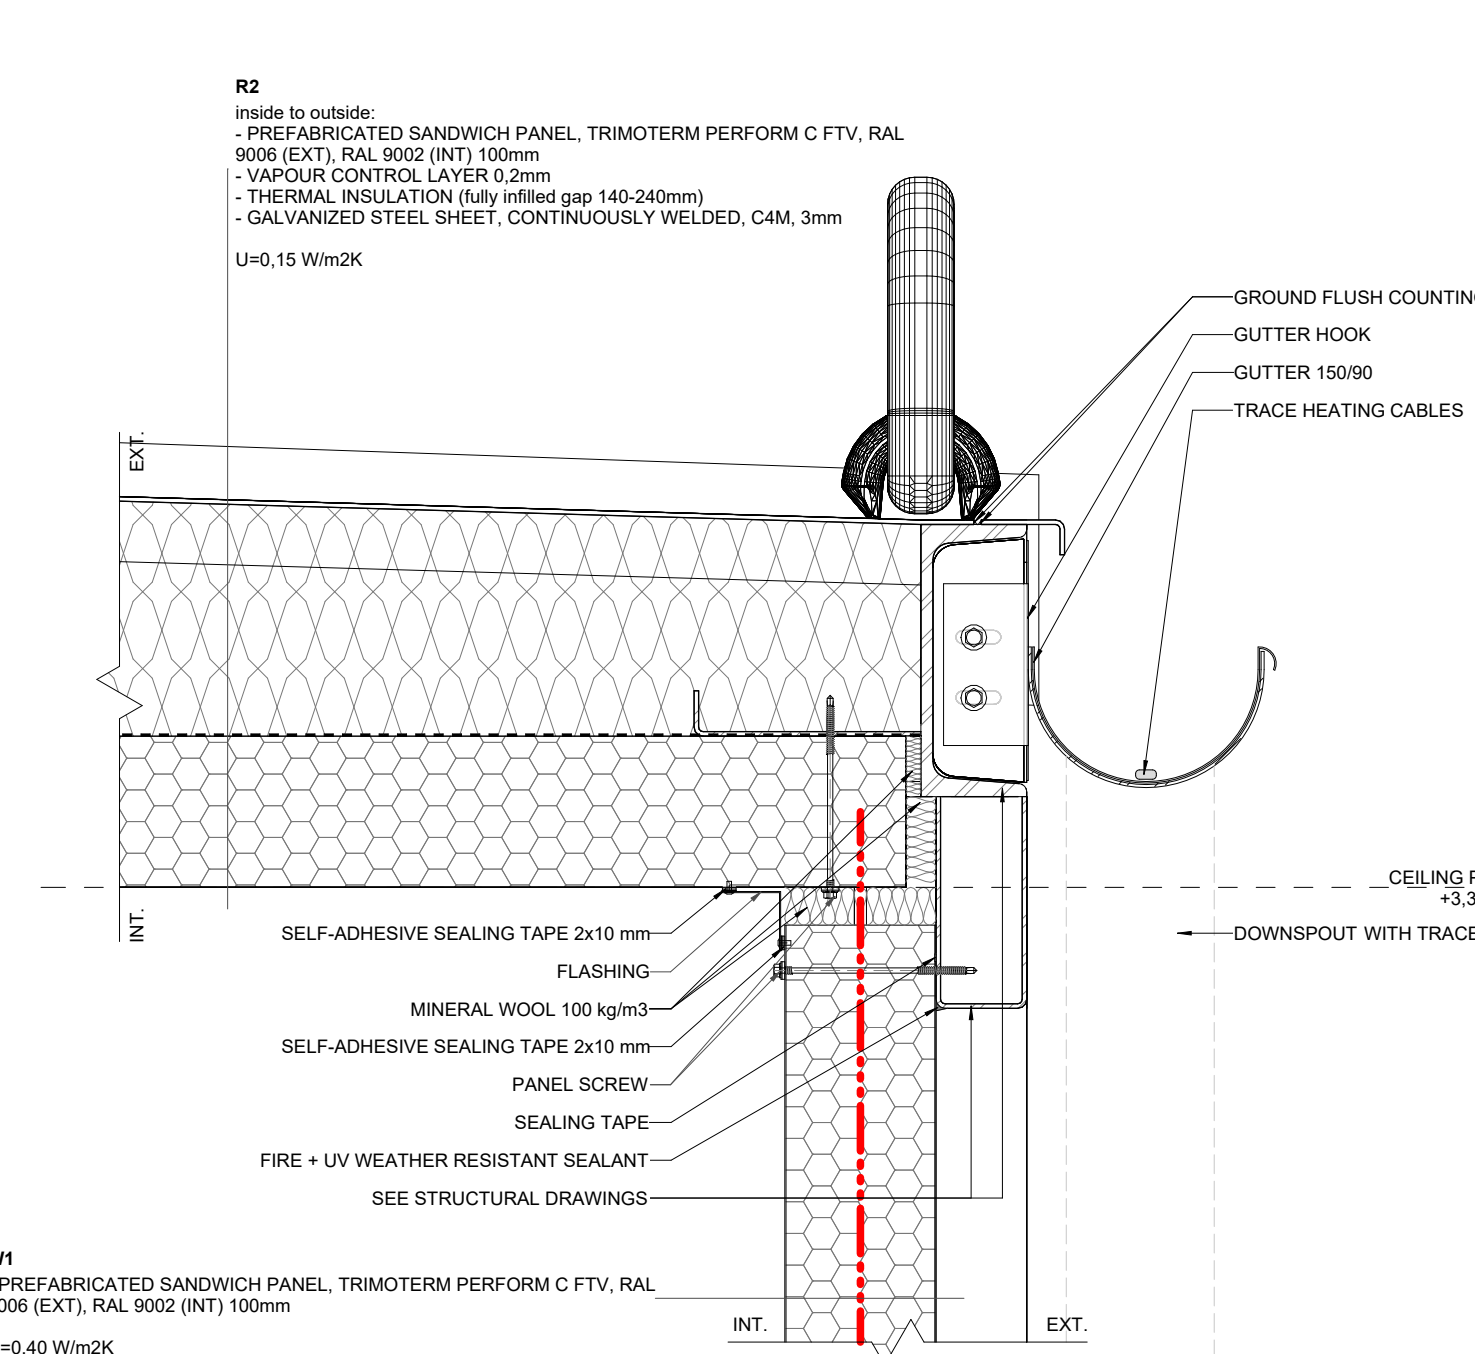

V09 PM/MV/MS - EXT. WALL/ROOF CONNECTION
1:5

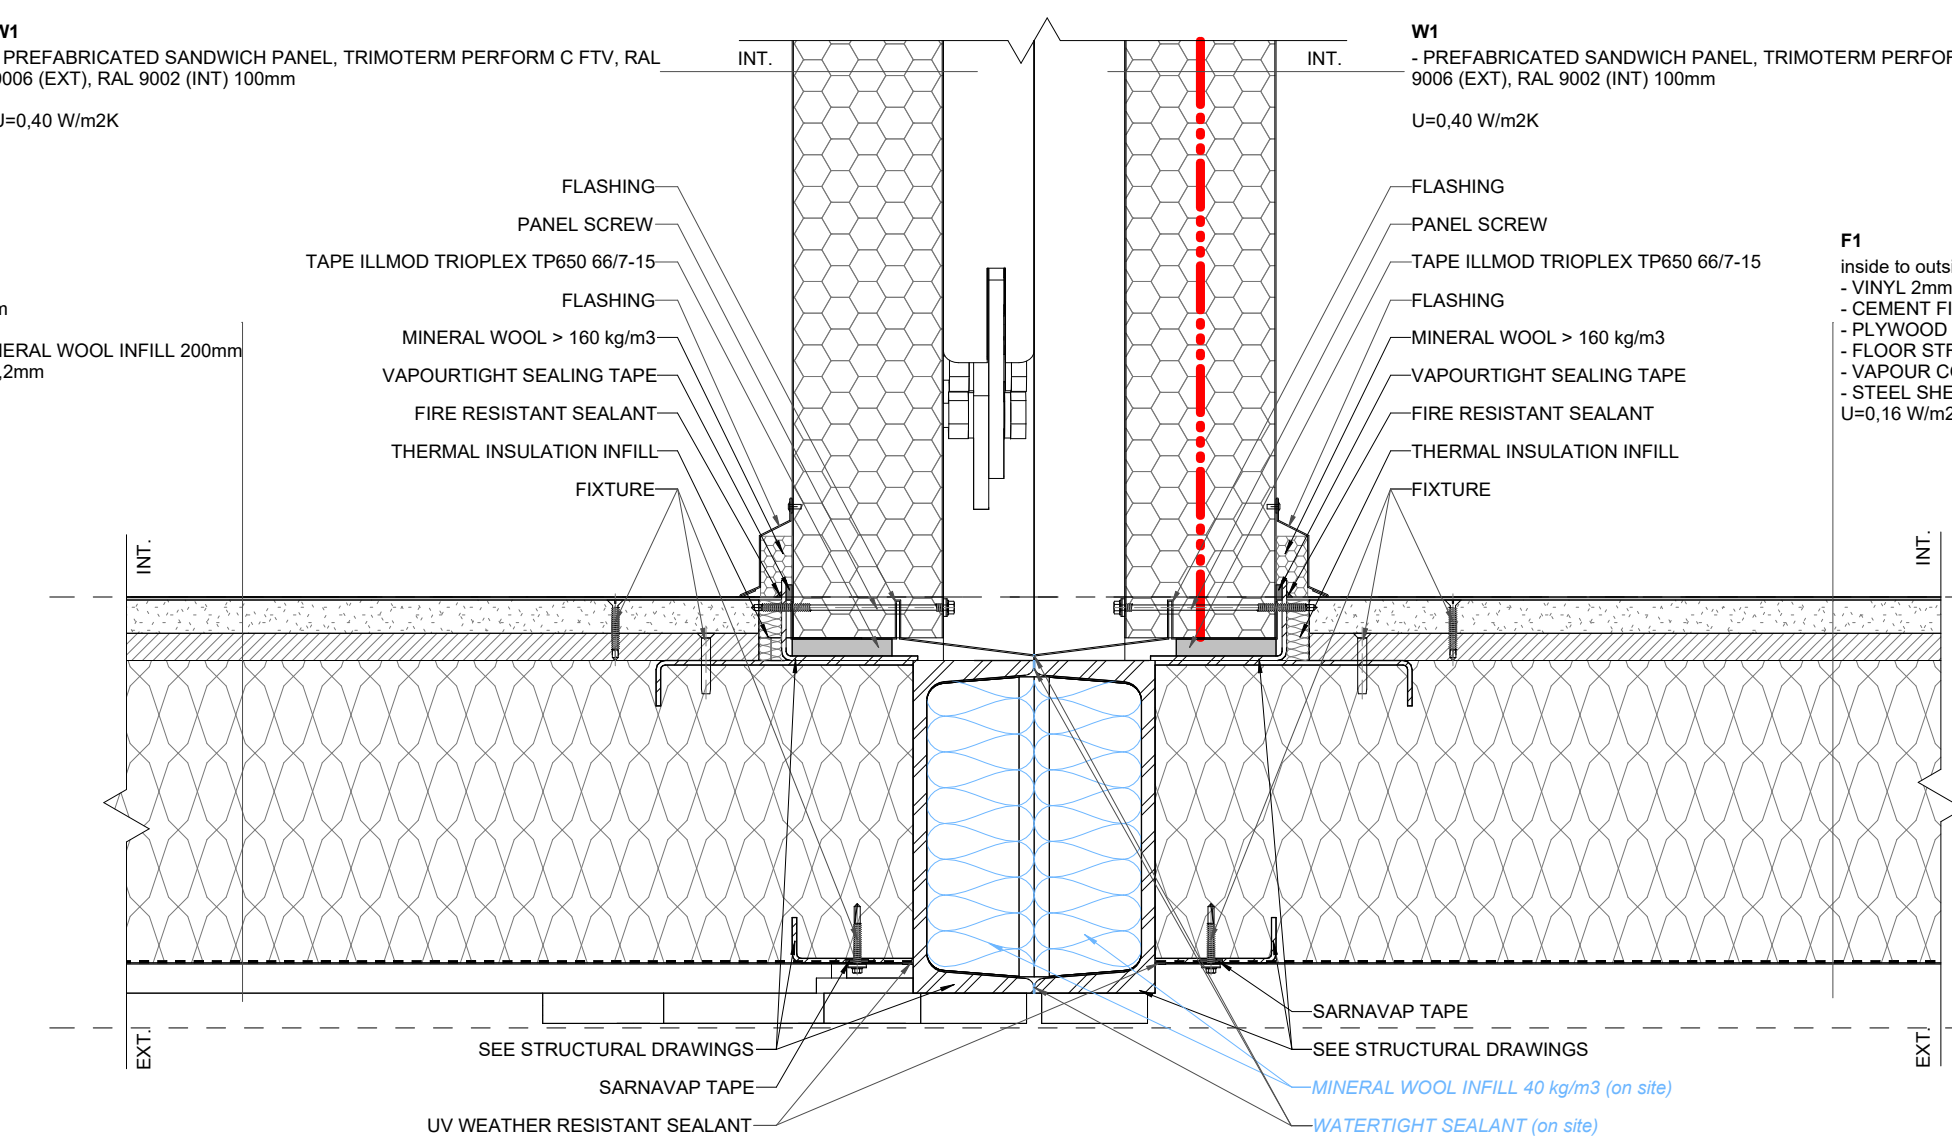


V08 PM/MV - MODULE CONNECTION-FLOOR
1:5

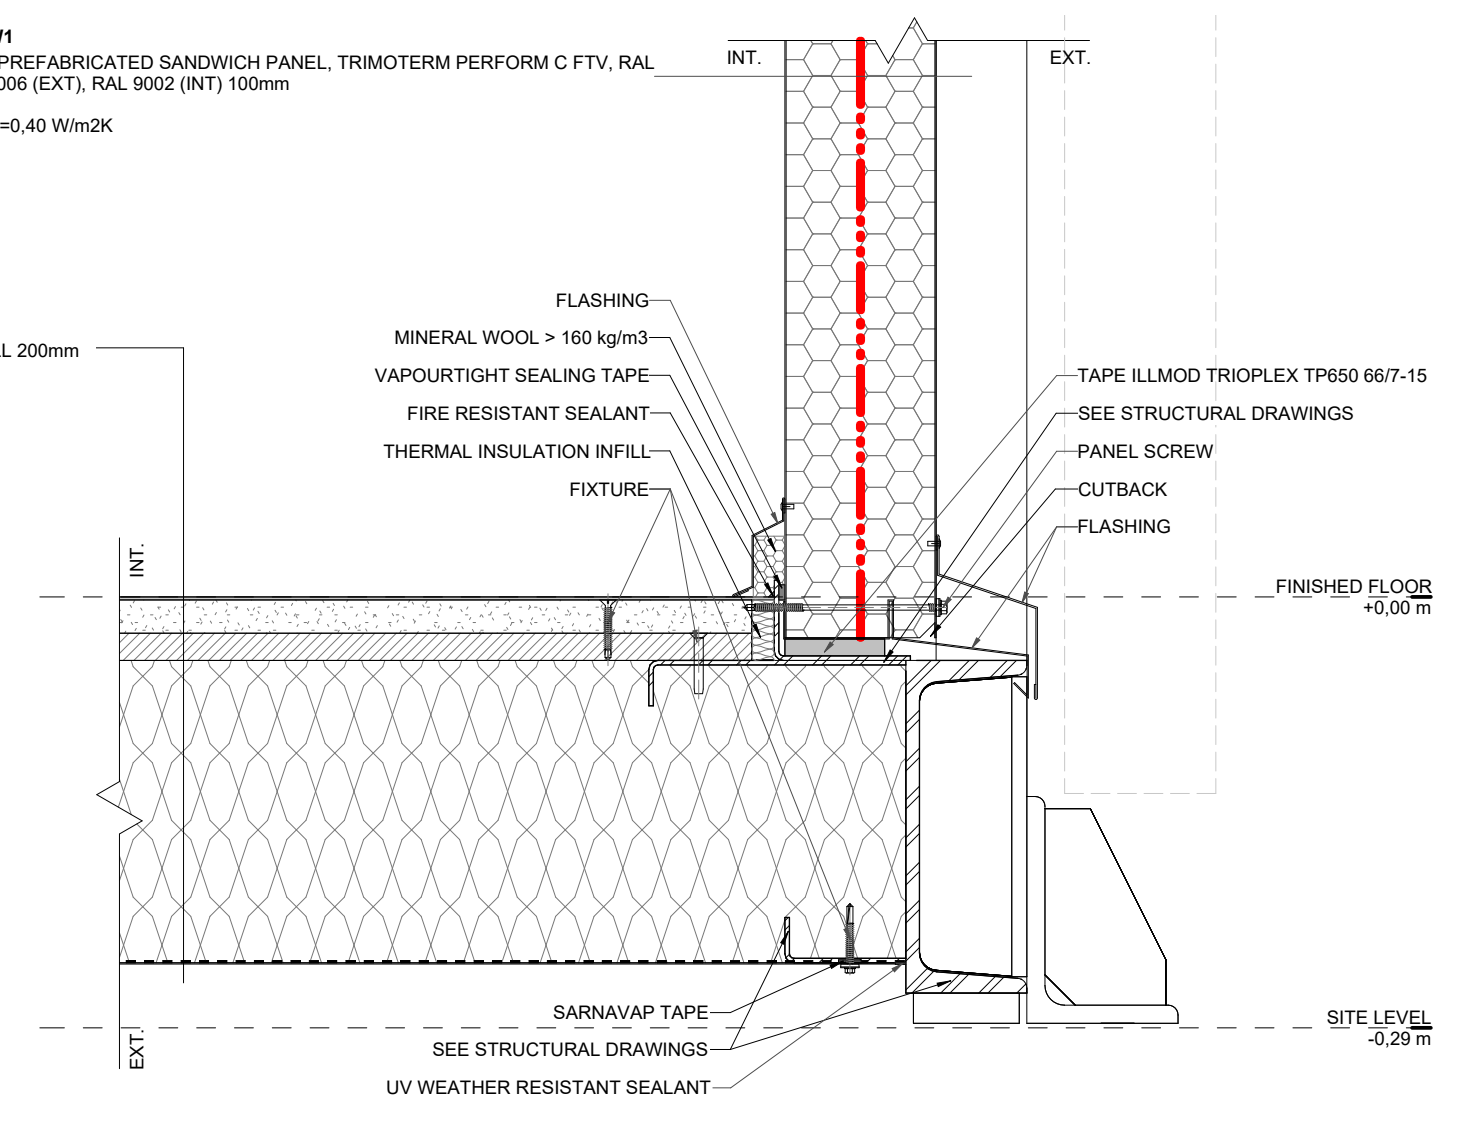

V10 PM/MV/MS - EXT. WALL/FLOOR CONNECTION
1:5

KEYNOTES:
LEGEND:
- FIRE COMPARTMENT BORDER 60
- FIRE COMPARTMENT BORDER 30
- ELEMENTS INSTALLED ON SITE

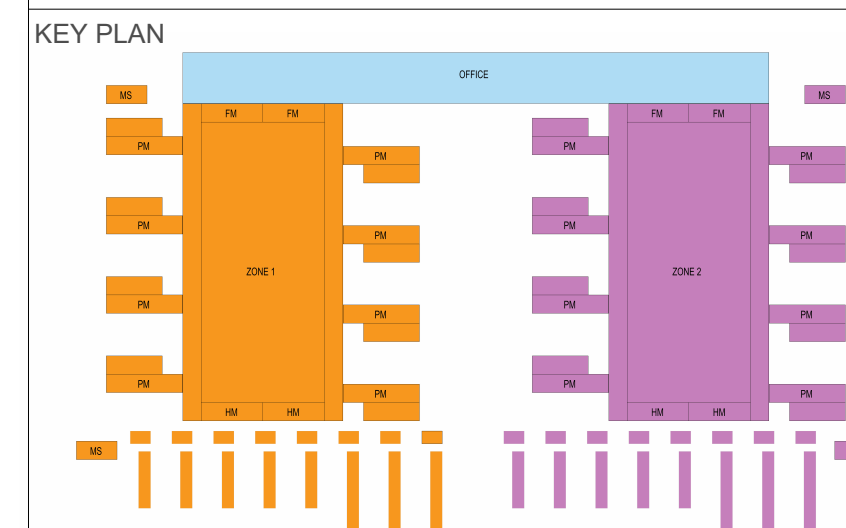

REV.	DESCRIPTION	DATE
R02	CD SET - FOR INFORMATION 2026-09-11	
R01	CD SET - FOR INFORMATION 2026-07-24	



PROJECT NAME
ECO DC MONALISA

DRAWING NAME
**ARCHITECTURAL DETAILS
- PREFABRICATED MODULES
- VERTICAL VIEWS - PM - MV - MS**

PREPARED (ALSO SUBJECT RESPONSIBLE IF OTHER)
L. MAVREK / K. KOZINA

DOCUMENT RESPONSIBLE (APPROVED)
M. PACAK

CAD / BIM SYSTEM
AUTODESK REVIT 2025

DOCUMENT NUMBER
ECODC-VRT-MDC19-00-DR-A-50102

SHEET SIZE
A0

DRAWING SCALE
1:5

DATE (YYYY-MM-DD)
2026-09-11

SHEET 1 OF 1

REVISION

R02