
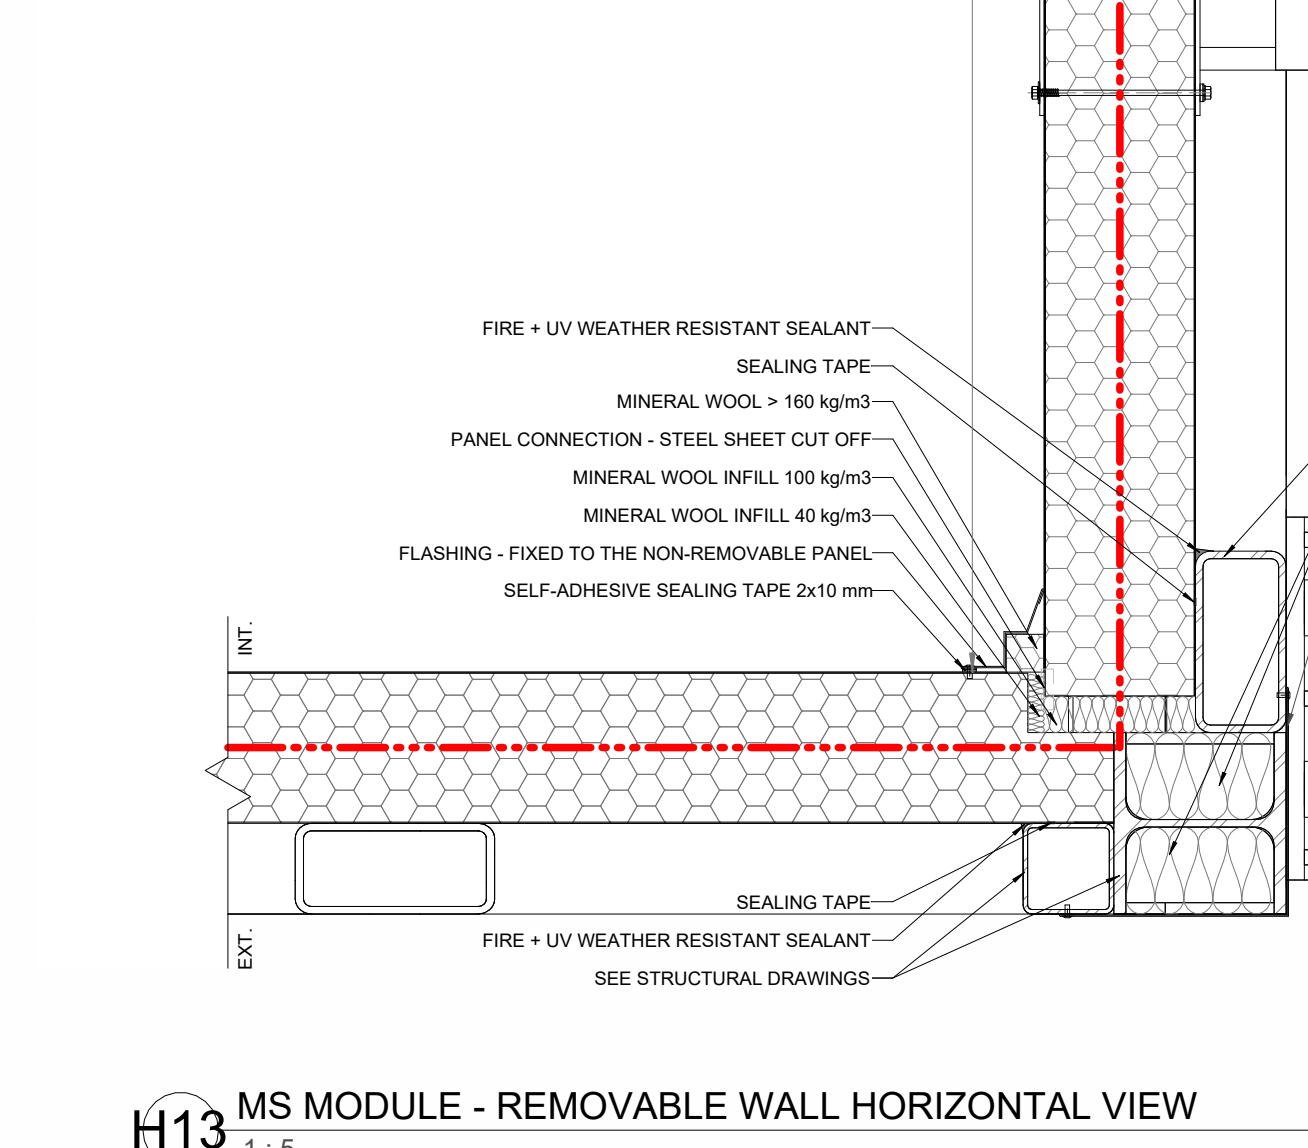
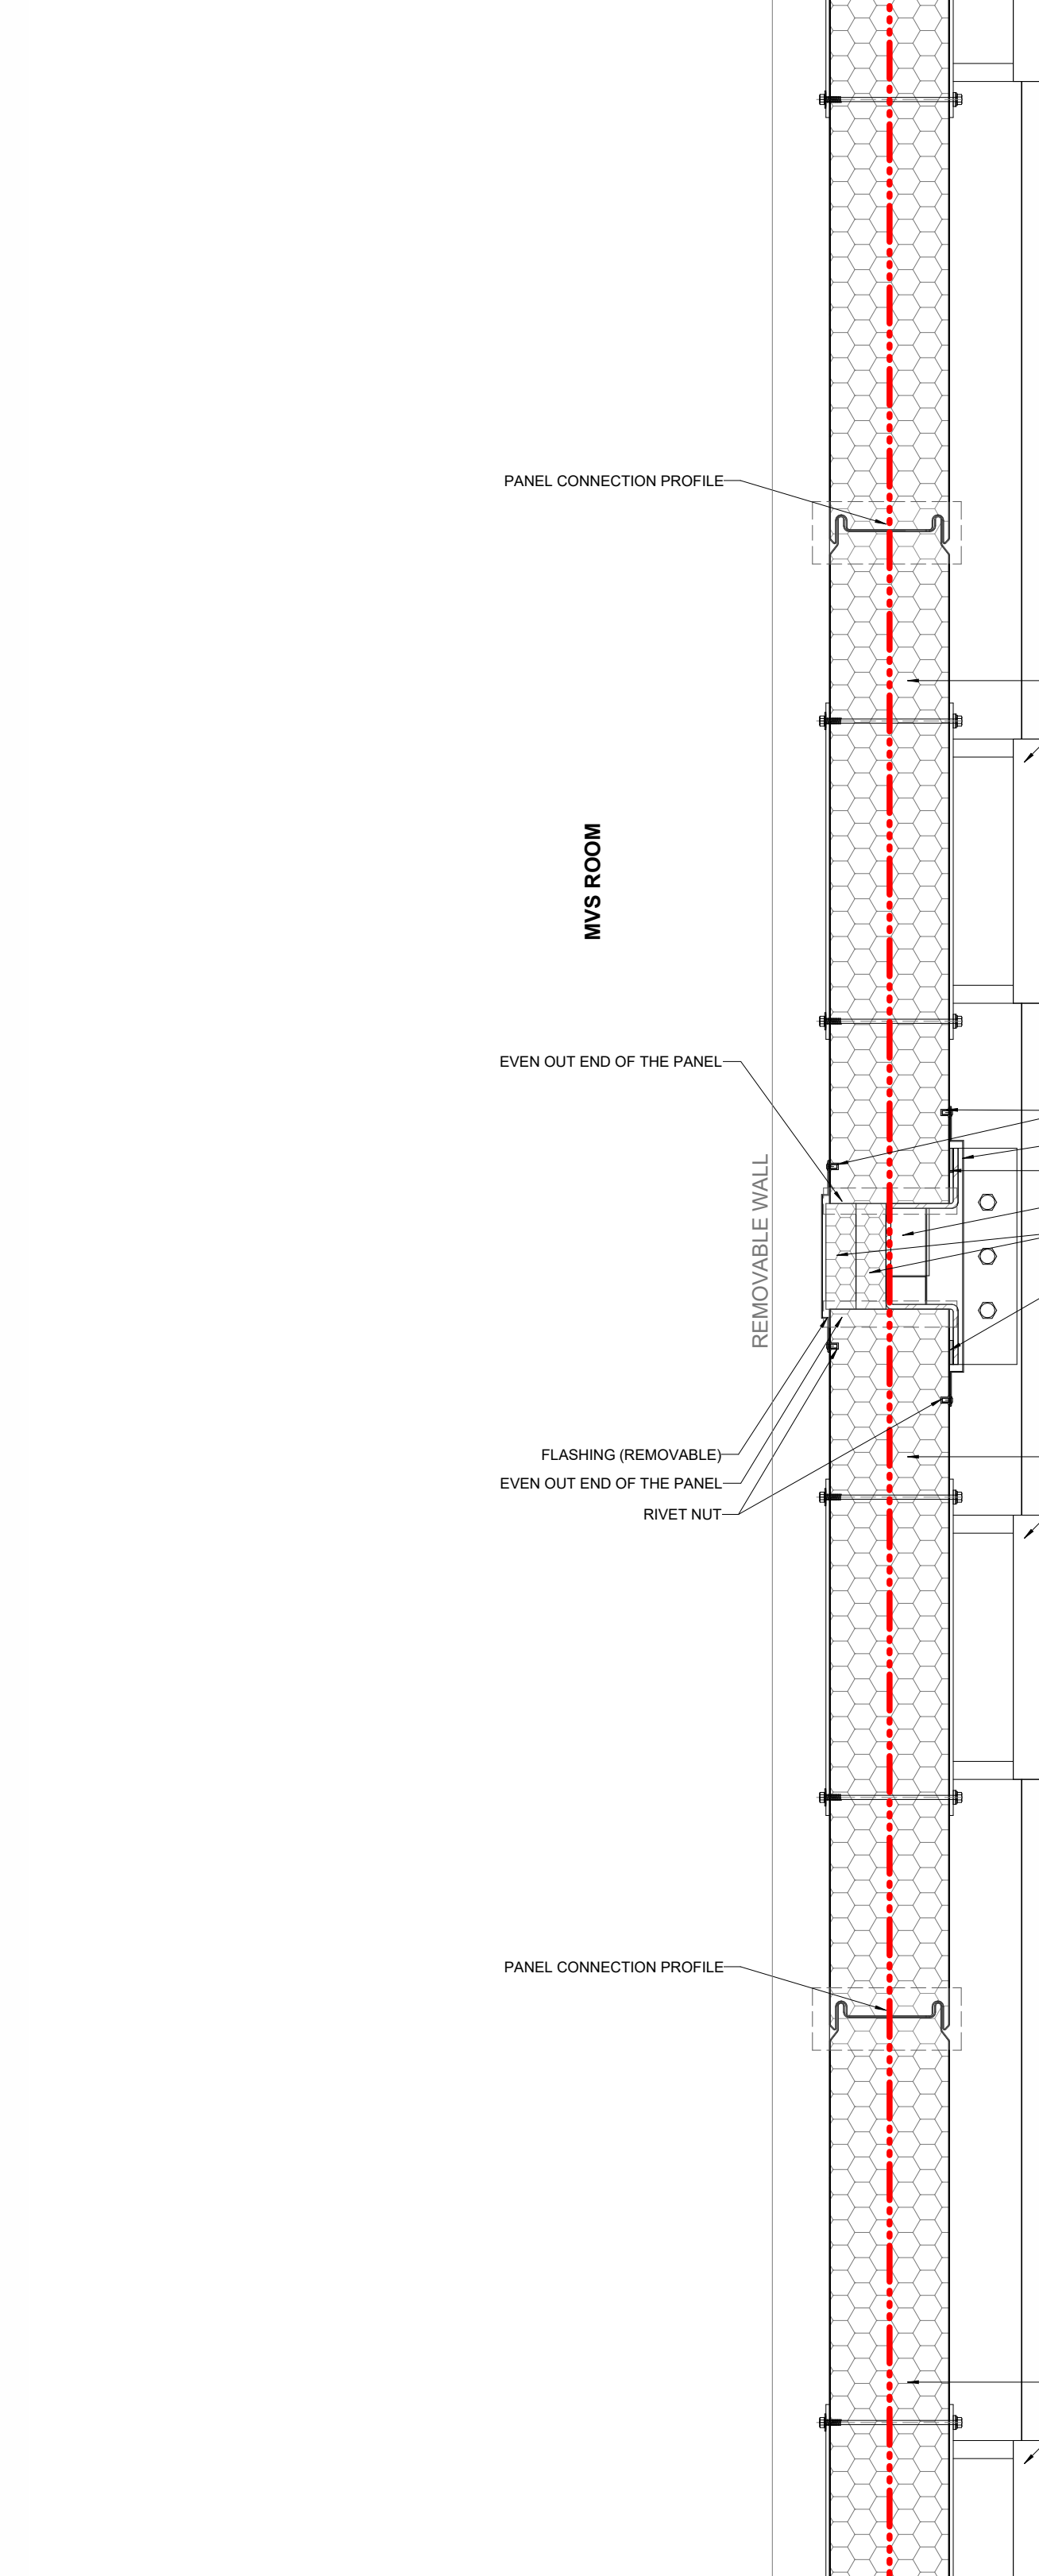
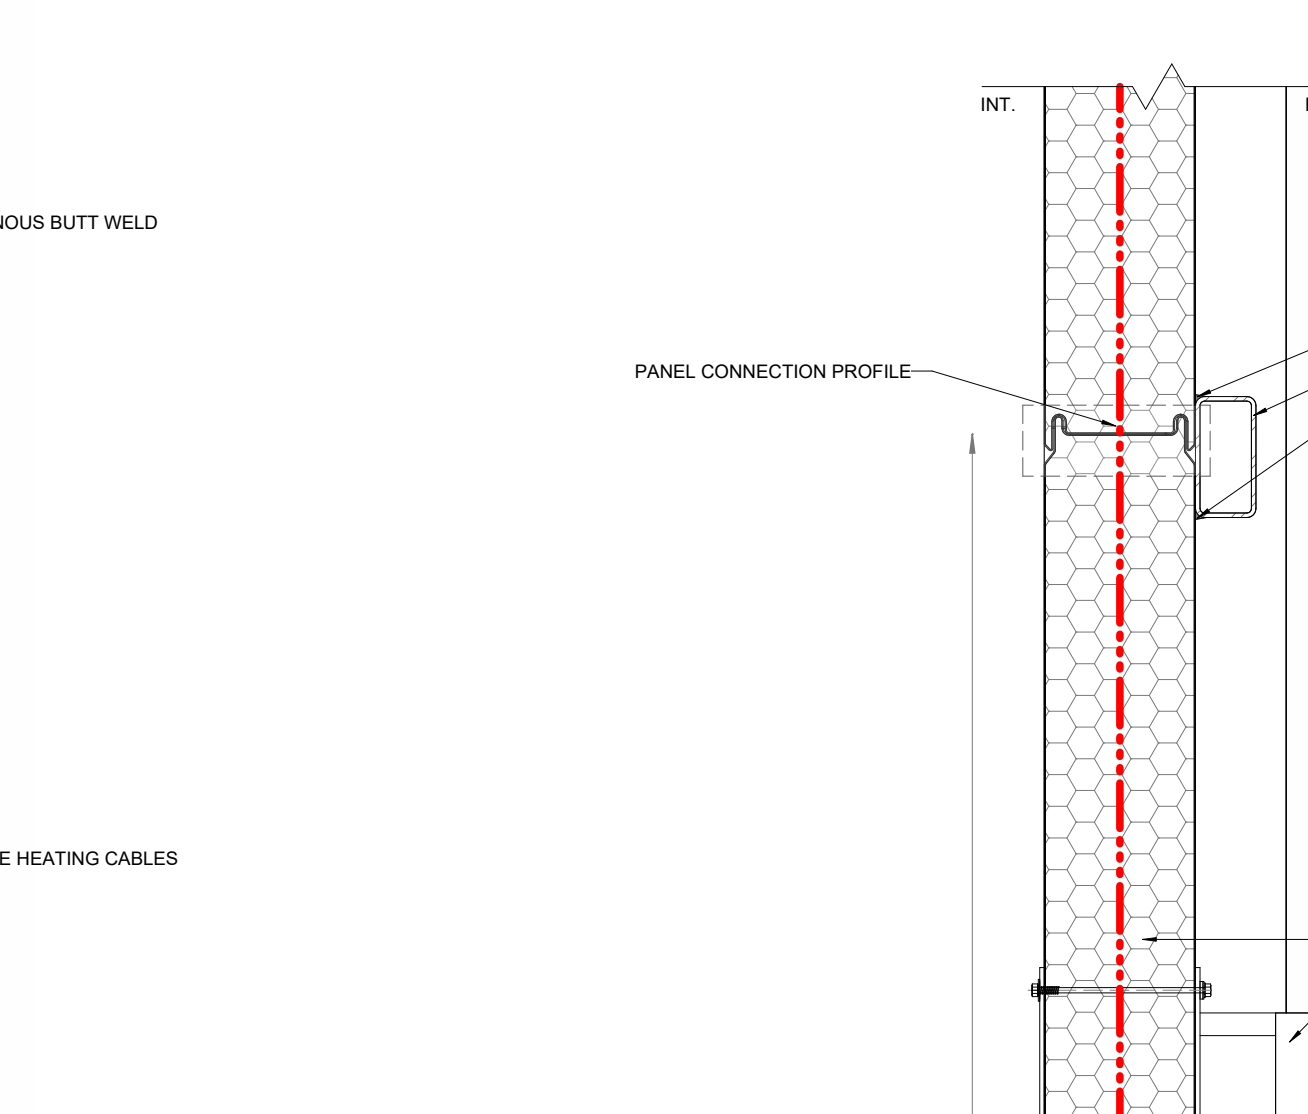
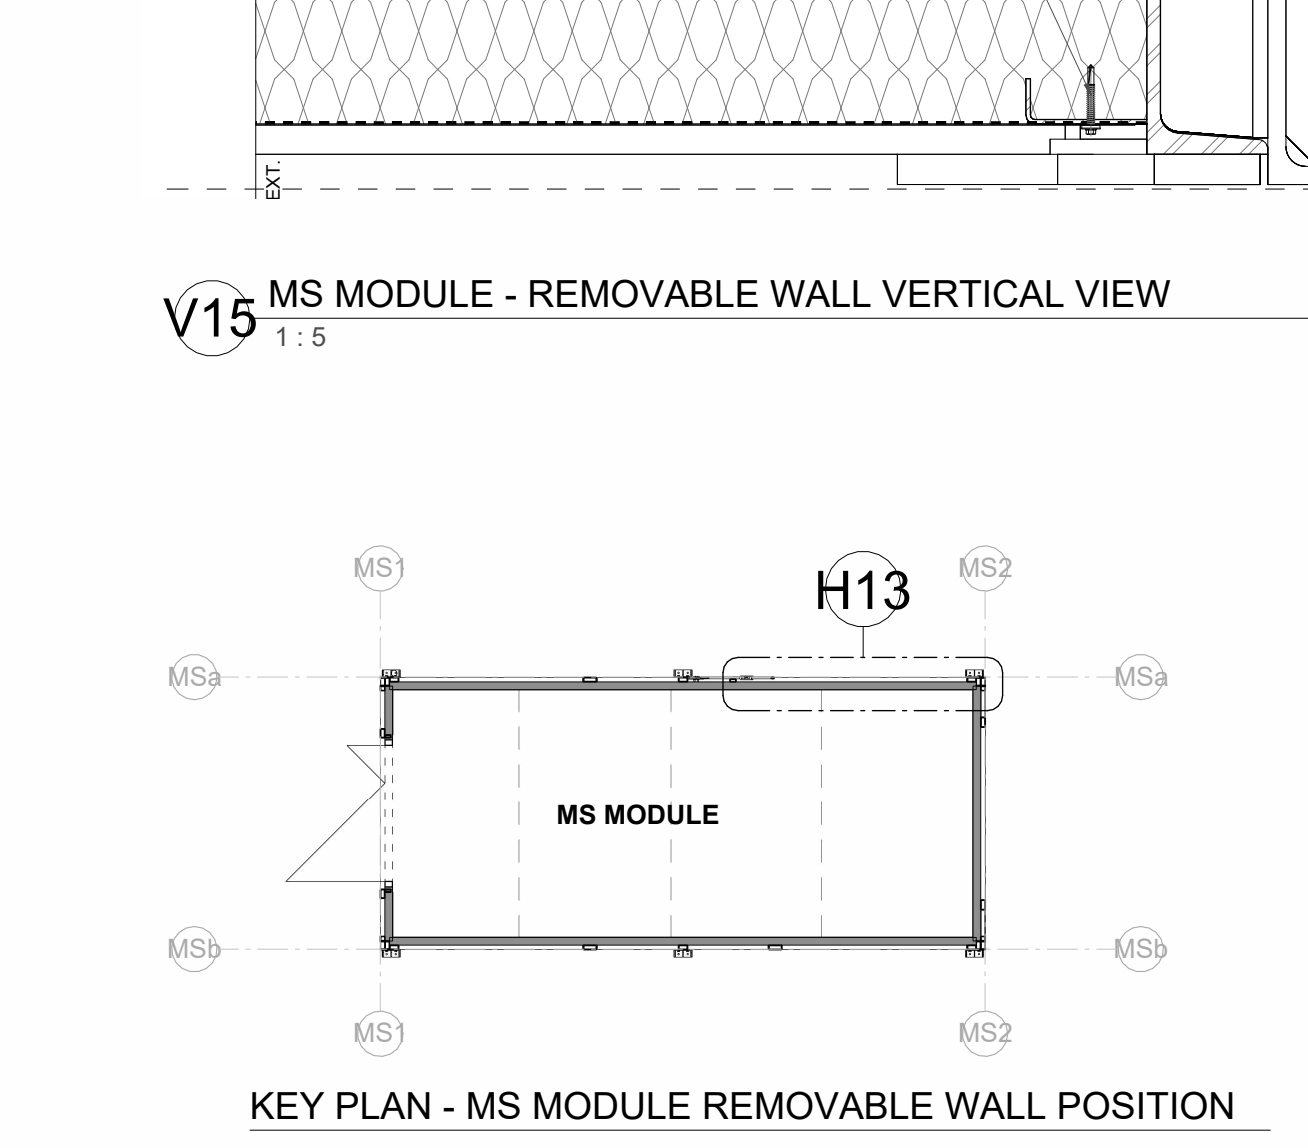
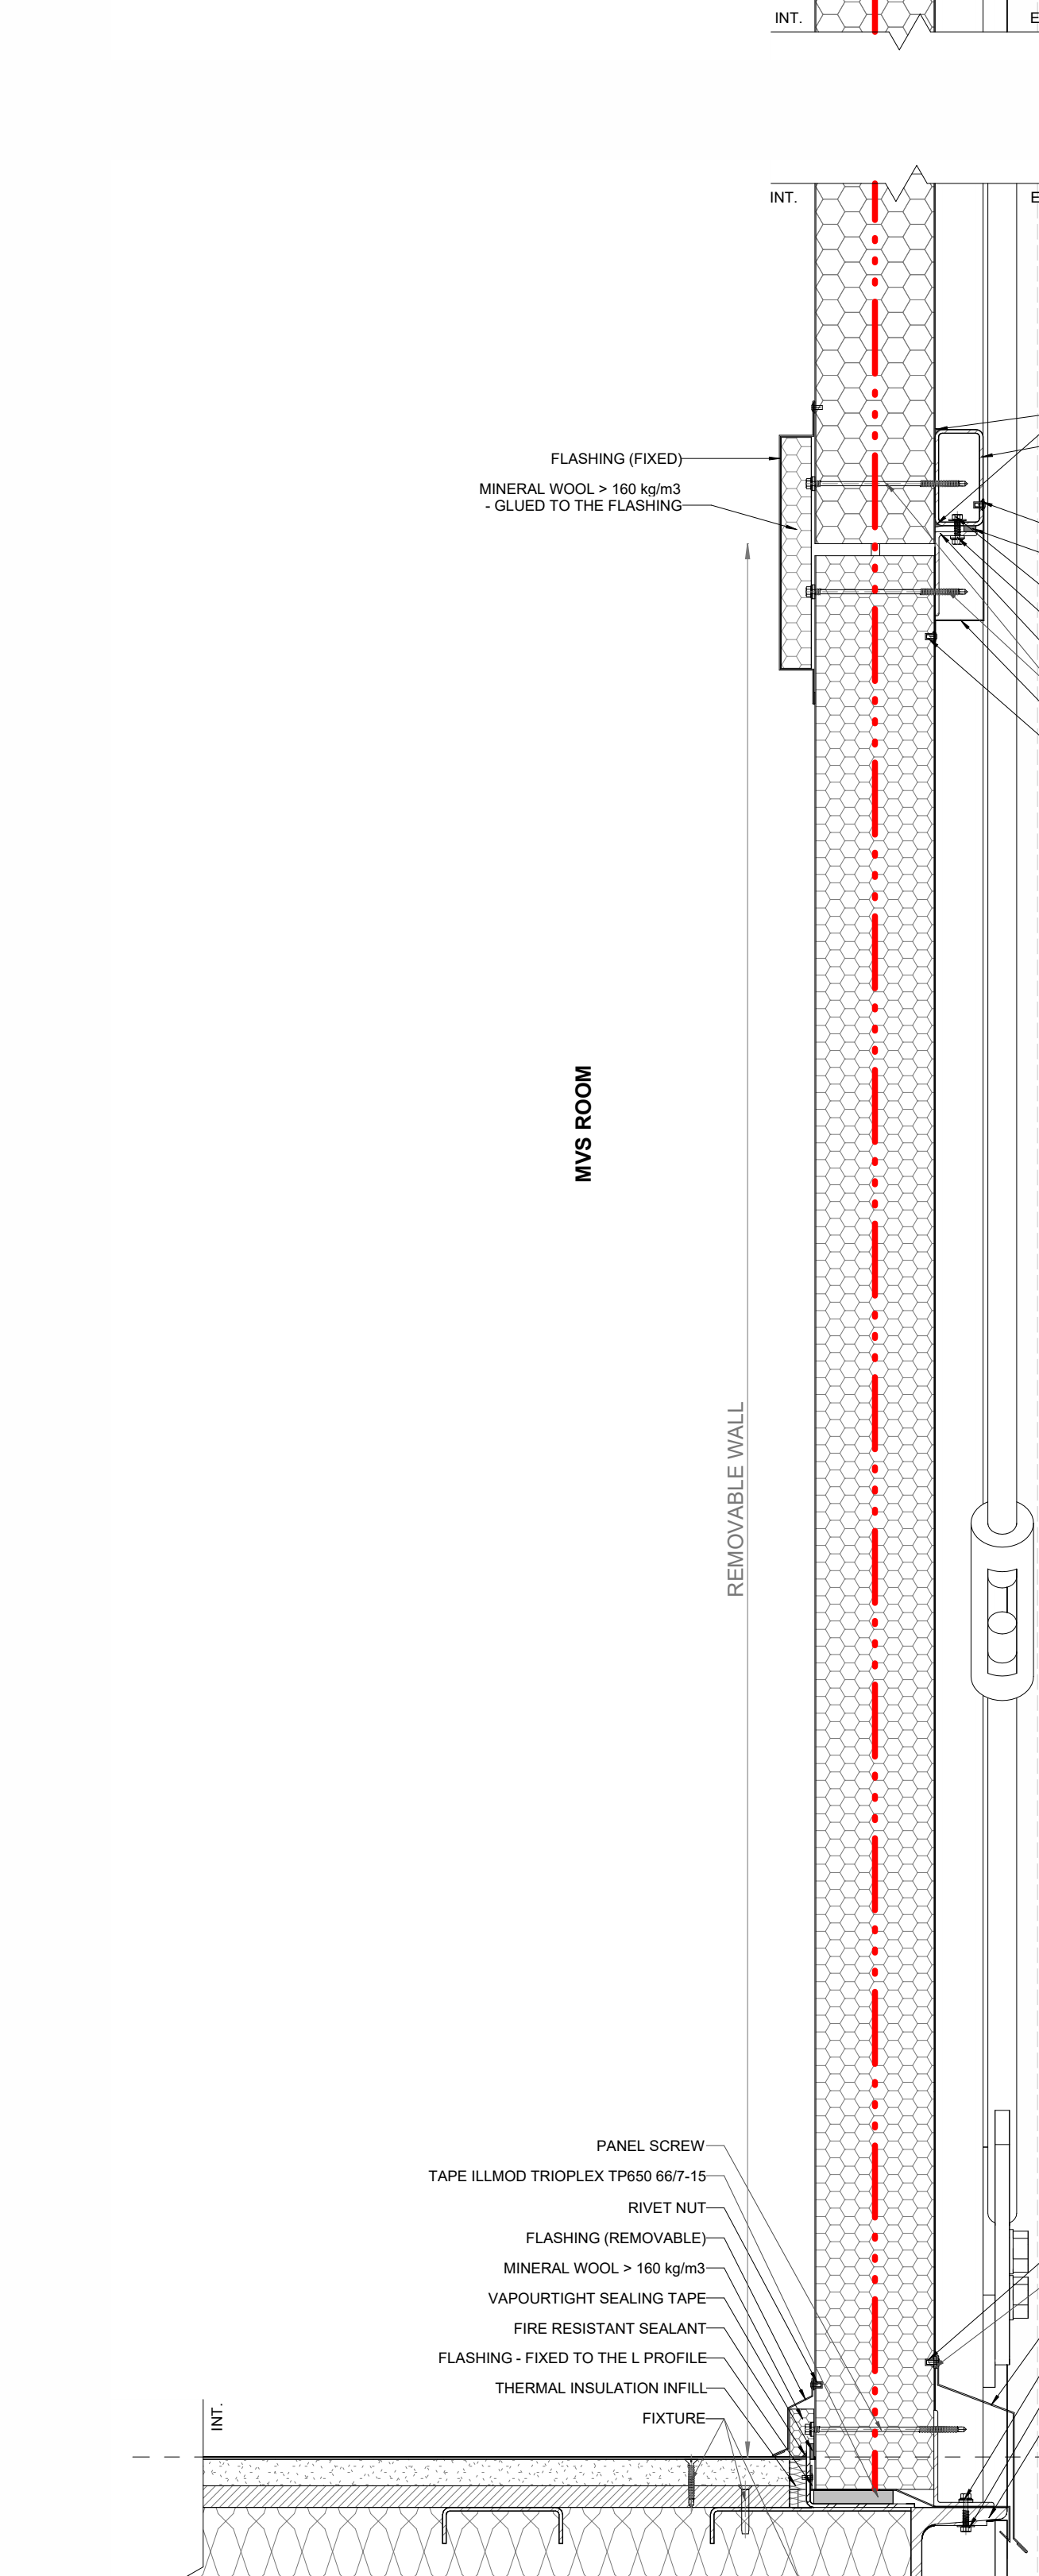
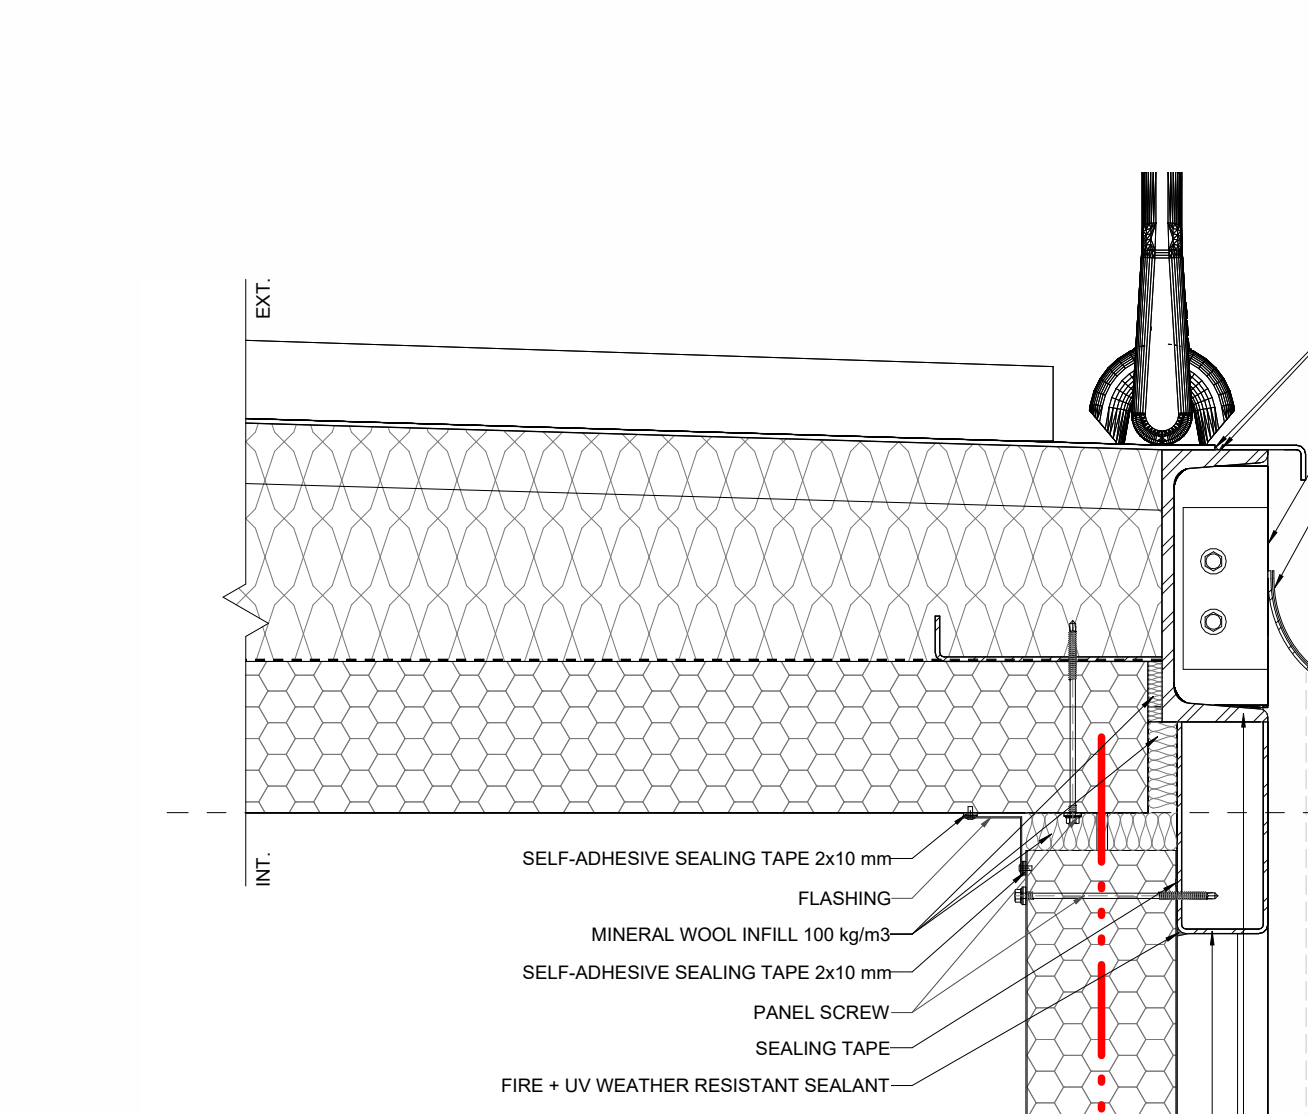
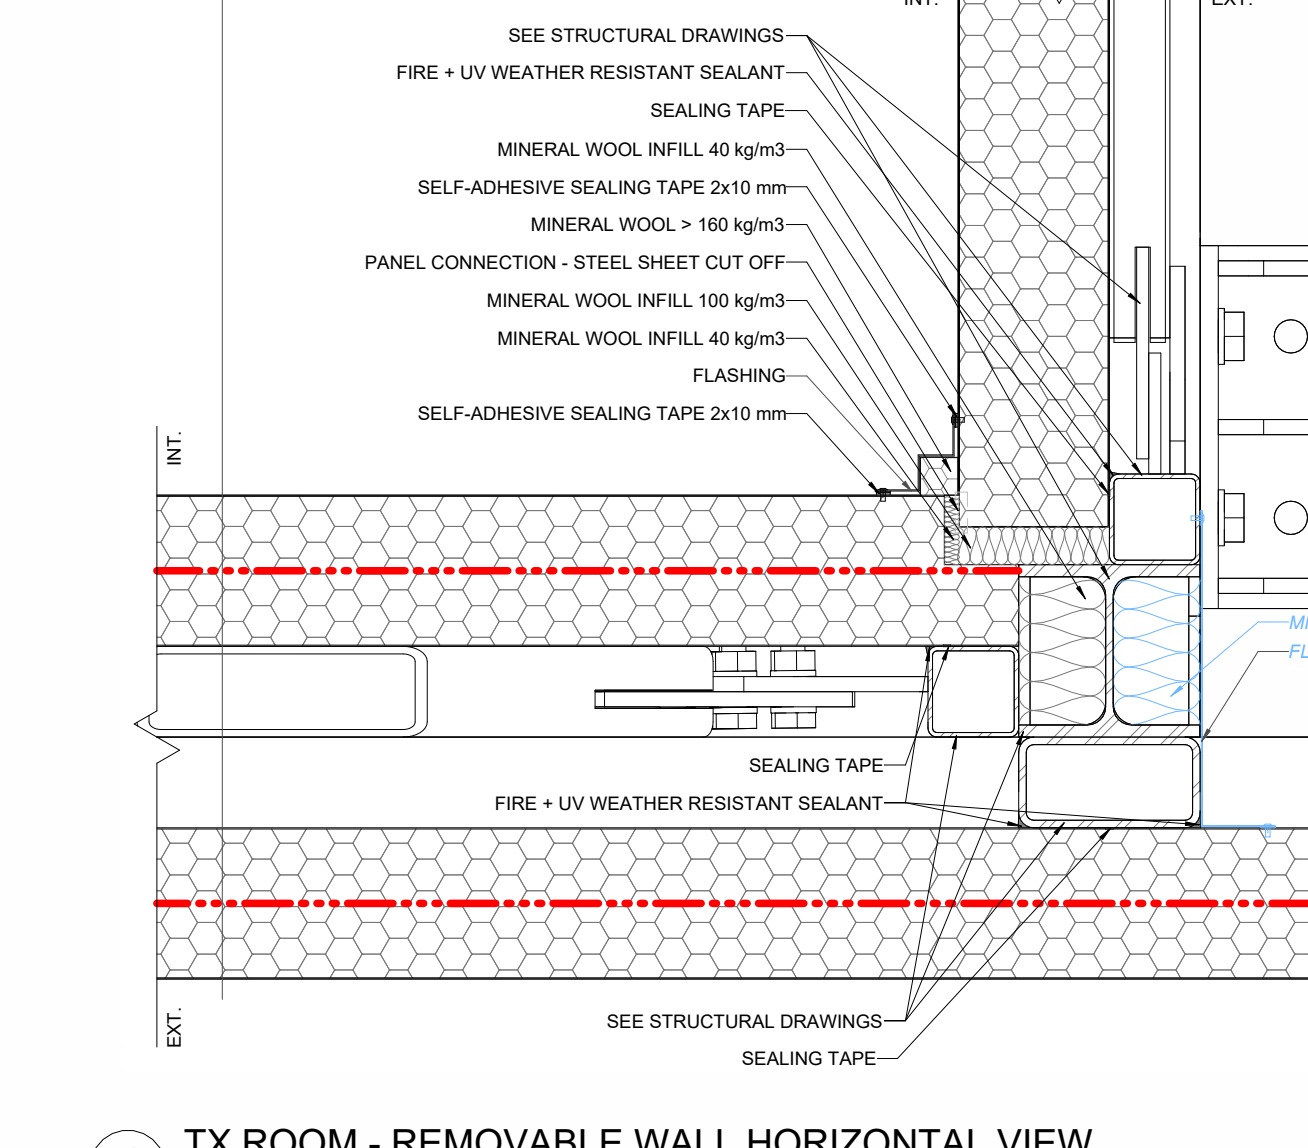
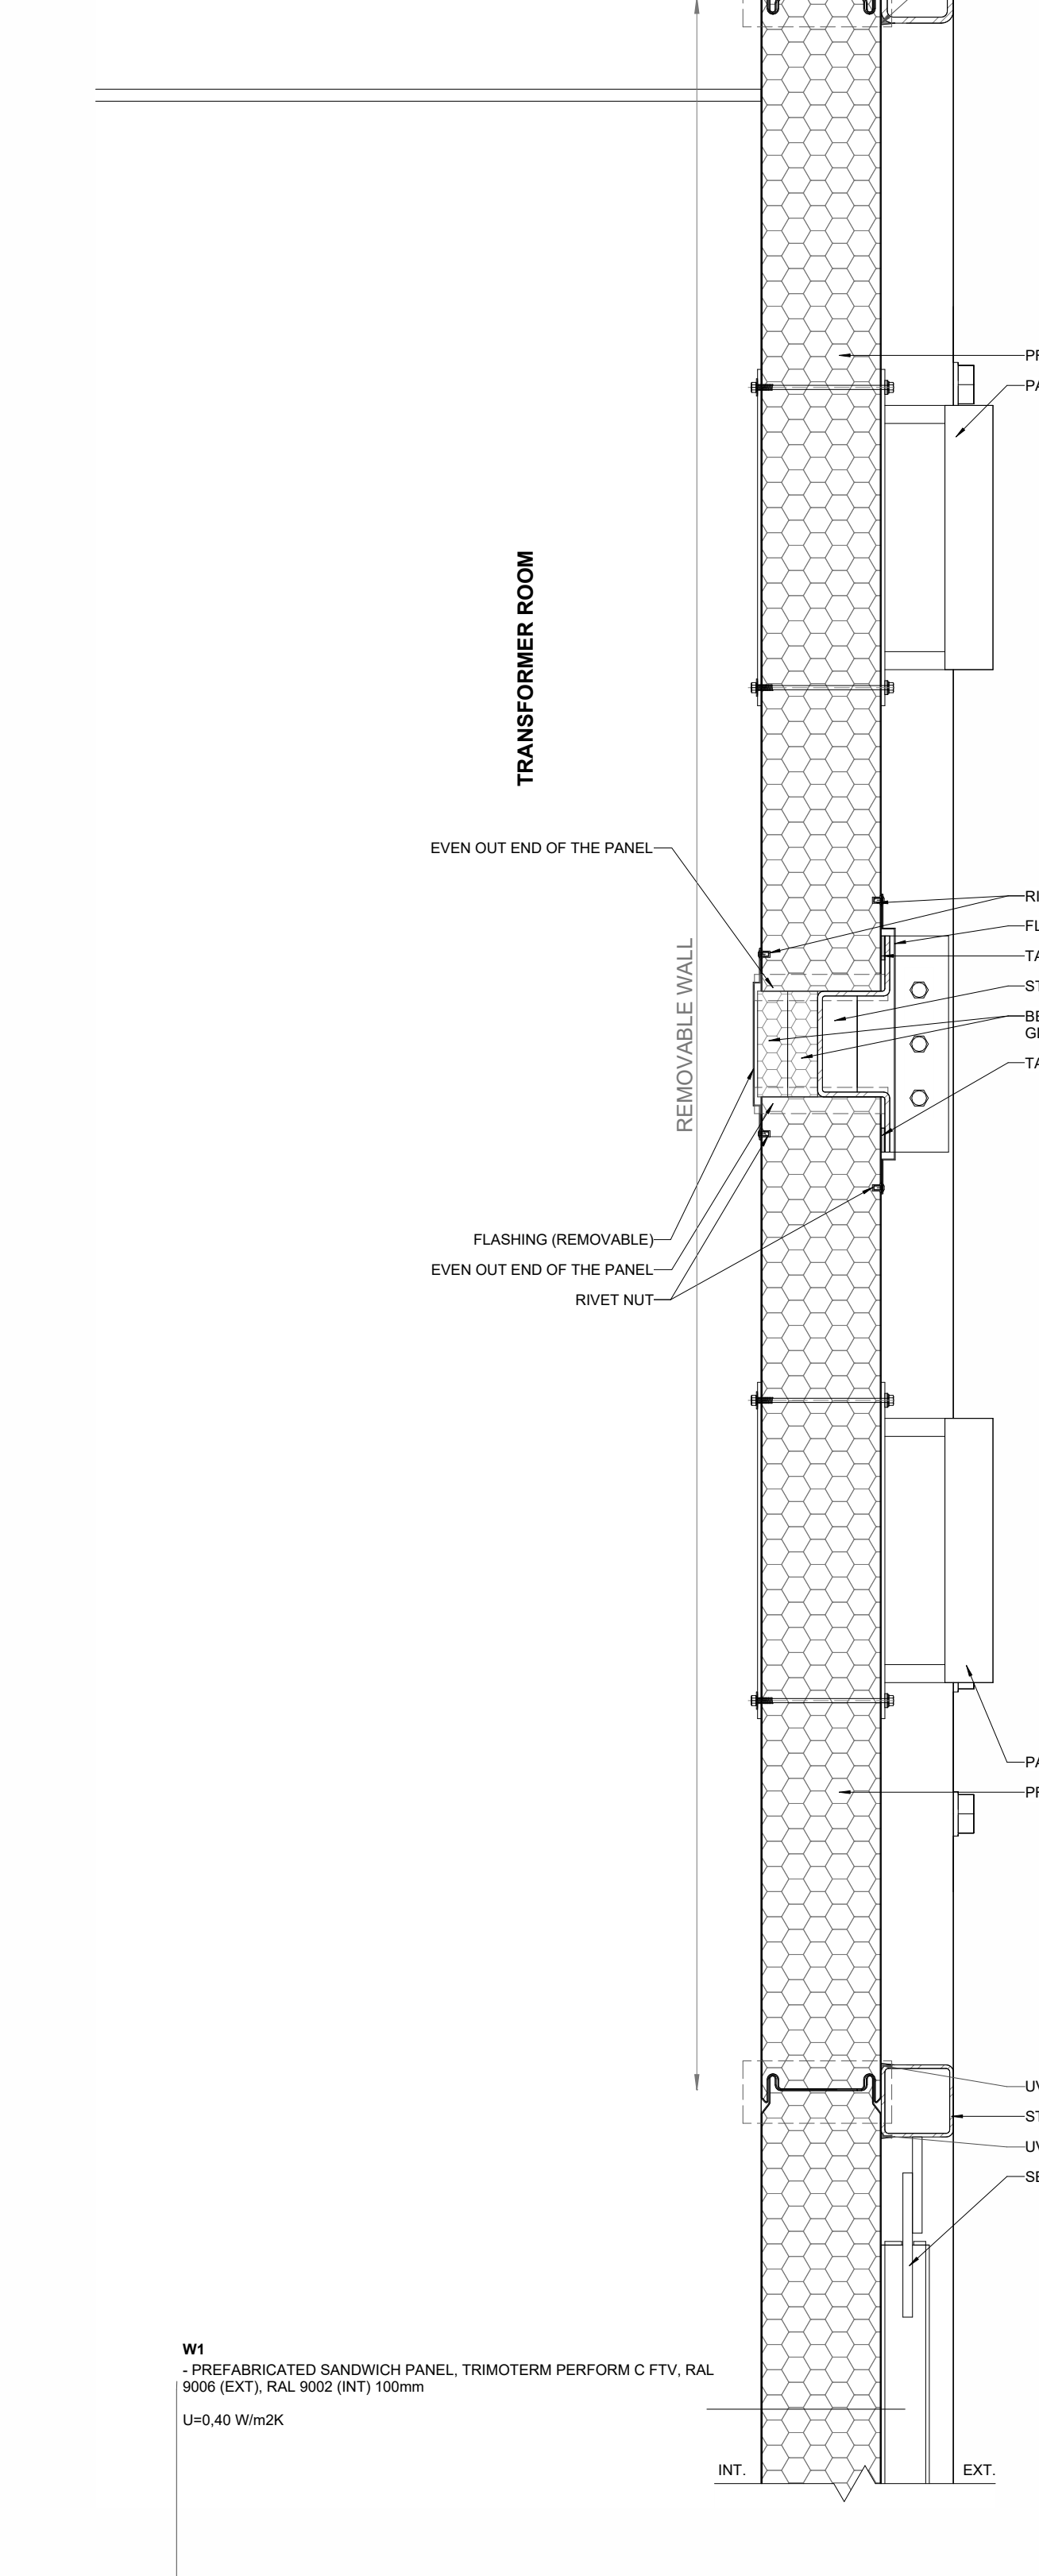
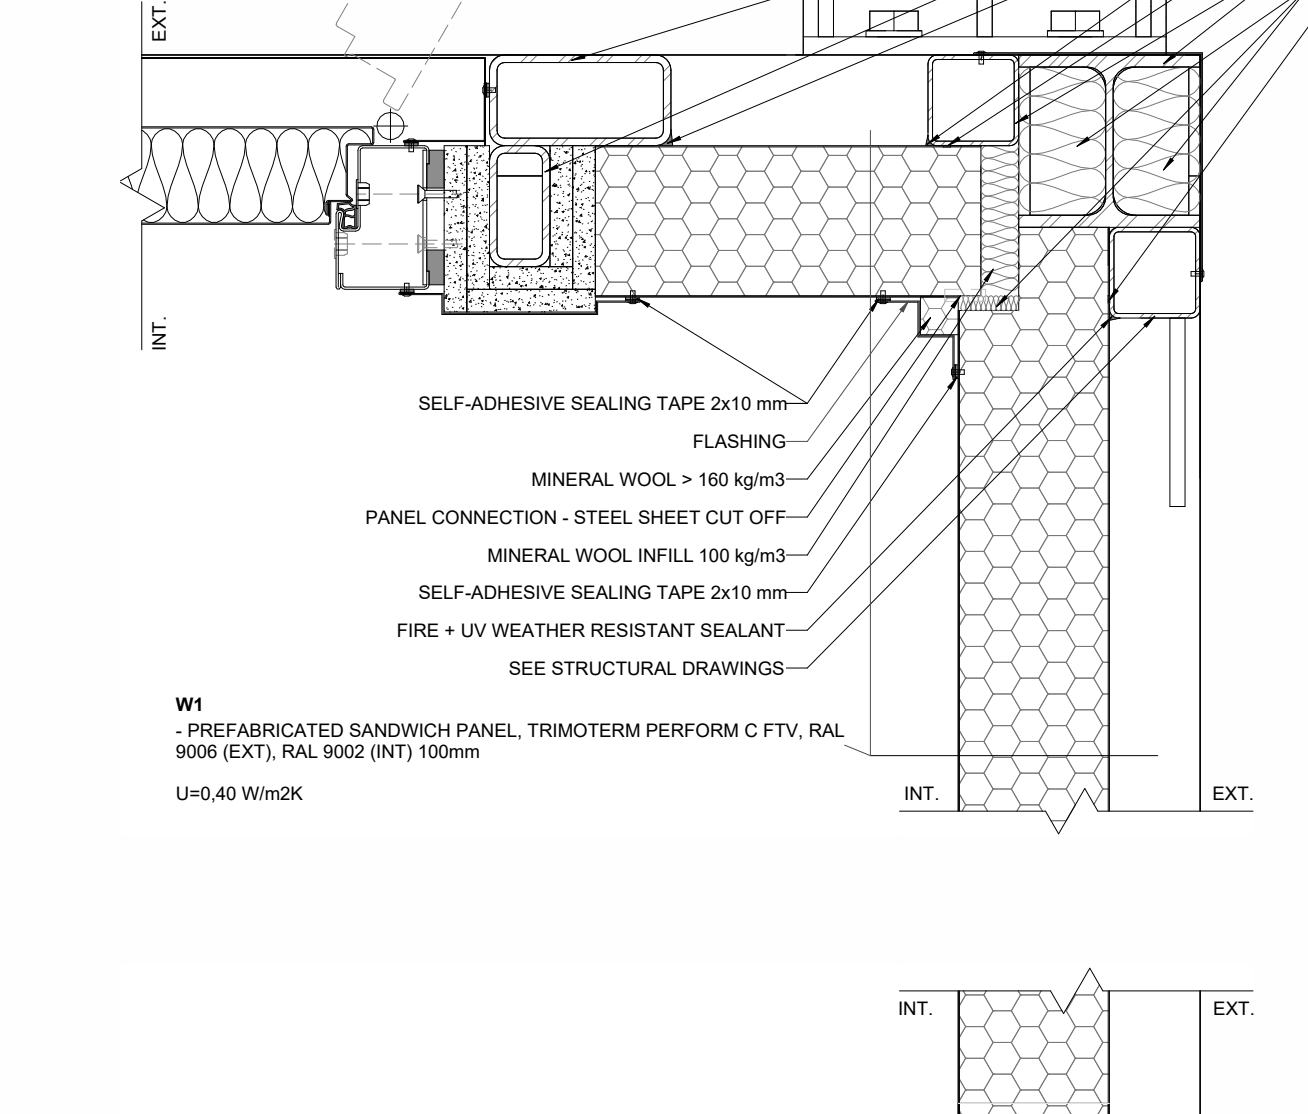
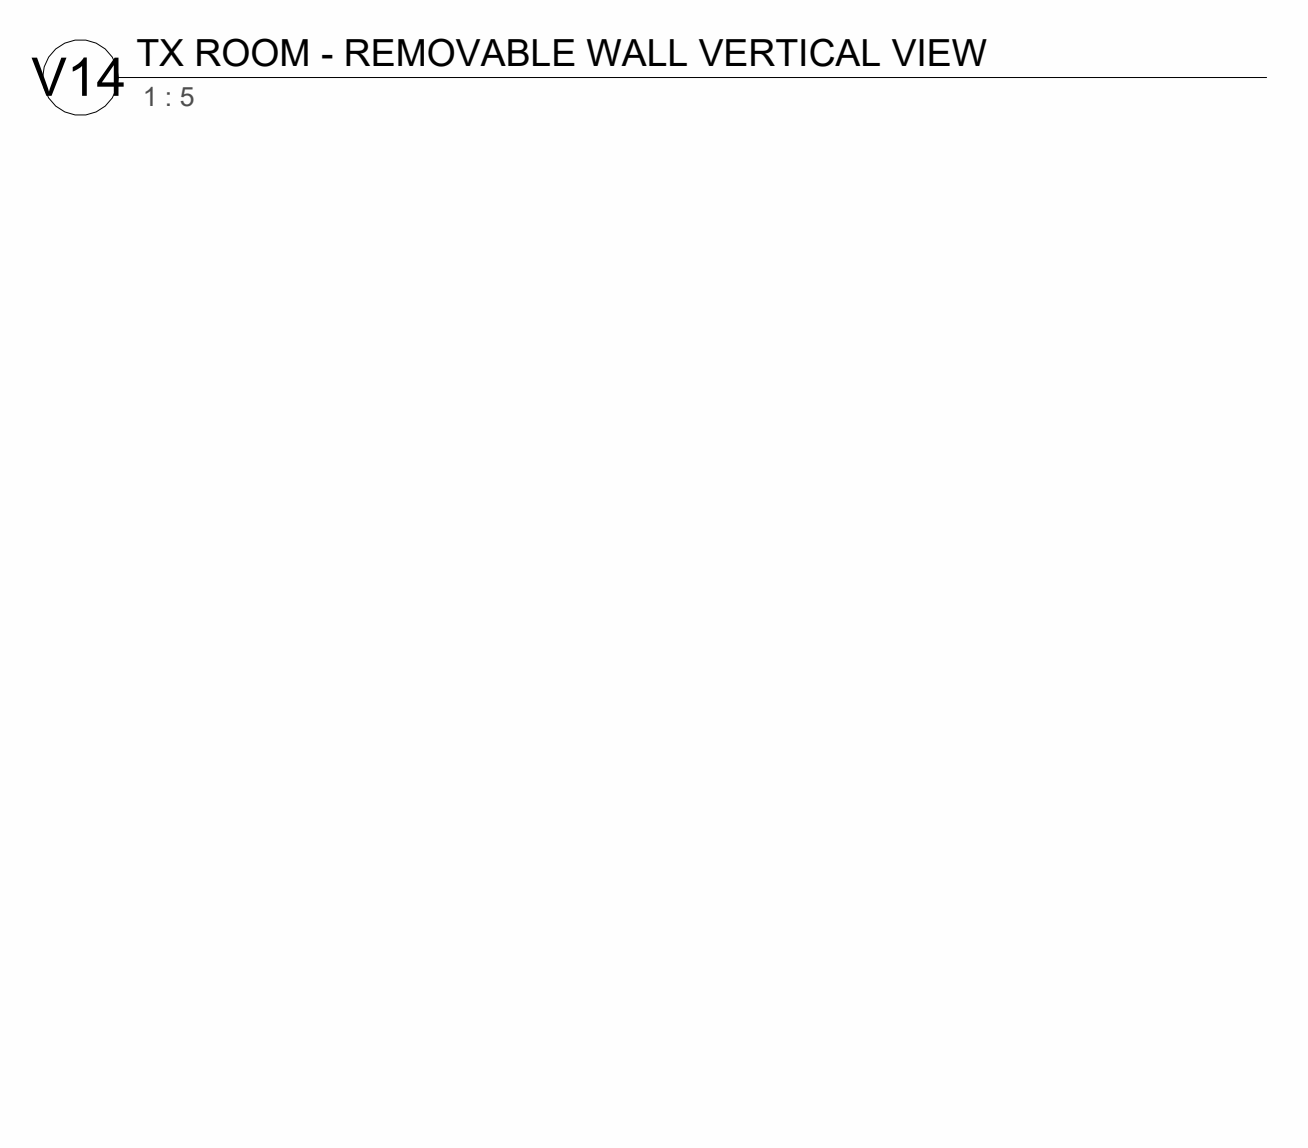
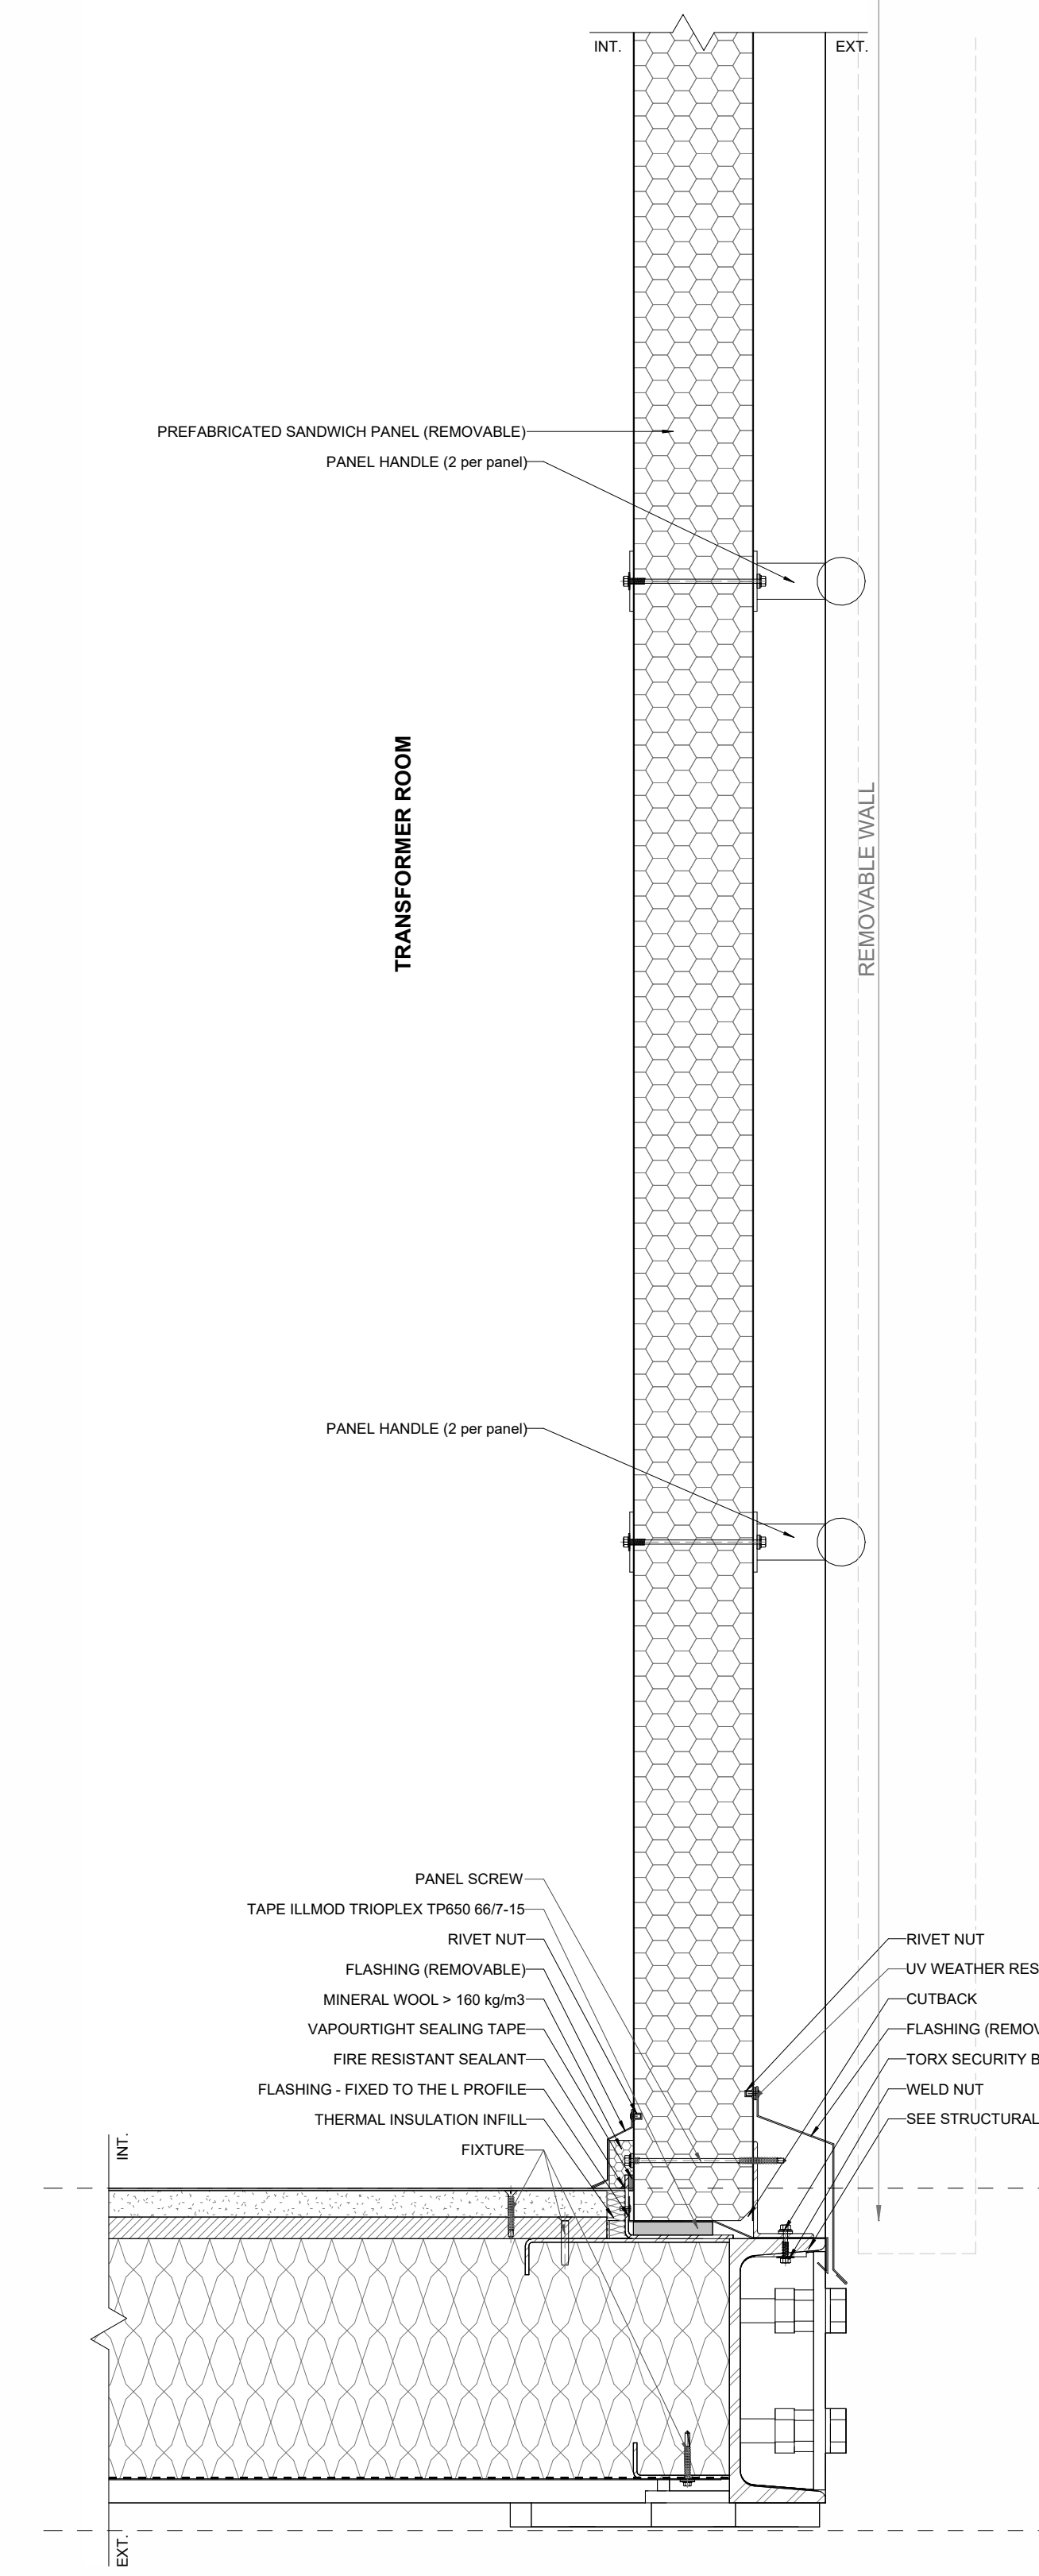
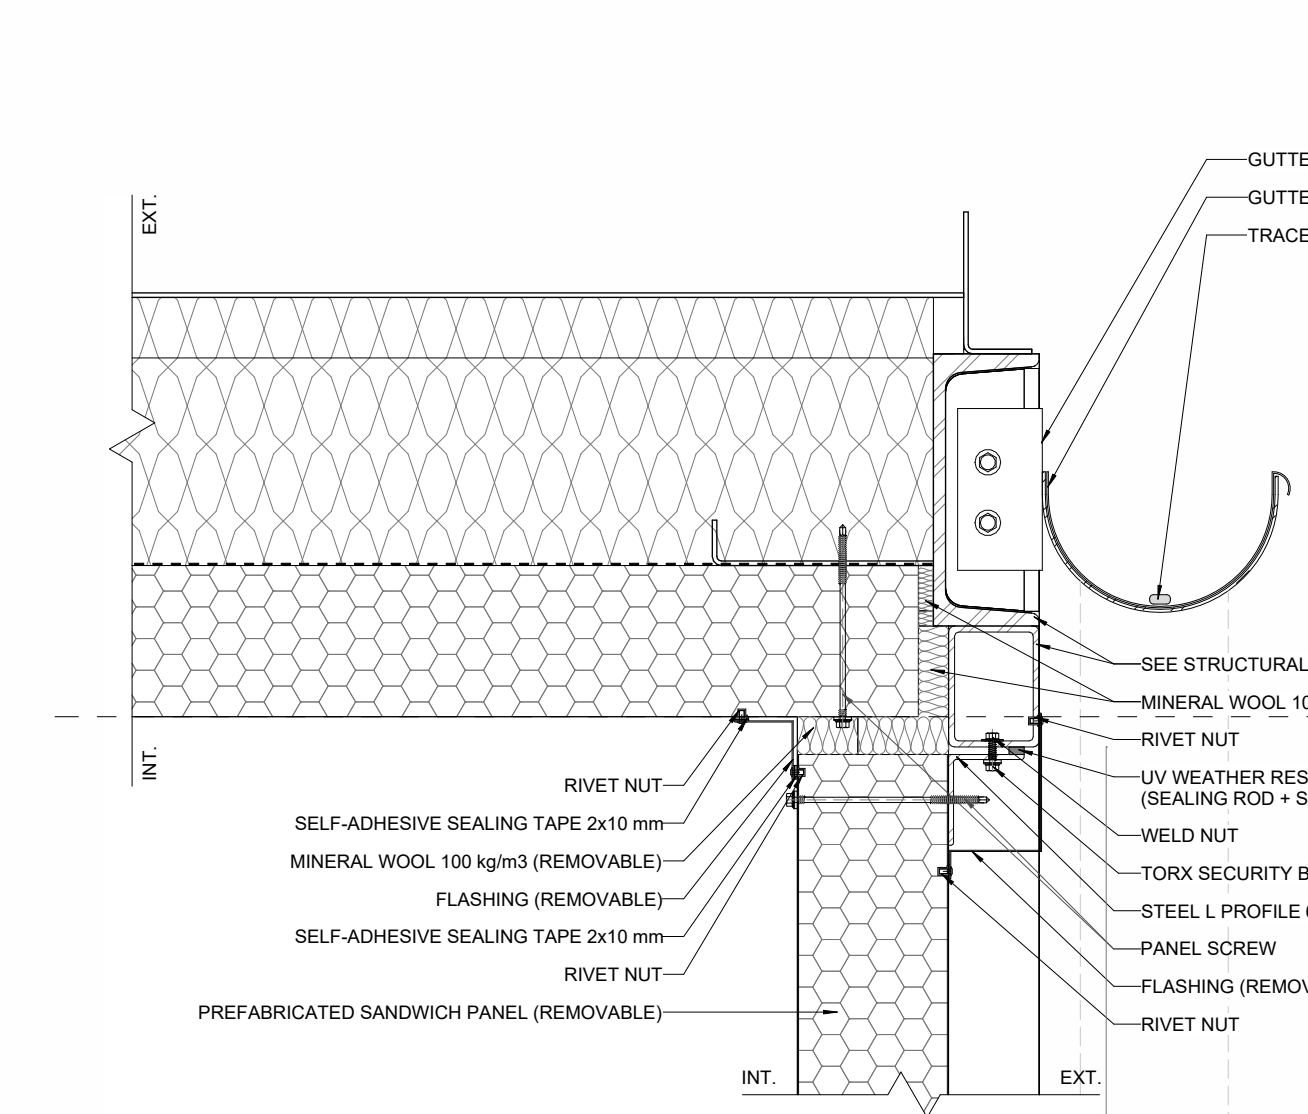
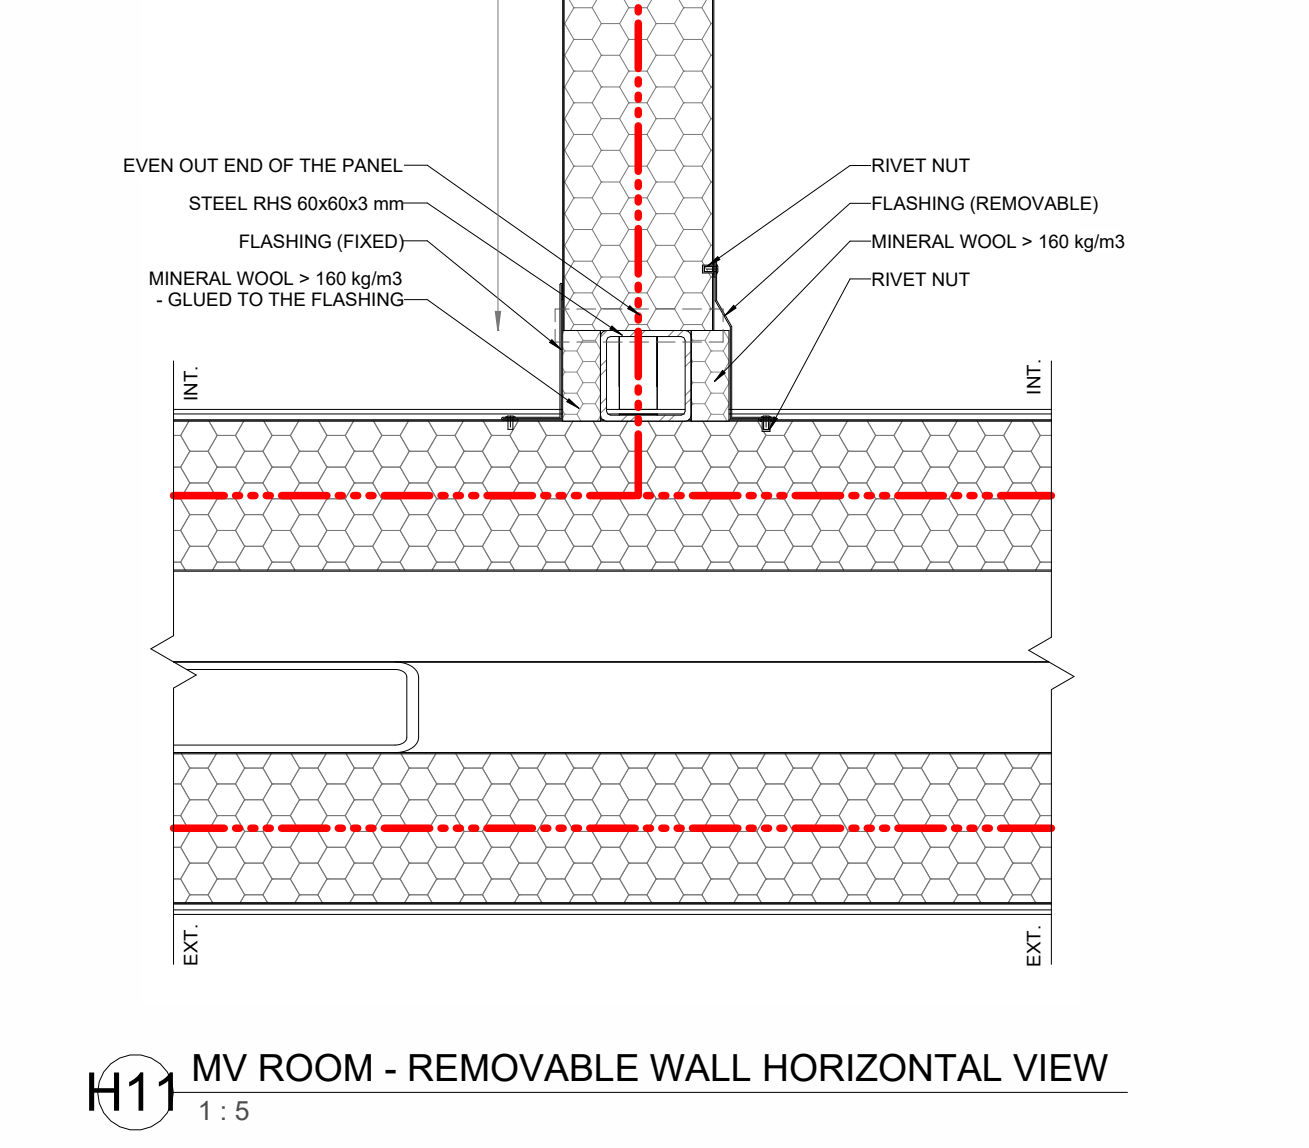
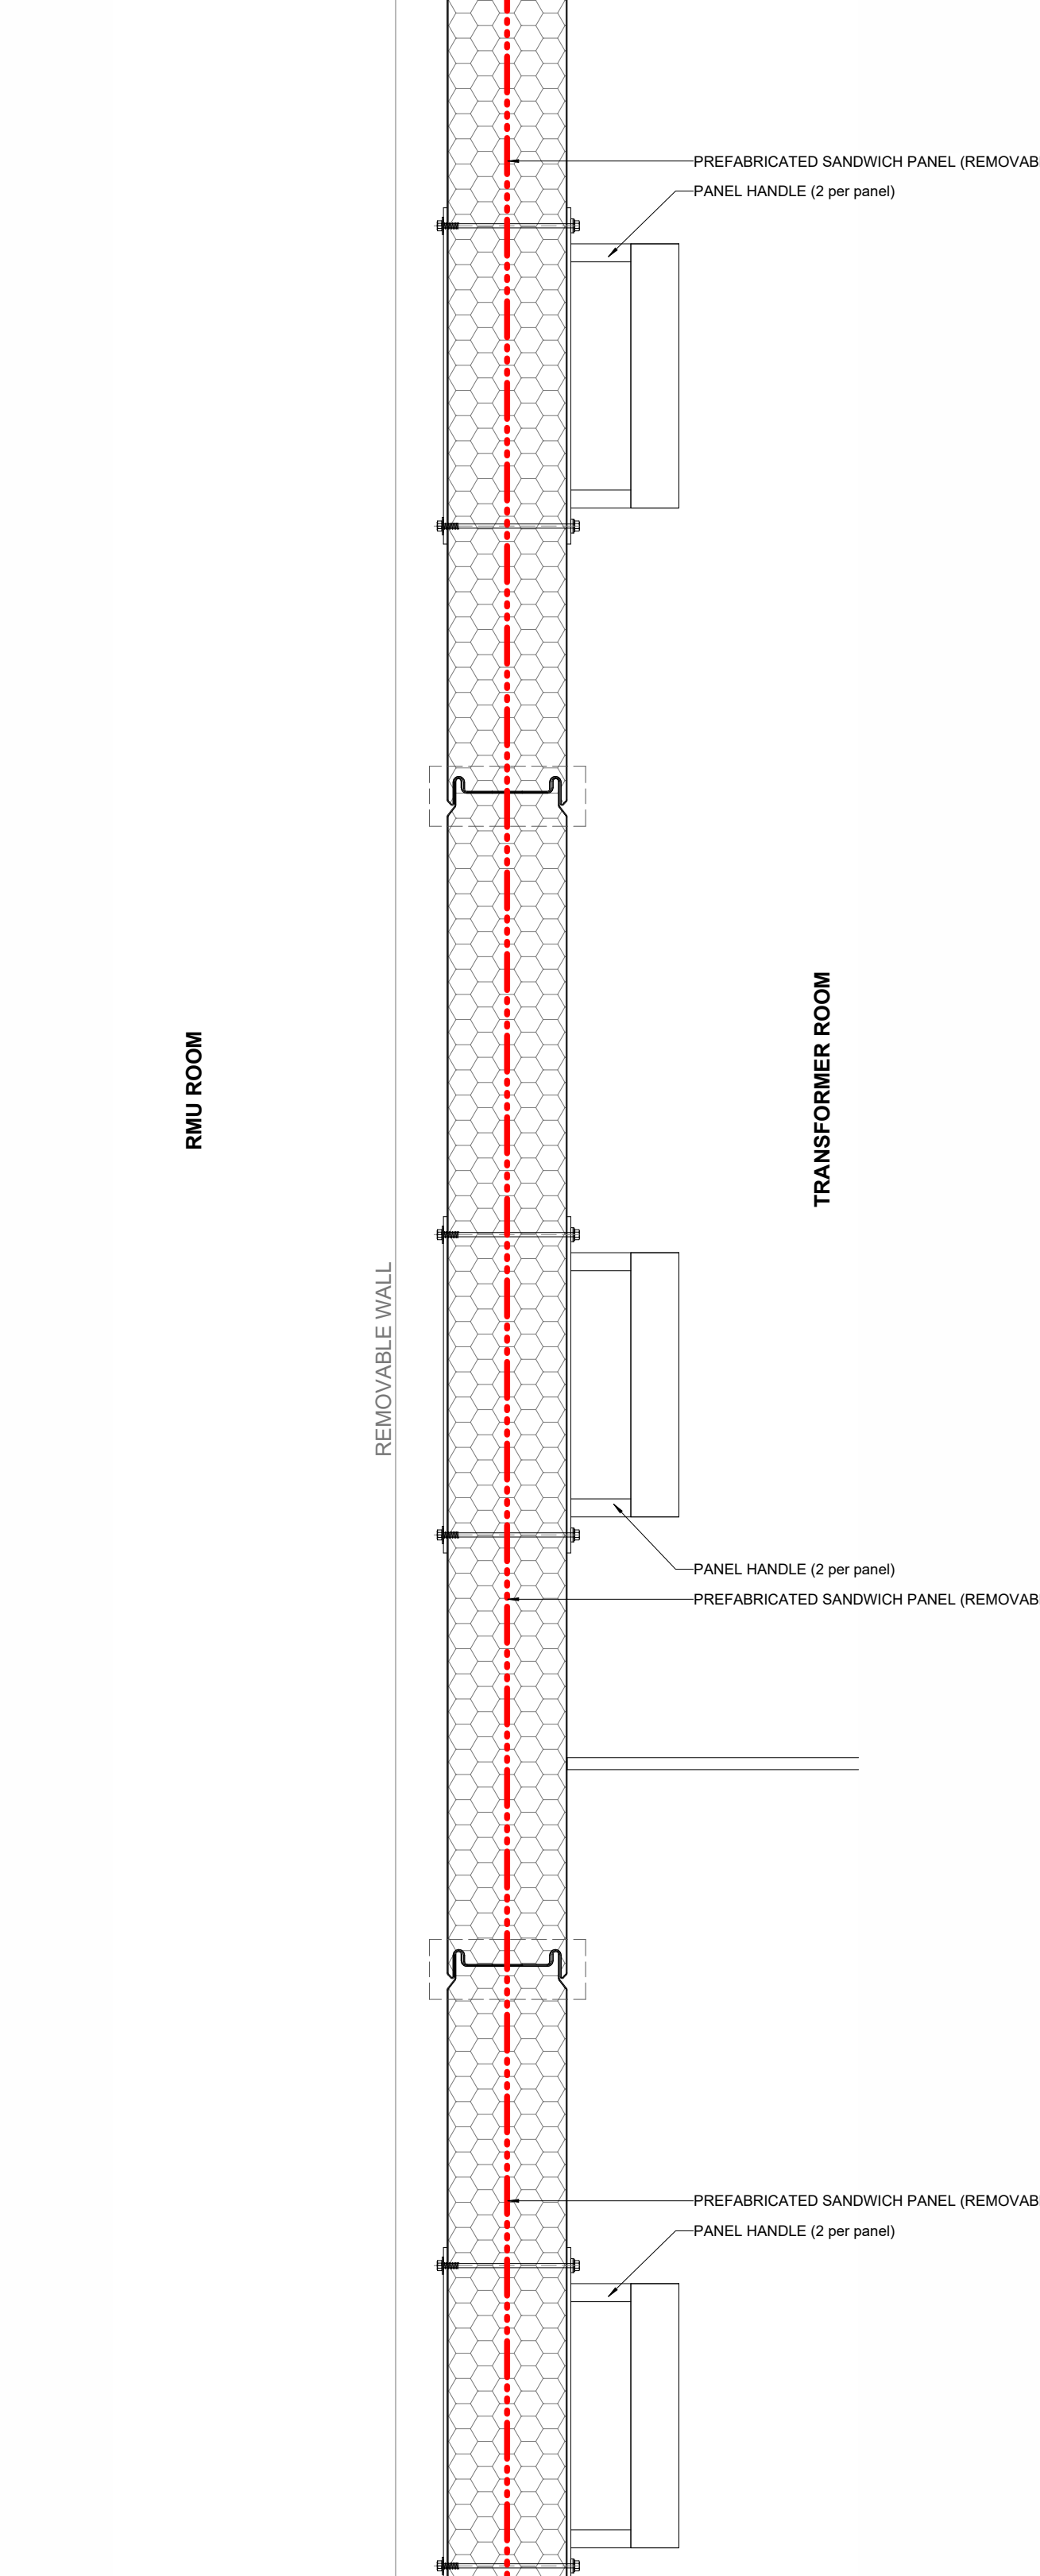
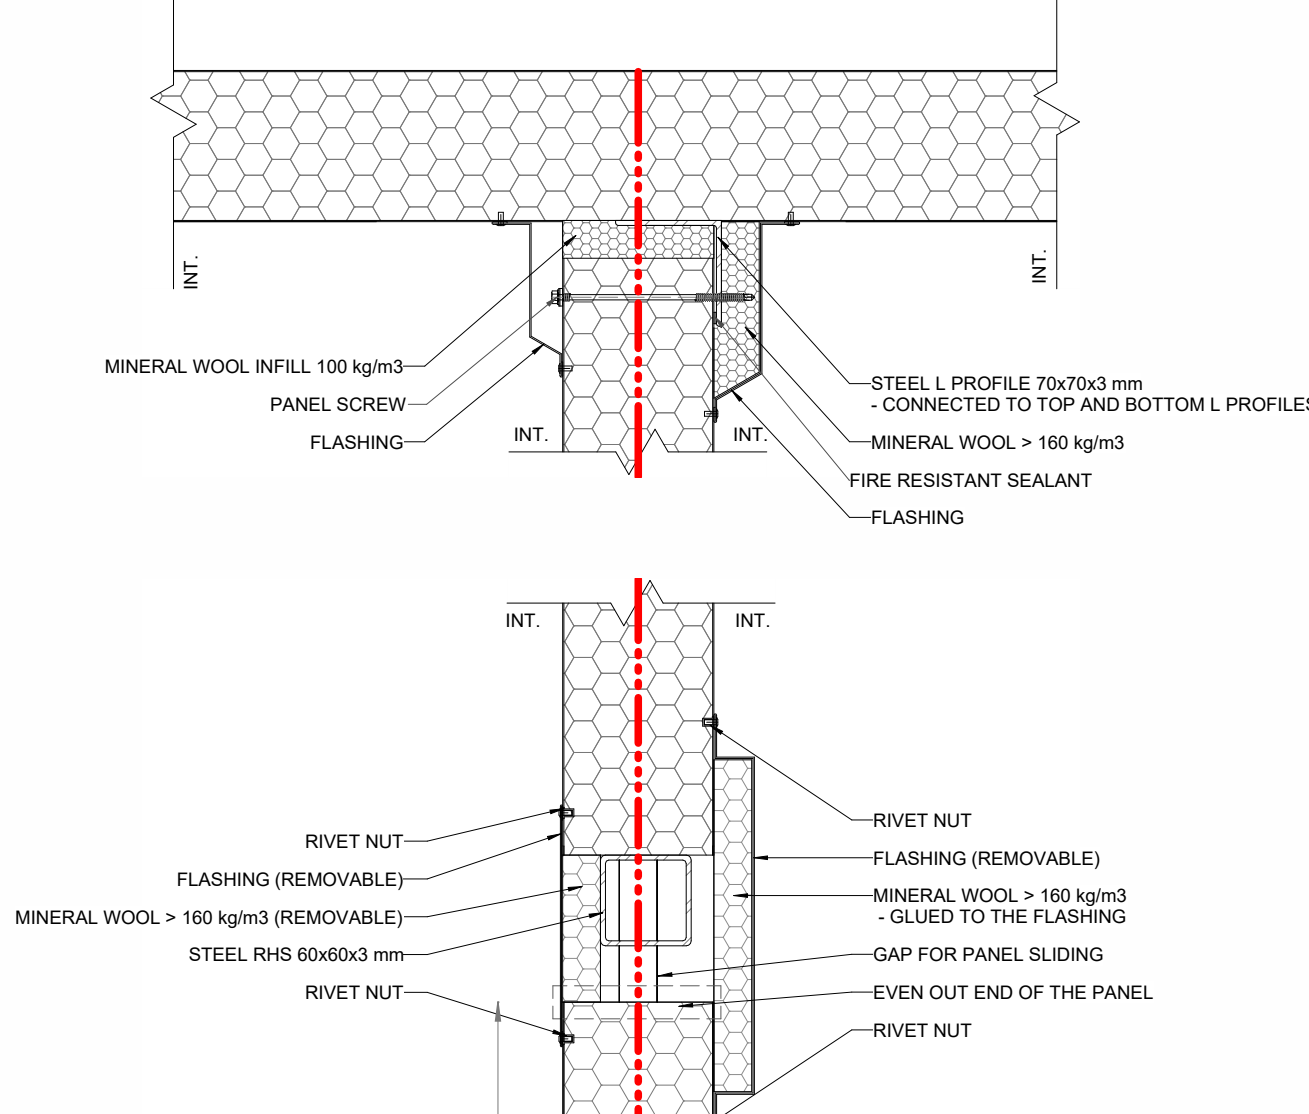
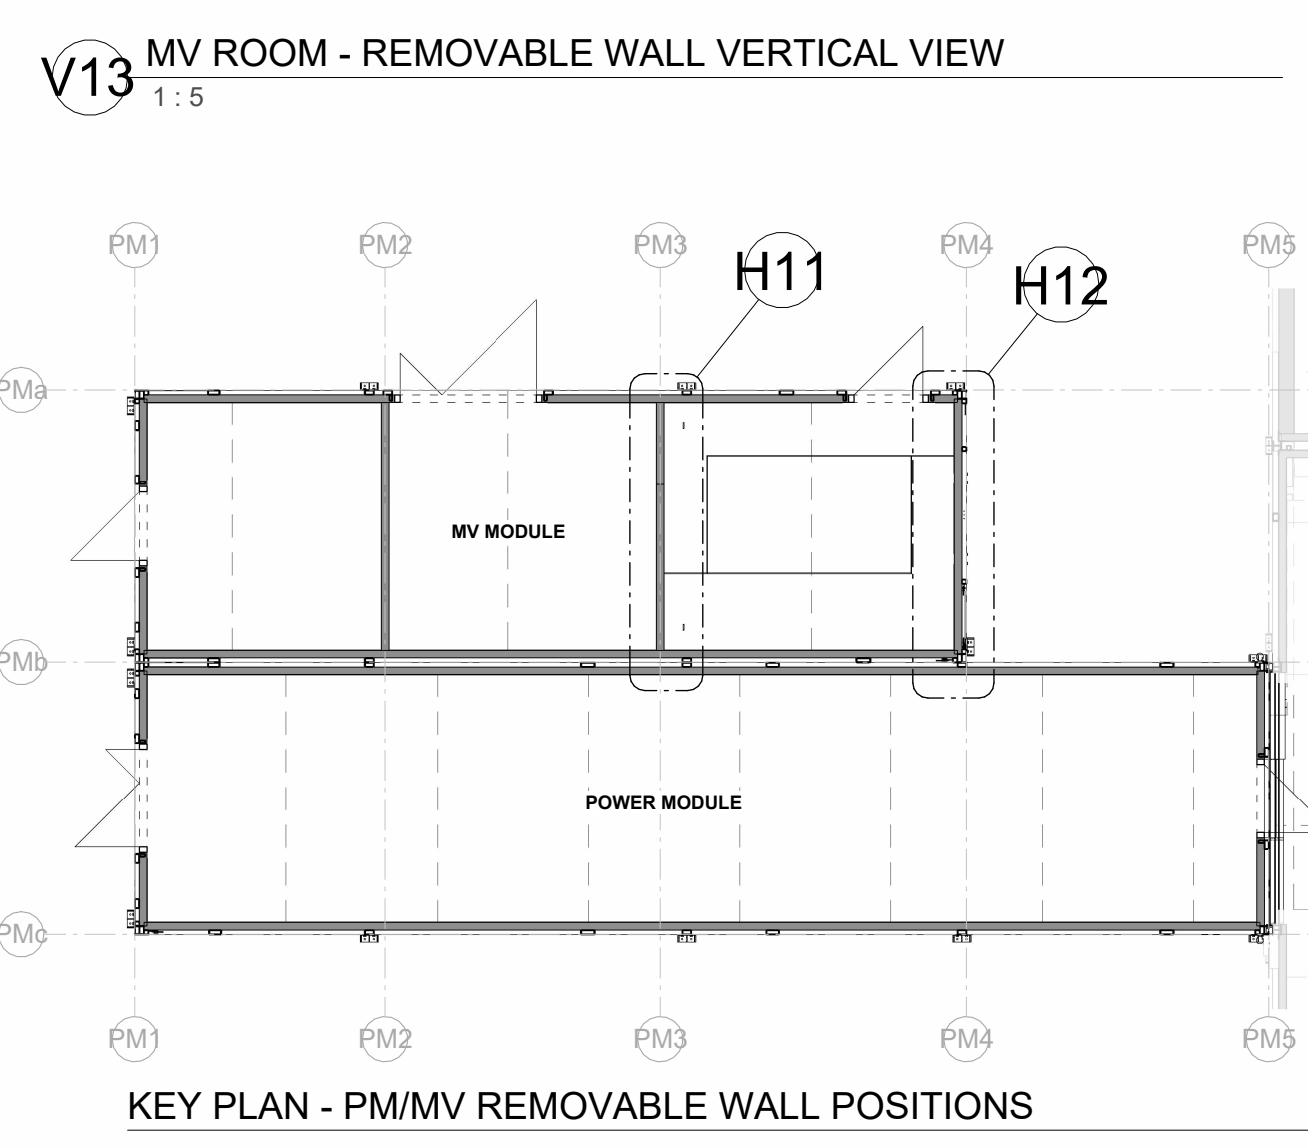
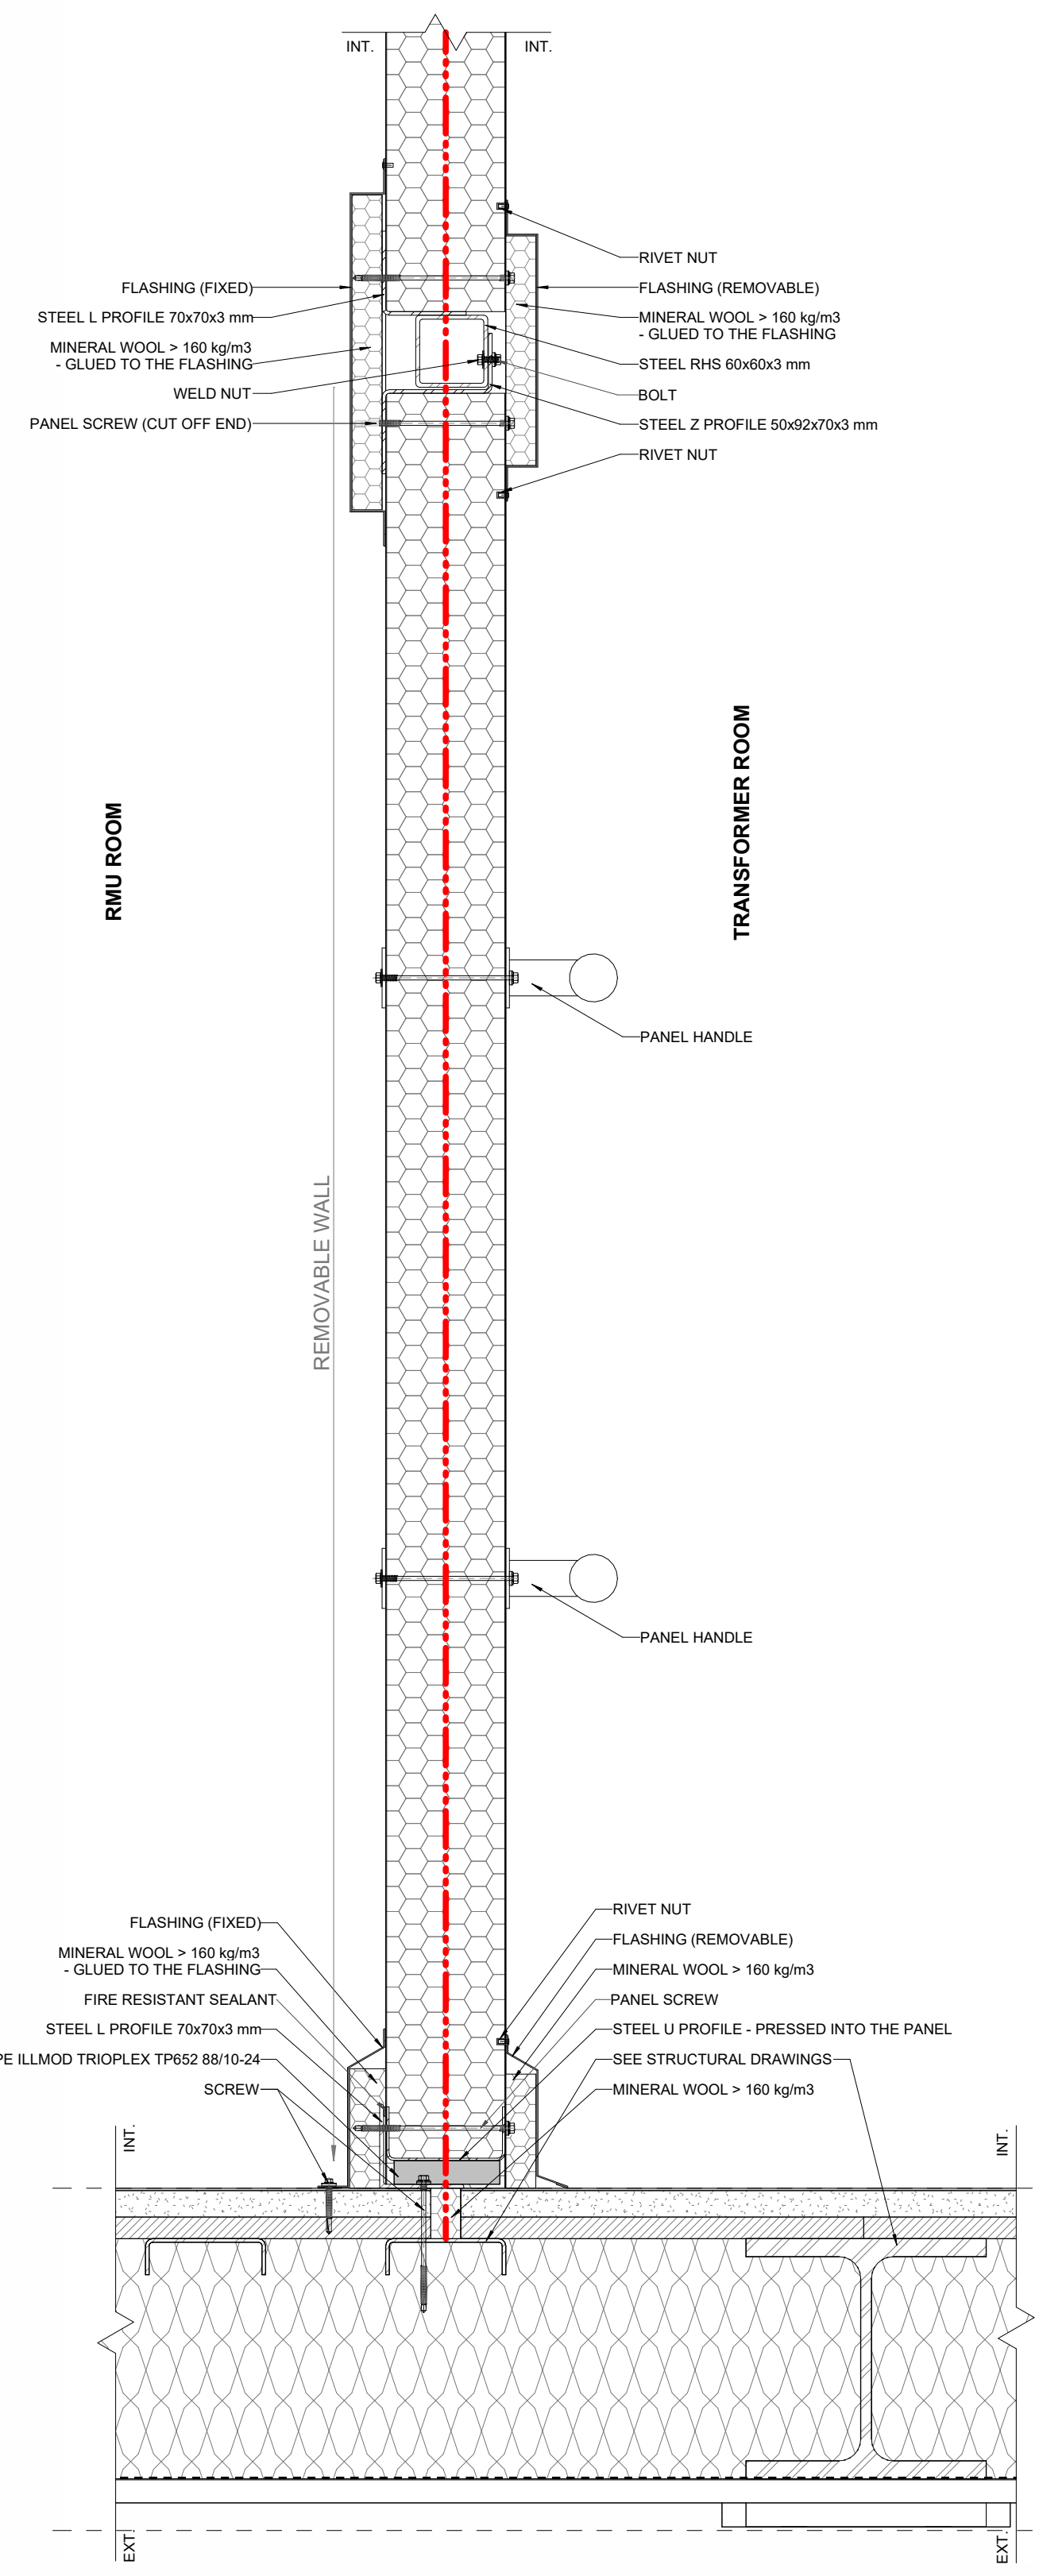


LEGAL DISCLAIMER: THIS DOCUMENT AND THE CONTENTS HEREIN ARE CONFIDENTIAL AND THE SOLE PROPERTY OF VERTIV GROUP CORP. REPRODUCTION, DISTRIBUTION OR UNAUTHORIZED USE OF THIS DOCUMENT OR ANY PARTS WITHIN THIS DOCUMENT ARE FORBIDDEN WITHOUT THE WRITTEN CONSENT OF VERTIV GROUP CORP.

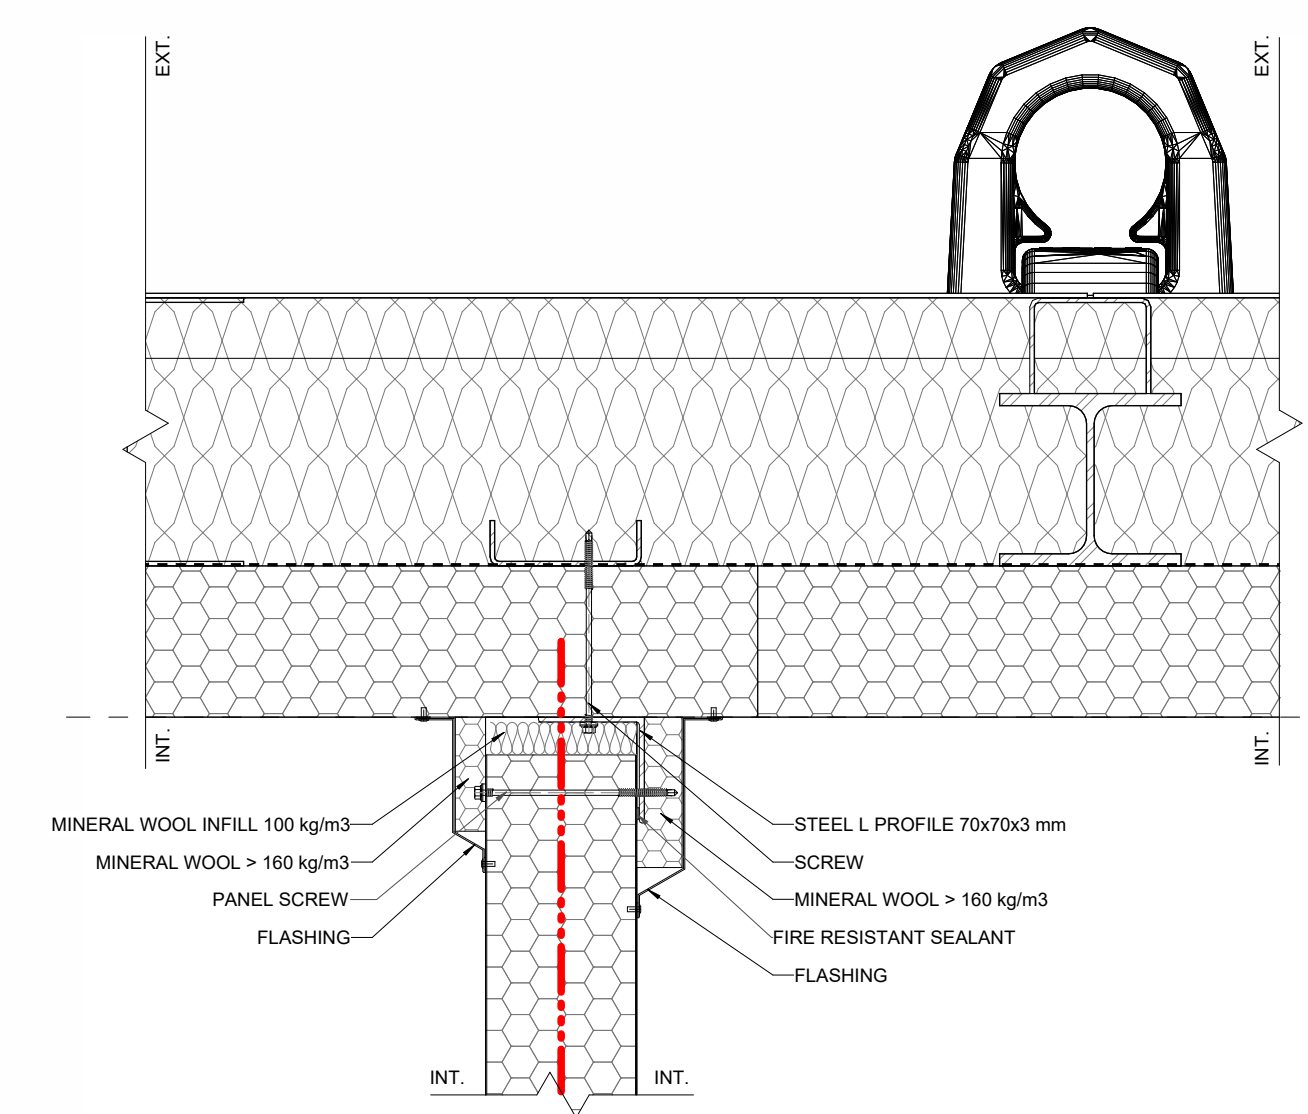

KEYNOTES

- FIRE COMPARTMENT BORDER (E-10)
- FIRE COMPARTMENT BORDER (E-10)
- ELEMENTS INSTALLED ON SITE

KEY PLAN

R02 CD SET - FOR INFORMATION 2026-09-11

R01 CD SET - FOR INFORMATION 2026-07-24

REV. DESCRIPTION DATE

VERTIV

PROJECT NAME: ECO DC MONALISA

DRAWING NAME: ARCHITECTURAL DETAILS - PREFABRICATED MODULES - REMOVABLE WALL - PM - MV - MS

PREPARED BY: L. MAVREK / K. KOZINA

CHECKED BY: M. PACAK

DATE: 2026-09-11

ECO DC VRT-MDC19-00-DR-A-50103

1:5

2026-09-11

R02

SHEET 1 OF 1