




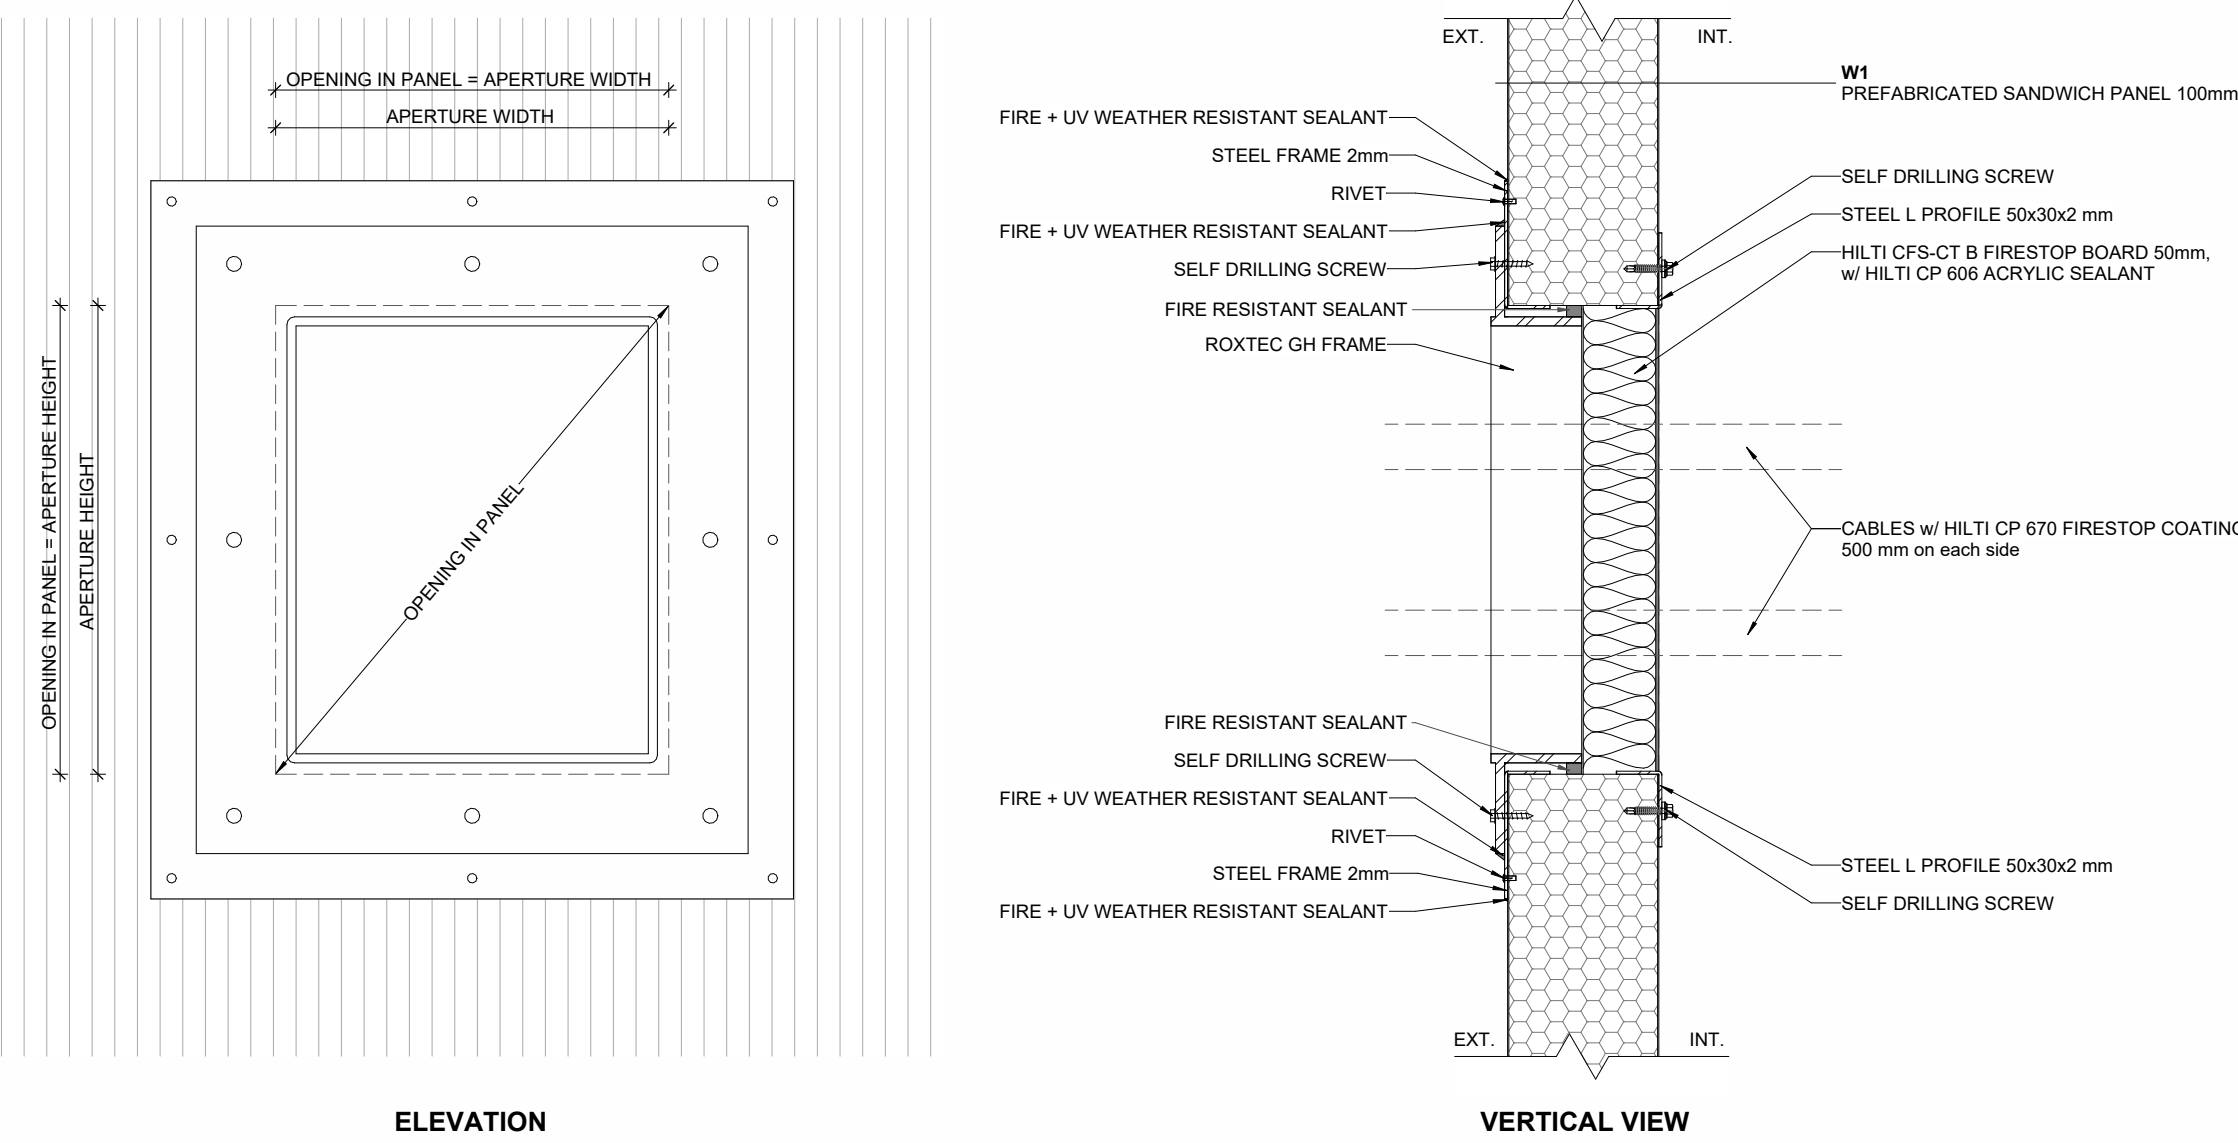


P01 ROXTEC GH - EXTERIOR WALL 100 mm
1:5

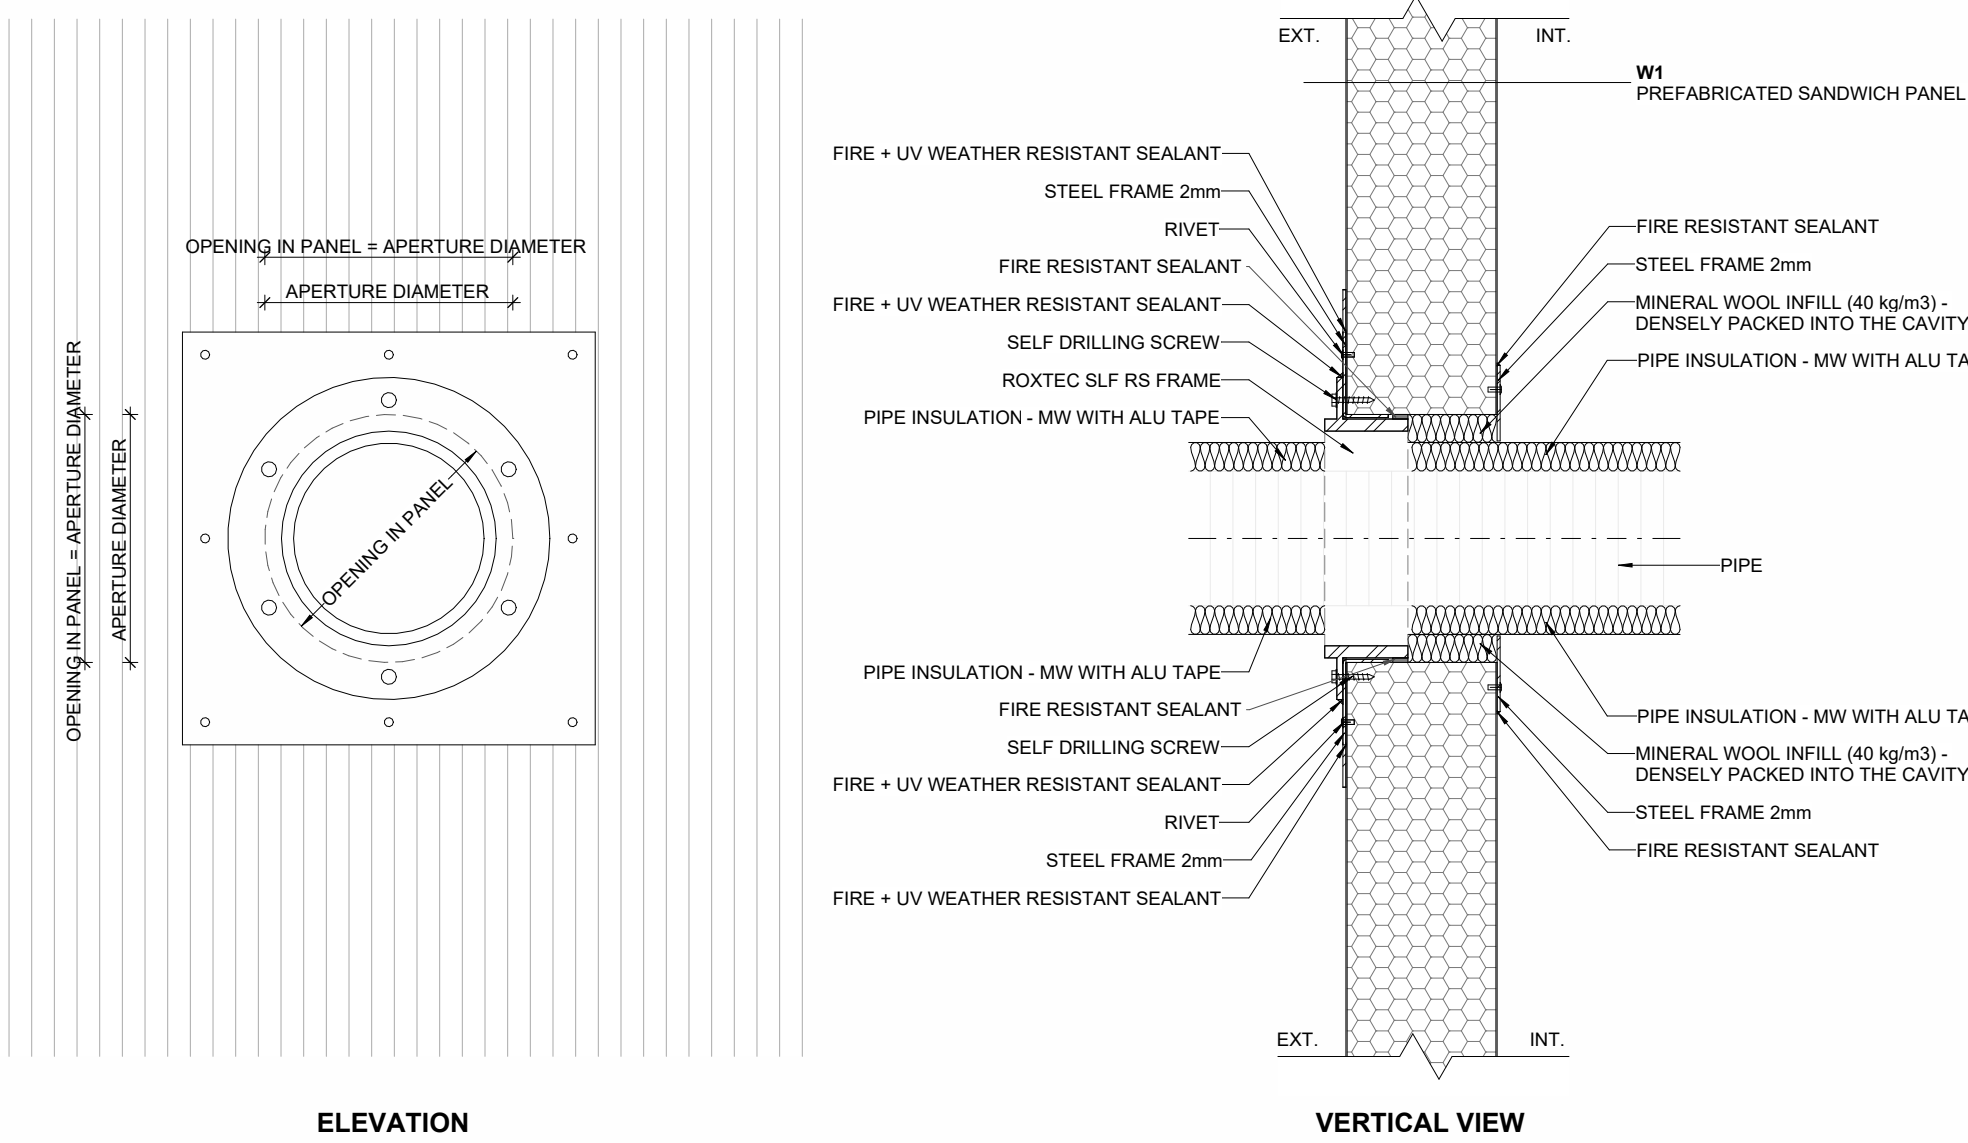


P02 ROXTEC SLF RS - EXTERIOR WALL 100 mm
1:5

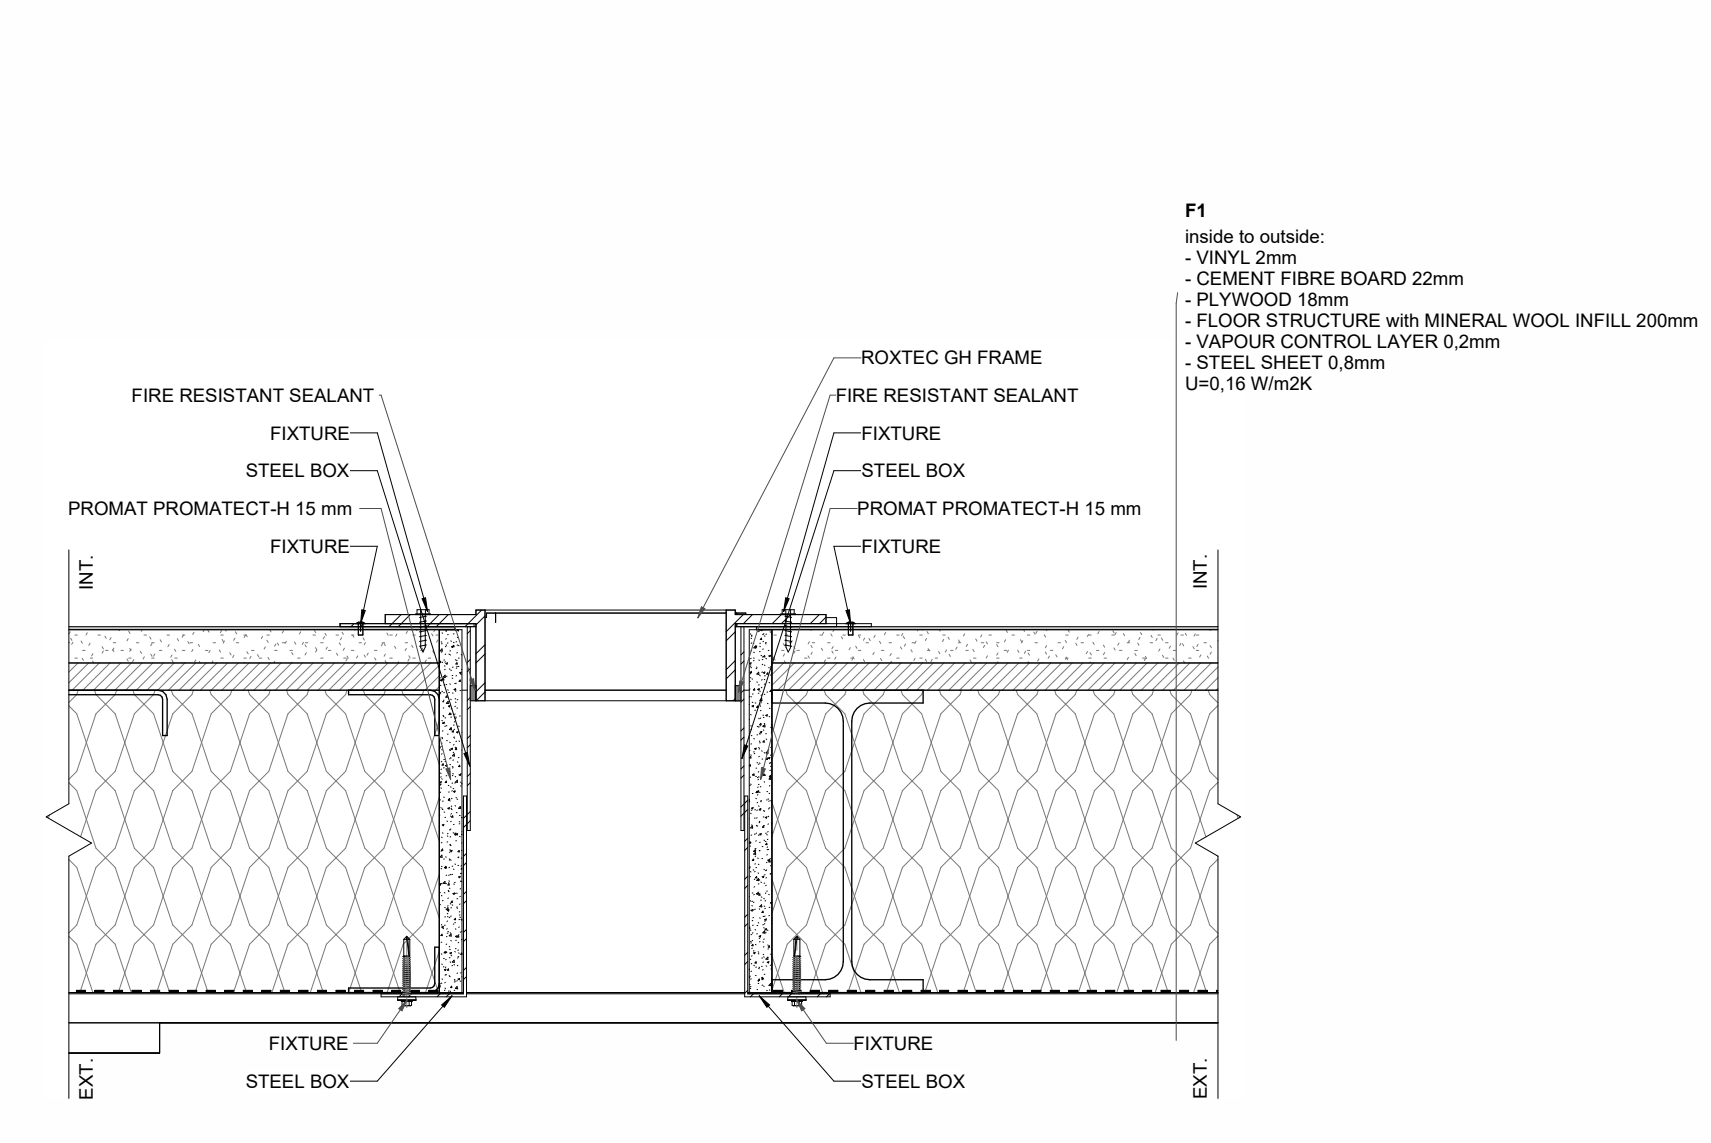


P03 ROXTEC GH - FLOOR
1:5

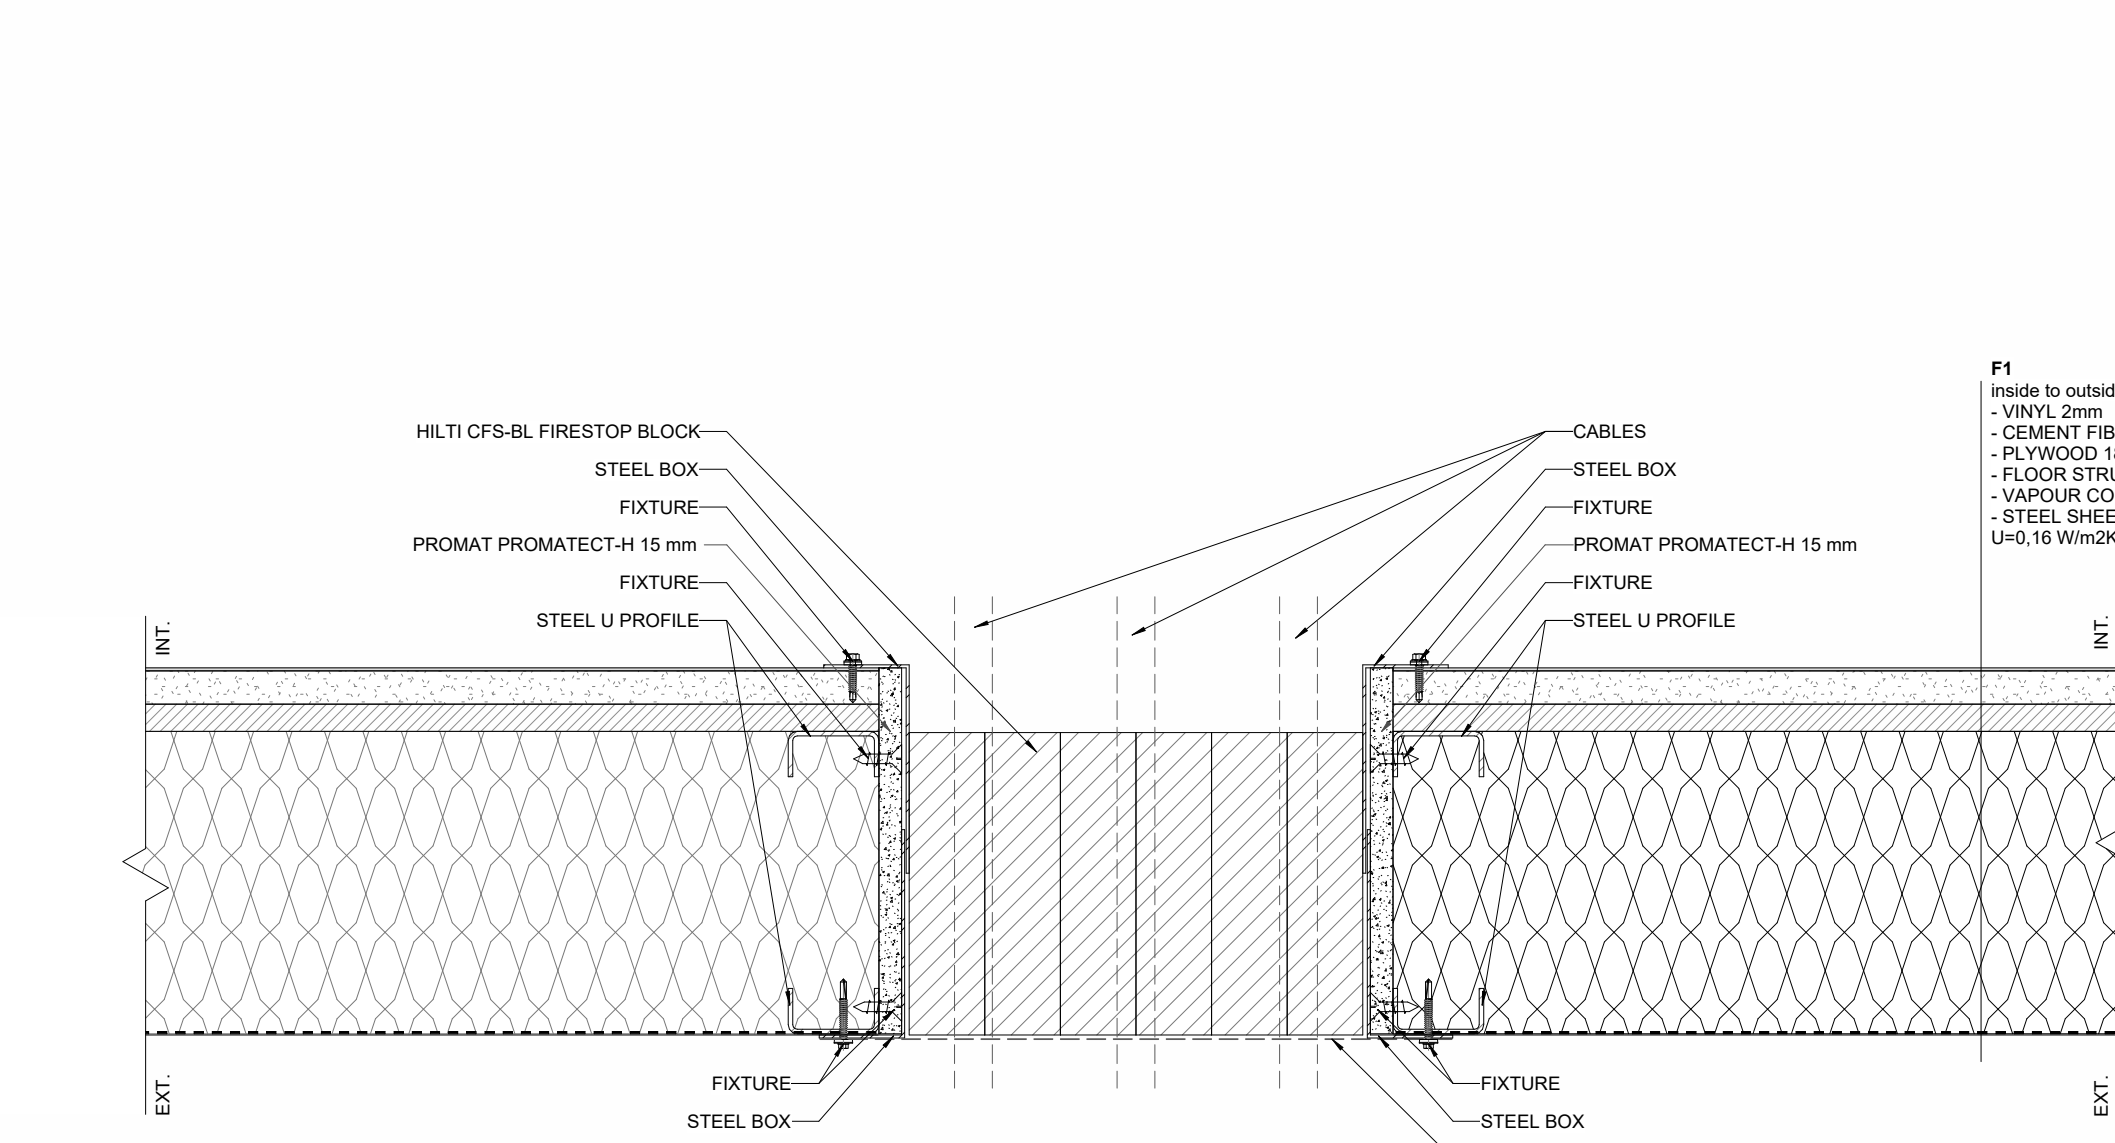


P15 HILTI CFS-BL FIRESTOP BLOCKS - FLOOR
1:5

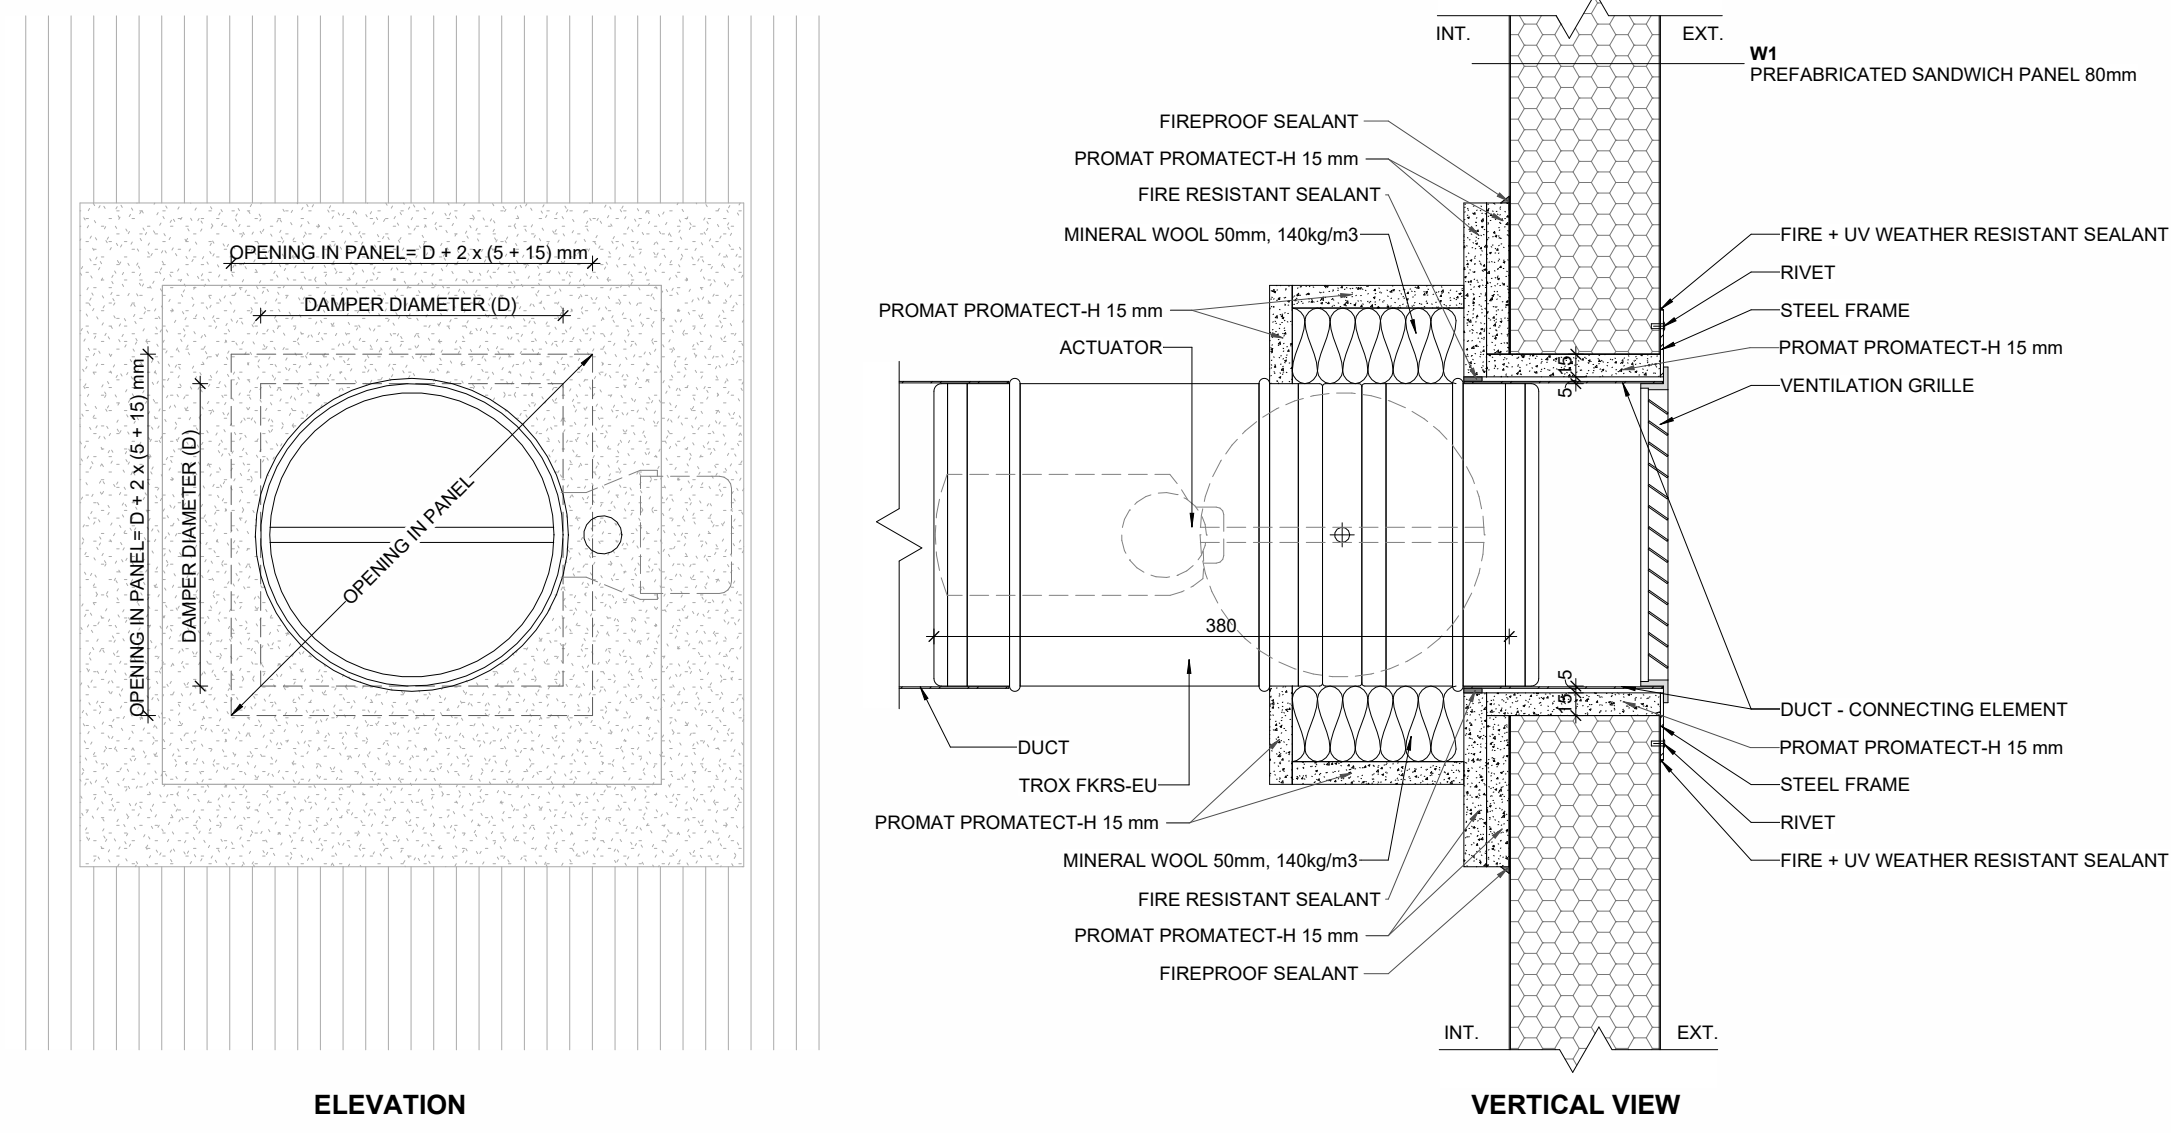


P06 TROX FKRS-EU
1:5

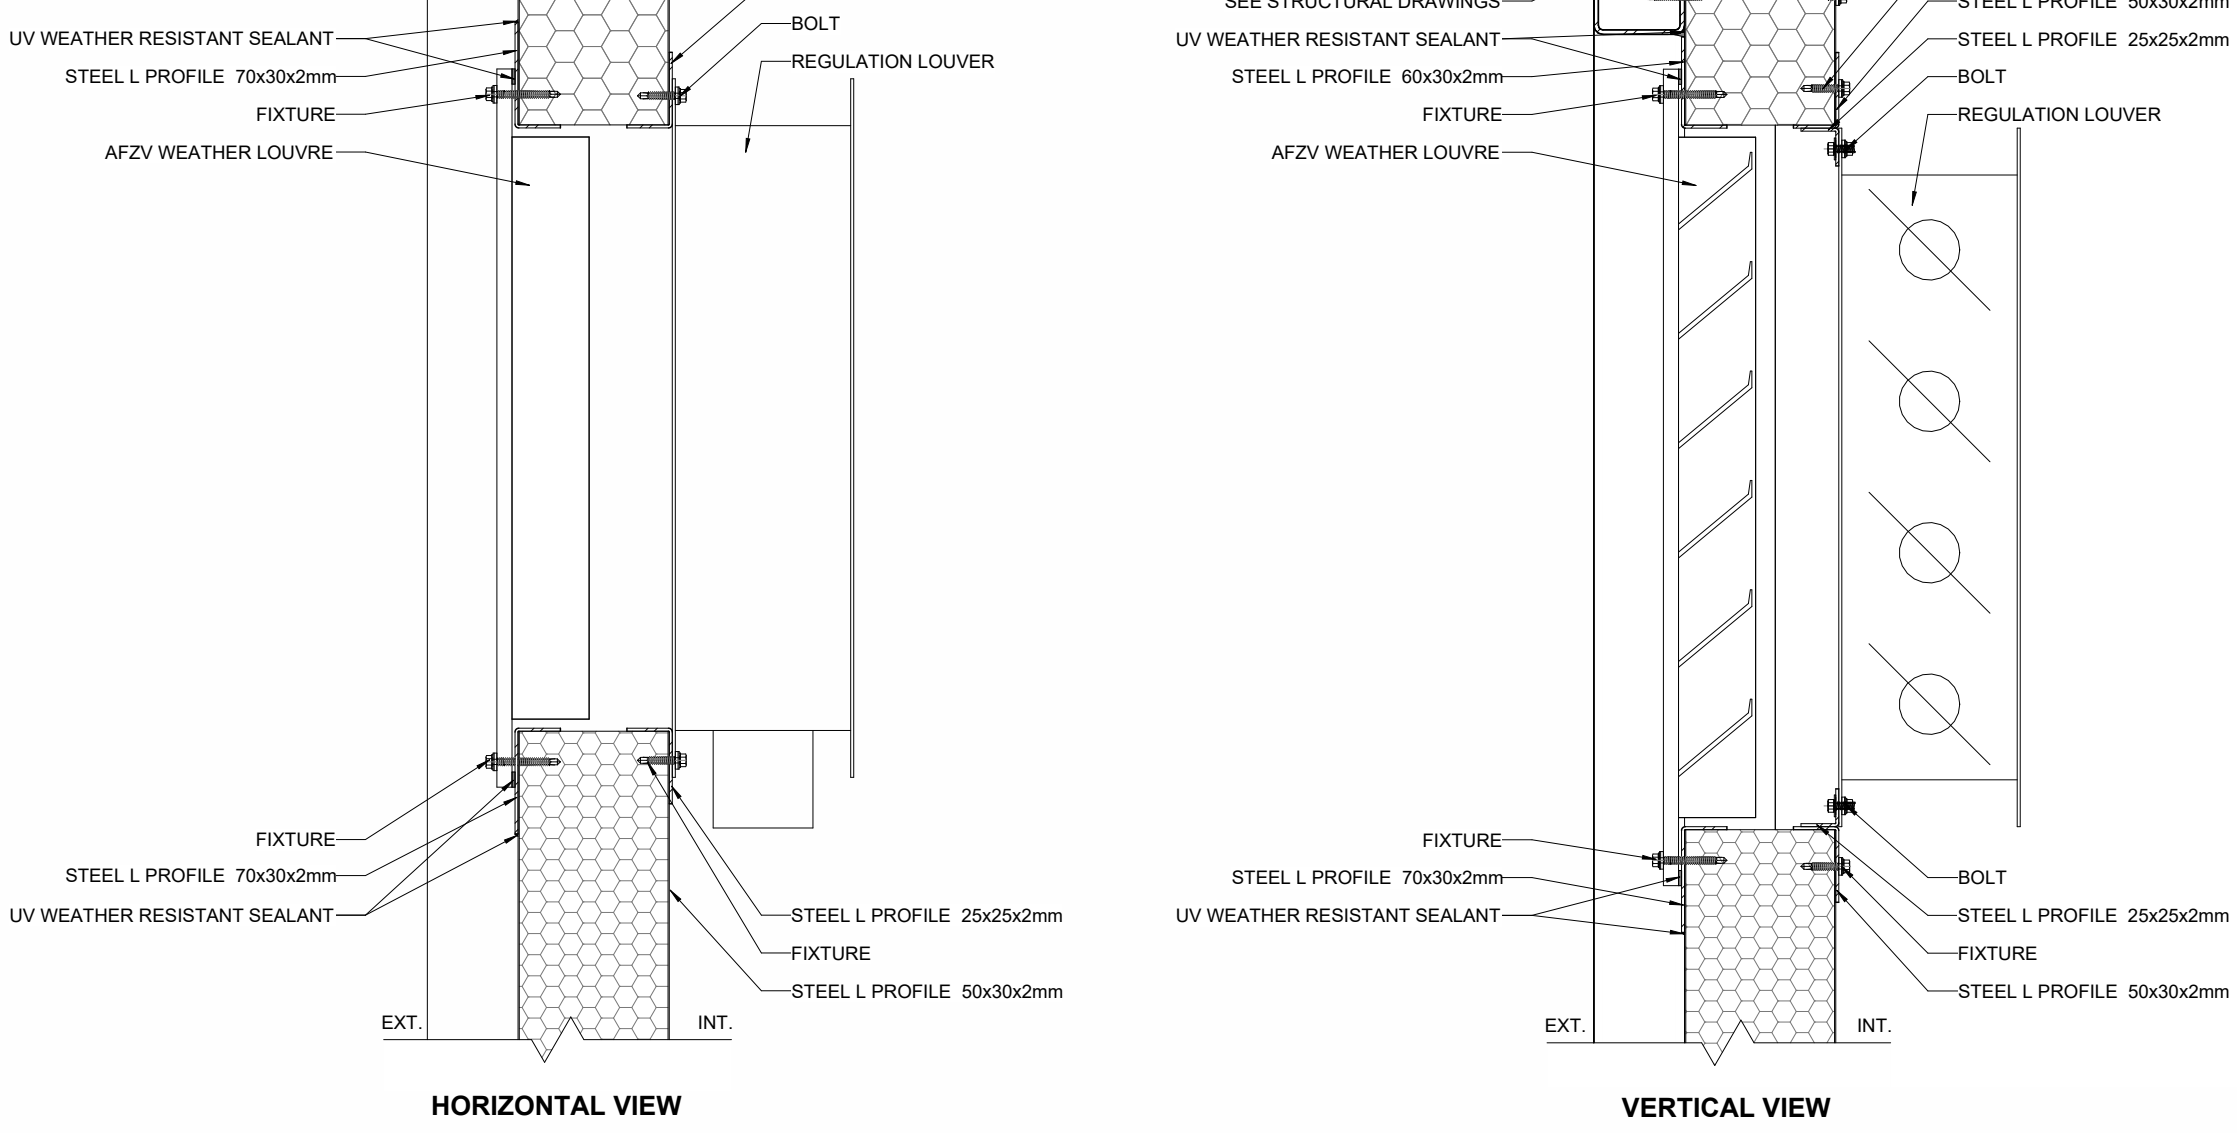


P11 AFZV WEATHER LOUVRE + REGULATION LOUVRE
1:5

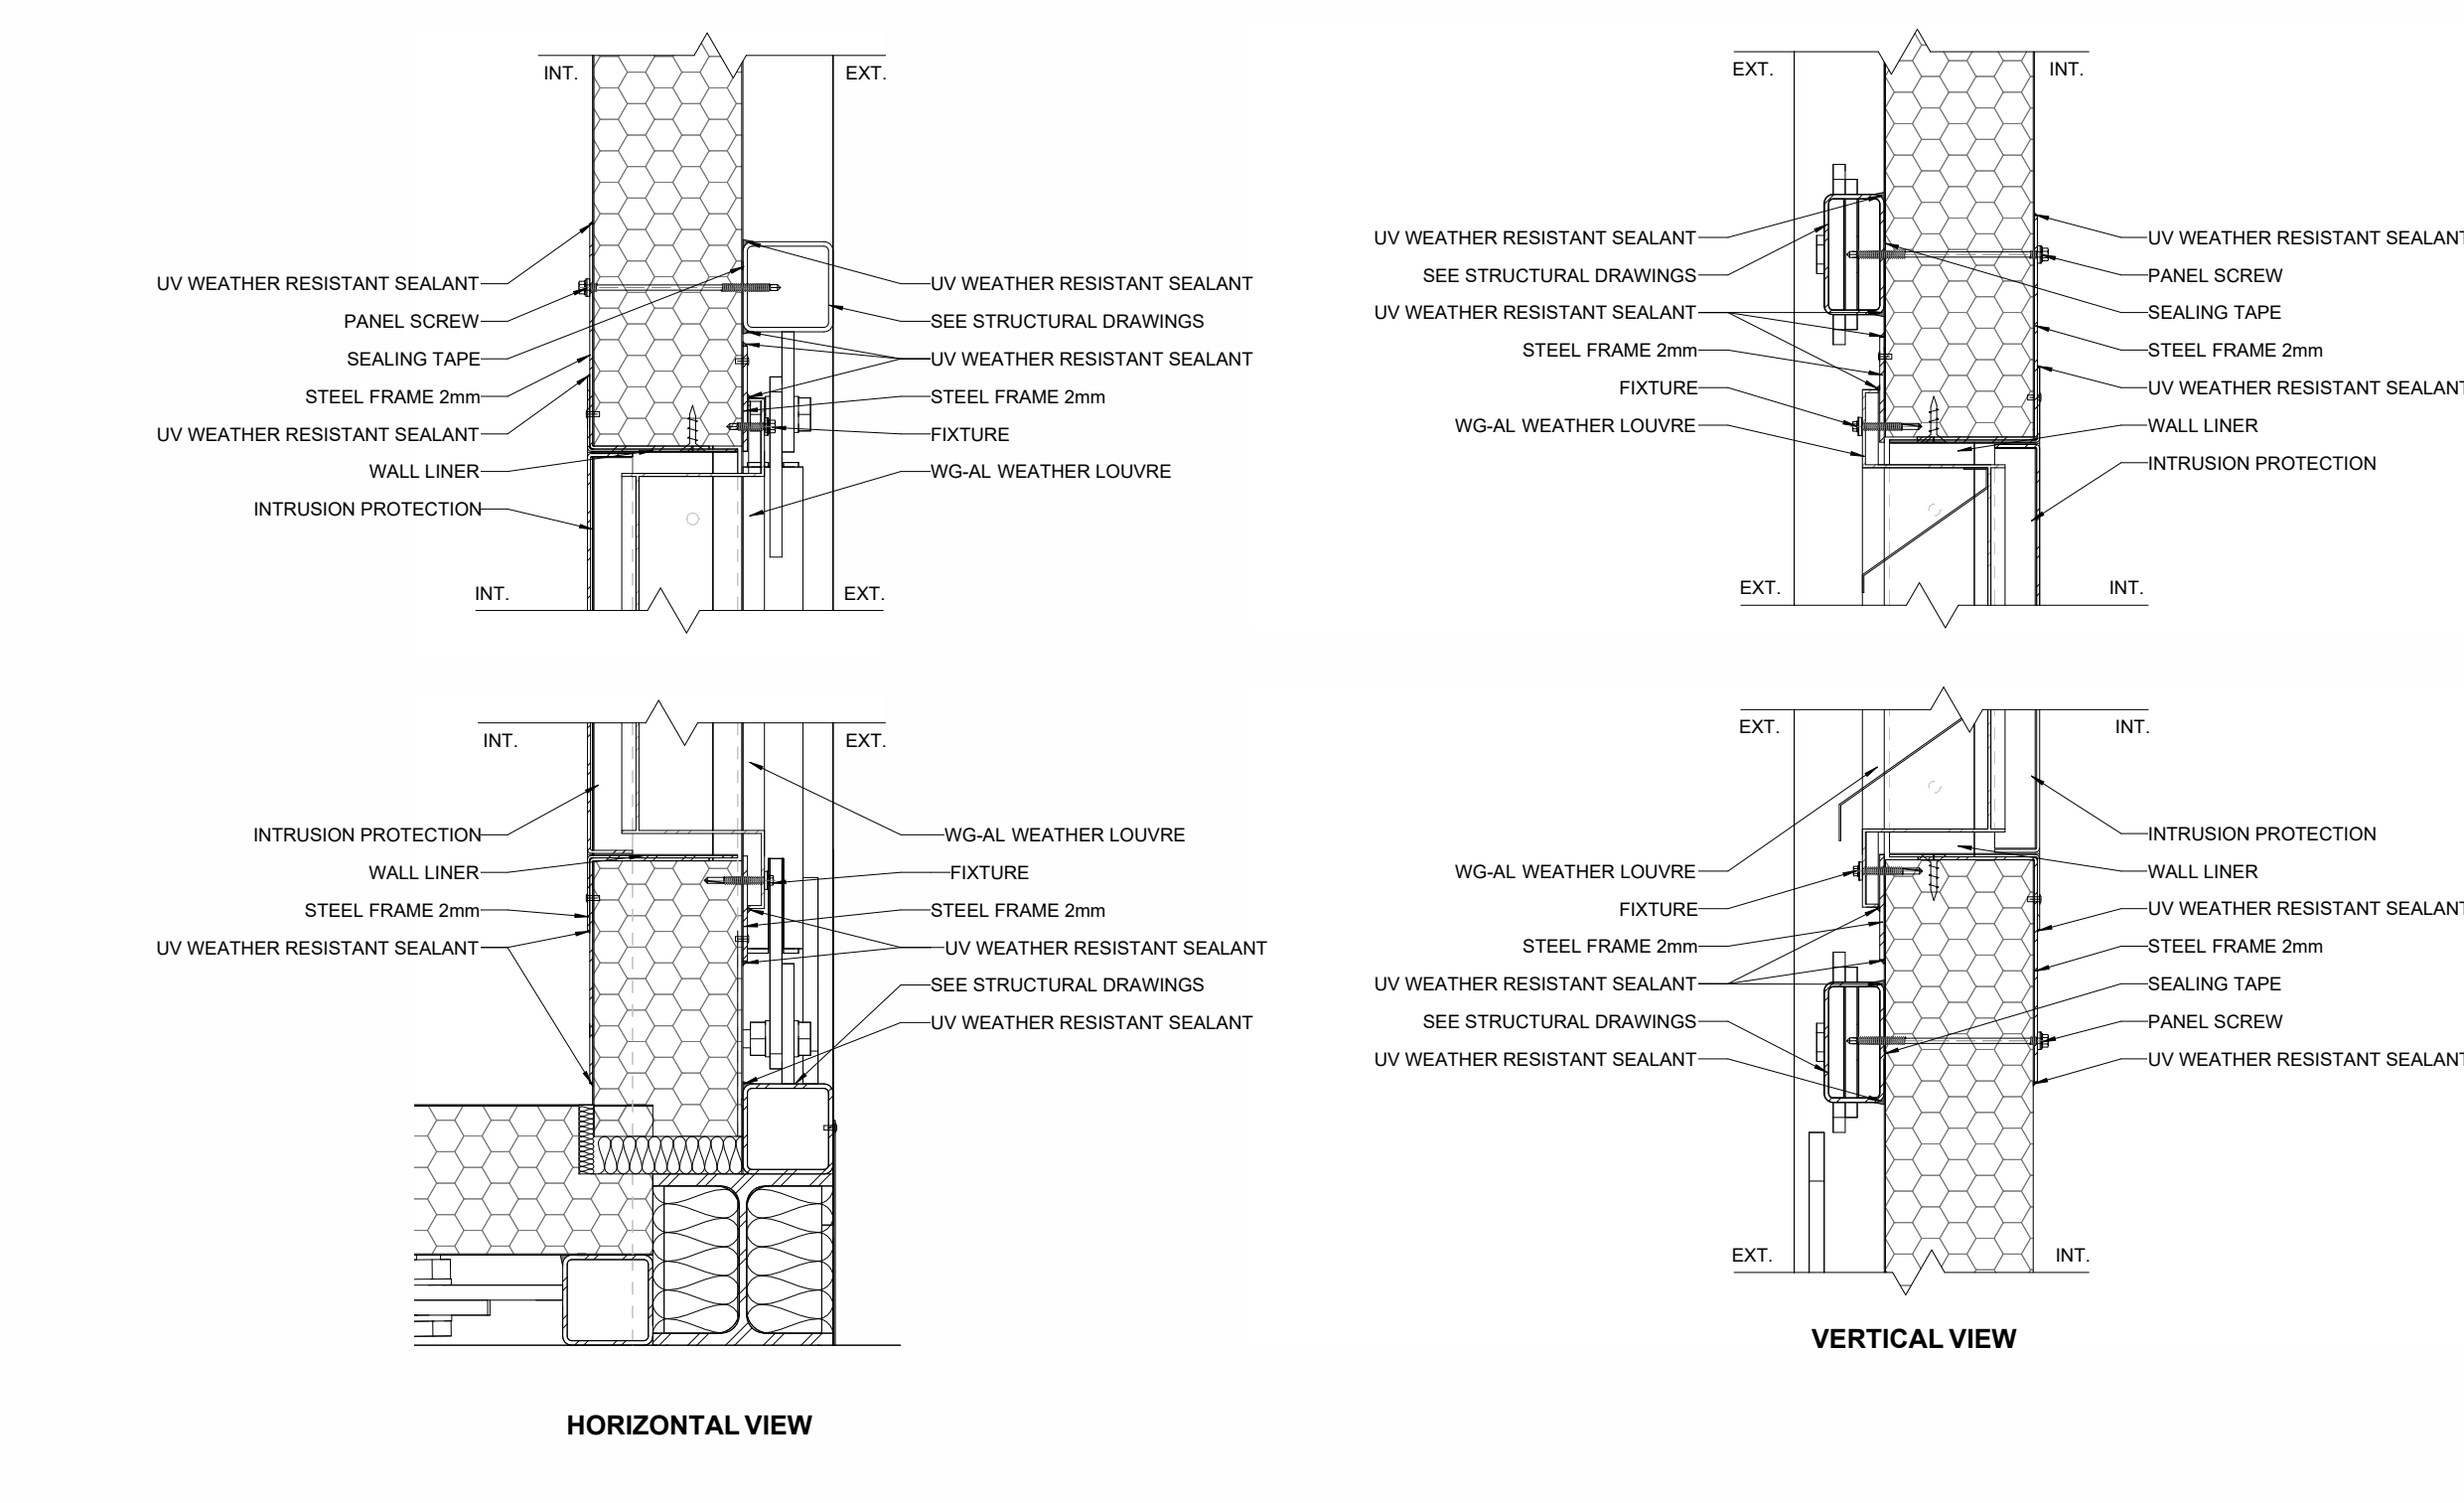


P11b WG-AL WEATHER LOUVRE
1:5

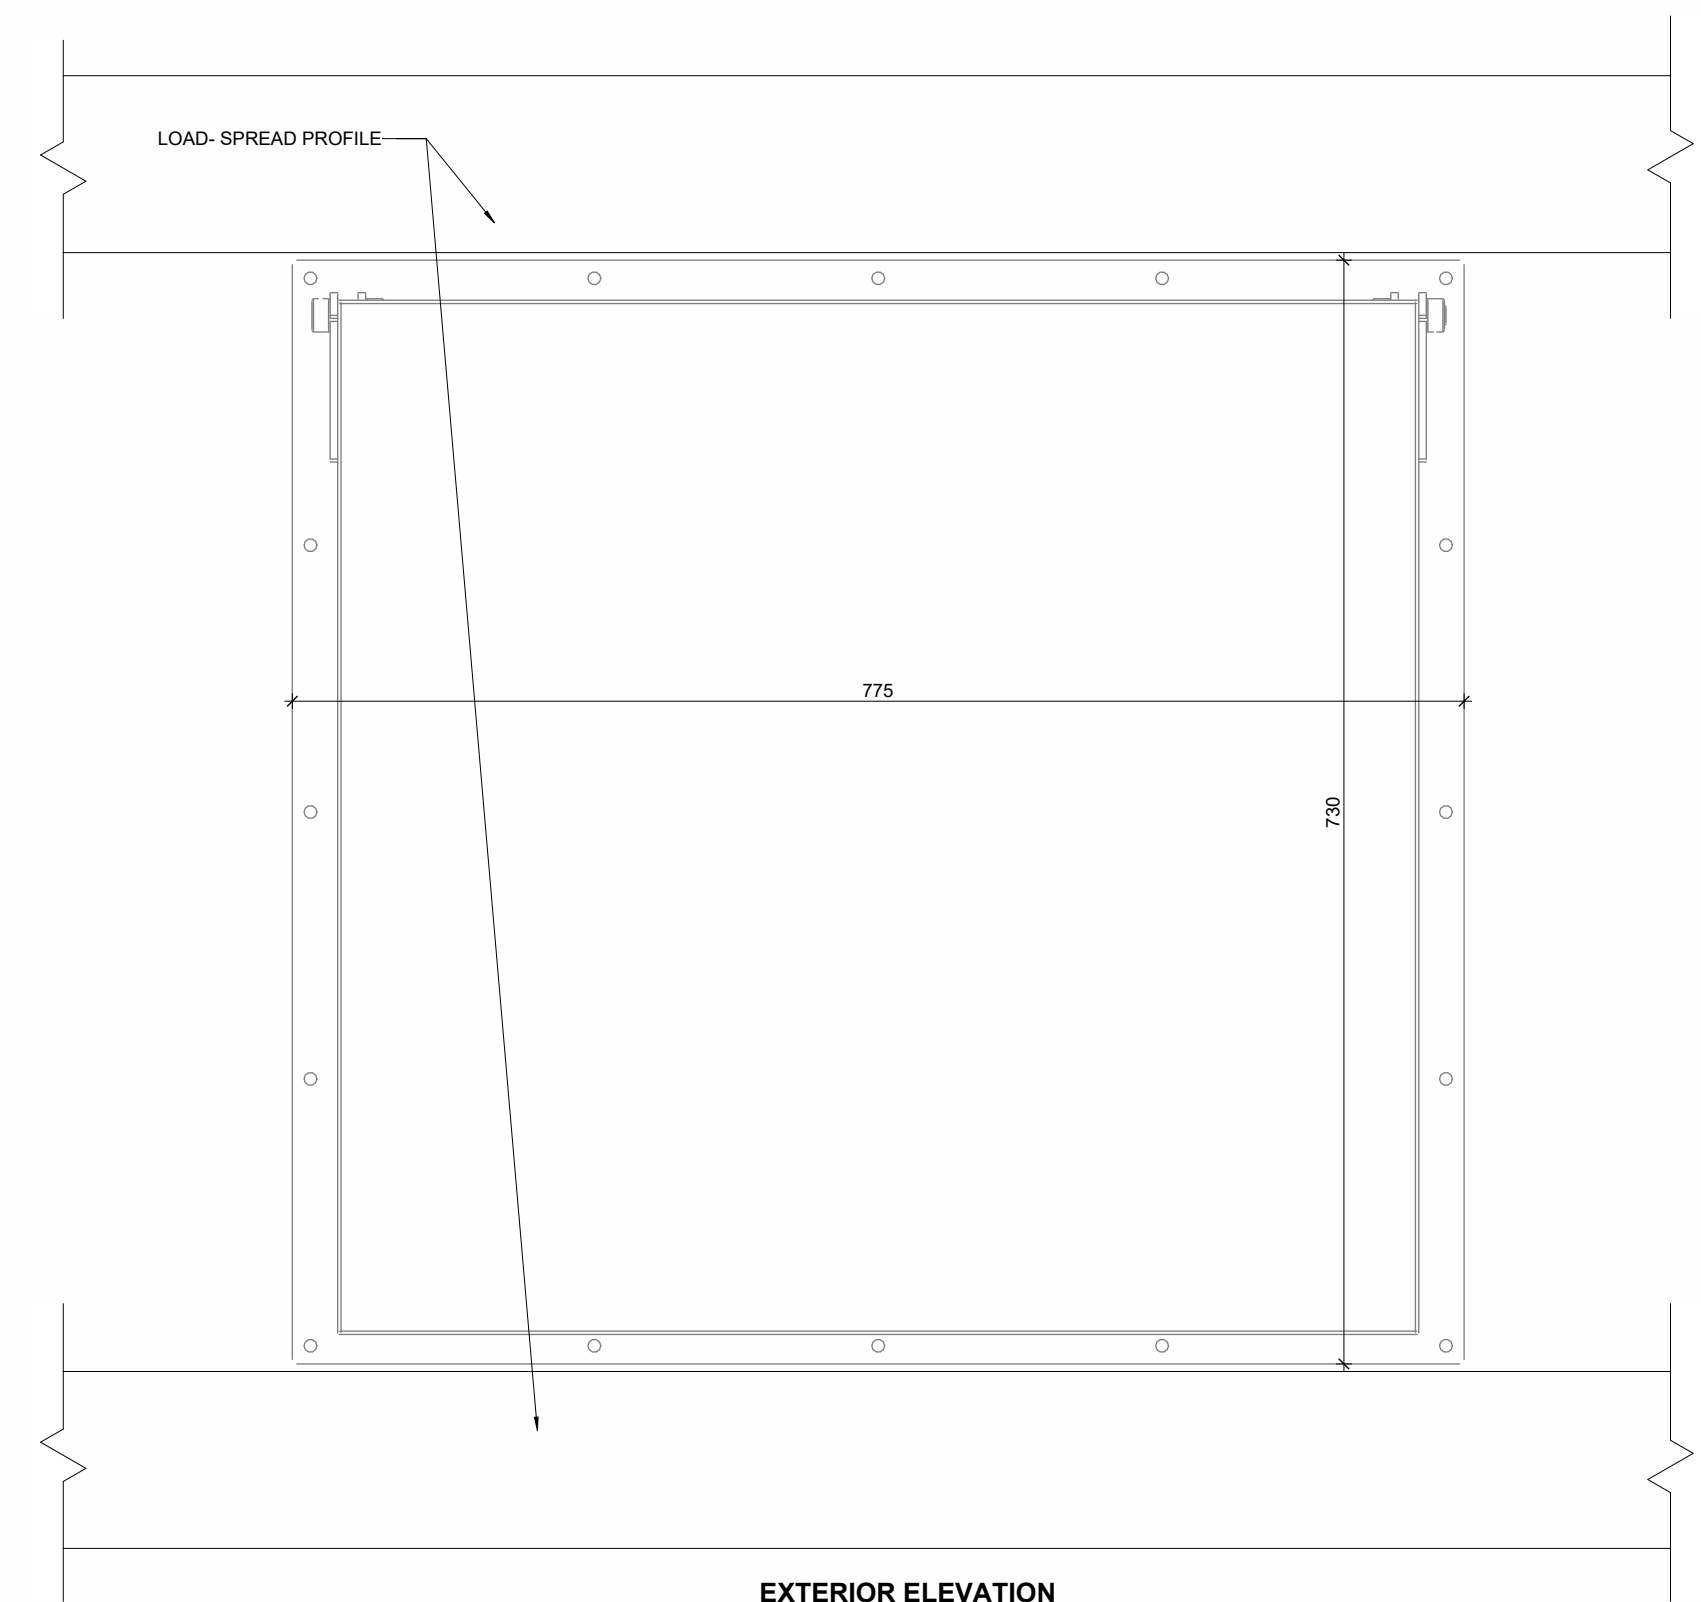


EXTERIOR ELEVATION

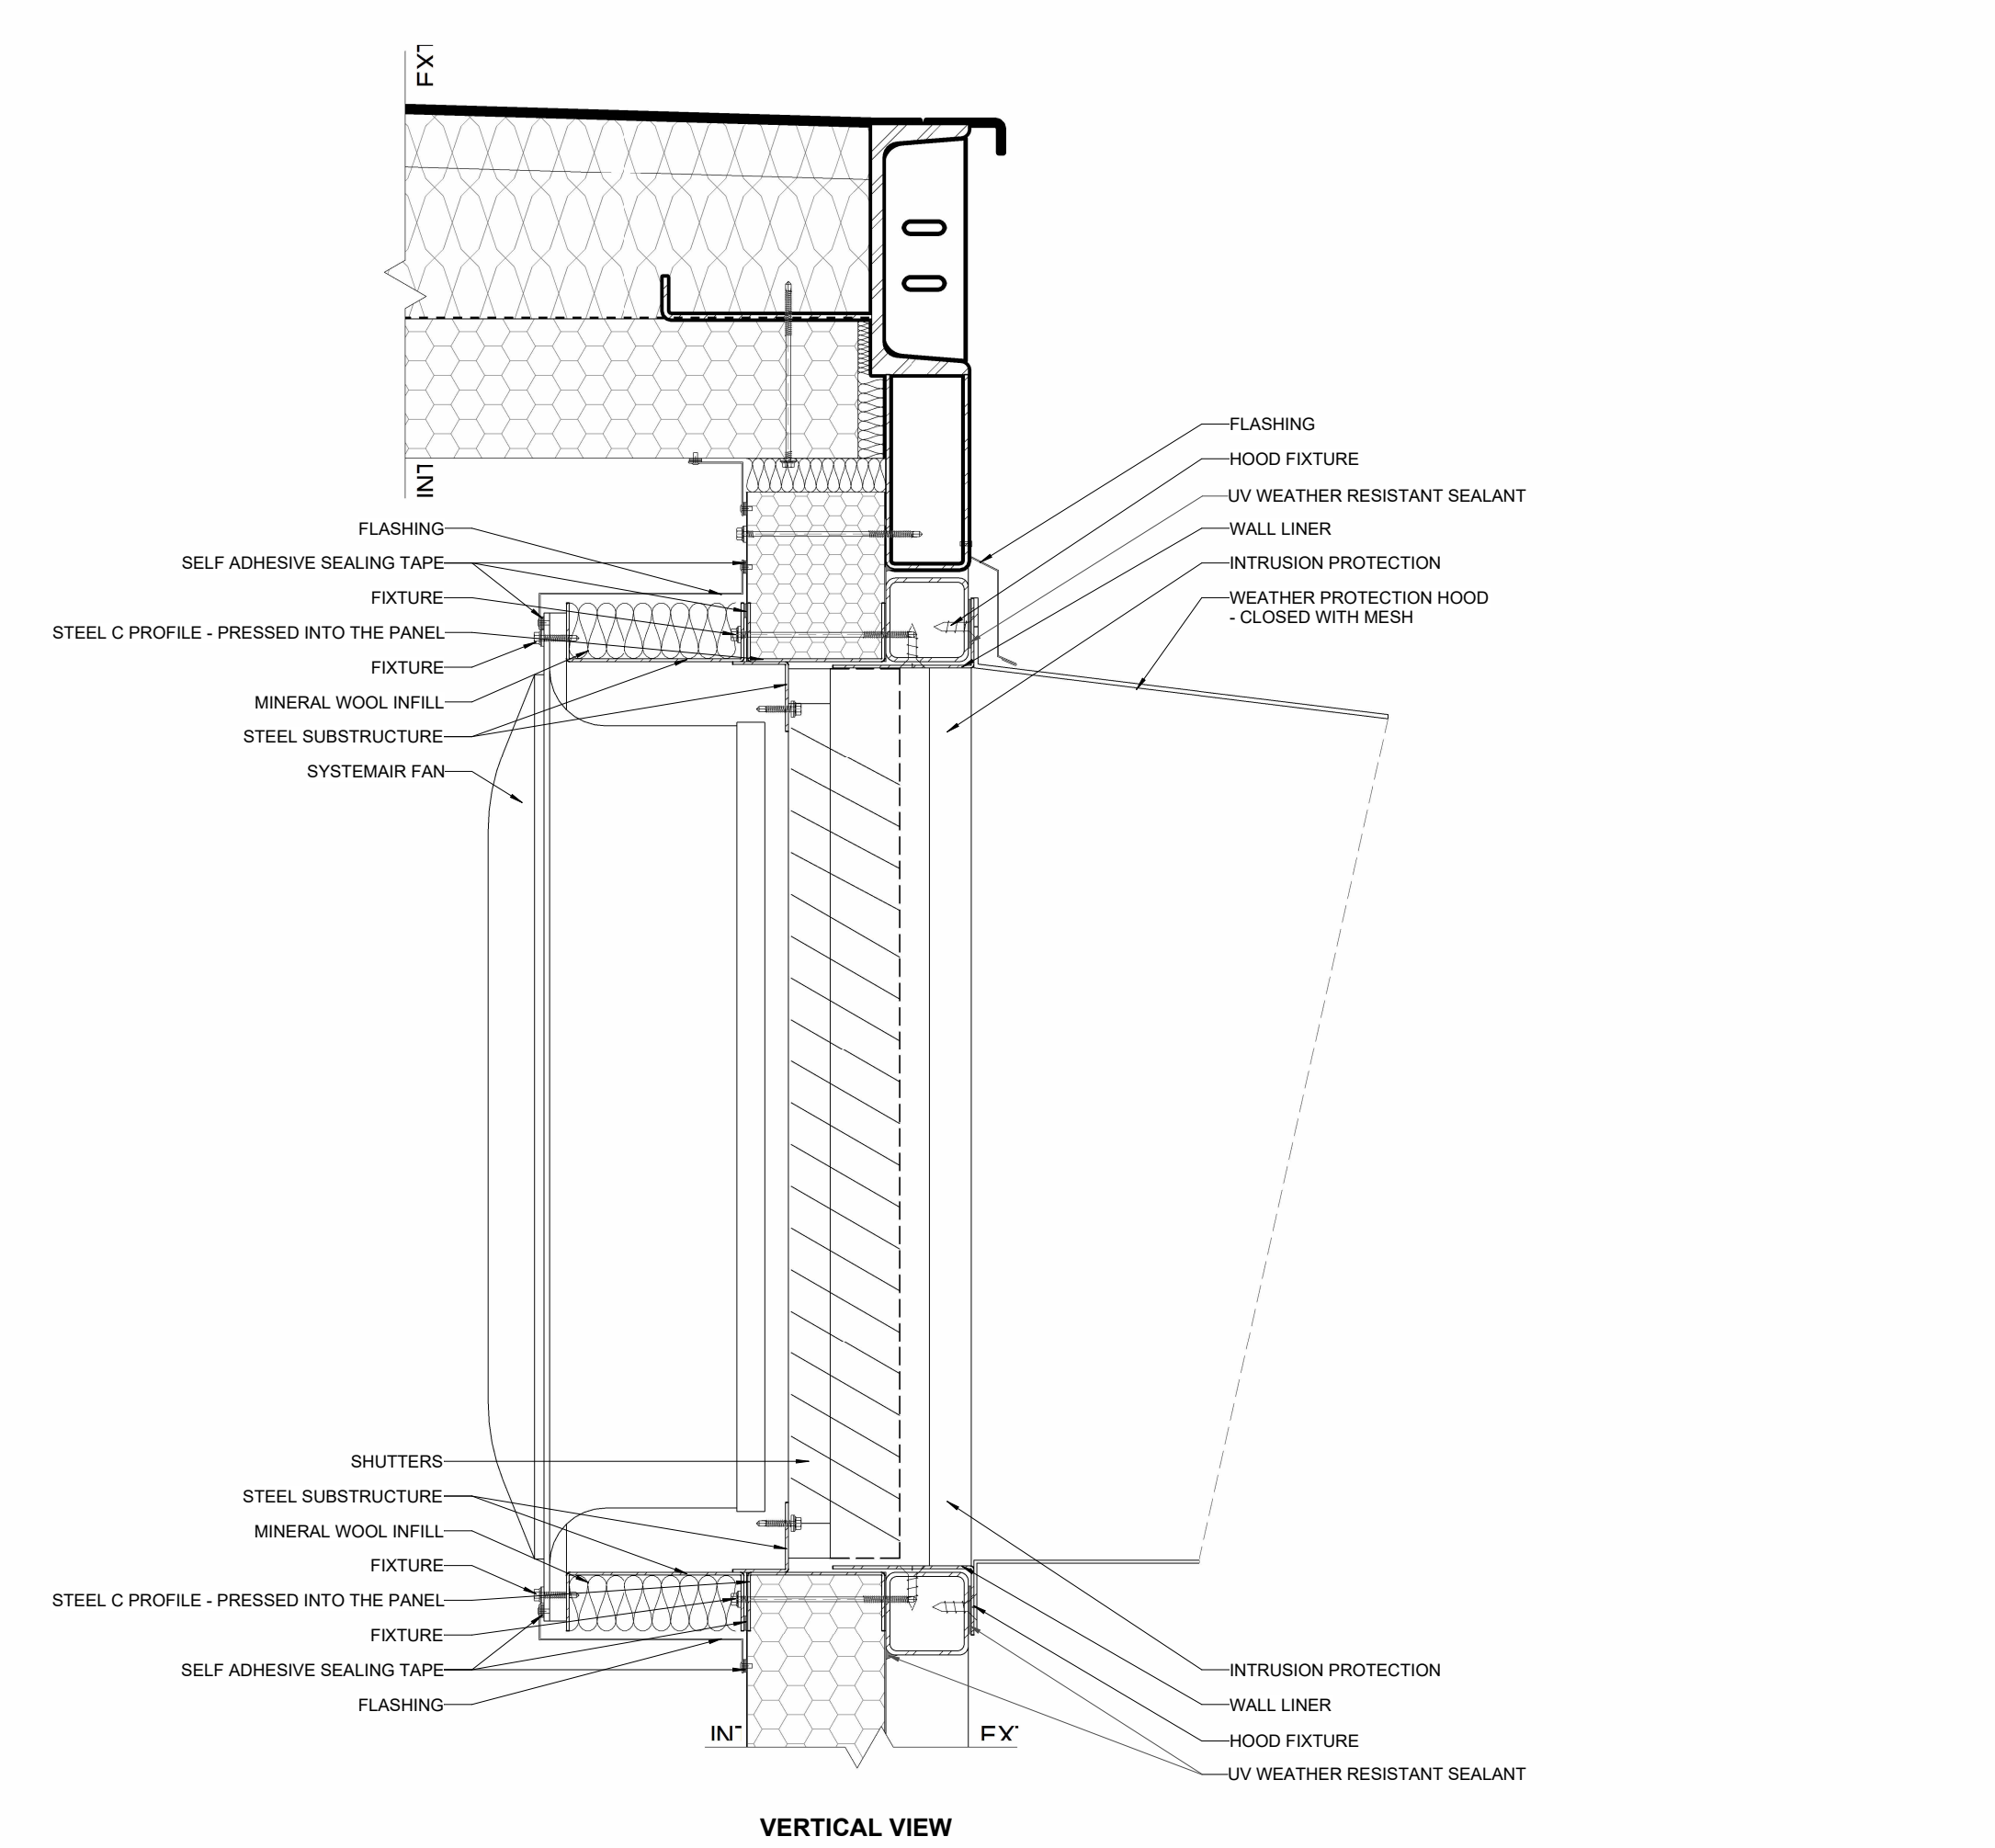


P12 SYSTEMAIR FAN
1:5

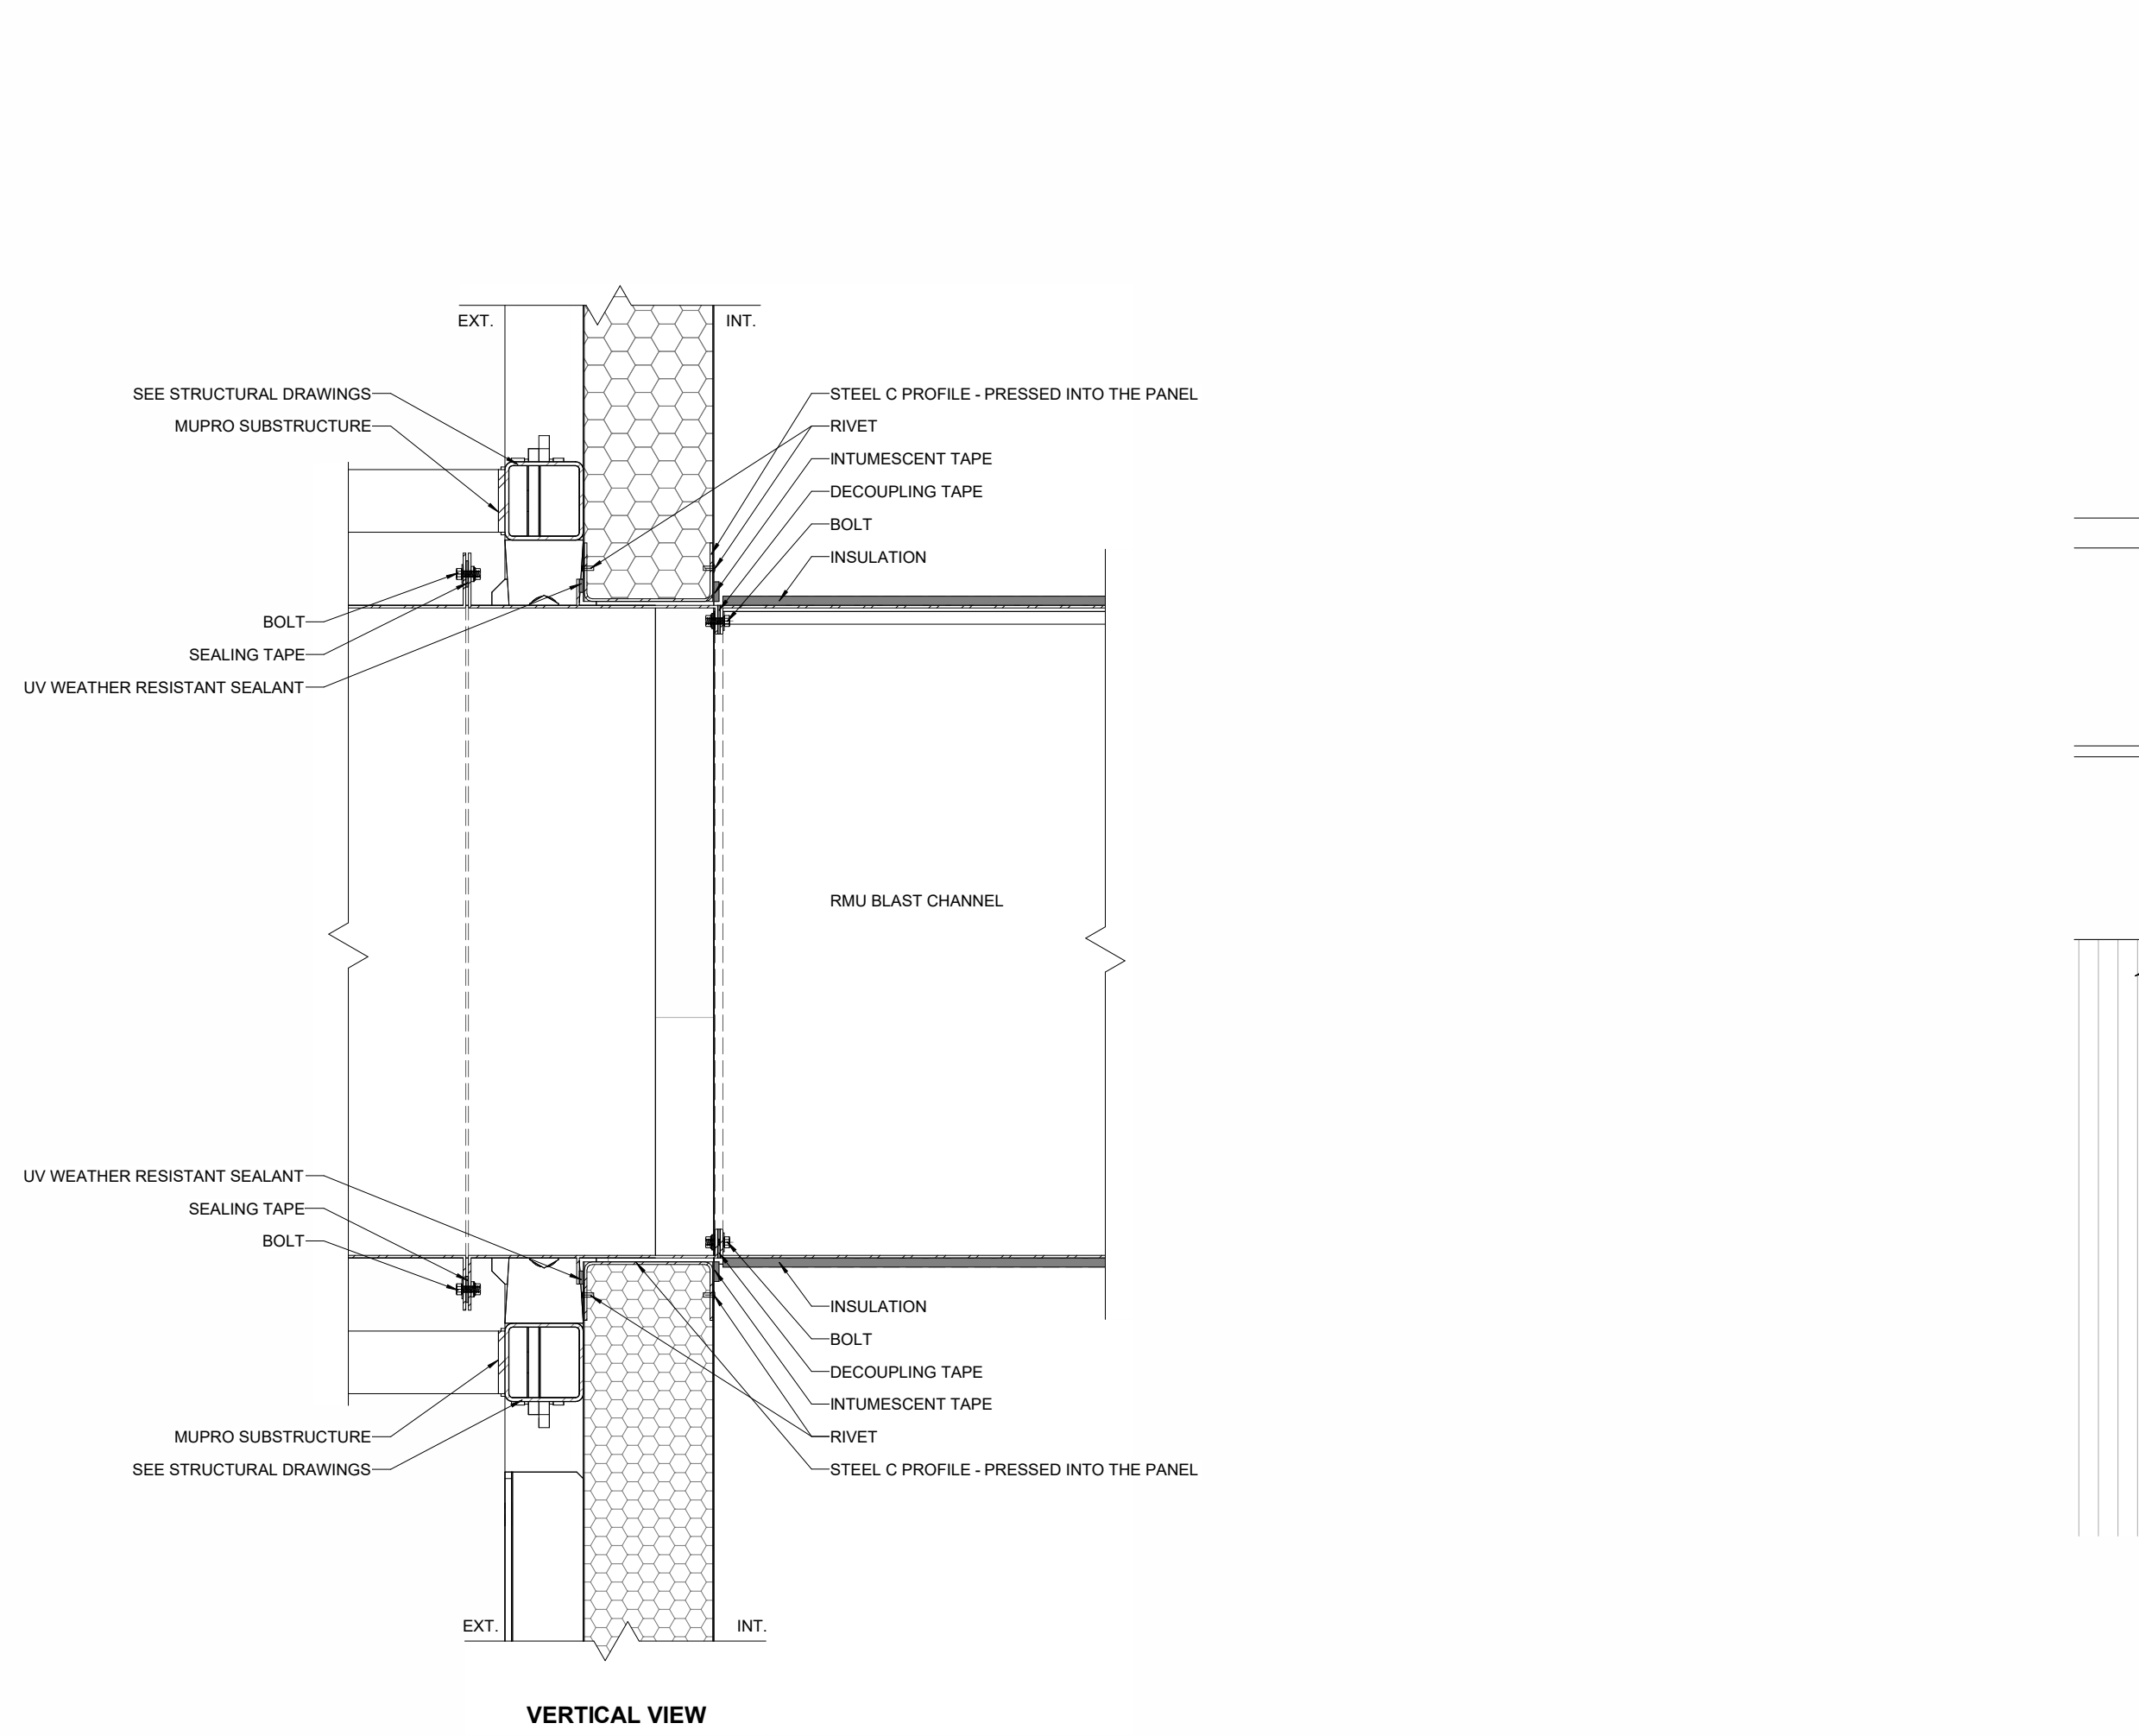


P13 RMU ARC BLAST
1:5

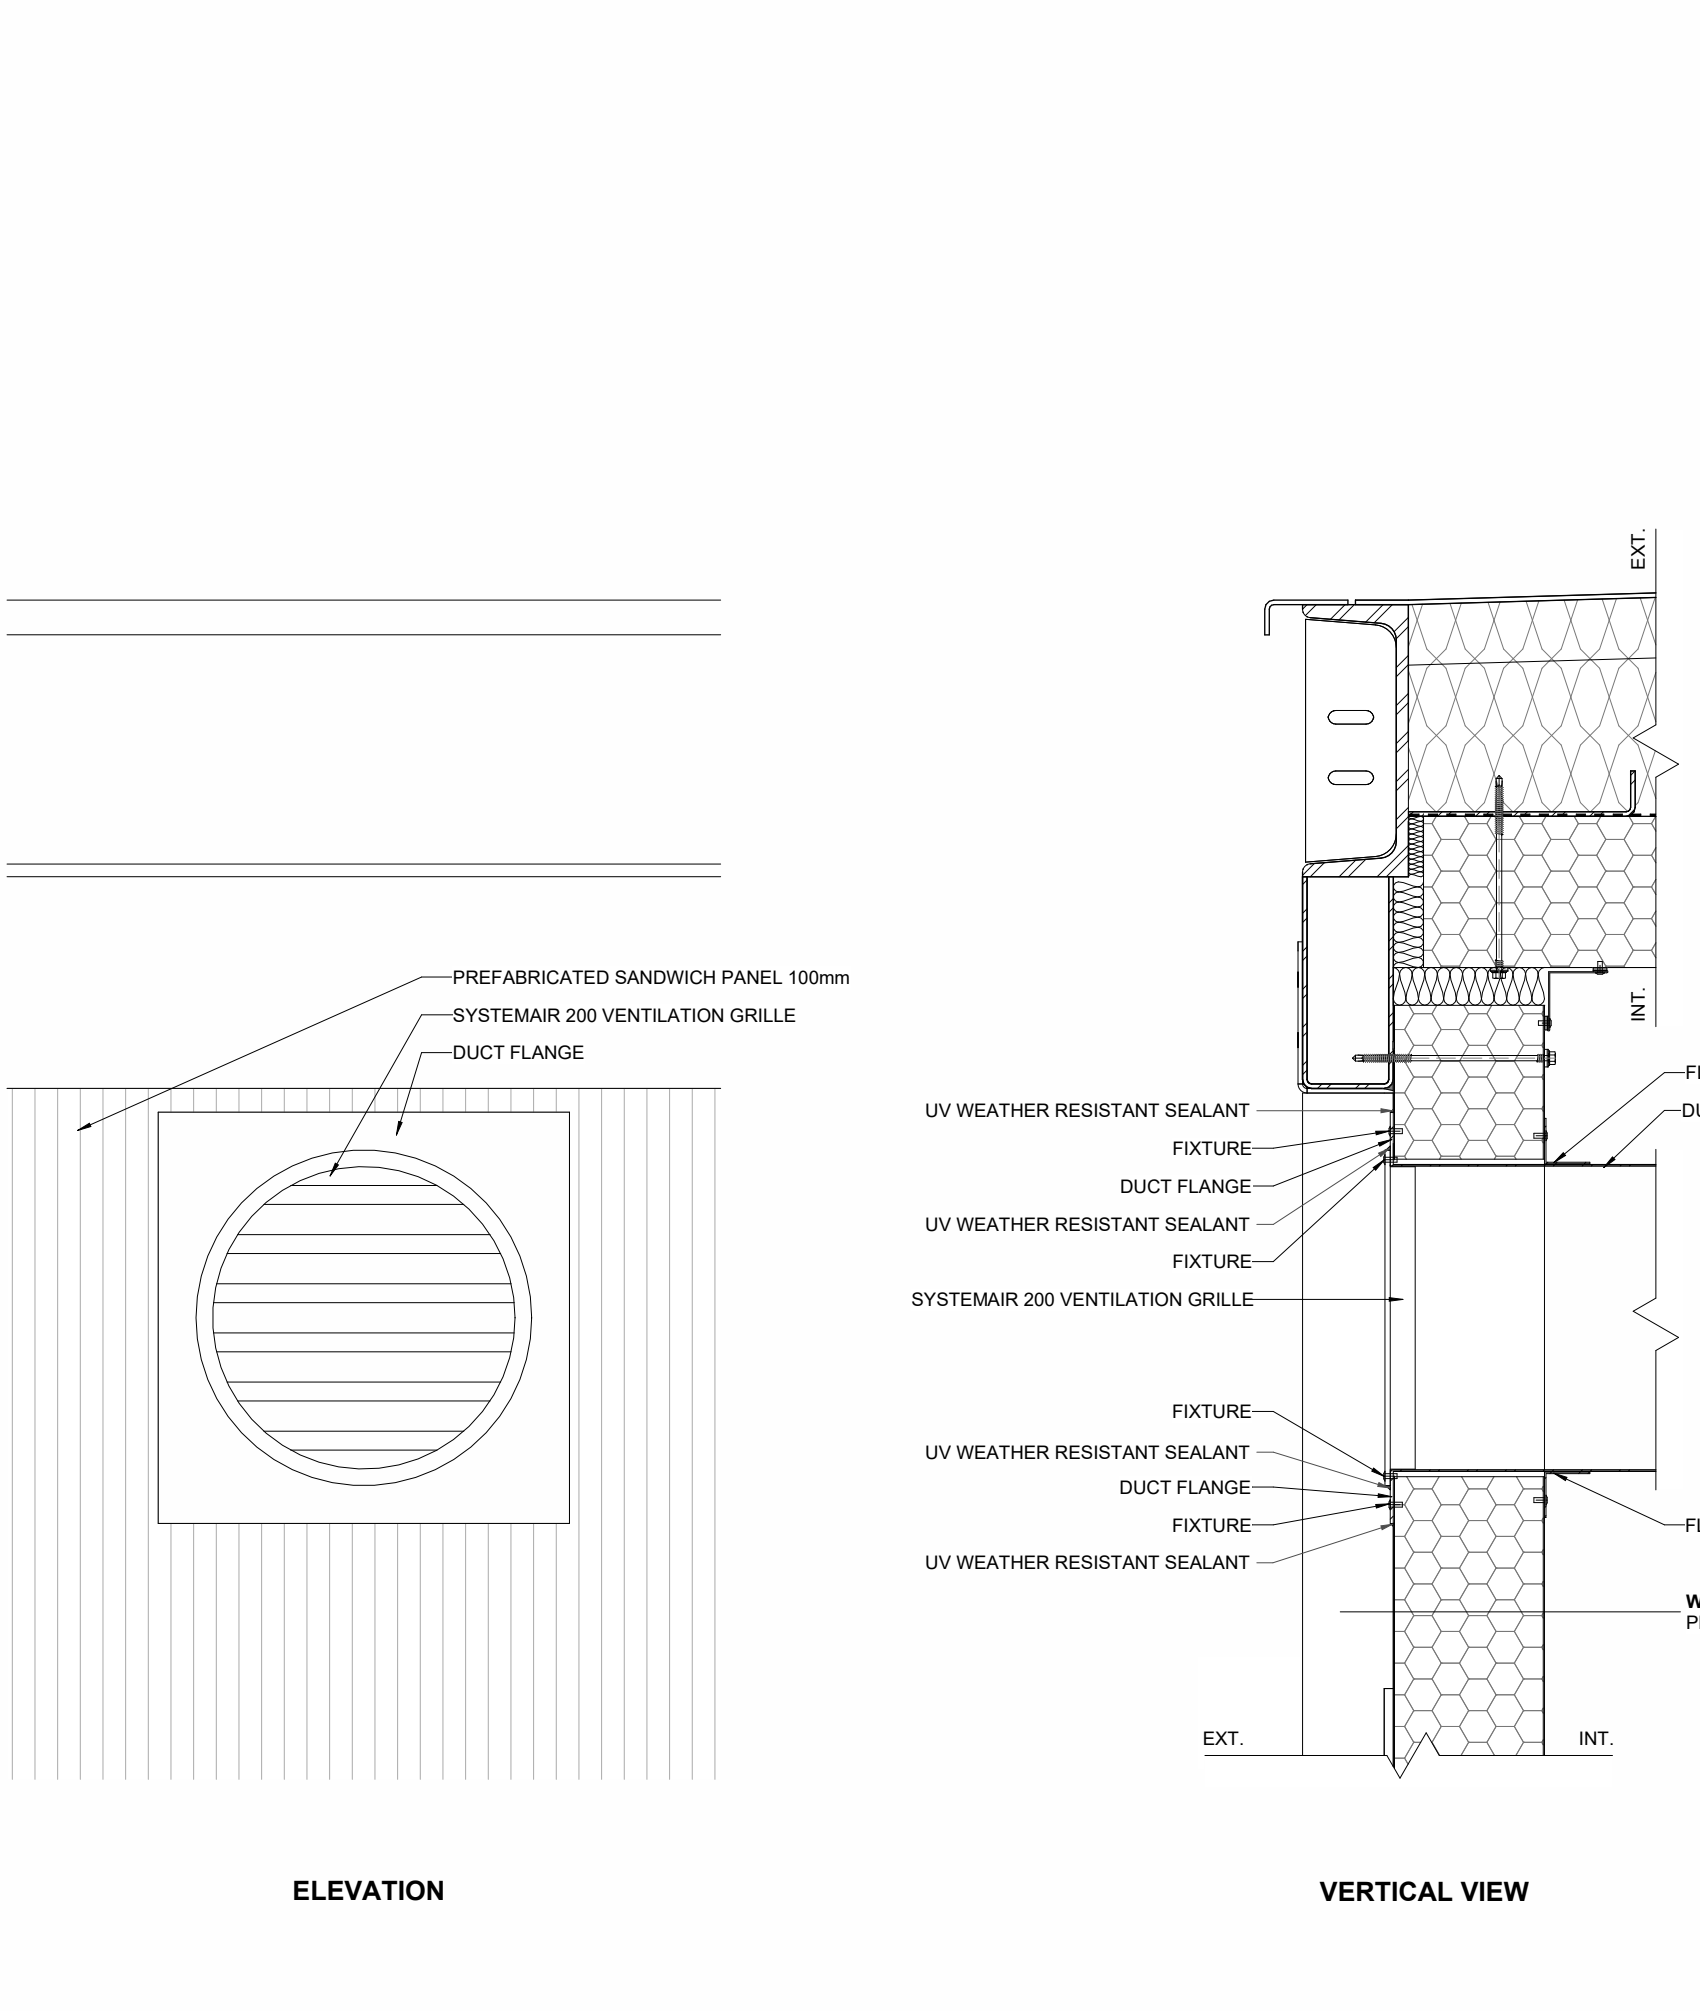


P16 SYSTEMAIR VENTILATION GRILLE
1:5

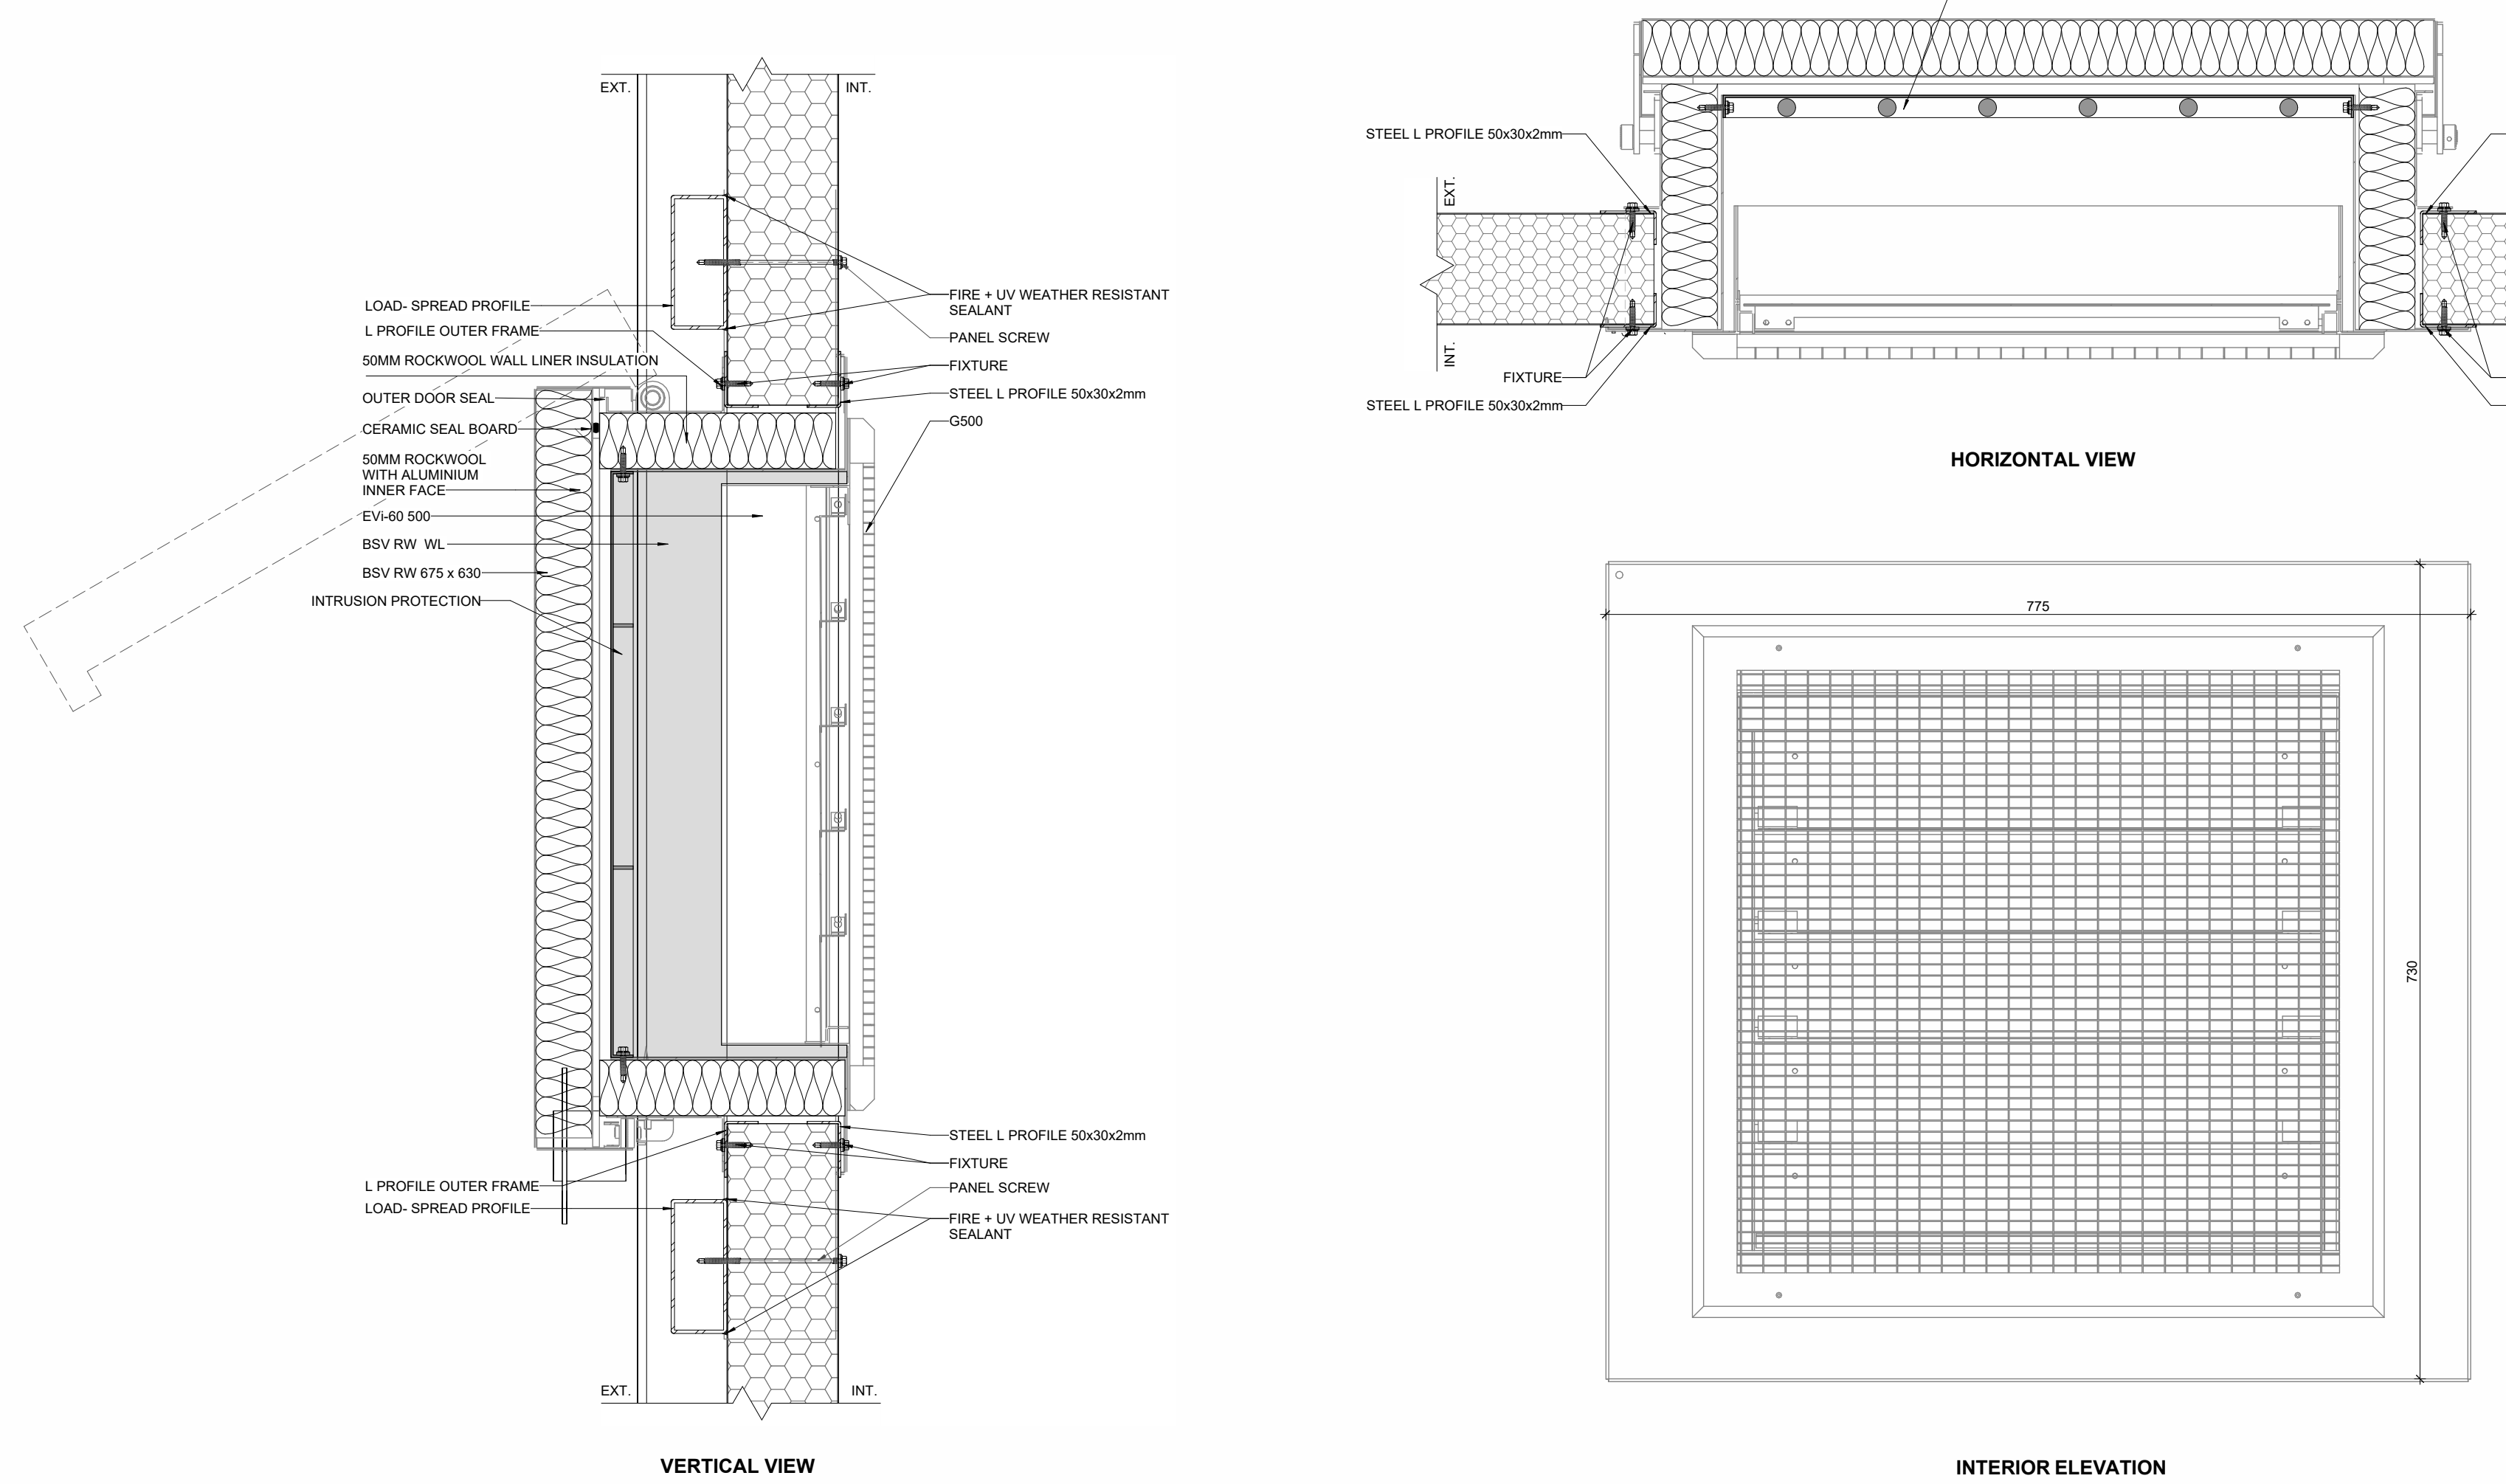

P10b BSV + EVI500 + SGHD
1:5

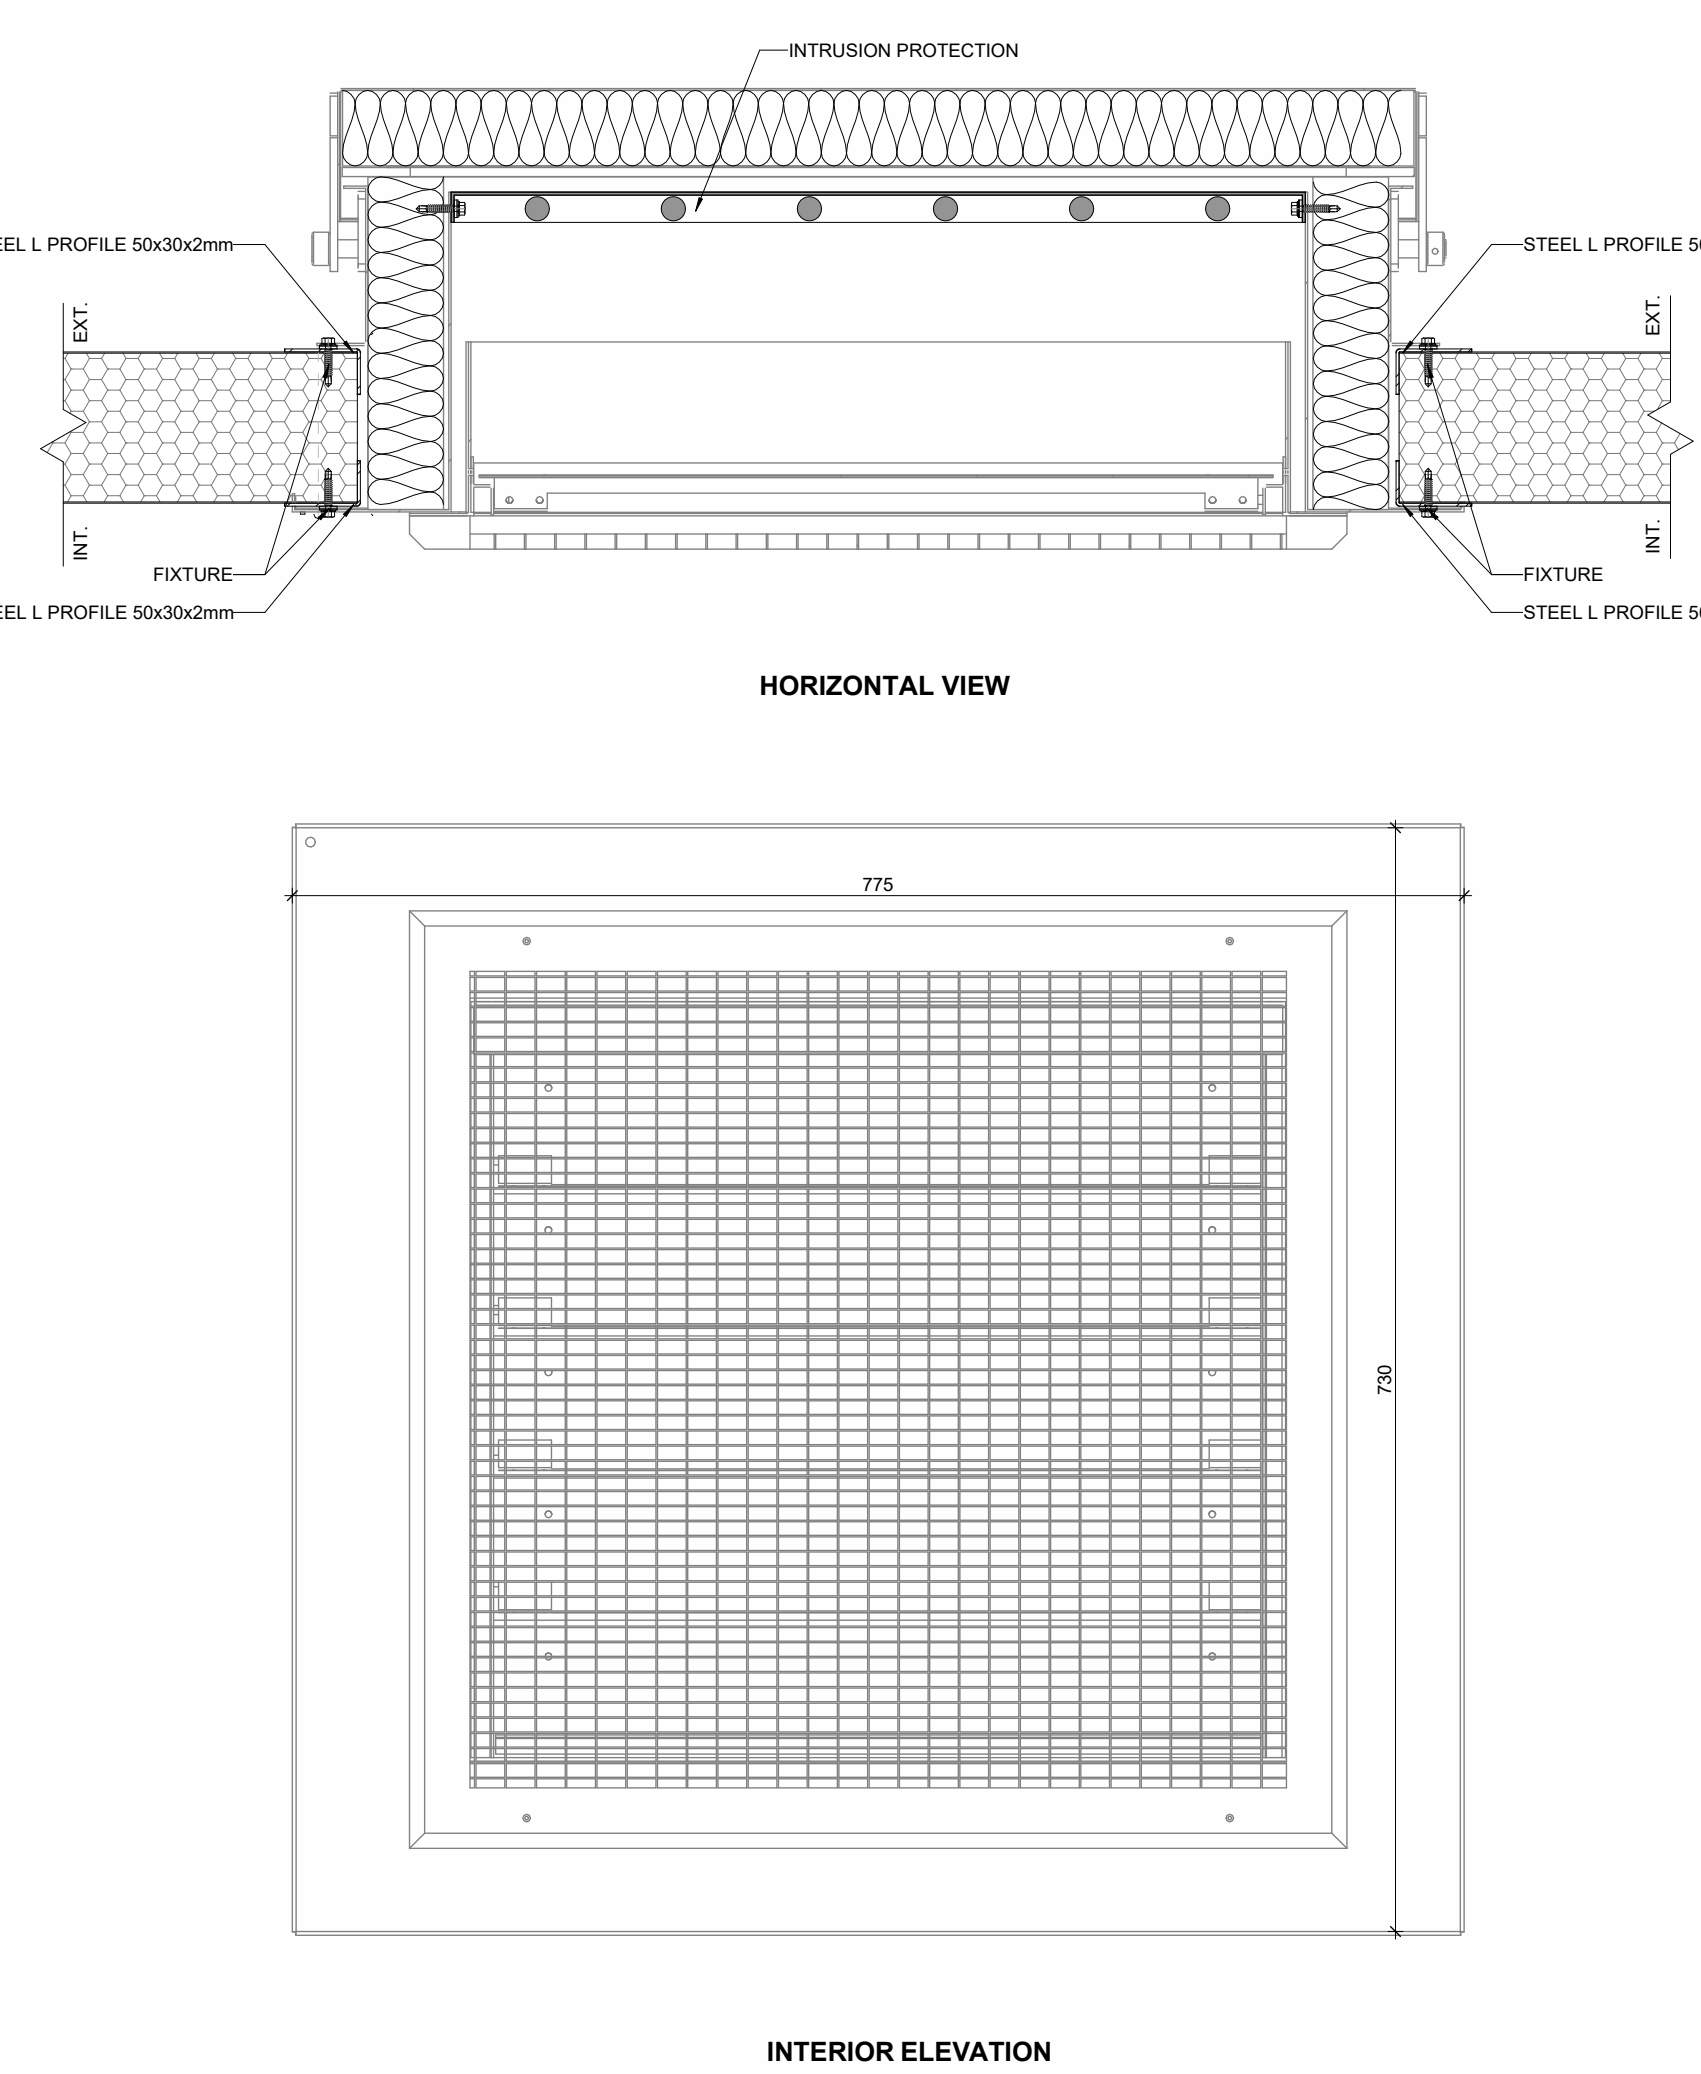

INTERIOR ELEVATION

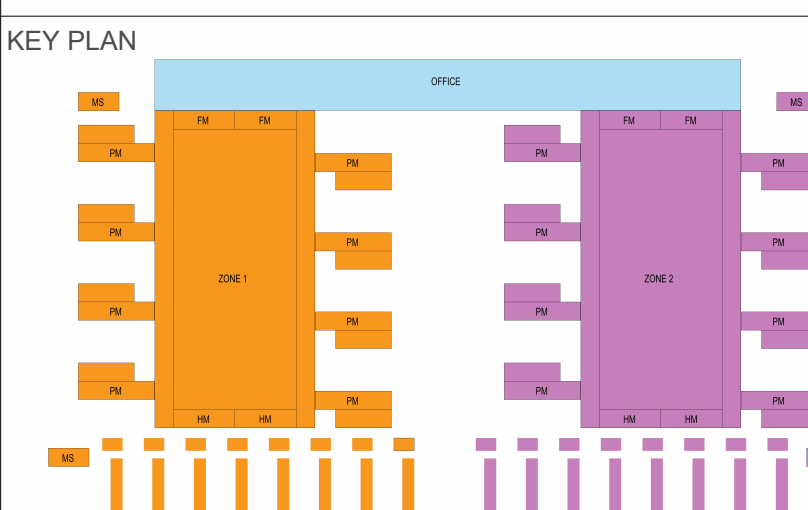

REV.	DESCRIPTION	DATE
R02	CD SET - FOR INFORMATION 2026-09-11	
R01	CD SET - FOR INFORMATION 2026-07-24	



PROJECT NAME	ECO DC MONALISA
DRAWING NAME	ARCHITECTURAL DETAILS - PREFABRICATED MODULES - PENETRATIONS EXTERNAL - PM - MV - MS
PREPARED (ALSO SUBJECT TO APPROVAL BY OTHERS)	L. MAUREK / K. KOZINA
DRAWING NUMBER	M. PACAK
DATE	2026-09-11
SCALE	1:5
PROJECT NUMBER	ECODC-VRT-MDC19-00-DR-A-50105
PROJECT NAME	ECO DC MONALISA
PROJECT NUMBER	ECODC-VRT-MDC19-00-DR-A-50105
PROJECT NAME	ECO DC MONALISA
PROJECT NUMBER	ECODC-VRT-MDC19-00-DR-A-50105