




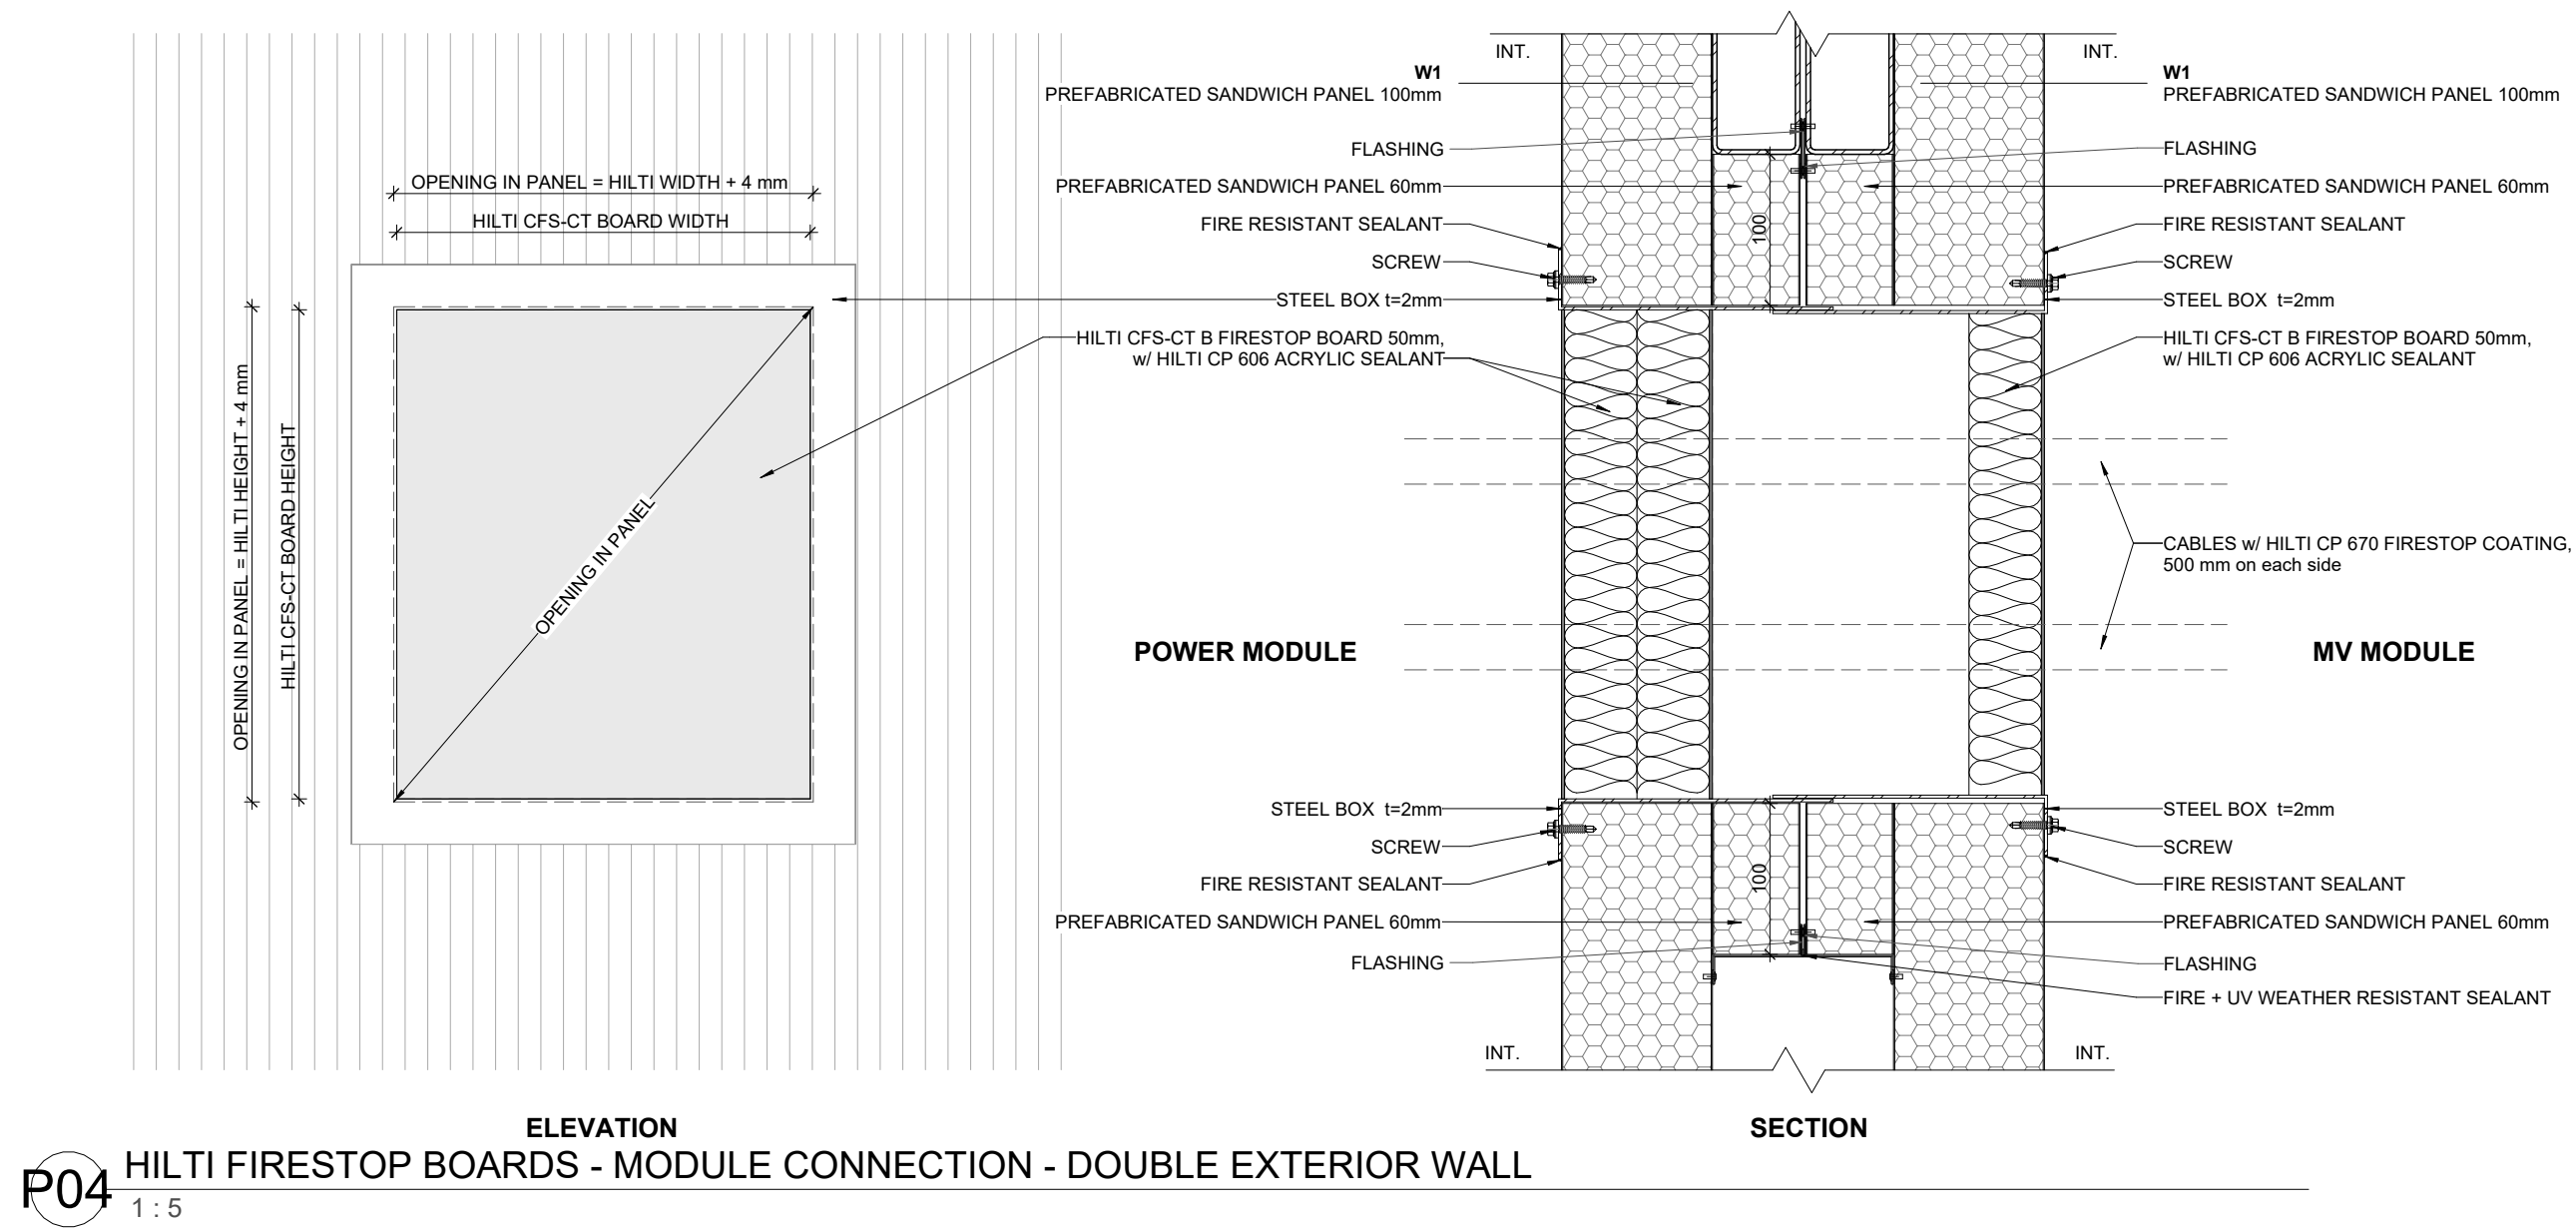


P04 HILTI FIRESTOP BOARDS - MODULE CONNECTION - DOUBLE EXTERIOR WALL
1:5

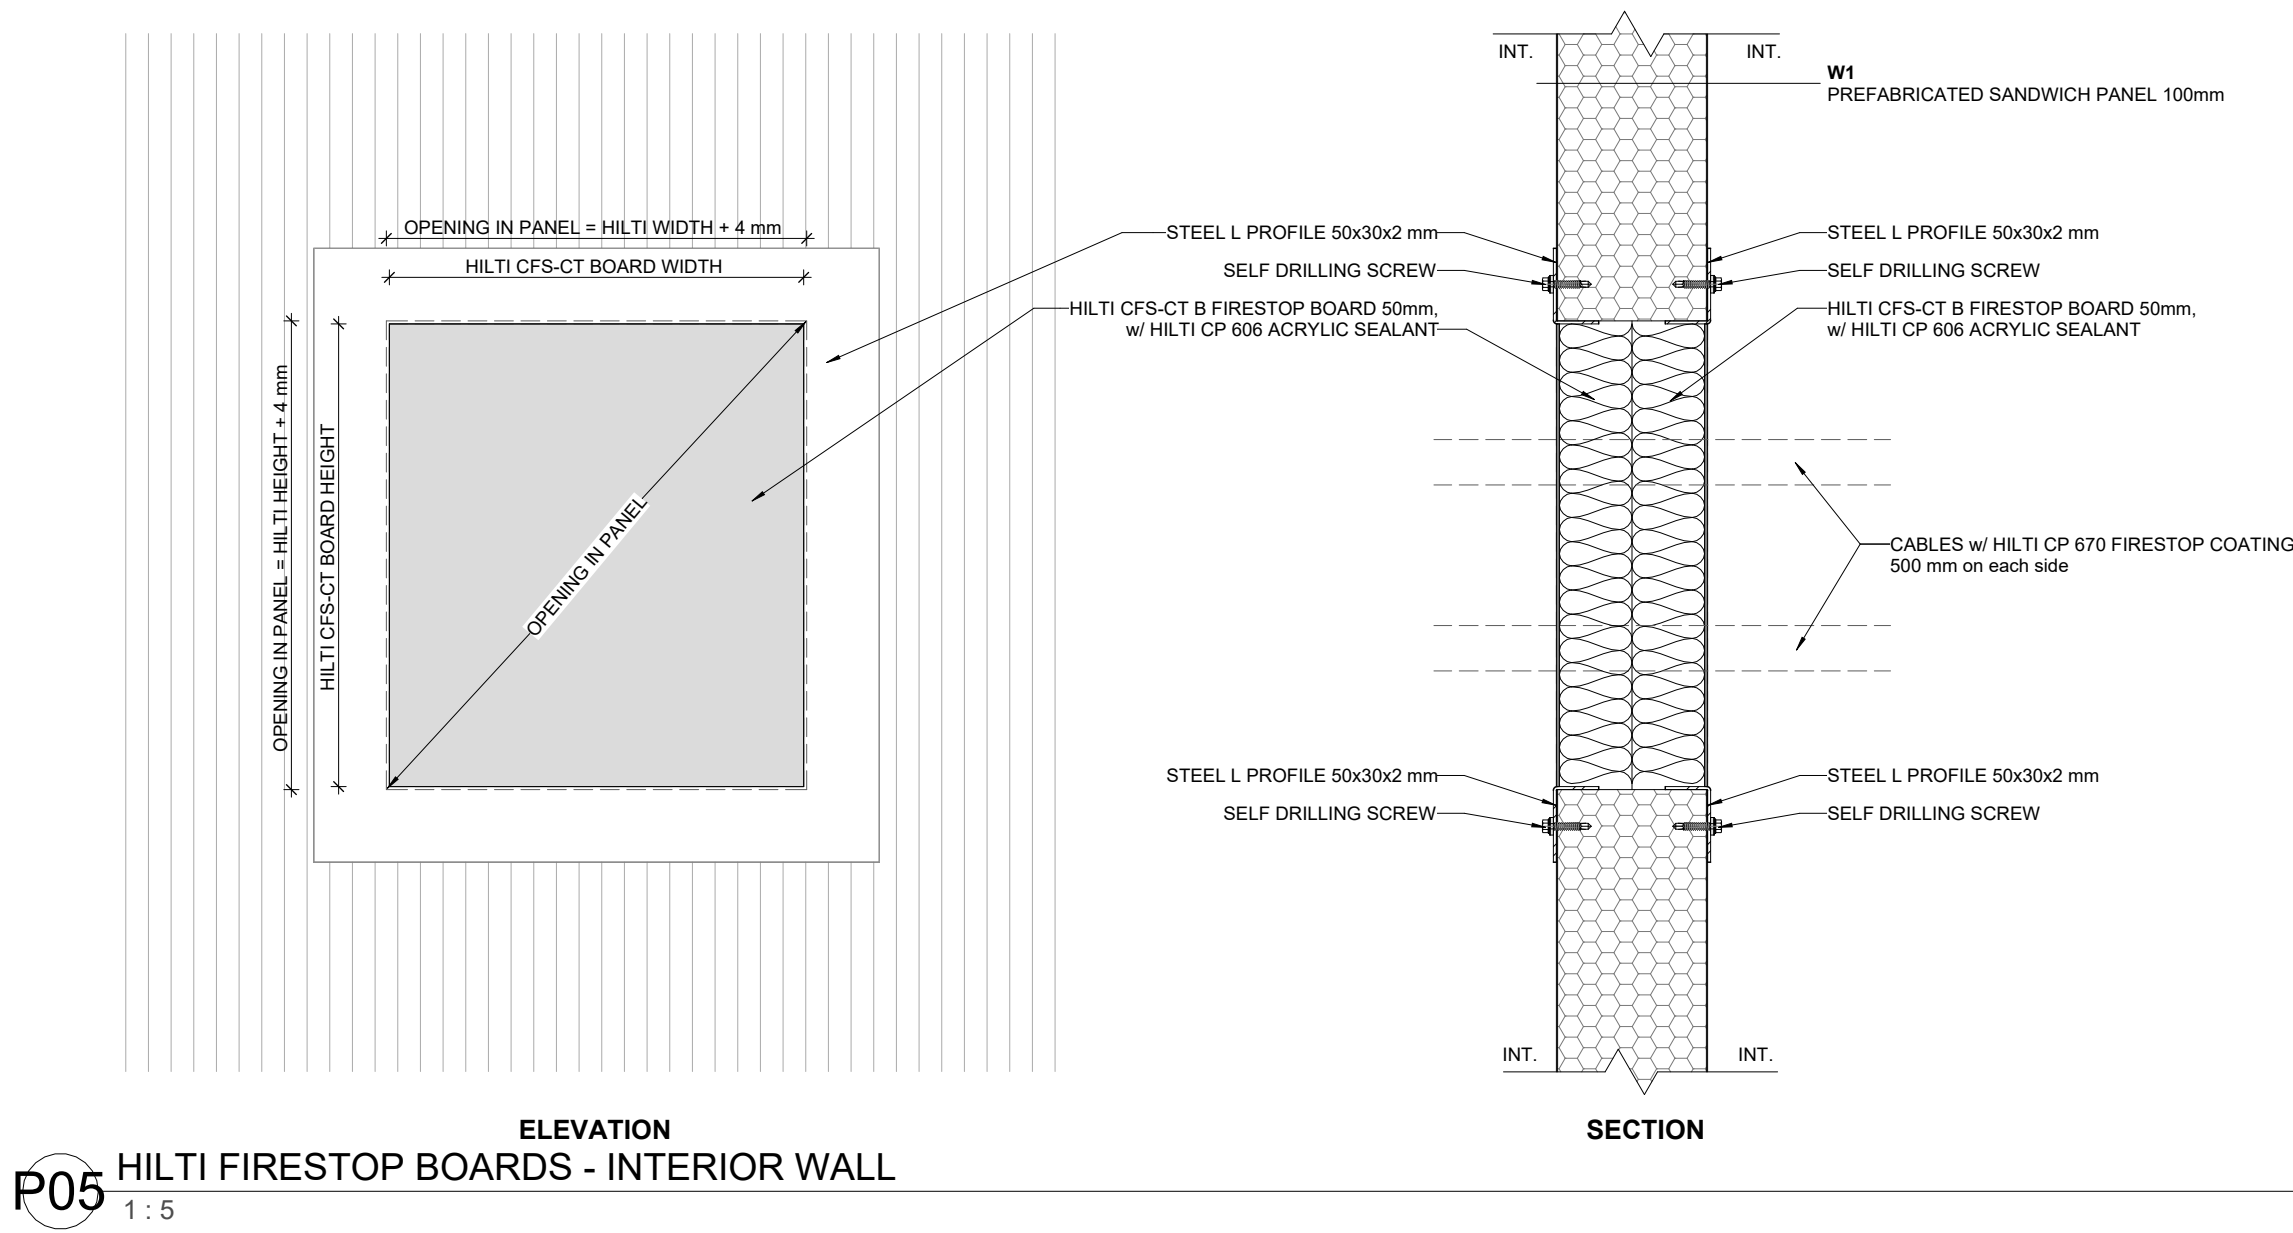


P05 HILTI FIRESTOP BOARDS - INTERIOR WALL
1:5

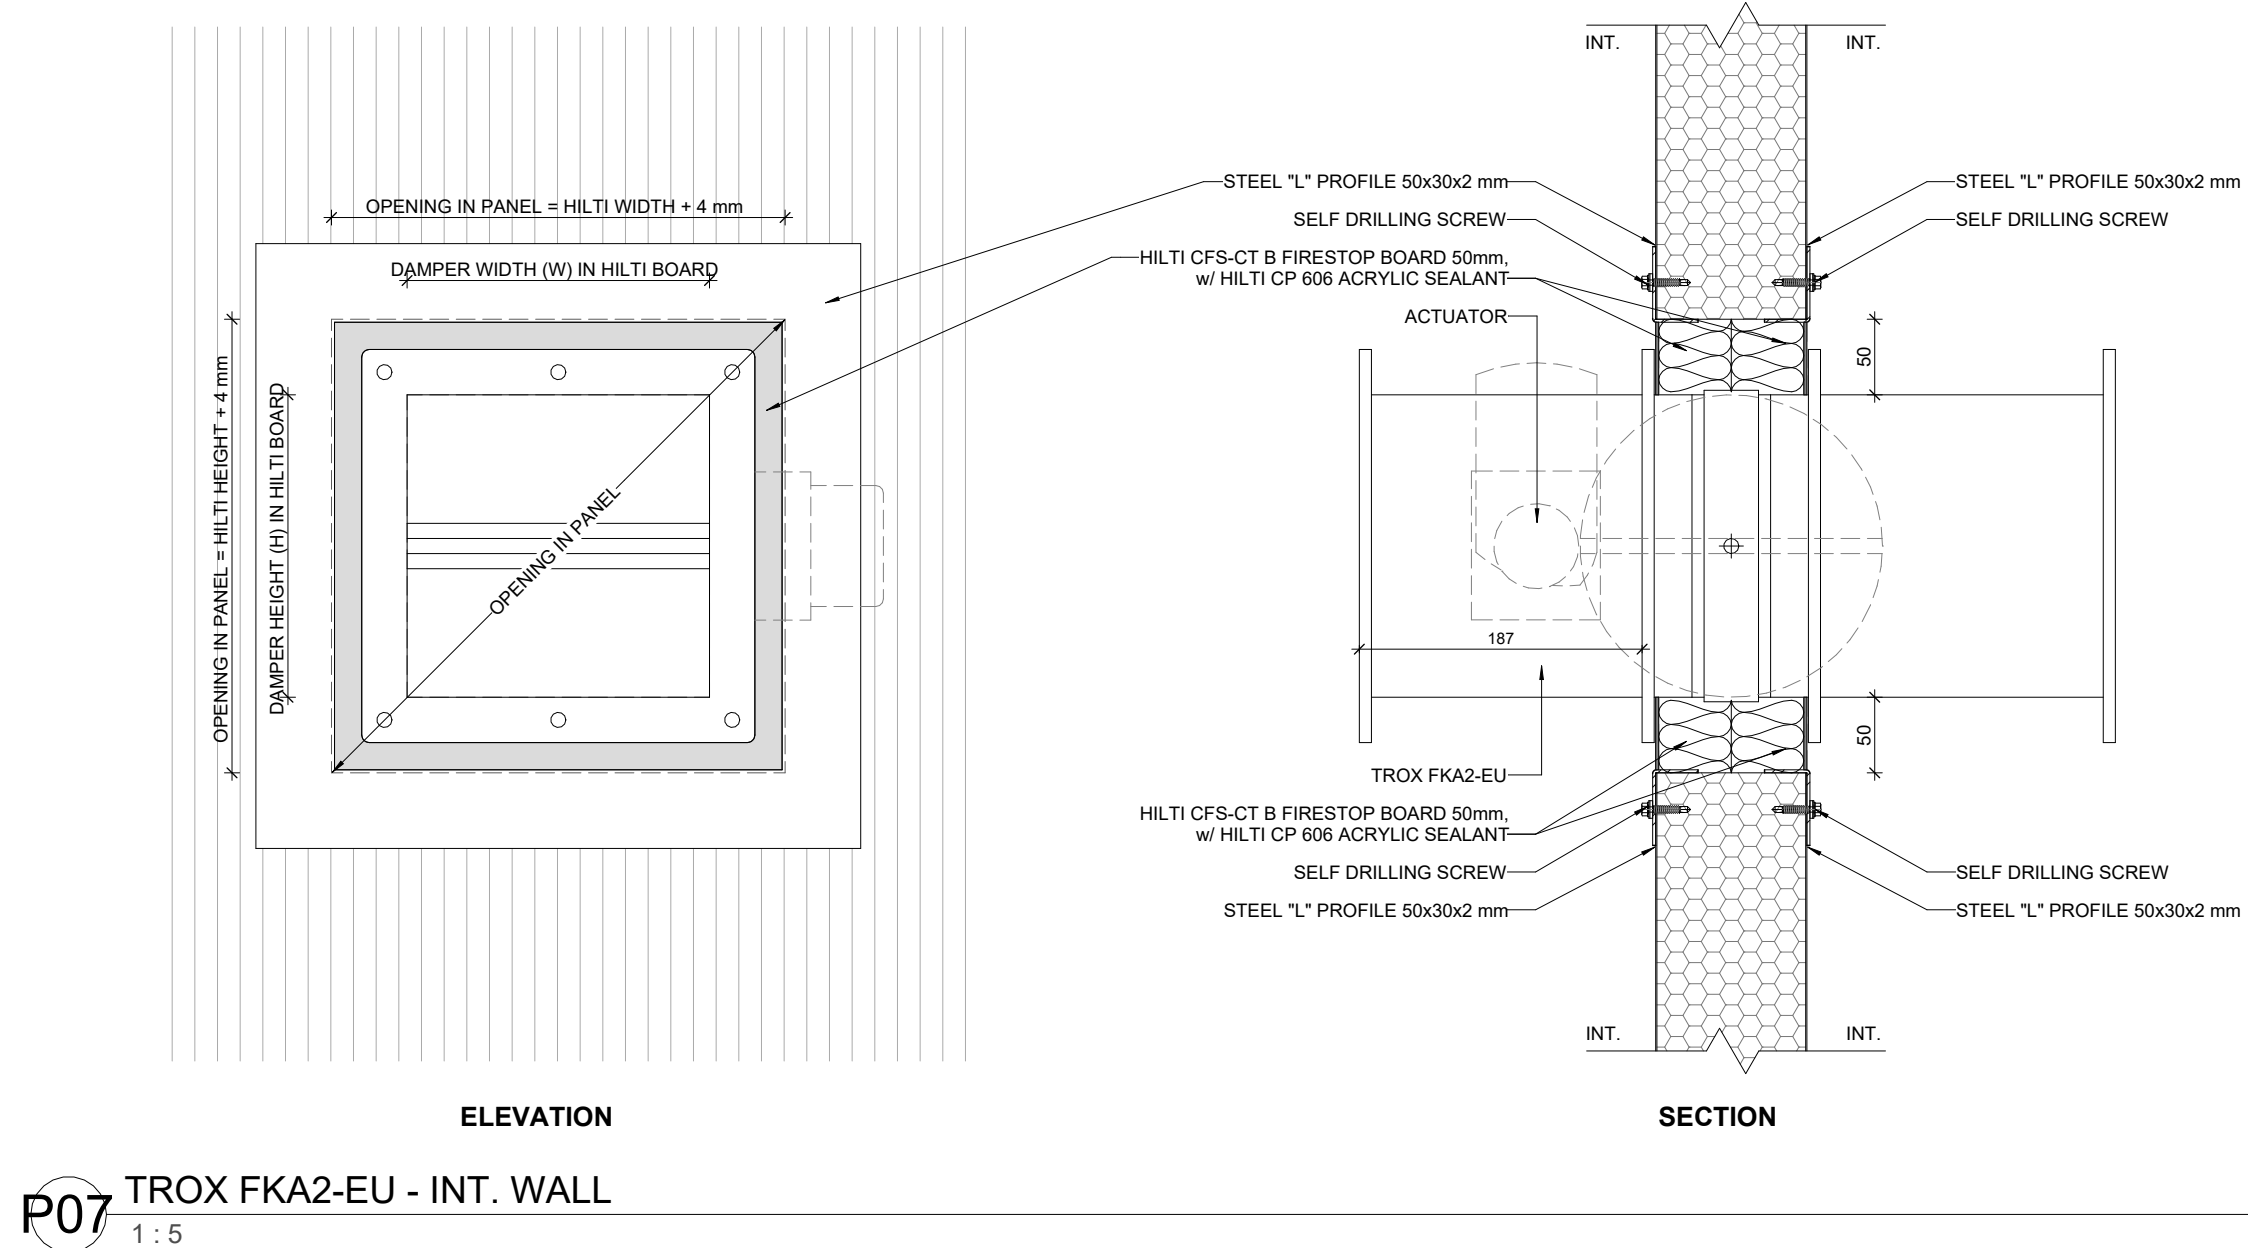


P07 TROX FKA2-EU - INT. WALL
1:5

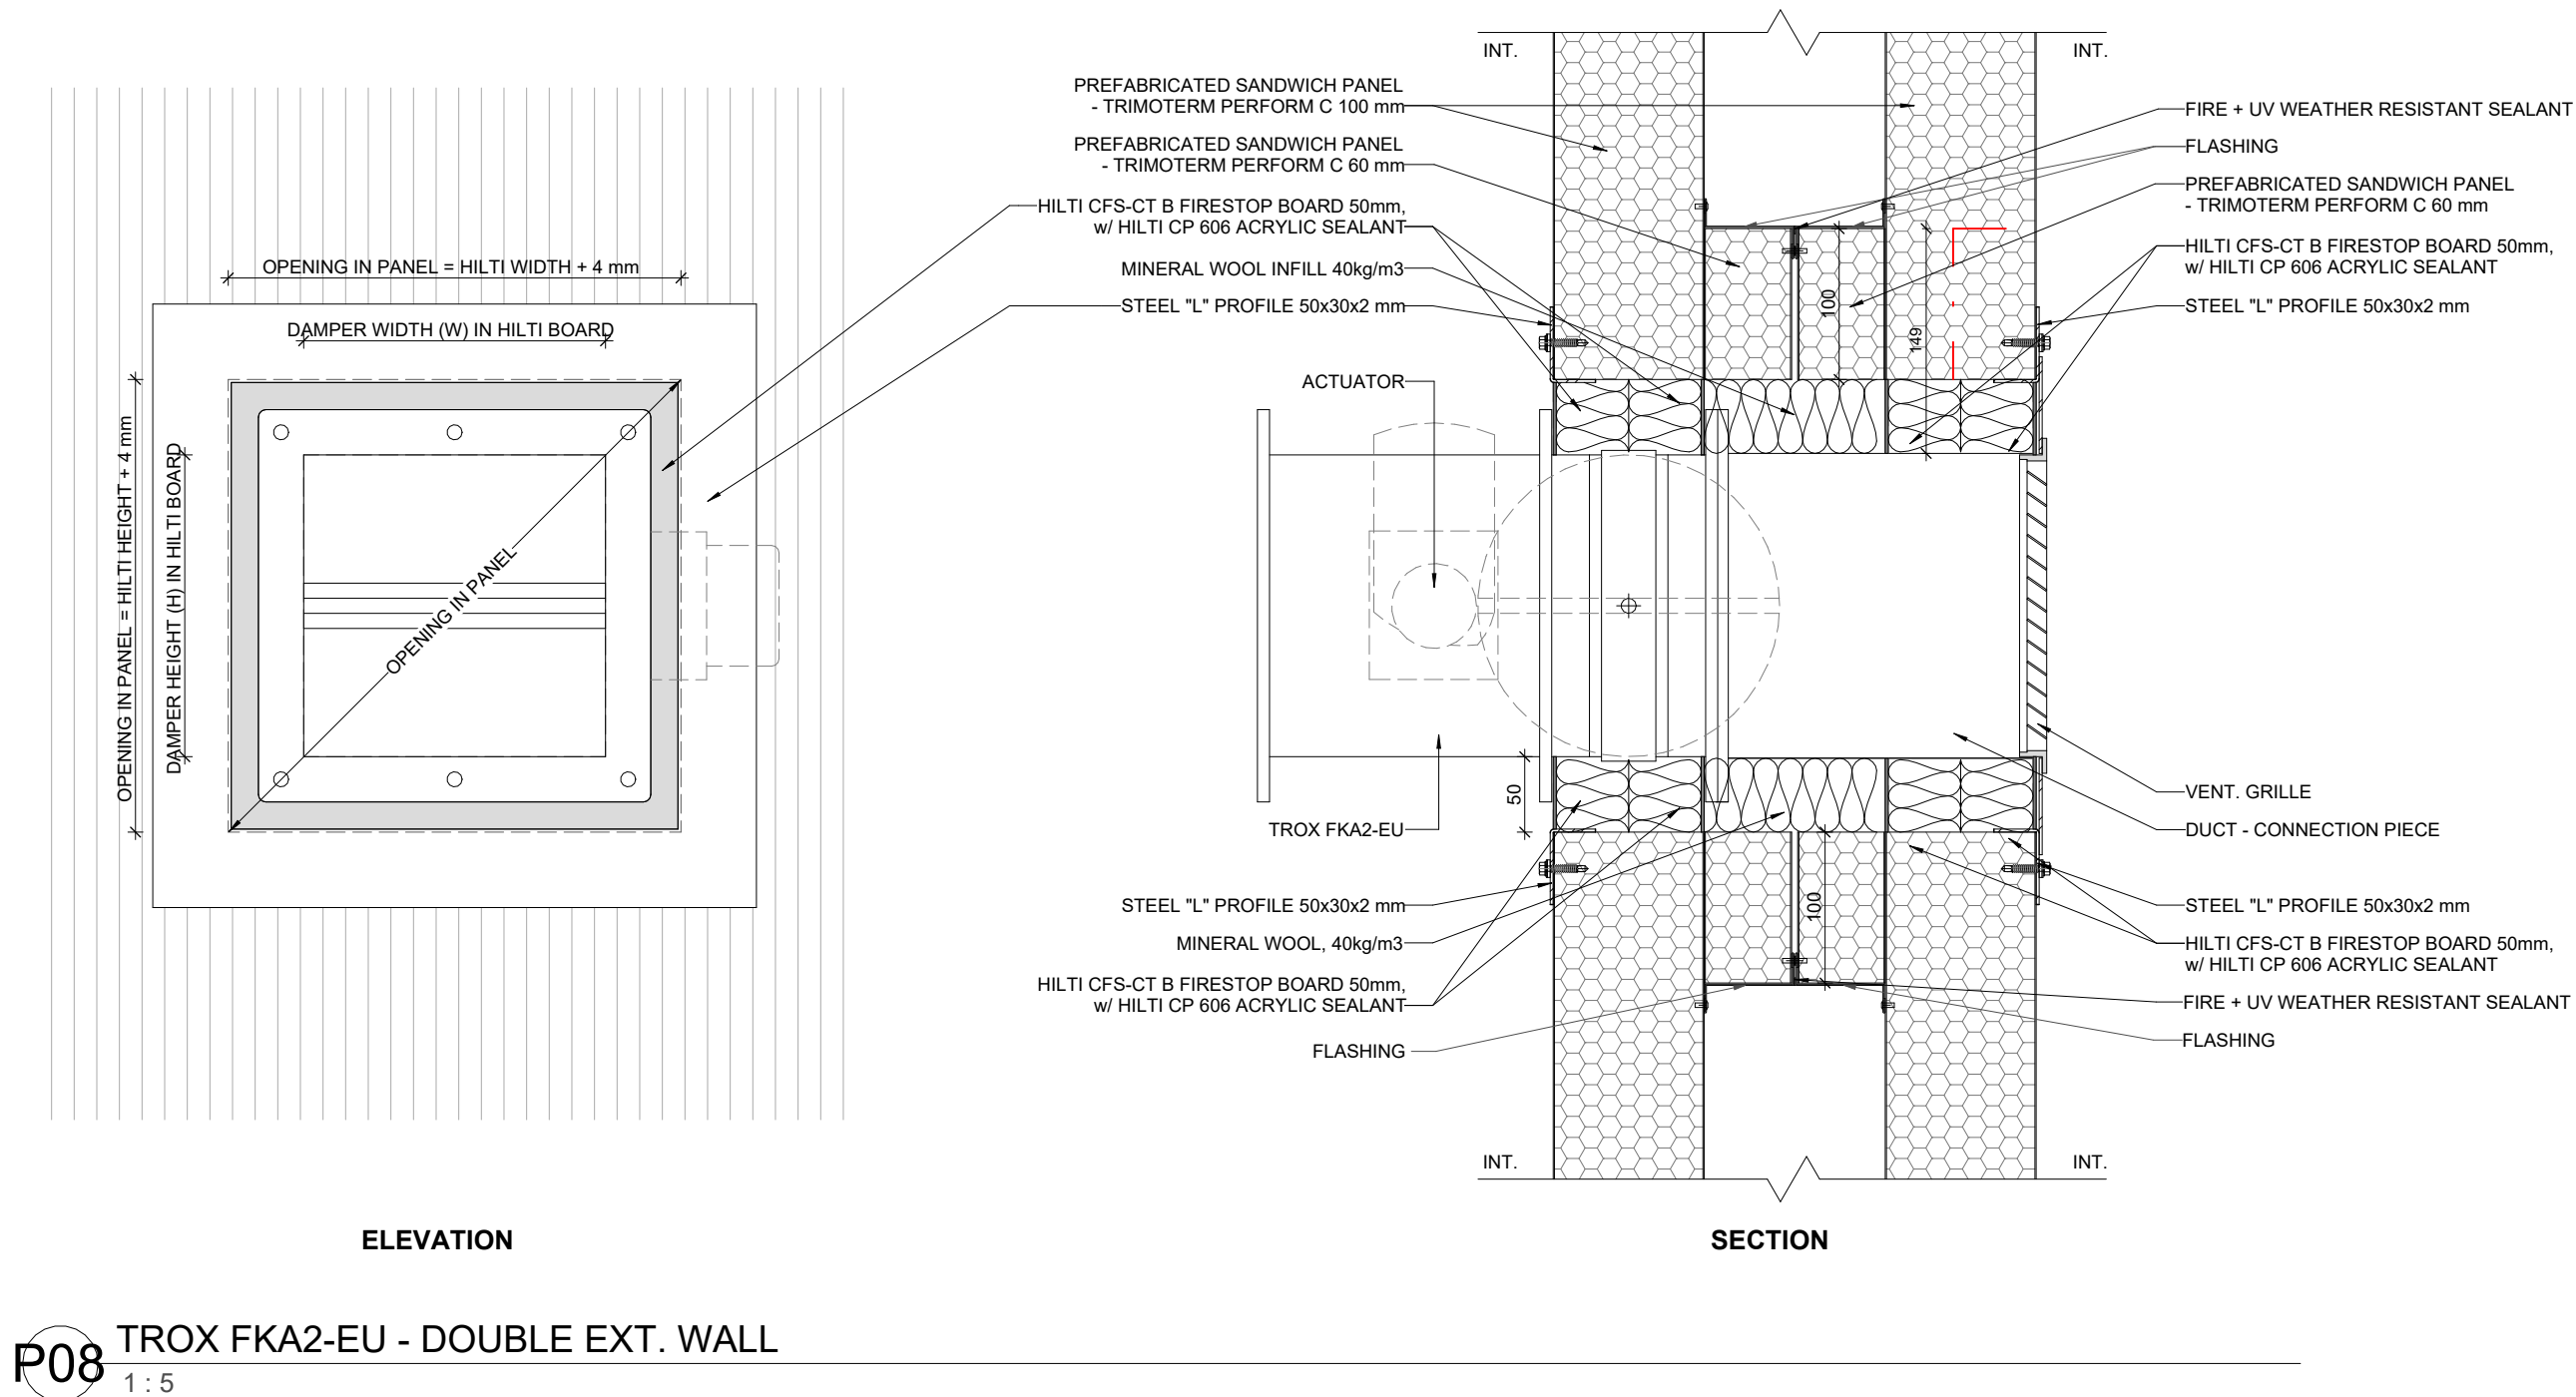

P08 TROX FKA2-EU - DOUBLE EXT. WALL
1:5

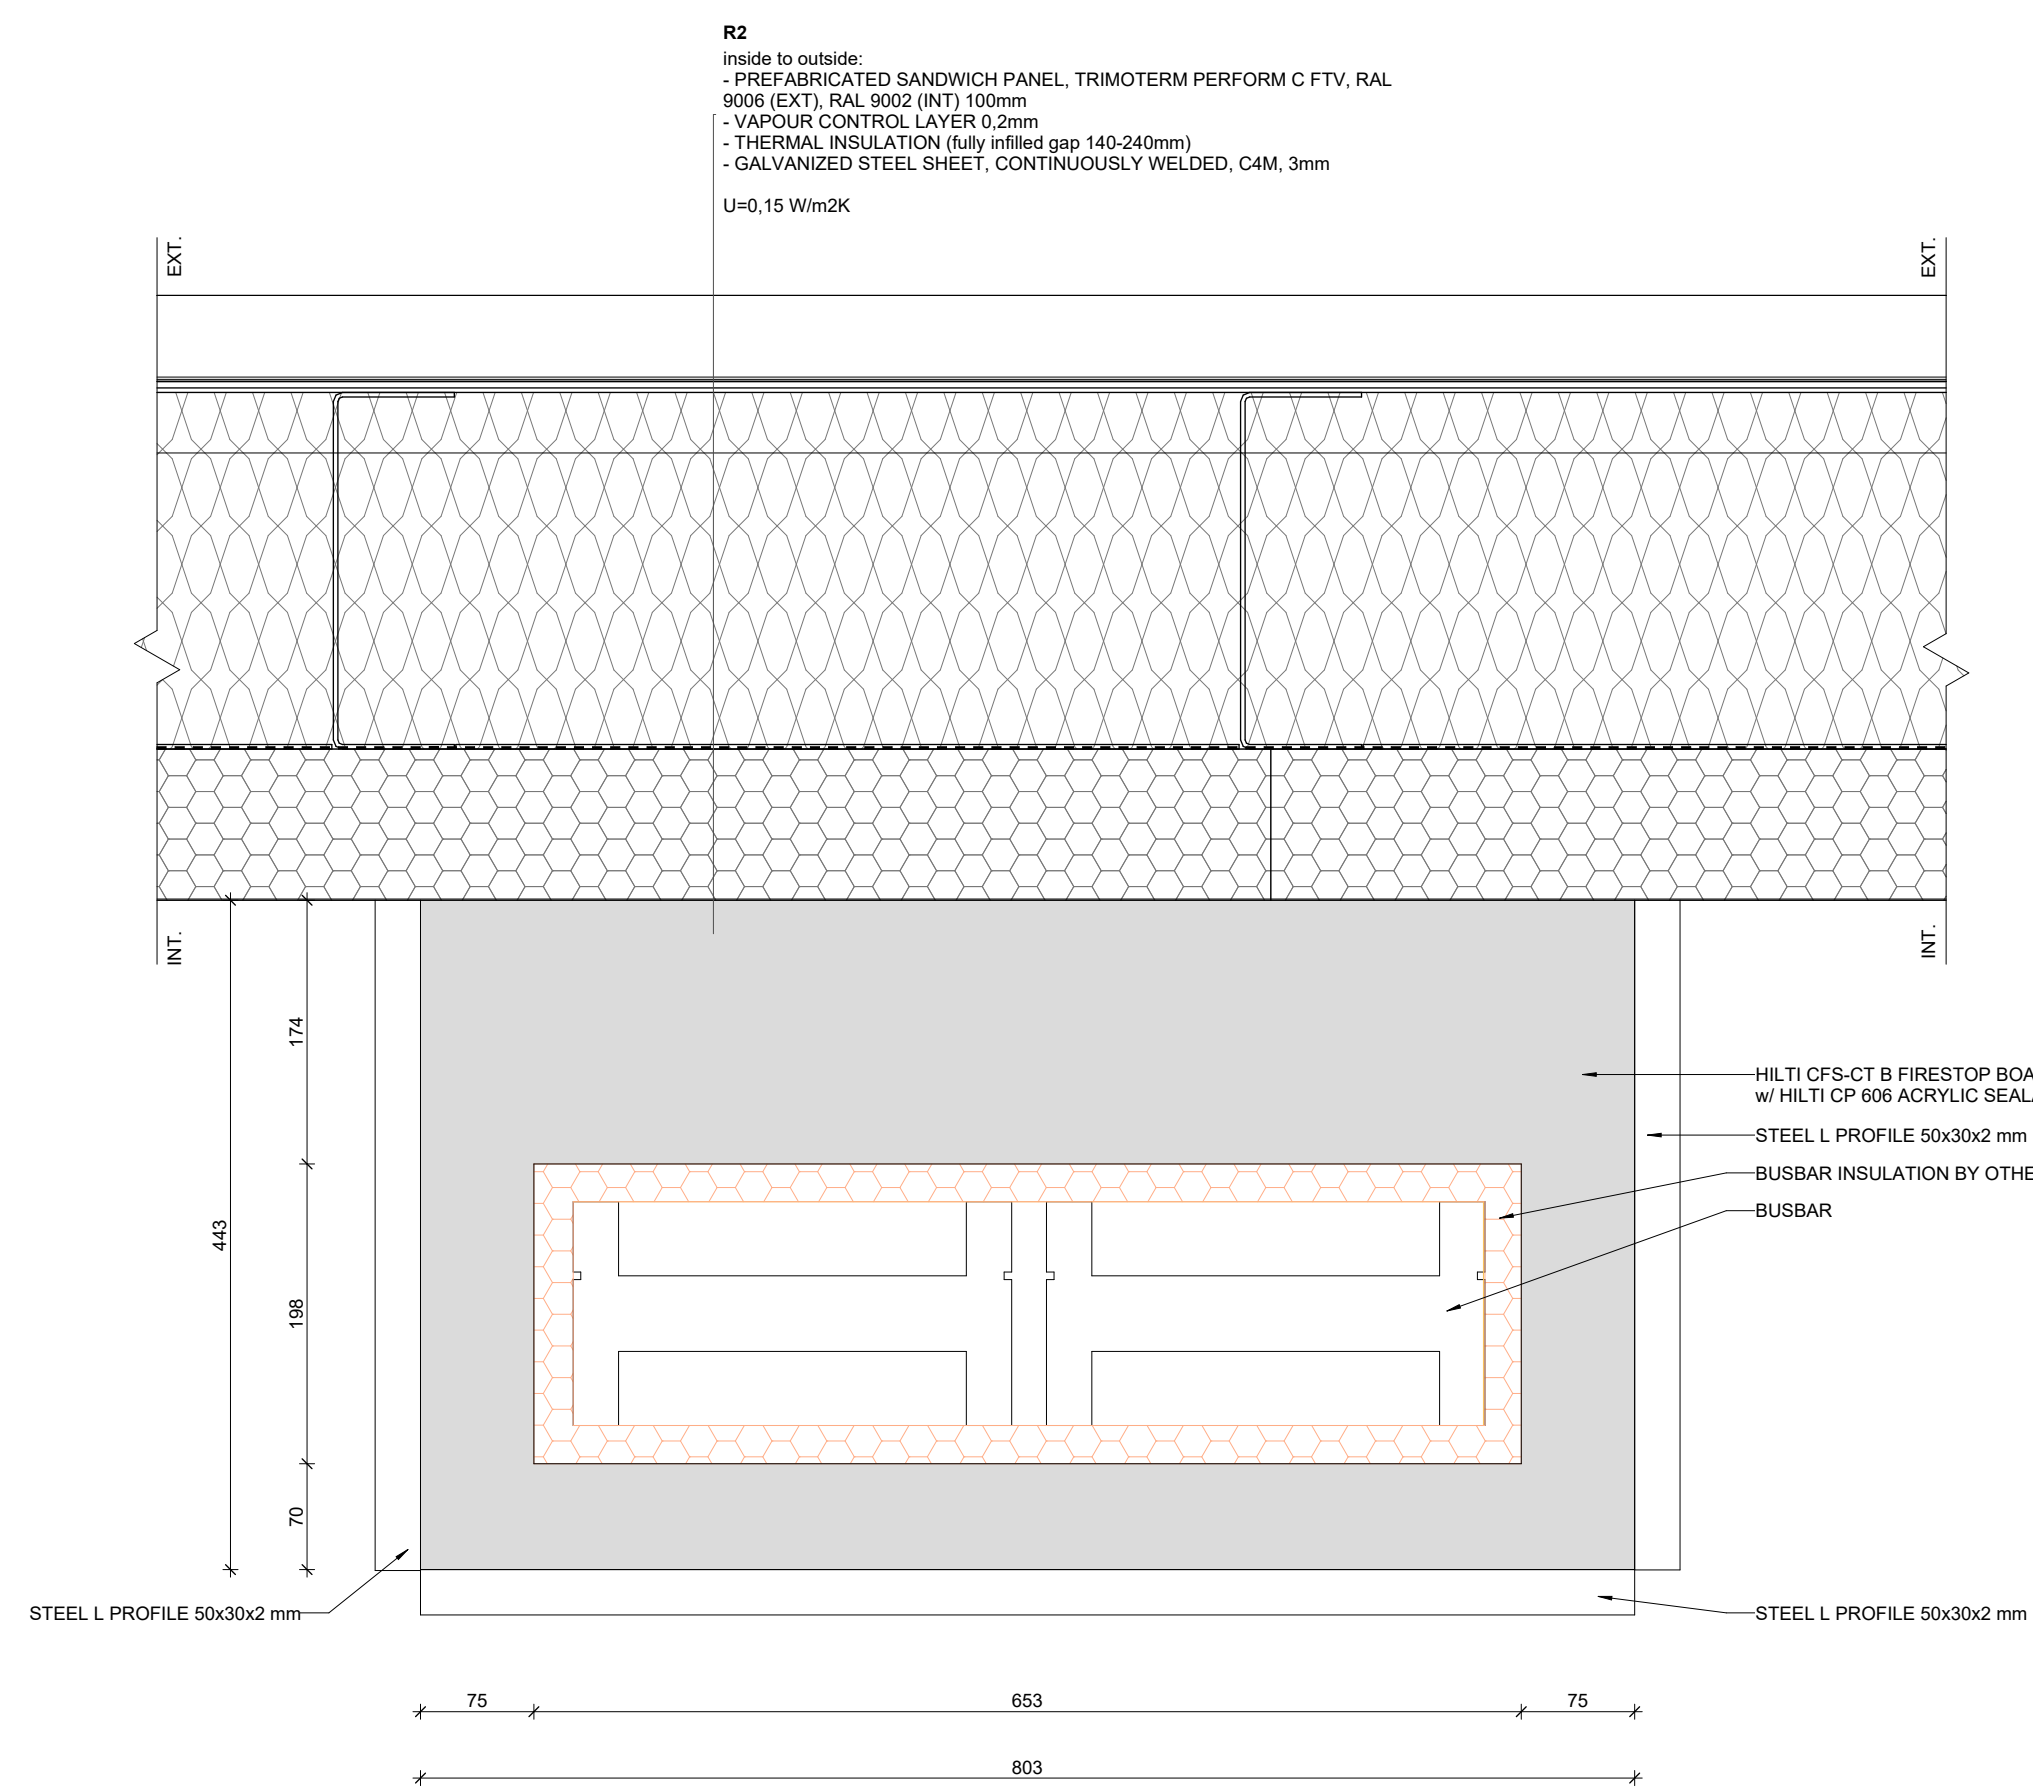


P09 PM BUSBAR-DOUBLE EXT. WALL
1:5

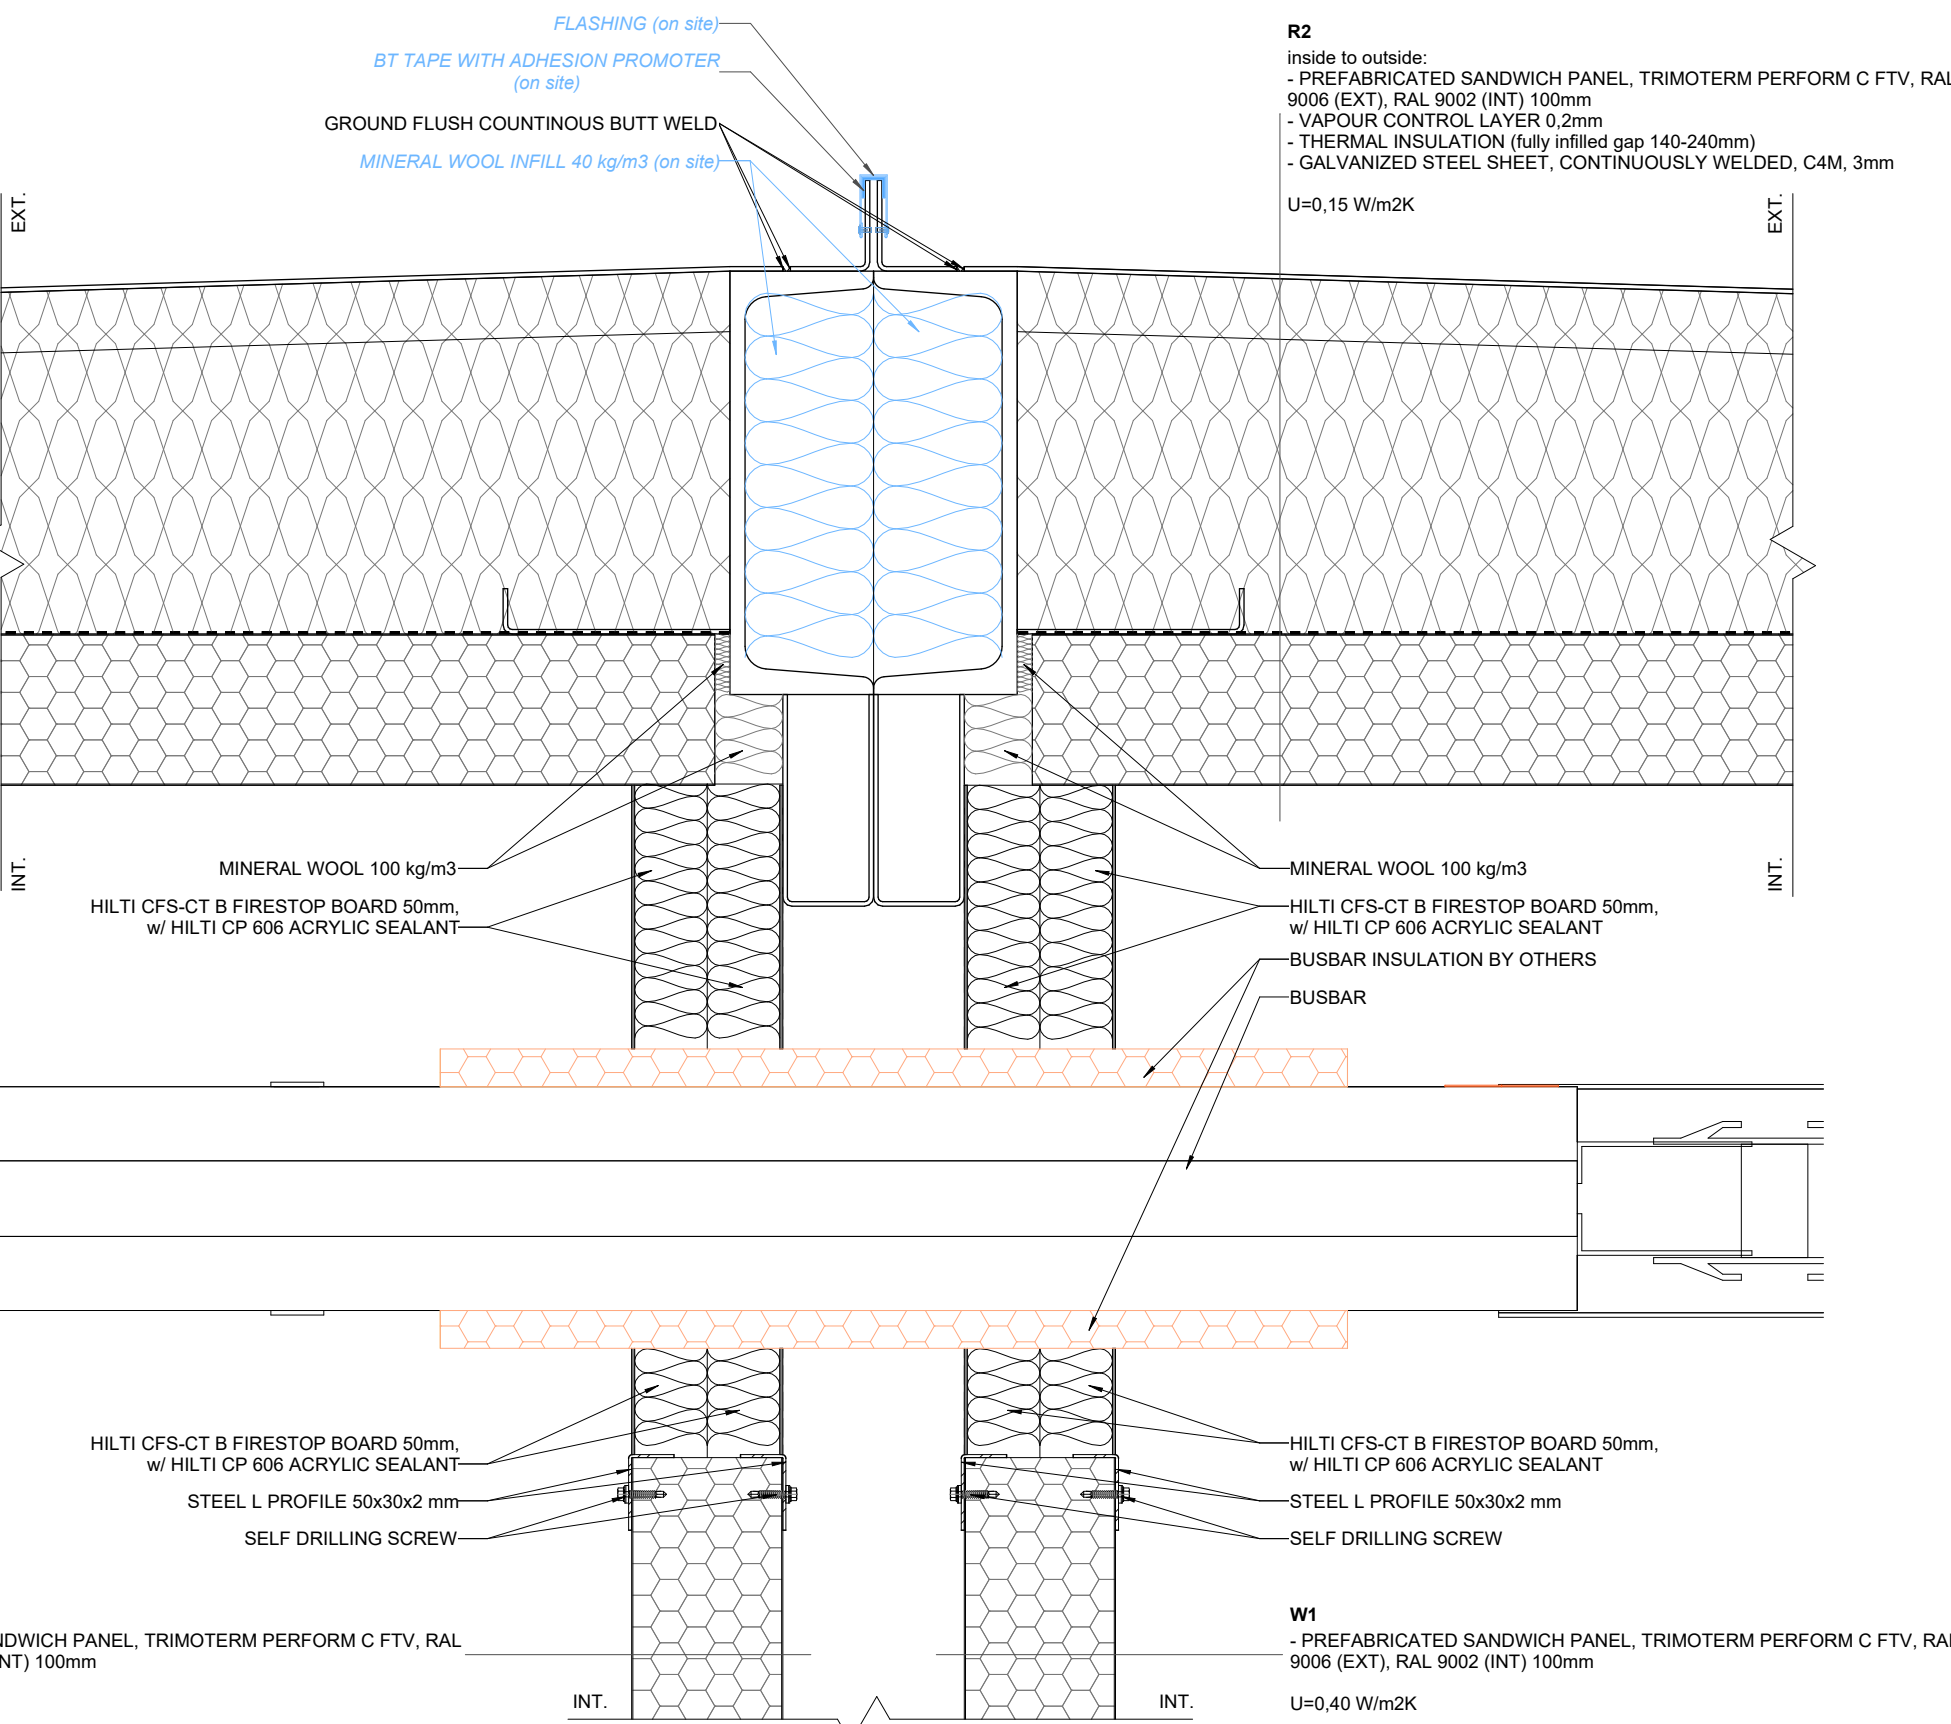

P10 TROX FKA2-EU - DOUBLE EXT. WALL
1:5

KEYNOTES

KEY PLAN

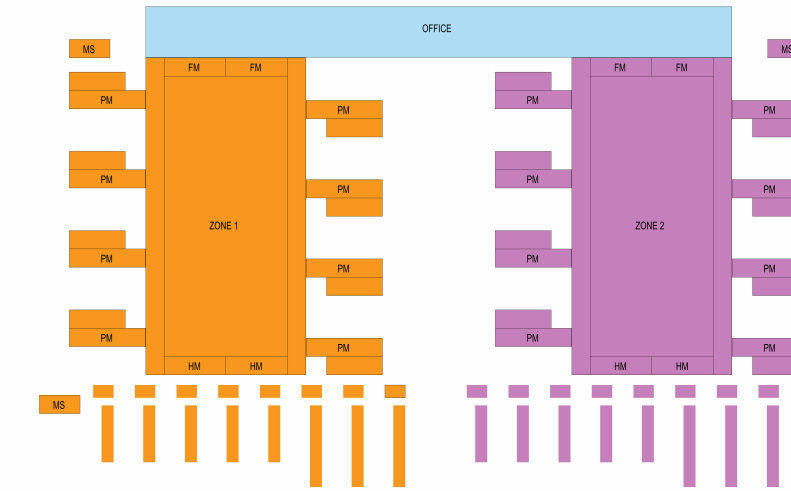

R02	CD SET - FOR INFORMATION	2026-09-
R01	CD SET - FOR INFORMATION	2026-07-
REV.	DESCRIPTION	DATE



PROJECT NAME
ECO DC MONALISA

DRAWING NAME
**ARCHITECTURAL DETAILS
- PREFABRICATED MODULES
- PENETRATIONS INTERNAL - PM - MV - MS**

PREPARED (ALSO SUBJECT RESPONSIBLE IF OTHER)
L. MAVREK / K. KOZINA
DOCUMENT RESPONSIBLE (APPROVED)
M. PACAK
CAD / BIM SYSTEM
AUTODESK REVIT 2025

DOCUMENT NUMBER ECODC-VRT-MDC19-00-DR-A-50106	SHEET SIZE A0	DRAWING SCALE 1:5	DATE (YYYYMMDD) 2026-09-11	SHEET 1 OF 1 REVISION R02
---	-------------------------	-----------------------------	--------------------------------------	--