




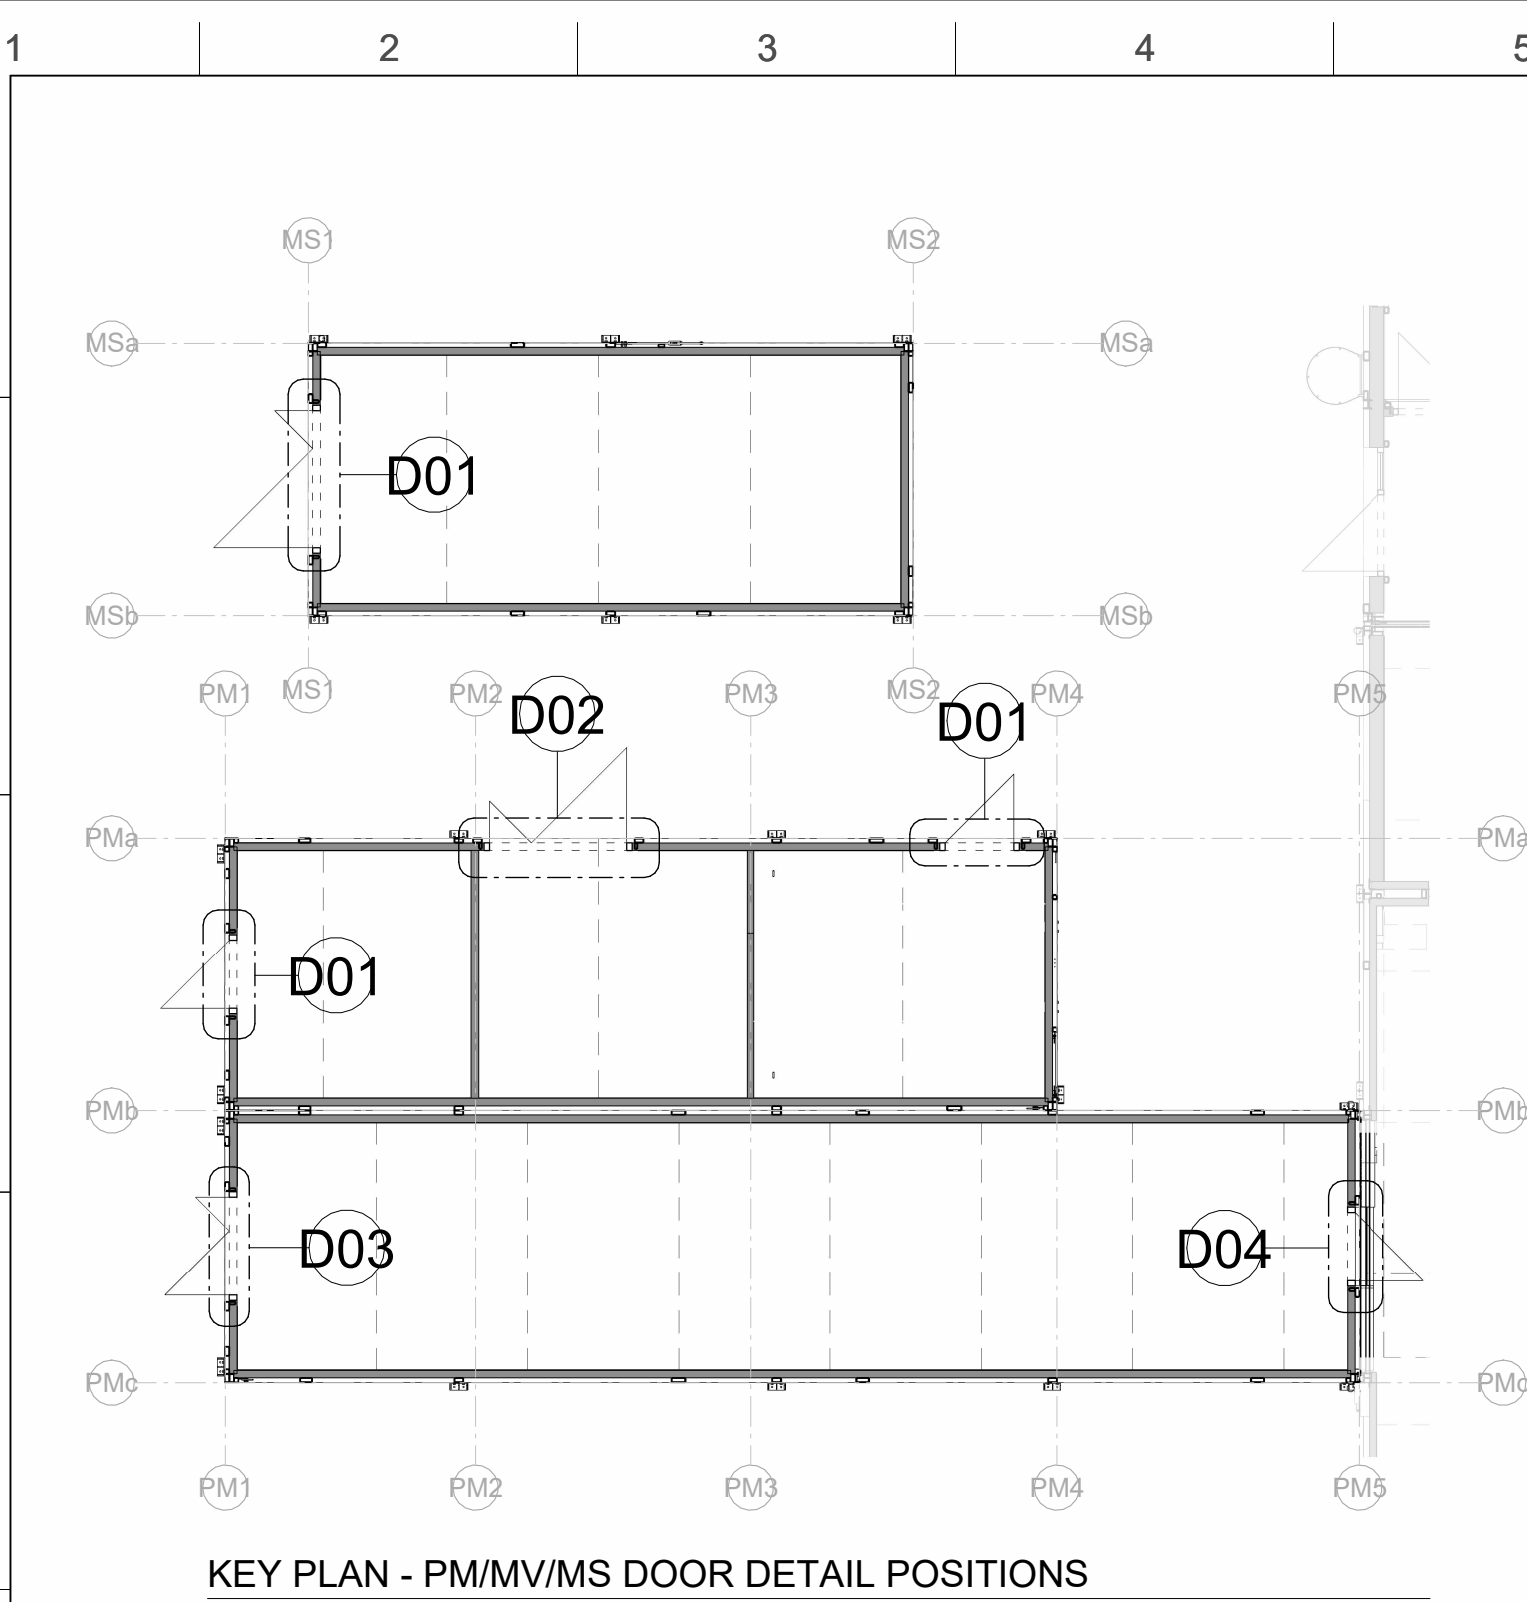


KEY PLAN - PM/MV/MS DOOR DETAIL POSITIONS

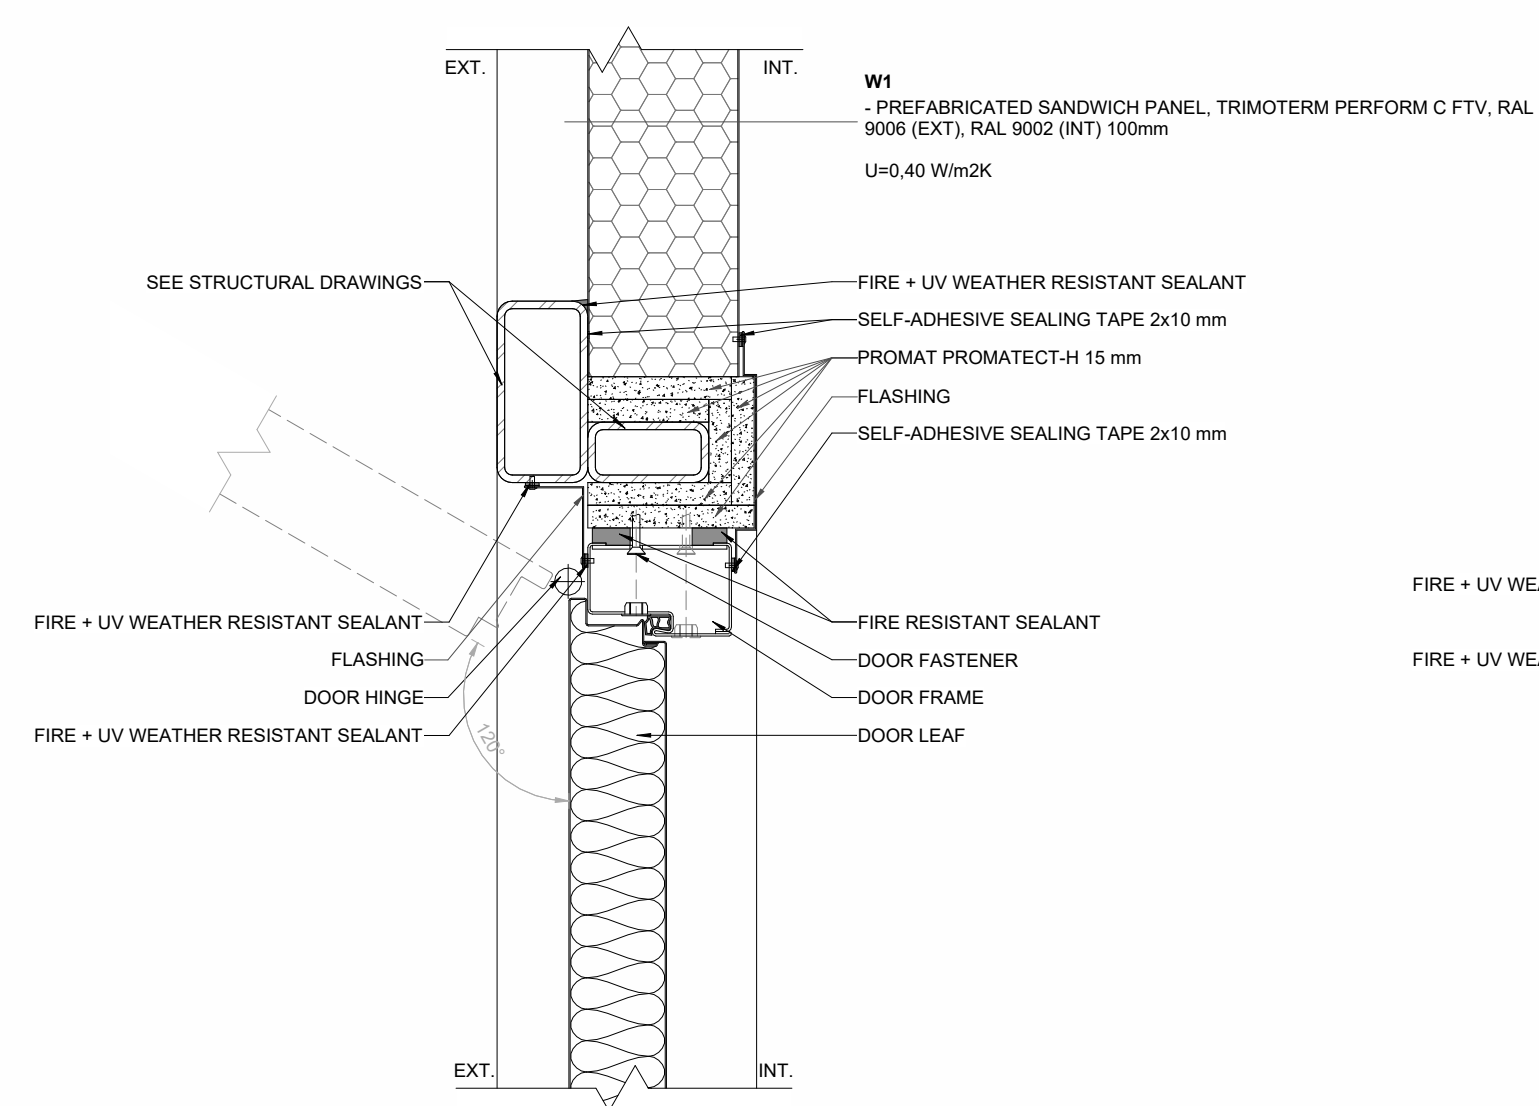


D01 D01-Ext. Door NON-FR
1:5

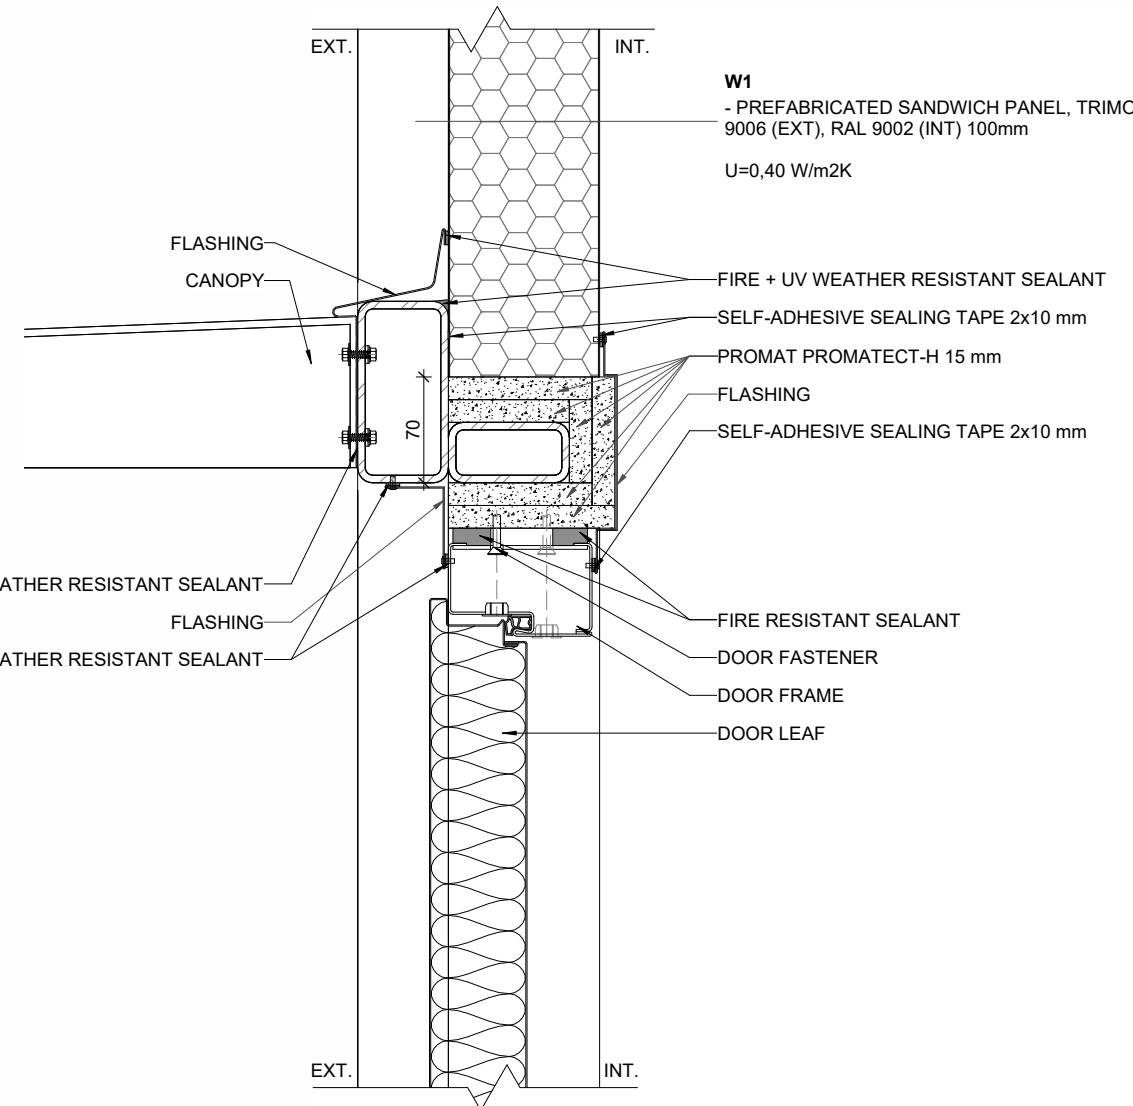


VERTICAL VIEW

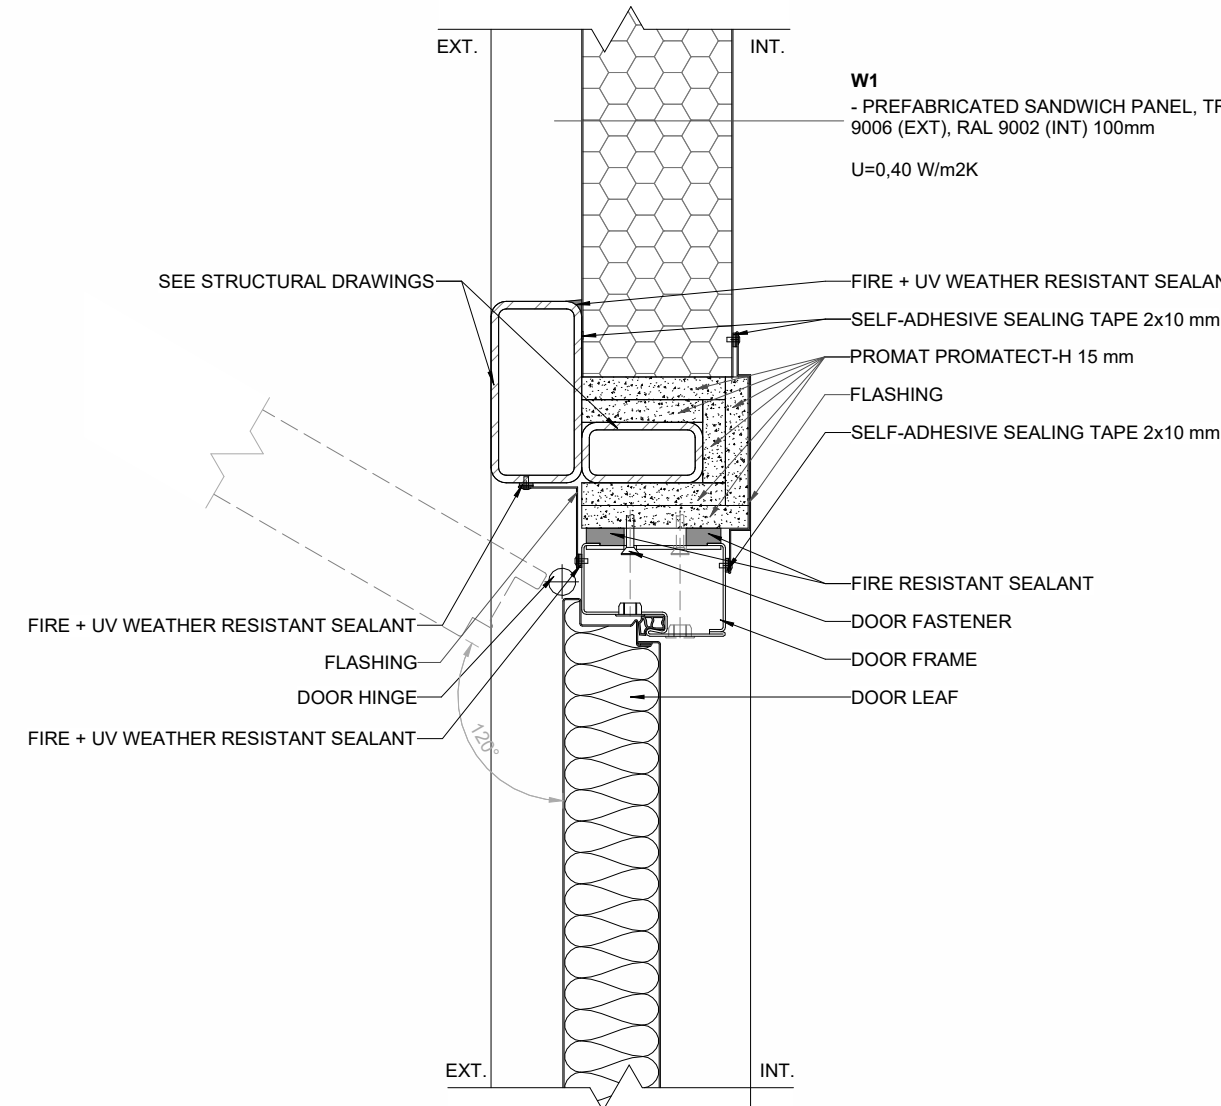


D02 D02-Ext. Door NON-FR
1:5

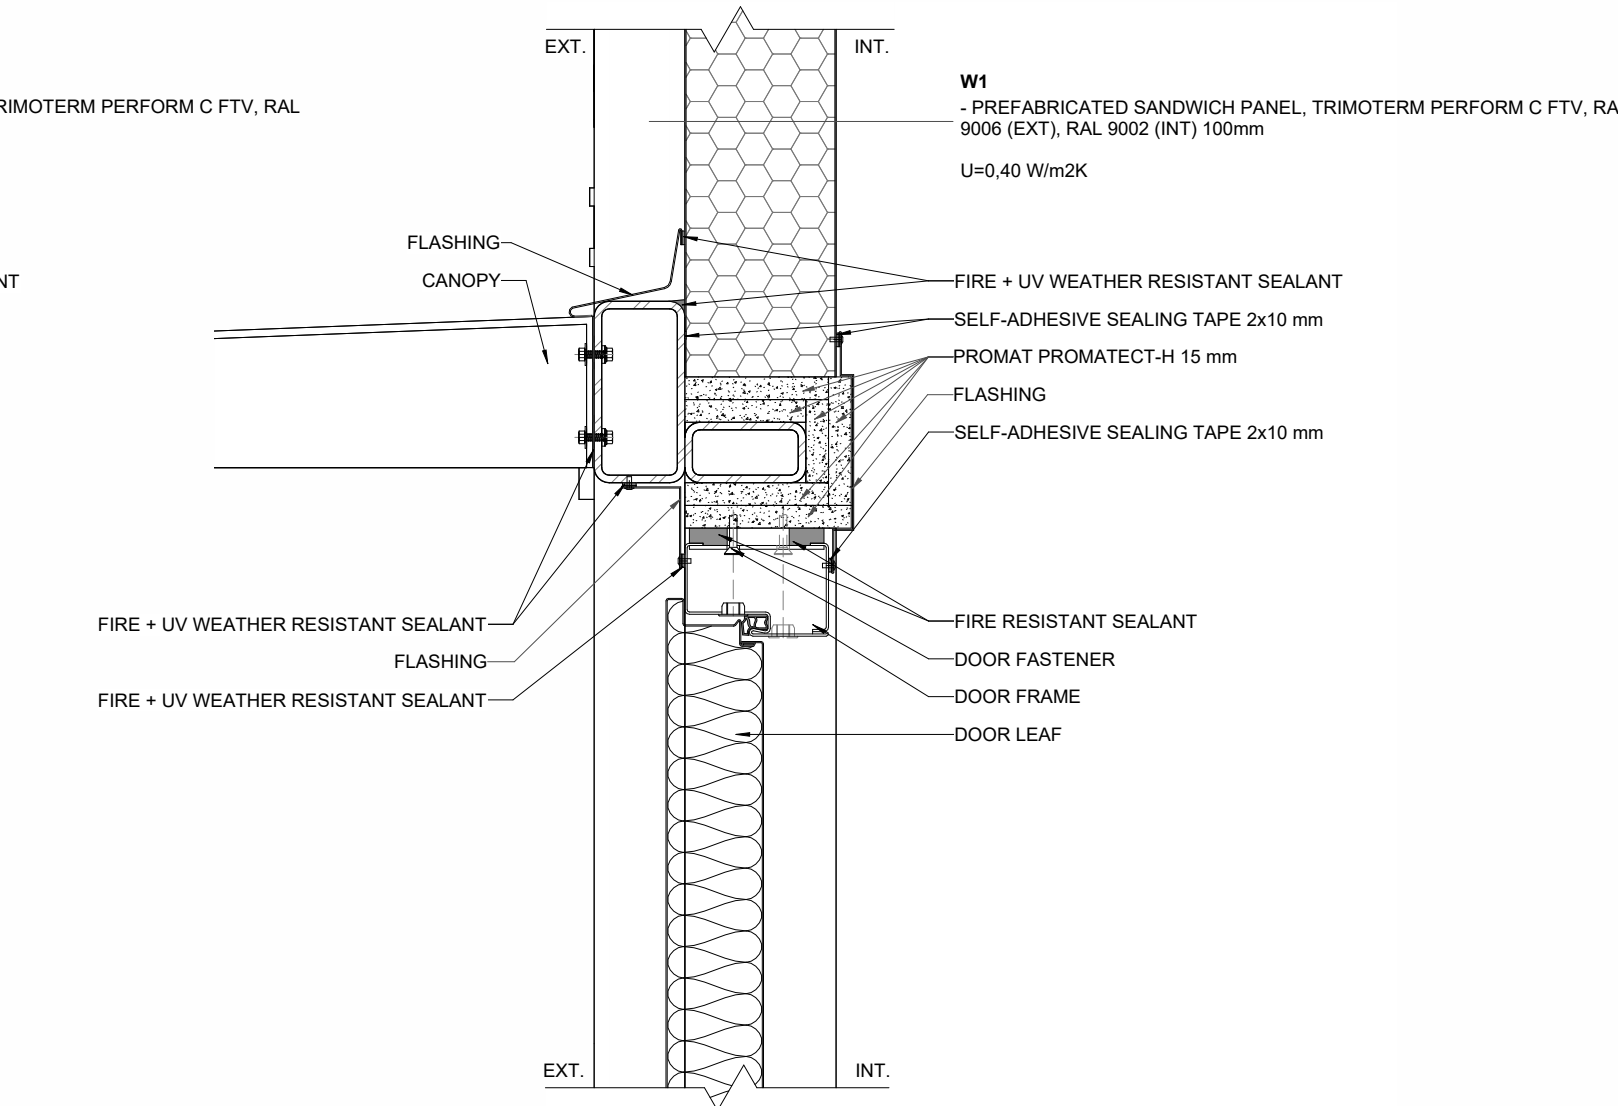


VERTICAL VIEW

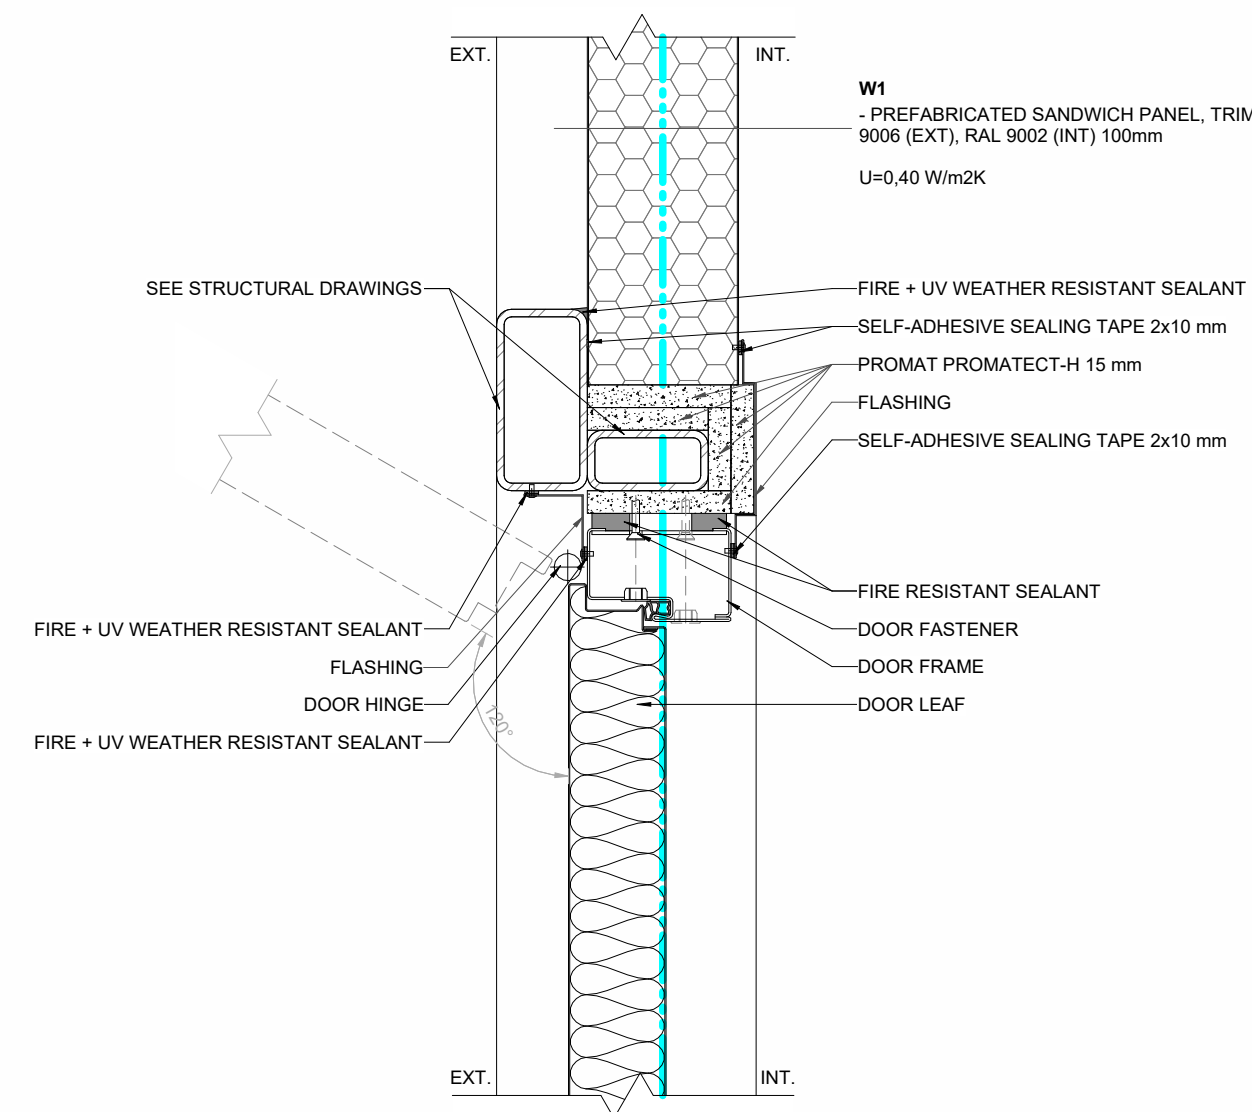


D03 D03-Ext. Door FR
1:5

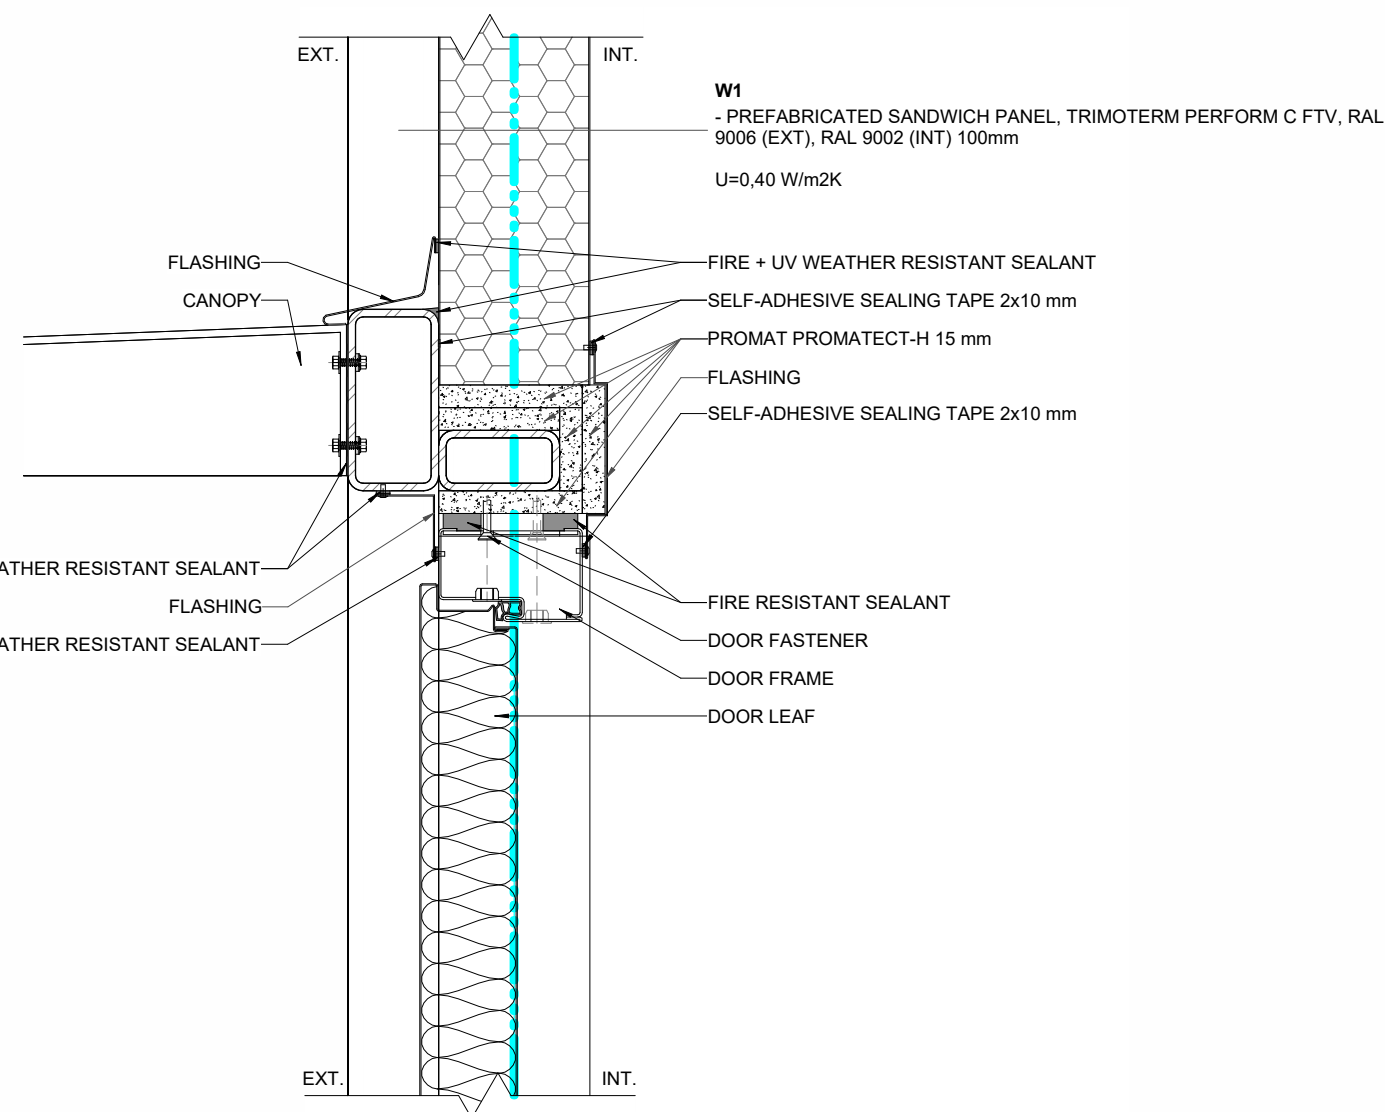


VERTICAL VIEW

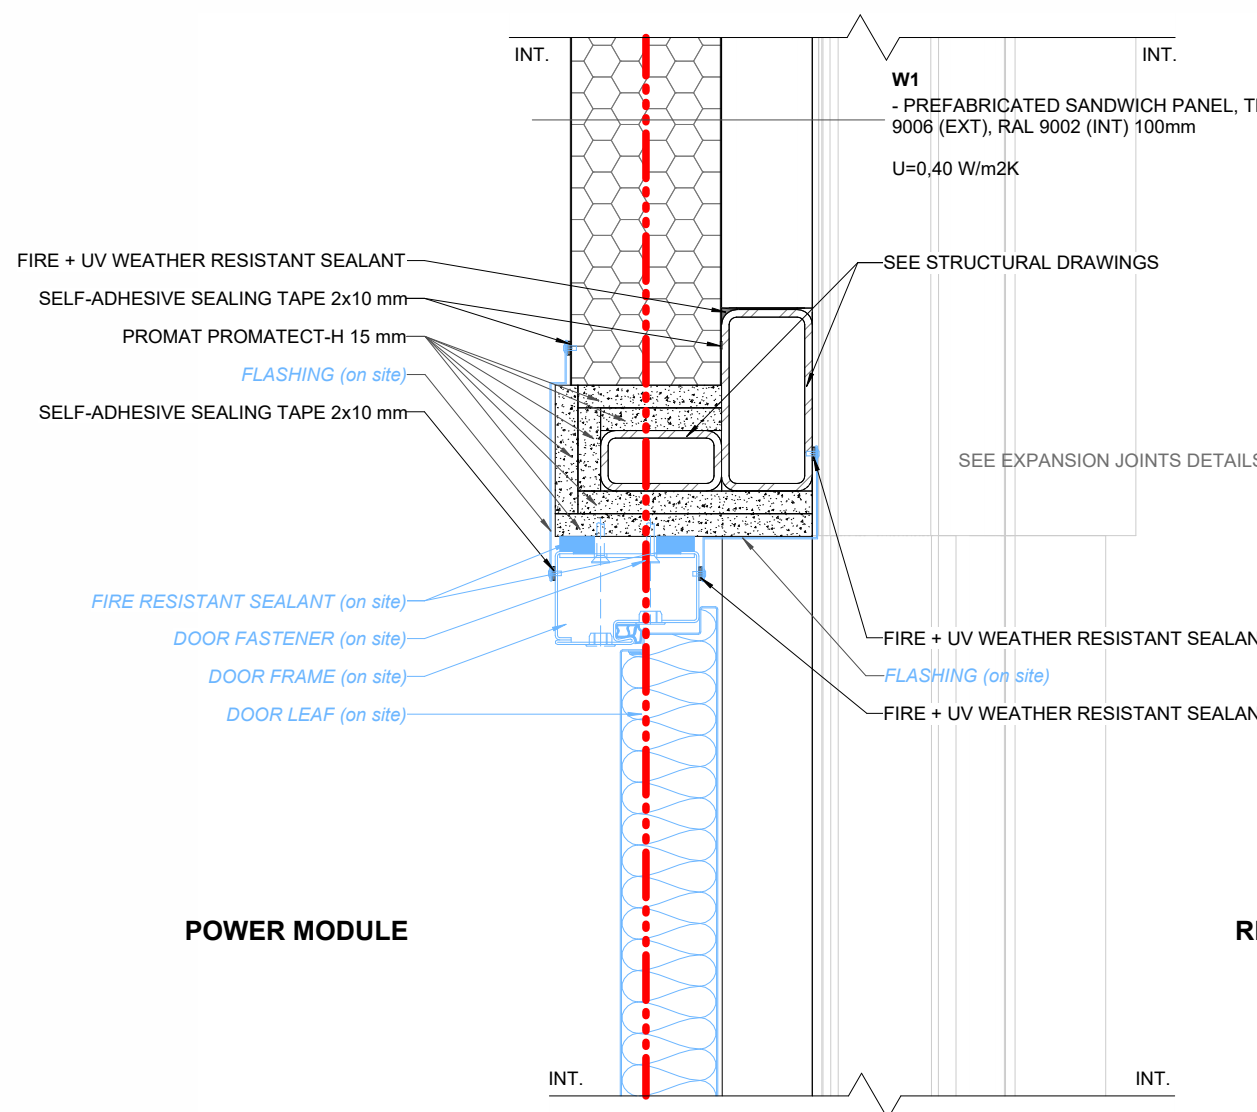

D04 D04-Module Connection Door FR
1:5

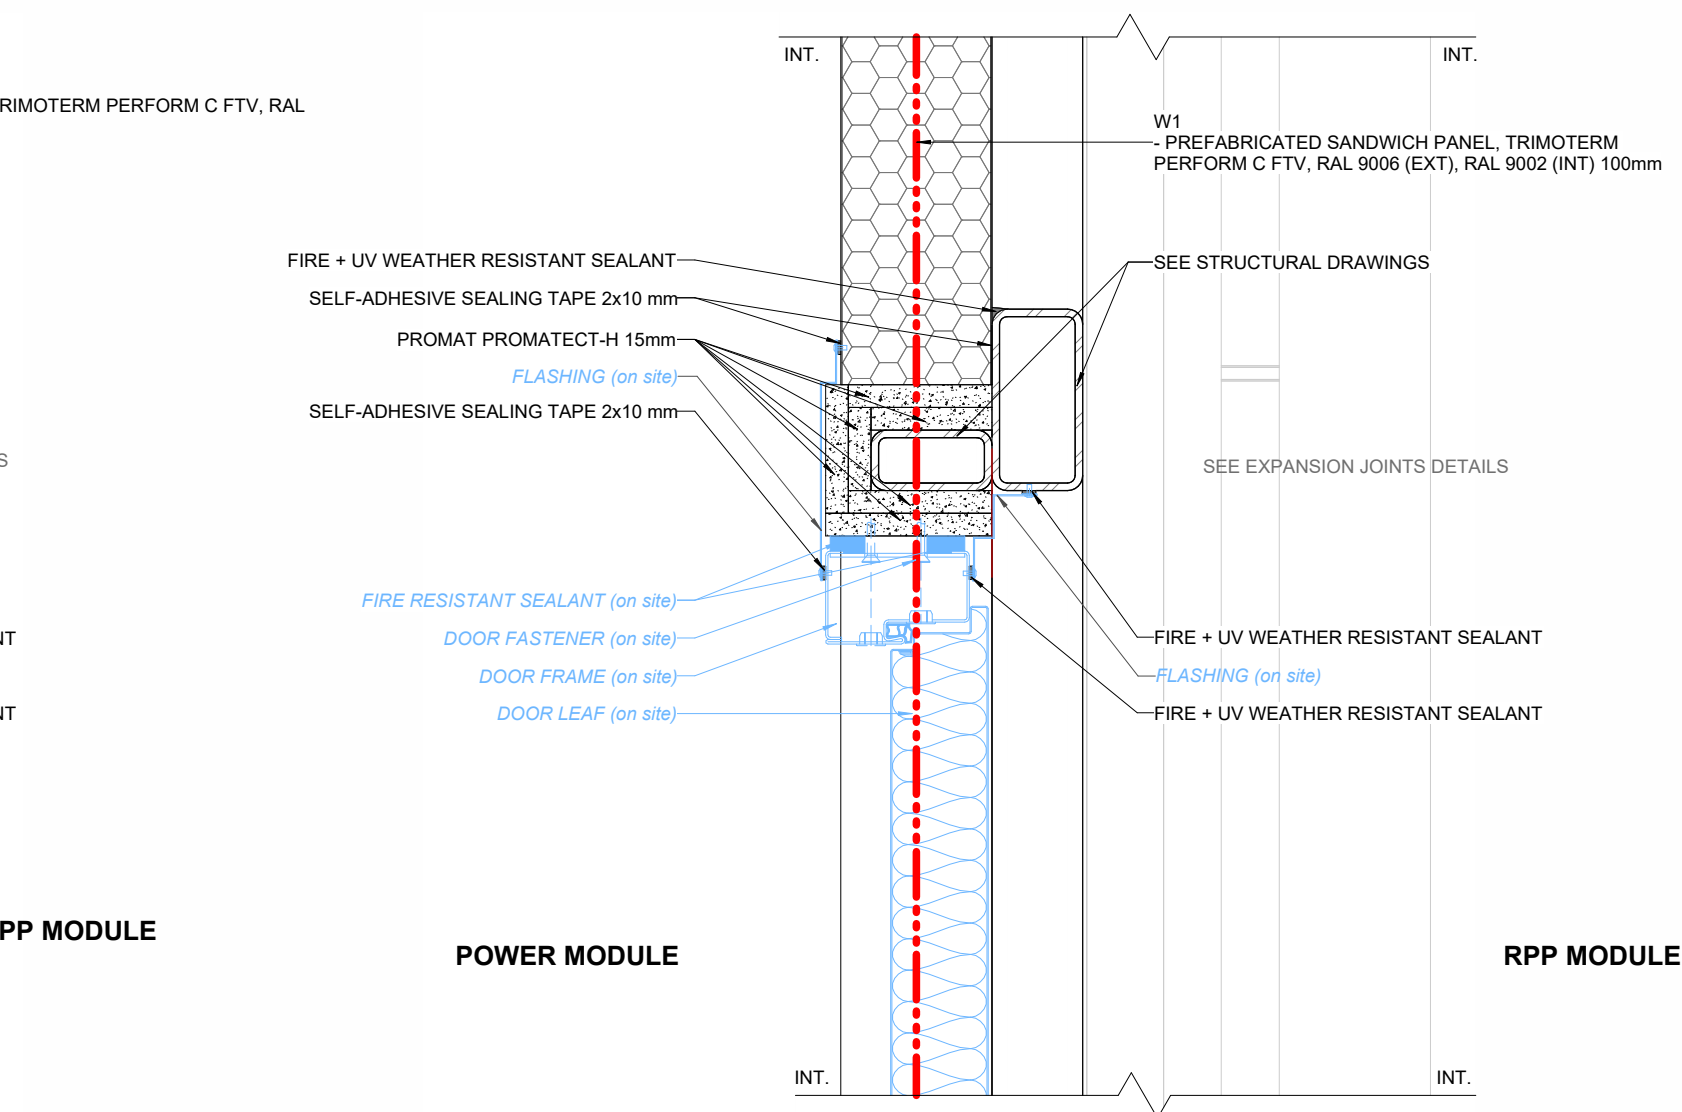

VERTICAL VIEW

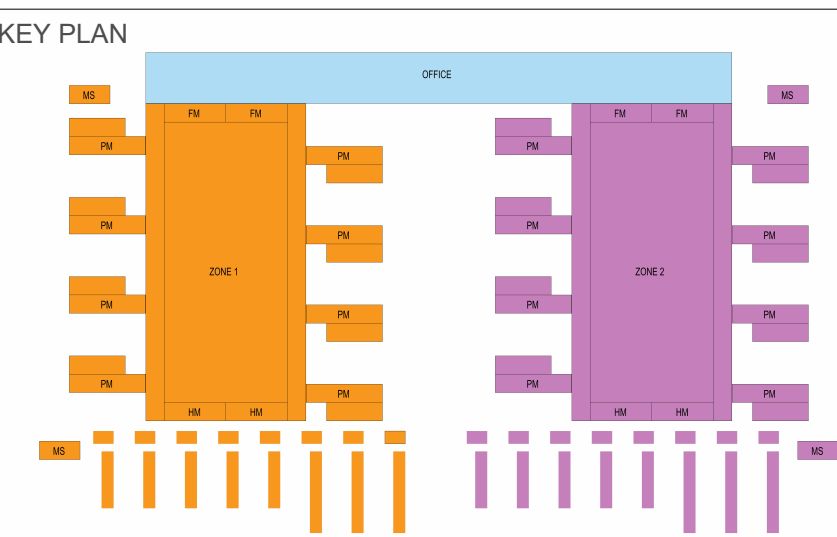

R02	CD SET - FOR INFORMATION	2026-09-11
R01	CD SET - FOR INFORMATION	2026-07-24
REV.	DESCRIPTION	DATE



PROJECT NAME

ECO DC MONALISA

ARCHITECTURAL DETAILS – PREFABRICATED MODULES – DOORS – PM – MV – MS

PREPARED (ALSO SUBJECT RESPONSIBLE IF OTHER)
L. MAVREK / K. KOZINA

DOCUMENT RESPONSES / APPROVED

M. PACAK

CAD / BIM SYSTEM AUTODESK REVIT 2025

DOCUMENT NUMBER	SHEET 1 of 1
ECODC-VRT-MDC19-00-DR-A-50130	REVISION

SHEET SIZE A0	DRAWING SCALE 1 : 5	DATE (YYYYMM-DD) 2026-09-11	R02
------------------	------------------------	--------------------------------	------------

22 23 24